

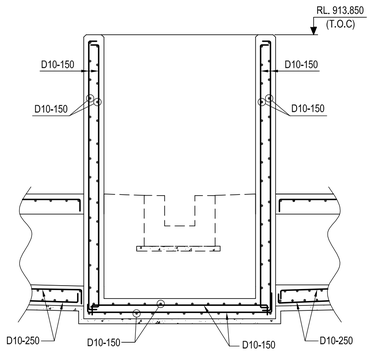



SECTION A-A
(R.C DETAIL)
SCALE 1:30

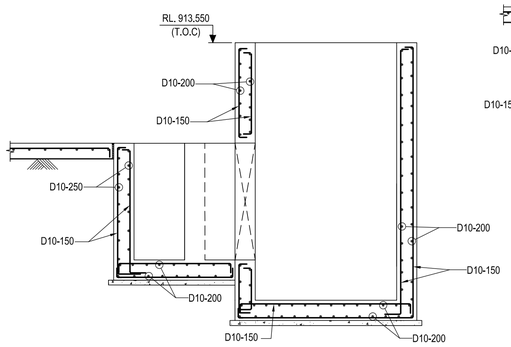


SECTION B-B
(RCC DETAIL)
SCALE 1:30

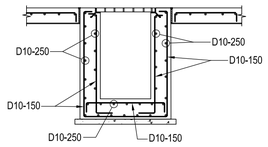


SECTION C-C
(RCC DETAIL)
SCALE 1:30

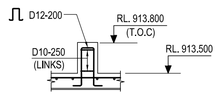


SECTION D-D & E-E
(RCC DETAIL)
SCALE 1:30

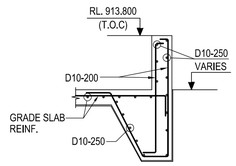


SECTION G-G
SECTION G'-G' (OPPOSITE HAND)
(R.C DETAIL)
SCALE 1:30

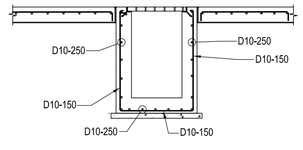


SECTION F-F, F'-F' & S-S
(RCC DETAIL)
SCALE 1:30

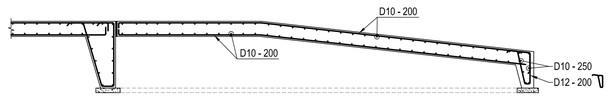


SECTION Z-Z
(R.C DETAIL)
SCALE 1:50

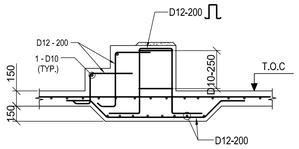


SECTION Z-Z
(R.C DETAIL)
SCALE 1:30

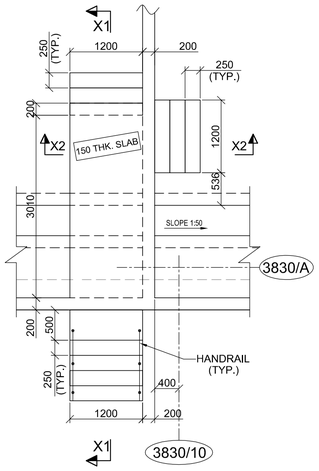


DETAIL-D4
SCALE 1:50

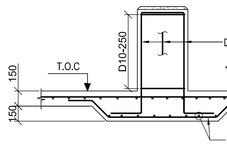


DETAIL - P1
(R.C DETAIL)
SCALE 1:30

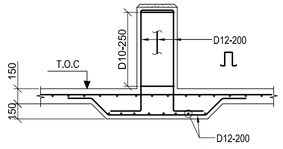


DETAIL - P2
(R.C DETAIL)
SCALE 1:30

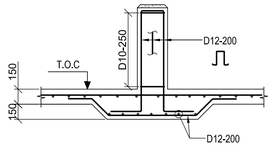


DETAIL - P3
(R.C DETAIL)
SCALE 1:30

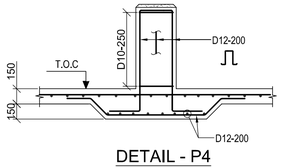


DETAIL - P4
(R.C DETAIL)
SCALE 1:30

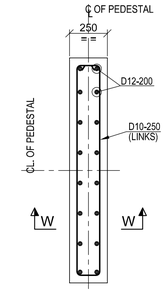


DETAIL OF COLUMN
MKD. C1, C1A, C2, C2A, C3, C3A,
C4, C4A, C5, C5A & C6
(SCALE - 1:20)

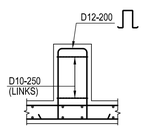


SECTION W-W
(SCALE - 1:20)

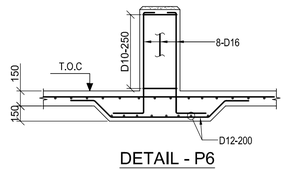


DETAIL - P6
(R.C DETAIL)
SCALE 1:30

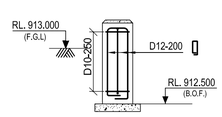


DETAIL OF F1
(RCC DETAIL)
SCALE 1:30

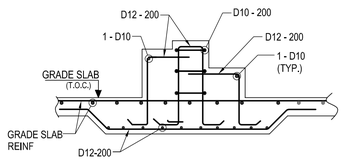


SECTION : S2-S2 & S3-S3
SECTION : S1-S1 (OPPOSITE HAND)
(RCC DETAIL)
(SCALE 1:25)

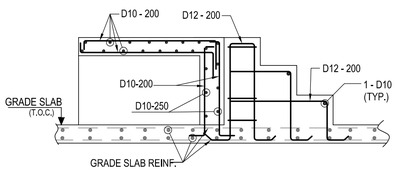


SECTION : X2-X2
(RCC DETAIL)
(SCALE 1:25)

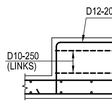


SECTION P-P
(R.C DETAIL)
(SCALE - 1:20)

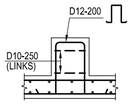

SECTION Q-Q
(R.C DETAIL)
(SCALE - 1:20)

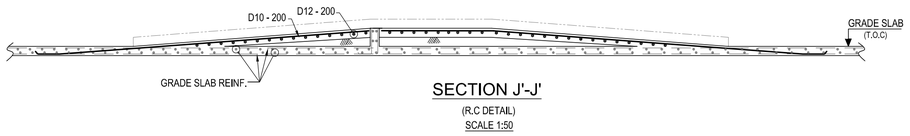

SECTION J'-J'
(R.C DETAIL)
SCALE 1:50

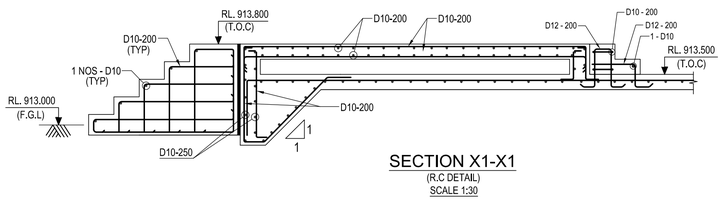

SECTION X1-X1
(R.C DETAIL)
SCALE 1:30

LEGEND :-

R.L. - REDUCED LEVEL
T.O.C - TOP OF CONCRETE
RCC - REINFORCED CEMENT CONCRETE
℄ - CENTRE LINE
F.G.L. - FINISHED GROUND LEVEL.
RC - REINFORCED CONCRETE
MKD. - MARKED
REINF. - REINFORCEMENT
REF. - REFERENCE

NOTES:-

1. ALL DIMENSIONS ARE IN MILLIMETRES AND LEVELS AND CO-ORDINATES ARE IN METRES UNLESS OTHERWISE STATED.
2. FOR DETAILS OF GRADE SLAB REFER DRAWING NO. MD-216-1000-EG-CV-DED-1002.
3. FOR GENERAL ARRANGEMENT DRAWING REFER DRAWING NO. MD-216-3830-EG-CV-GAD-1421.

DOCUMENT NUMBER	REFERENCE DOCUMENTS	REV	DATE	REVISION DESCRIPTION	DRN	CHK	ENG	APP	EMP
		D01	05/05/2023	AS - BUILT	SYA	SJM	SOR	AG	
		C02	12/03/2021	ISSUED FOR CONSTRUCTION & REVISED AS MARKED C02	SYA	SJM	SOR	AG	
		C01	20/01/2021	ISSUED FOR CONSTRUCTION & REVISED AS MARKED C01	SYA	SJM	SOR	AG	
		A01	20/10/2020	ISSUED FOR REFERENCE	PML	SJM	SOR	AG	

RESERVED FOR VENDOR LOGO AND DRAWING NUMBER

LARSEN & TOUBRO

This drawing is the property of LARSEN & TOUBRO and must not be passed on to any person or body not authorized by us to receive it nor be copied or otherwise made use either in full or in part by such person or body without our prior permission in writing.

Outotec

The content of these documents are the sole property of Outotec Oyj. Any rights not expressly granted herein are reserved. Reproduction, transfer or distribution of part or all of the contents in any form without prior written permission of Outotec is prohibited.

MA'ADEN معادن
Saudi Arabian Mining Company شركة التعدين العربية السعودية

This document and the information contained herein is Ma'aden proprietary know-how. This document or any part thereof should not be reproduced, stored in a retrieval system or transmitted by any means, electronic or otherwise, or divulged without prior written permission of Ma'aden.

LARSEN & TOUBRO DRAWING NUMBER			REVISION
019045_450_C_D_24563_001			3
OUTOTEC DRAWING NUMBER		DOCUMENT ID	REVISION
900707__GAU01__AA02__CTB17__38305		OU100704164	3
DRAWN	PML	14/10/2020	MANSOURAH - MASSARAH GOLD PROJECT
CHECKED	SJM	16/10/2020	DETAIL DRAWING
ENGINEER	SOR	14/10/2020	REAGENTS - FLOTATION REAGENTS EQUIPMENT
APPROVED	AG	20/10/2020	RCC DETAILS OF GRADE SLAB
EMPLOYER			
SCALE 1:30	A1		DRAWING NUMBER: MD-216-3830-EG-CV-DED-1424 REV: D01