

DRAWING NUMBER: MD-216-3830-EG-CV-GAD-1001
REV: A02

LEVEL +913.500
1:50

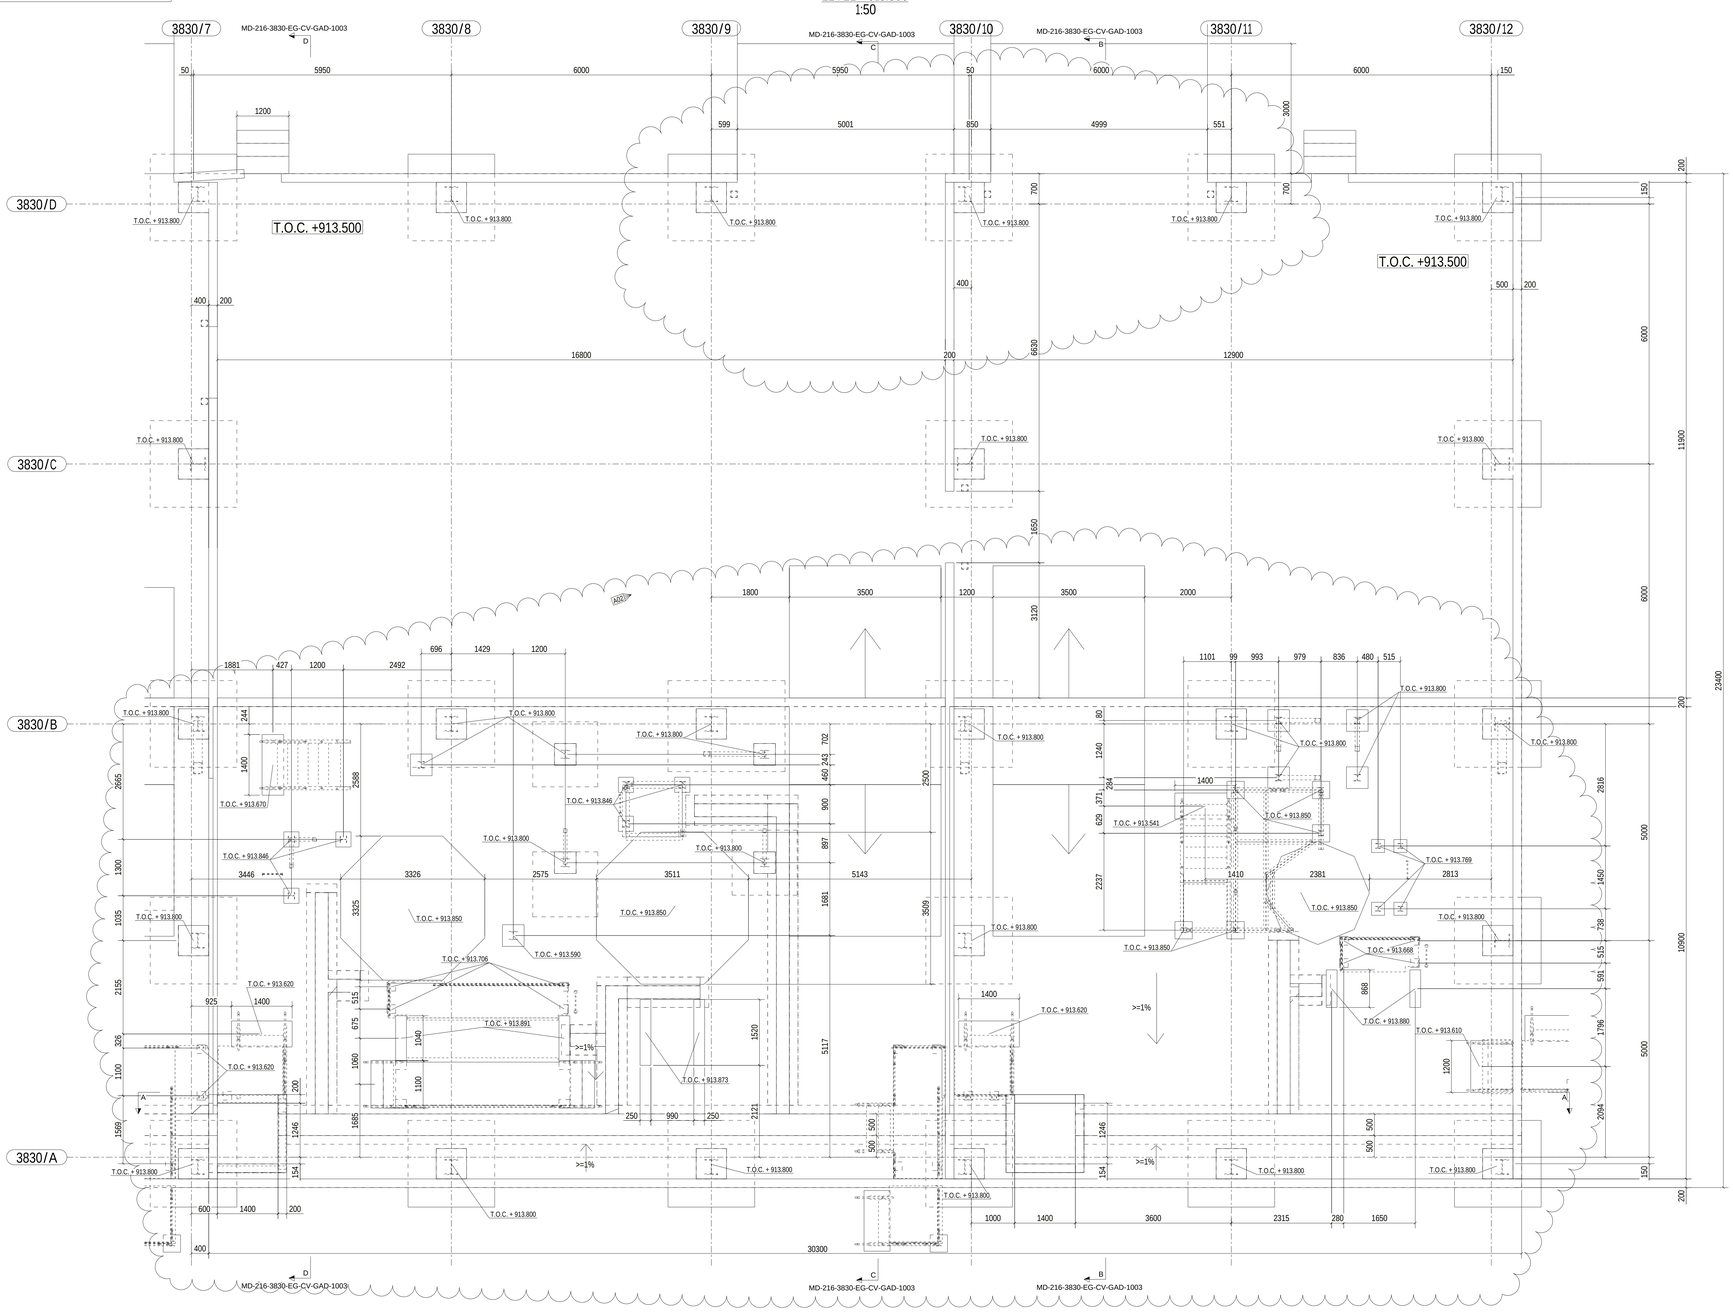

A - A
1:50

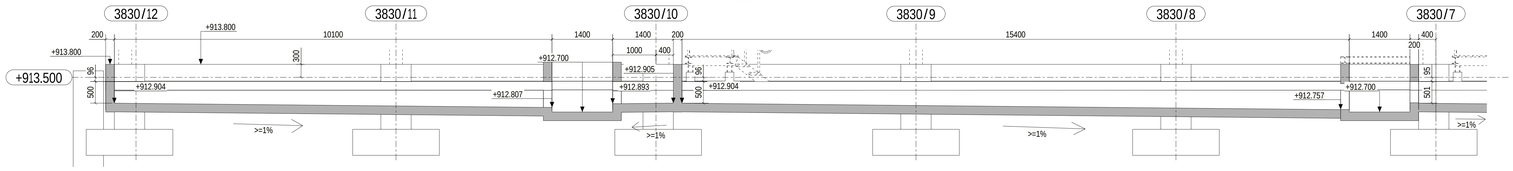


THIS DESIGN IS NOT ISSUED FOR CONSTRUCTION

FINISHED TOP GROUND LEVEL (F.G.L) FOR PROCESS AREA 3830 = RL(+)913.500 m

- CONCRETE ELEMENT FLOOR (PRE-CAST SLAB)
- CONCRETE FLOOR
- CONCRETE FLOOR WITH ACID RESISTANT COATING
- CONCRETE WALL

1. ALL DIMENSIONS ARE IN MILLIMETER, ELEVATIONS ARE IN METER UNLESS OTHERWISE STATED
2. CO-ORDINATES ARE SHOWN IN GENERAL ARRENGEMENT DRAWINGS
3. GRATING TYPE (FRP OR NORMAL) IS SPECIFIED IN GENERAL ARRENGEMENT DRAWINGS
4. F.F.L, F.G.L, T.O.C = FINISHED FLOOR LEVEL, FINISHED GROUND LEVEL, TOP OF CONCRETE, T.O.S, B.O.S, B.O.B, = TOP OF STEEL, BOTTOM OF STEEL, BOTTOM OF BASE PLATE
5. BUILDING DIMENSIONS AND HEIGHTS ARE TENTATIVE, SHALL BE FINALIZED DURING DETAIL ENGINEERING SUBJECT TO MINIMUM AS SHOWN.
6. ALL MAINTENANCE FACILITIES, HANDLING PROVISIONS, ACCESS WAYS, PLATFORMS FOR MAINTENANCE SHALL BE PROVIDED DURING DETAIL ENGINEERING WHICH ARE NOT SHOWN ENTIRELY, THIS DRAWING IS TO BE CONSIDERED AS CONCEPTUAL ARRANGEMENT OF THE FACILITIES.

KEYPLAN

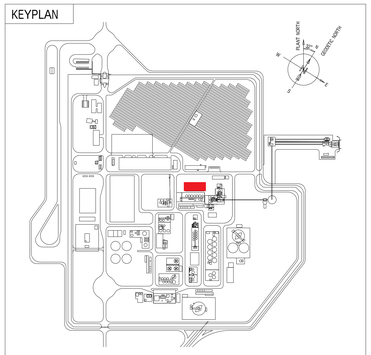

DOCUMENT NUMBER	REFERENCE DOCUMENTS	DOCUMENT NUMBER	REFERENCE DOCUMENTS
MD-216-3830-EG-ST-GAD-1003	SECTIONS	MD-216-1000-EG-ST-CRT-0001	CIVIL,STRUCTURAL AND ARCHITECTURAL DESIGN BASIS
MD-216-3830-EG-ST-GAD-1001	3D VIEW	MD-216-3830-EG-ST-GAD-1002	PLAN VIEW
MD-216-3830-EG-CV-GAD-1002	PLAN AT EL. +913.500	MD-216-3830-EG-CV-GAD-1003	SECTIONS

REV	DATE	REVISION DESCRIPTION	DRN	CHK	ENG	APP	EMP
A02	10.07.2020	Issued for detail design(equipment foundations modified/moved/added)	NikSni	WaLai	LuiPiz	SuoCha	
A01	17.01.2020	ISSUED FOR APPROVAL	AnnFor	WaLai	LuiPiz	SuoCha	

RESERVED FOR VENDOR LOGO AND DRAWING NUMBER

LARSEN & TOUBRO

This drawing is the property of LARSEN & TOUBRO and must not be passed on to any person or body not authorized by us to receive it nor be copied or otherwise made use either in full or in part by such person or body without our prior permission in writing.

Ototec

The content of these documents are the sole property of Ototec Oy. Any rights not expressly granted herein are reserved. Reproduction, transfer or distribution of part or all of the contents in any form without prior written permission of Ototec is prohibited.

MA'ADEN معادن
Saudi Arabian Mining Company شركة معادن العربية السعودية

This document and the information contained herein is Ma'aden proprietary know-how. This document or any part thereof should not be reproduced, stored in a retrieval system or transmitted by any means, electronic or otherwise, or divulged without prior written permission of Ma'aden.

LARSEN & TOUBRO DRAWING NUMBER: REVISION 1
OUTOTEC DRAWING NUMBER: 900707_GAU01_AA02_CTA04_38301
DOCUMENT ID: 0U100668146 REVISION 1

DRAWN	AnnFor	17.01.2020
CHECKED	WaLai	17.01.2020
ENGINEER	LuiPiz	17.01.2020
APPROVED	SuoCha	17.01.2020
EMPLOYER		
SCALE	1:100	A0

MANSOURAH - MASSARAH GOLD PROJECT
CIVIL WORKS GUIDE DRAWING
3830 FLOTATION REAGENTS
PLAN AT EL. +913.500

DRAWING NUMBER: MD-216-3830-EG-CV-GAD-1001
REV: A02

Tekla Structures