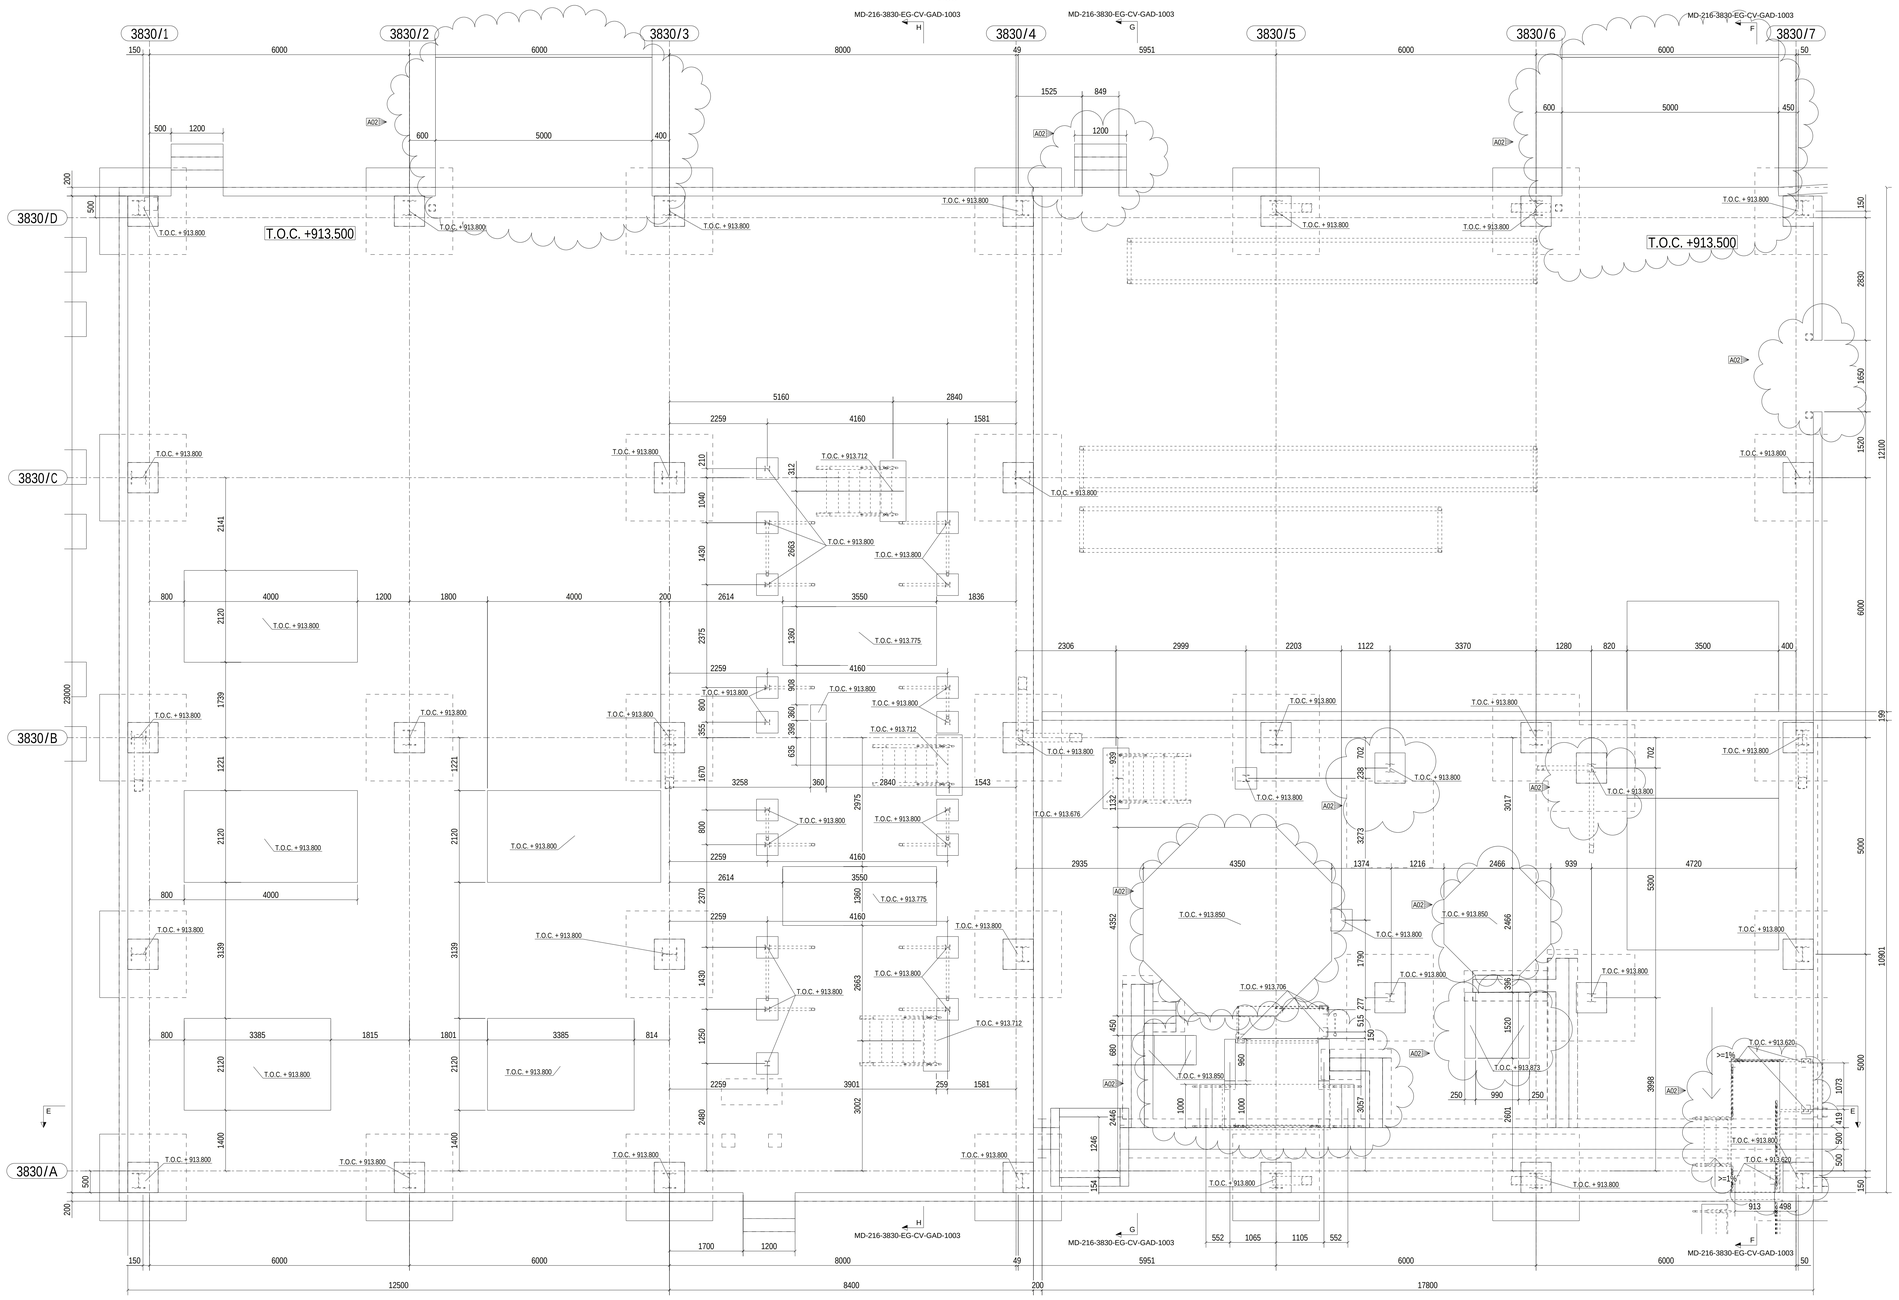
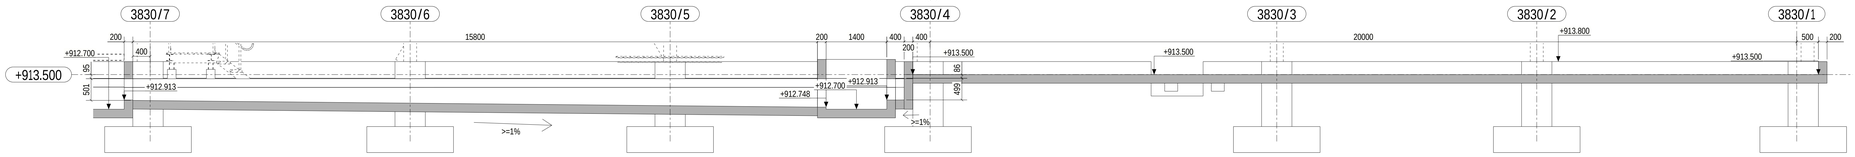
DRAWING NUMBER: MD-216-3830-EG-CV-GAD-1002
REV: A02

## LEVEL +913.500
1:50




## E - E
1:50



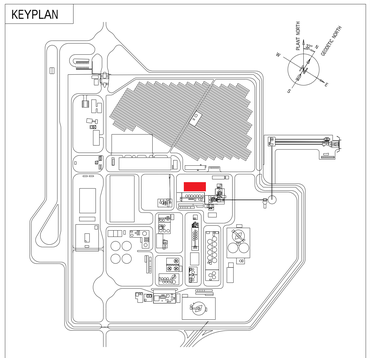

THIS DESIGN IS NOT ISSUED FOR CONSTRUCTION

FINISHED TOP GROUND LEVEL (F.G.L) FOR PROCESS AREA 3830 = RL(+)913.500 m

- CONCRETE ELEMENT FLOOR (PRE-CAST SLAB)
- CONCRETE FLOOR
- CONCRETE FLOOR WITH ACID RESISTANT COATING
- CONCRETE WALL

1. ALL DIMENSIONS ARE IN MILLIMETER, ELEVATIONS ARE IN METER UNLESS OTHERWISE STATED
2. CO-ORDINATES ARE SHOWN IN GENERAL ARRENGEMENT DRAWINGS
3. GRATING TYPE (FRP OR NORMAL) IS SPECIFIED IN GENERAL ARRENGEMENT DRAWINGS
4. F.F.L, F.G.L, T.O.C = FINISHED FLOOR LEVEL, FINISHED GROUND LEVEL, TOP OF CONCRETE, T.O.S, B.O.S, B.O.B, = TOP OF STEEL, BOTTOM OF STEEL, BOTTOM OF BASE PLATE
5. BUILDING DIMENSIONS AND HEIGHTS ARE TENTATIVE, SHALL BE FINALIZED DURING DETAIL ENGINEERING SUBJECT TO MINIMUM AS SHOWN.
6. ALL MAINTENANCE FACILITIES, HANDLING PROVISIONS, ACCESS WAYS, PLATFORMS FOR MAINTENANCE SHALL BE PROVIDED DURING DETAIL ENGINEERING WHICH ARE NOT SHOWN ENTIRELY. THIS DRAWING IS TO BE CONSIDERED AS CONCEPTUAL ARRANGEMENT OF THE FACILITIES.

KEYPLAN



| DOCUMENT NUMBER | REFERENCE DOCUMENTS |
|---|---|
| MD-216-3830-EG-ST-GAD-1003 | SECTIONS |
| MD-216-3830-EG-ST-GAD-1001 | 3D VIEW |
| MD-216-3830-EG-CV-GAD-1001 | PLAN AT EL. +913.500 |

| DOCUMENT NUMBER | REFERENCE DOCUMENTS |
|---|---|
| MD-216-1000-EG-ST-CRT-0001 | CIVIL,STRUCTURAL AND ARCHITECTURAL DESIGN BASIS |
| MD-216-3830-EG-ST-GAD-1002 | PLAN VIEW |
| MD-216-3830-EG-CV-GAD-1003 | SECTIONS |

| REV | DATE | REVISION DESCRIPTION | DRN | CHK | ENG | APP | EMP |
|---|---|---|---|---|---|---|---|
| A02 | 10.07.2020 | Issued for detail design (concrete foundations modified/moved/removed/added) | NkSrn | MkLai | LuiPiz | SuoCha | |
| A01 | 17.01.2020 | ISSUED FOR APPROVAL | AmFor | MkLai | LuiPiz | SuoCha | |

RESERVED FOR VENDOR LOGO AND DRAWING NUMBER

LARSEN & TOUBRO DRAWING NUMBER: —
REVISION: 1

OUTOTEC DRAWING NUMBER: 900707_GAU01_AA02_CTA04_38302
DOCUMENT ID: OU100668147
REVISION: 1

| | | |
|---|---|---|
| DRAWN | AmFor | 17.01.2020 |
| CHECKED | MkLai | 17.01.2020 |
| ENGINEER | LuiPiz | 17.01.2020 |
| APPROVED | SuoCha | 17.01.2020 |
| EMPLOYER | | |
| SCALE | 1:100 | A0 |

MANSOURAH - MASSARAH GOLD PROJECT
CIVIL WORKS GUIDE DRAWING
3830 FLOTATION REAGENTS
PLAN AT EL. +913.500

DRAWING NUMBER: MD-216-3830-EG-CV-GAD-1002
REV: A02

LARSEN & TOUBRO
This drawing is the property of LARSEN & TOUBRO and must not be passed on to any person or body not authorized by us to receive it nor be copied or otherwise made use either in full or in part by such person or body without our prior permission in writing.

Outotec
The content of these documents are the sole property of Outotec Oy. Any rights not expressly granted herein are reserved. Reproduction, transfer or distribution of part or all of the contents in any form without prior written permission of Outotec is prohibited.

MA'ADEN معادن
Saudi Arabian Mining Company شركة معادن العربية السعودية
This document and the information contained herein is Ma'aden proprietary know-how. This document or any part thereof should not be reproduced, stored in a retrieval system or transmitted by any means, electronic or otherwise, or divulged without prior written permission of Ma'aden.

Data Structures