


DRAWING NUMBER: MD-216-3830-EG-CV-GAD-1417
REV: D01

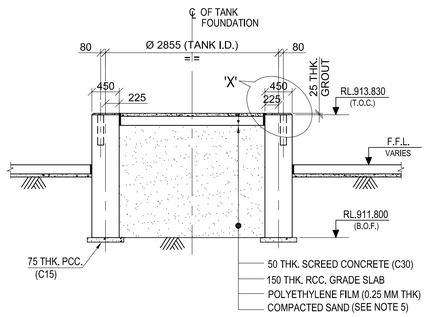


SECTION : A-A
SCALE 1:50

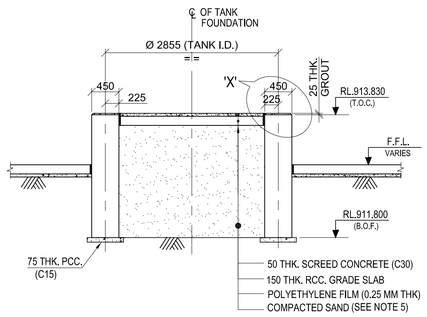


SECTION : B-B
SCALE 1:50

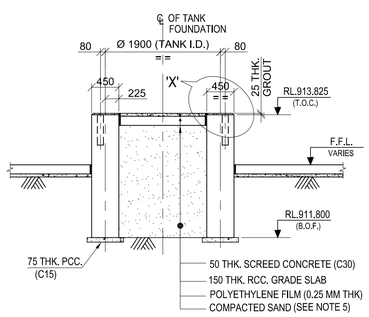


SECTION : C-C
SCALE 1:50

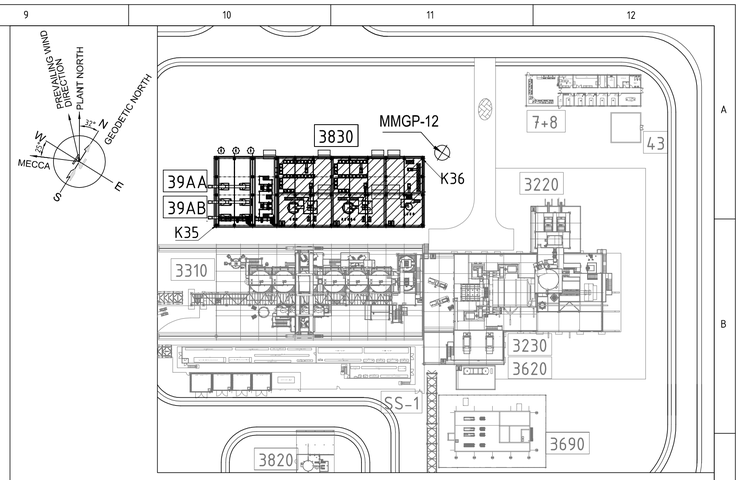


KEY PLAN
SCALE 1:1000

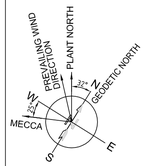


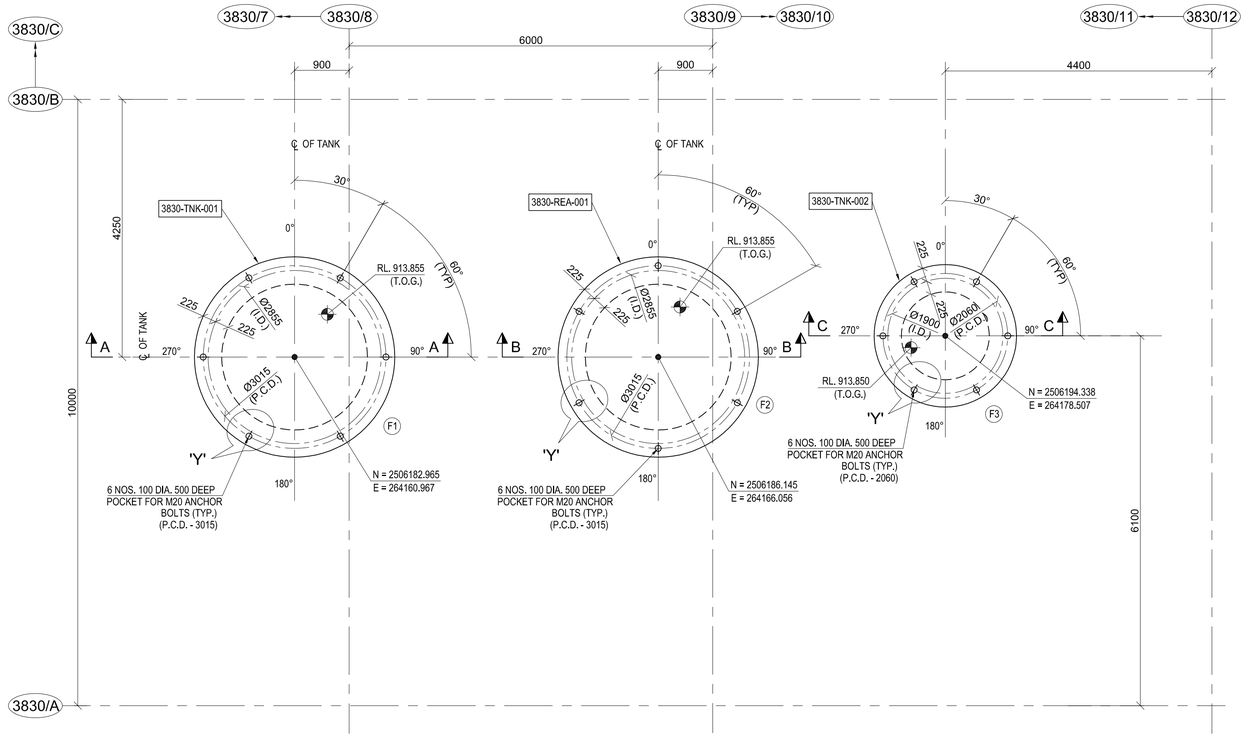


LAYOUT OF FOUNDATION
SCALE 1:50

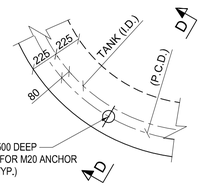

DETAIL : 'Y'
SCALE 1:25

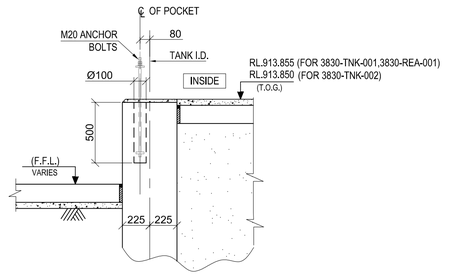

SECTION : D-D
SCALE 1:25

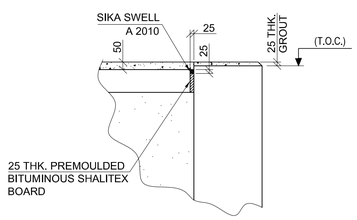

DETAIL - 'X'
SCALE 1:20

LEGEND :-

R.L. - REDUCED LEVEL
℄ - CENTRE LINE
T.O.C. - TOP OF CONCRETE
TYP. - TYPICAL
I.D. - INTERNAL DIAMETER
T.O.G. - TOP OF GROUT
B.O.F. - BOTTOM OF FOUNDATION
F.G.L. - FINISHED GROUND LEVEL.
EQV. - EQUIVALENT
F.F.L. - FINISHED FLOOR LEVEL
P.C.C - PLAIN CEMENT CONCRETE
DET. - DETAIL
FDN. - FOUNDATION
DIA. - DIAMETER
THK. - THICK
C/C - CENTRE TO CENTRE
R.C.C - REINFORCED CEMENT CONCRETE
P.C.D. - PITCH CIRCLE DIAMETER
MKD. - MARKED
Ø - DIAMETER

NOTES:-

1. ALL DIMENSIONS ARE IN MILLIMETRES AND LEVELS AND CO-ORDINATES ARE IN METRES UNLESS OTHERWISE STATED.
2. GRADE OF CONCRETE SHALL BE C35 (35MPa) FOR FOUNDATION, C30 C30 (30MPa) FOR GRADE SLAB & C15 (15MPa) FOR BLINDING CONCRETE.
3. NET SAFE BEARING CAPACITY OF SOIL AT BOTTOM OF FOUNDATION IS CONSIDERED AS 350KN/ SQ. M
4. IF ANY PART OF FOUNDATION COMES ON BACKFILL ZONE OF ADJACENT FOUNDATION OR ANY LOOSE SOIL ARE ENCOUNTERED BELOW FOUNDATION LEVEL THE SAME SHALL BE REMOVED AND FILLED WITH PCC.
5. SAND SHALL BE COMPACTED TO A MAXIMUM DEPTH OF 300MM AND SHALL BE COMPACTED TO 80% RELATIVE DENSITY AS DETERMINED BY ASTM D4253 AND ASTM D4254.

DOCUMENT NUMBER	REFERENCE DOCUMENTS	REV	DATE	REVISION DESCRIPTION	DRN	CHK	ENG	APP	EMP
MD-216-3830-EG-GV-DED-1420	RCC. DET. FOR 3830-TNK-001, 002 & 3830-REA-001								
MD-216-1000-EG-ST-CRT-1001	CIVIL, STRUCTURAL & ARCHITECTURAL - DESIGN CRITERIA	D01	03/07/2023	AS - BUILT	PML	SJM	SOR	AG	
MD-216-3830-EG-ME-GAD-1017	FLOTATION REAGENTS, BLOWERS AND PLANT AIR	C02	26/09/2020	ISSUED FOR CONSTRUCTION & REVISED AS MARKED (C02)	PML	SJM	SOR	AG	
MD-216-3830-EG-CV-GAD-1002	3830 FLOTATION REAGENTS	C01	08/07/2020	ISSUED FOR CONSTRUCTION AND REVISED AS MKD. (C01)	ABS	SJM	SOR	AG	
MD-216-3830-EG-CV-GAD-1001	3830 FLOTATION REAGENTS	A01	06/06/2020	ISSUED FOR REFERENCE	ABS	SJM	SOR	AG	

RESERVED FOR VENDOR LOGO AND DRAWING NUMBER

LARSEN & TOUBRO

This drawing is the property of LARSEN & TOUBRO and must not be passed on to any person or body not authorized by us to receive it nor be copied or otherwise made use either in full or in part by such person or body without our prior permission in writing.

Outotec

The content of these documents are the sole property of Outotec Oyj. Any rights not expressly granted herein are reserved. Reproduction, transfer or distribution of part or all of the contents in any form without prior written permission of Outotec is prohibited.

MA'ADEN معادن
Saudi Arabian Mining Company شركة معادن العربية السعودية

This document and the information contained herein is Ma'aden proprietary know-how. This document or any part thereof should not be reproduced, stored in a retrieval system or transmitted by any means, electronic or otherwise, or divulged without prior written permission of Ma'aden.

DRAWN	ABS	02/06/2020
CHECKED	SJM	05/06/2020
ENGINEER	SOR	02/06/2020
APPROVED	AG	06/06/2020
EMPLOYER		
SCALE	1:50, 1:25, 1:20	A1

LARSEN & TOUBRO DRAWING NUMBER: 019045_450_C_G_24158_002 — REVISION: 3
OUTOTEC DRAWING NUMBER: 900707 _GAU01 _AA02_MTL01 _38314 — DOCUMENT ID: OU100687748 — REVISION: 3

MANSOURAH - MASSARAH GOLD PROJECT
GENERAL ARRANGEMENT DRAWING
REAGENTS - FLOTATION REAGENTS EQUIPMENT
FDN. DET. FOR 3830-TNK-001,002 & 3830-REA-001

DRAWING NUMBER: MD-216-3830-EG-CV-GAD-1417 — REV: D01