


DRAWING NUMBER: MD - 216 - 3830 - EG - CV - GAD - 1421 | REV: D01

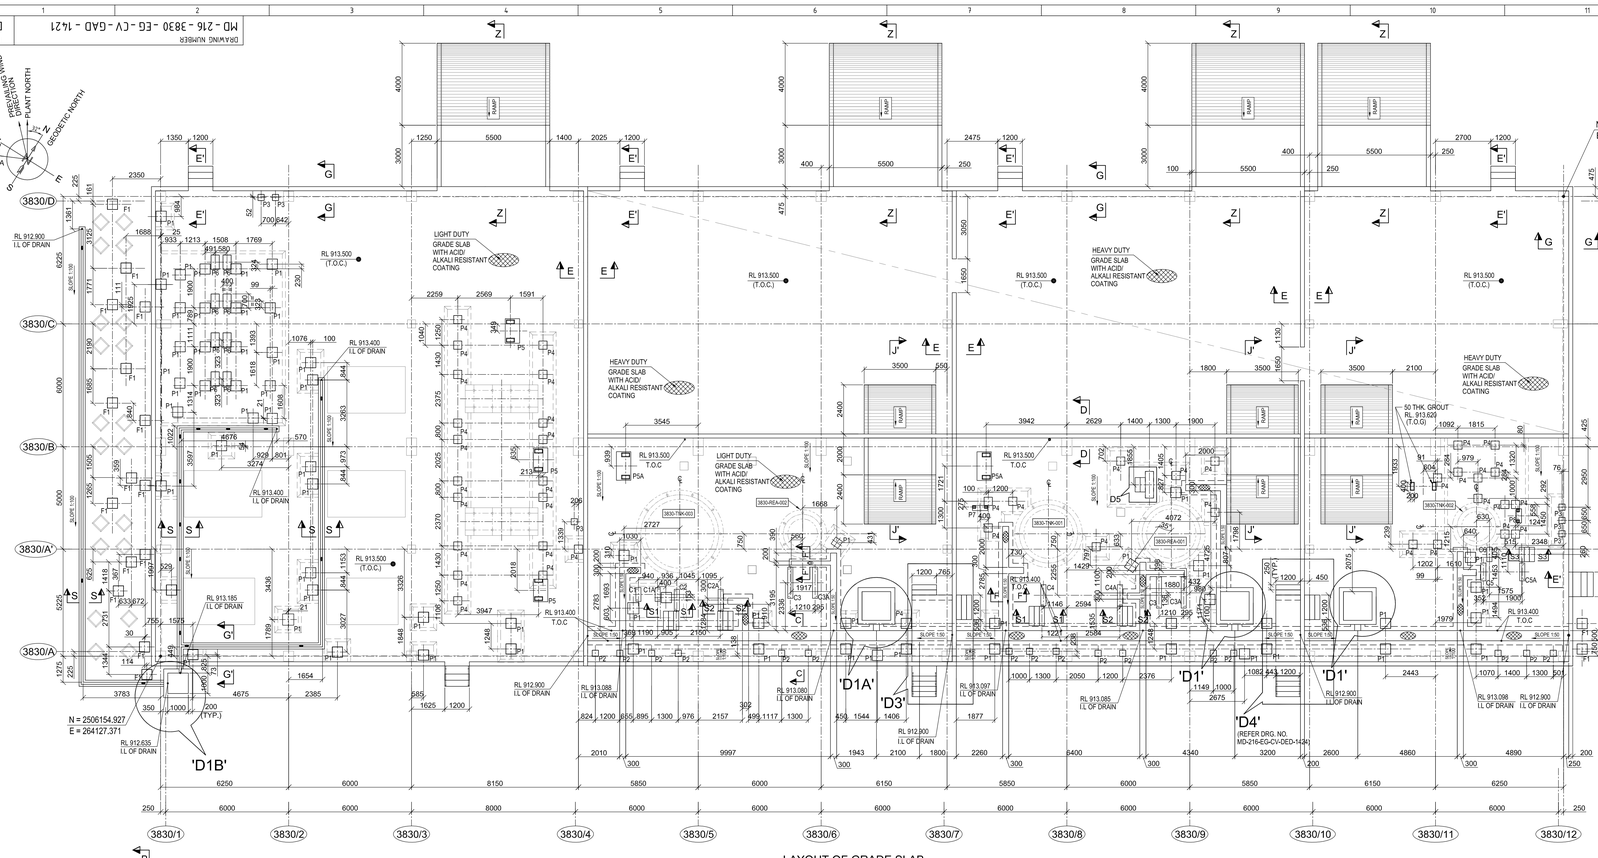


LAYOUT OF GRADE SLAB
(SCALE - 1:100)

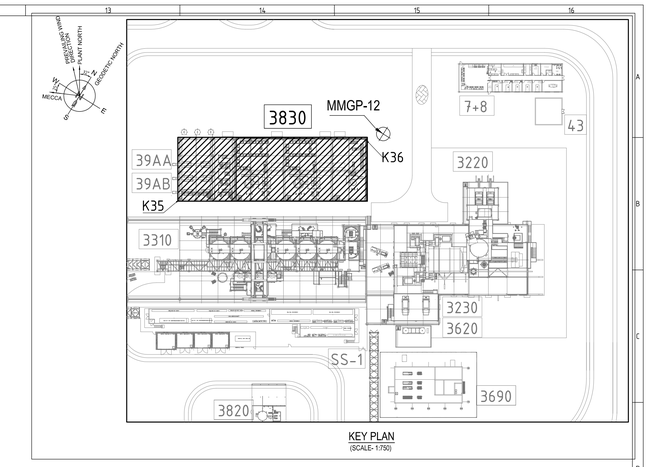


KEY PLAN
(SCALE- 1:750)

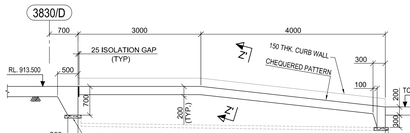


SECTION Z-Z
SCALE 1:50

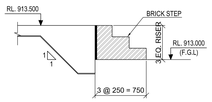


SECTION E'-E'
SCALE 1:30

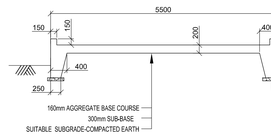


DETAIL-D3
SCALE 1:50

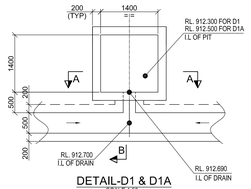


DETAIL-D1 & D1A
SCALE 1:50

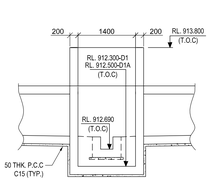


SECTION A-A
SCALE 1:50

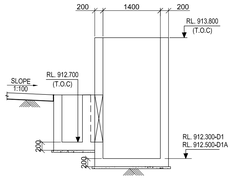


SECTION B-B
SCALE 1:50

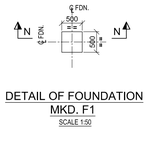


DETAIL OF FOUNDATION MKD. F1
SCALE 1:50

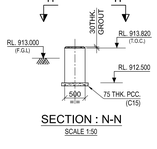


SECTION : N-N
SCALE 1:50

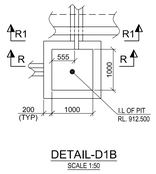


DETAIL-D1B
SCALE 1:50

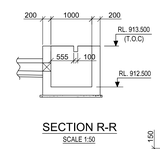


SECTION R-R
SCALE 1:50

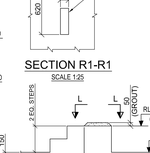


SECTION R1-R1
SCALE 1:25

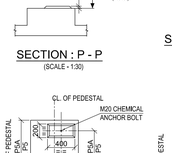


SECTION : P - P
(SCALE - 1:30)

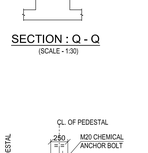

SECTION : Q - Q
(SCALE - 1:30)

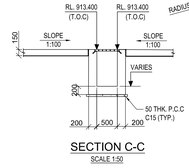


SECTION C-C
SCALE 1:50

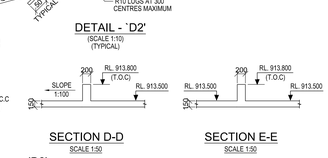


DETAIL - `D2'
(SCALE 1:10) (TYPICAL)

SECTION D-D
SCALE 1:50


SECTION E-E
SCALE 1:50

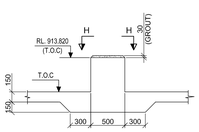


DETAIL - P1
SCALE 1:30

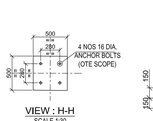


VIEW : H-H
SCALE 1:30

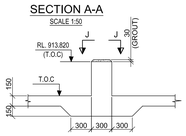


DETAIL - P2
SCALE 1:30

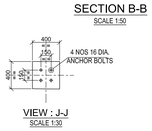


VIEW : J-J
SCALE 1:30

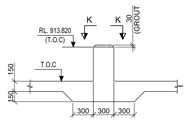


DETAIL - P3
SCALE 1:30

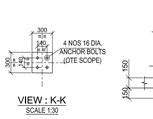

VIEW : K-K
SCALE 1:30

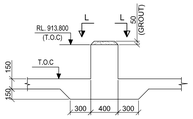

DETAIL - P4
SCALE 1:30

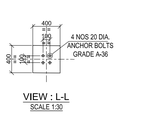

VIEW : L-L
SCALE 1:30



SECTION Z-Z
SCALE 1:30


DETAIL-D5
SCALE 1:30




DETAIL OF PEDESTAL MKD. P5 & P5A
(PEDESTAL ORIENTATION TREATED AS PER LAYOUT PLAN)
(SCALE - 1:30)




DETAIL OF PEDESTAL MKD. P7 & P8
(PEDESTAL ORIENTATION TREATED AS PER LAYOUT PLAN)
(SCALE - 1:30)

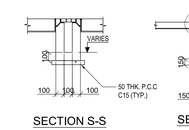


SECTION S-S
SCALE 1:25

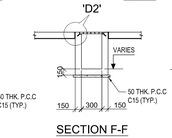


SECTION F-F
SCALE 1:50

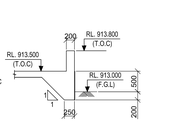


SECTION G-G
SECTION G'-G' (OPPOSITE HAND)

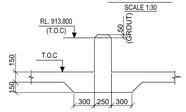


SECTION T-T
SCALE 1:30

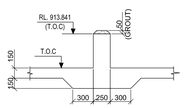


SECTION U-U
SCALE 1:30

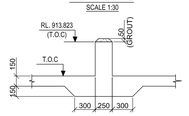


SECTION V-V
SCALE 1:30

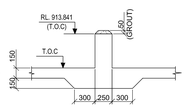


SECTION W-W
SCALE 1:30

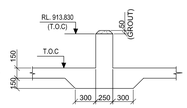


SECTION X-X
SCALE 1:30

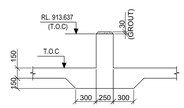

SECTION Y-Y
SCALE 1:30

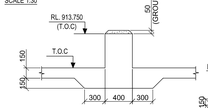


DETAIL - P6
SCALE 1:30

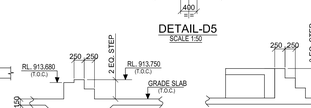


SECTION : S2-S2
SECTION : S1-S1 (OPPOSITE HAND)
(SCALE 1:50)




SECTION : X2-X2
(SCALE 1:50)

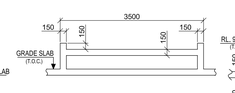


SECTION : J"-J"
(SCALE 1:50)

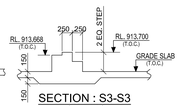


SECTION : S3-S3
(SCALE 1:50)

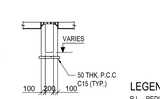


SECTION F'-F'
SCALE 1:50

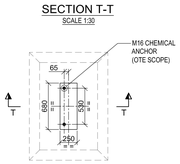


DETAIL - C1
DETAIL - C1A (OPPOSITE HAND)
SCALE 1:30

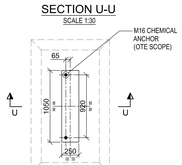


DETAIL - C2
DETAIL - C2A (OPPOSITE HAND)
SCALE 1:30

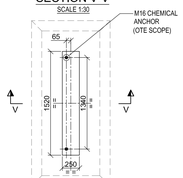


DETAIL - C3
DETAIL - C3A (OPPOSITE HAND)
SCALE 1:30

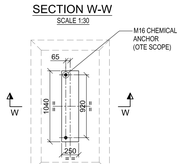


DETAIL - C4
DETAIL - C4A (OPPOSITE HAND)
SCALE 1:30

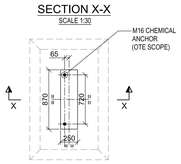


DETAIL - C5
DETAIL - C5A (OPPOSITE HAND)
SCALE 1:30

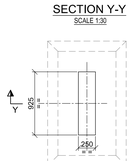

DETAIL - C6
SCALE 1:30

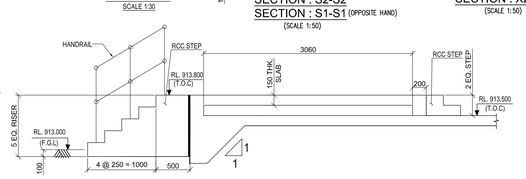

SECTION X1-X1
SCALE 1:30

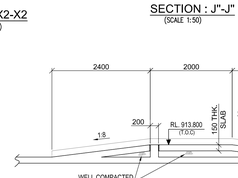

SECTION : J'-J'
(SCALE 1:50)

LEGEND :-
R.L - REDUCED LEVEL
I.L - INVERT LEVEL
THK. - THICK
TYP. - TYPICAL
T.O.C - TOP OF CONCRETE
℄ - CENTRE LINE
P.C.C - PLAIN CEMENT CONCRETE
F.G.L - FINISHED GROUND LEVEL.
FDN. - FOUNDATION
EQ. - EQUAL
T.O.G. - TOP OF GROUT
P.C.C - PLAIN CEMENT CONCRETE

NOTES:-
1. ALL DIMENSIONS ARE IN MILLIMETRES AND LEVELS AND CO-ORDINATES ARE IN METRES UNLESS OTHERWISE STATED.
2. FOR DETAILS OF GRADE SLAB REFER DRAWING NO. MD-216-1000-EG-CV-DED-1002.
3. FOR DETAILS OF EMBEDDED CONDUITS REFER SEPARATE DRAWING.
4. THIS DRAWING SHALL BE READ IN CONJUNCTION WITH DRAWING NO. MD-216-3830-EG-CV-DED-1424.

DOCUMENT NUMBER	REFERENCE DOCUMENTS	REV	DATE	REVISION DESCRIPTION	DRN	CHK	ENG	APP	EMP
		D01	03/07/2023	AS - BUILT	SYA	SJM	SOR	AG	
		C02	12/03/2021	ISSUED FOR CONSTRUCTION & REVISED AS MARKED _02	SYA	SJM	SOR	AG	
		C01	20/01/2021	ISSUED FOR CONSTRUCTION & REVISED AS MARKED _01	SYA	SJM	SOR	AG	
		A01	20/10/2020	ISSUED FOR REFERENCE	PML	SJM	SOR	AG	

RESERVED FOR VENDOR LOGO AND DRAWING NUMBER

LARSEN & TOUBRO

This drawing is the property of LARSEN & TOUBRO and must not be passed on to any person or body not authorised by us to receive it nor be copied or otherwise made use either in full or in part by such person or body without our prior permission in writing.

Outotec

The content of these documents are the sole property of Outotec Oyj. Any rights not expressly granted herein are reserved. Reproduction, transfer or distribution of part or all of the contents in any form without prior written permission of Outotec is prohibited.

MA'ADEN معادن
Saudi Arabian Mining Company شركة المعادن العربية السعودية

This document and the information contained herein is Ma'aden proprietary know-how. This document or any part thereof should not be reproduced, stored in a retrieval system or transmitted by any means, electronic or otherwise, or divulged without prior written permission of Ma'aden.

LARSEN & TOUBRO DRAWING NUMBER	019045_450_C_G_24562_001	REVISION 3
OUTOTEC DRAWING NUMBER	900707__GAU01__AA02_MTL01__38333	DOCUMENT ID OU100704162 / REVISION 3
DRAWN	PML	14/10/2020
CHECKED	SJM	16/10/2020
ENGINEER	SOR	14/10/2020
APPROVED	AG	20/10/2020
EMPLOYER		
SCALE	1:100, 1:50, 1:25, 1:20	A0

MANSOURAH - MASSARAH GOLD PROJECT
GENERAL ARRANGEMENT DRAWING
REAGENTS - FLOTATION REAGENTS EQUIPMENT
GA & DETAILS OF GRADE SLAB

DRAWING NUMBER: MD - 216 - 3830 - EG - CV - GAD - 1421 | REV: D01