

DRAWING NUMBER: MD-216-49PR-EG-CV-GAD-V553-1056 | REV: D01

PLAN 1:50

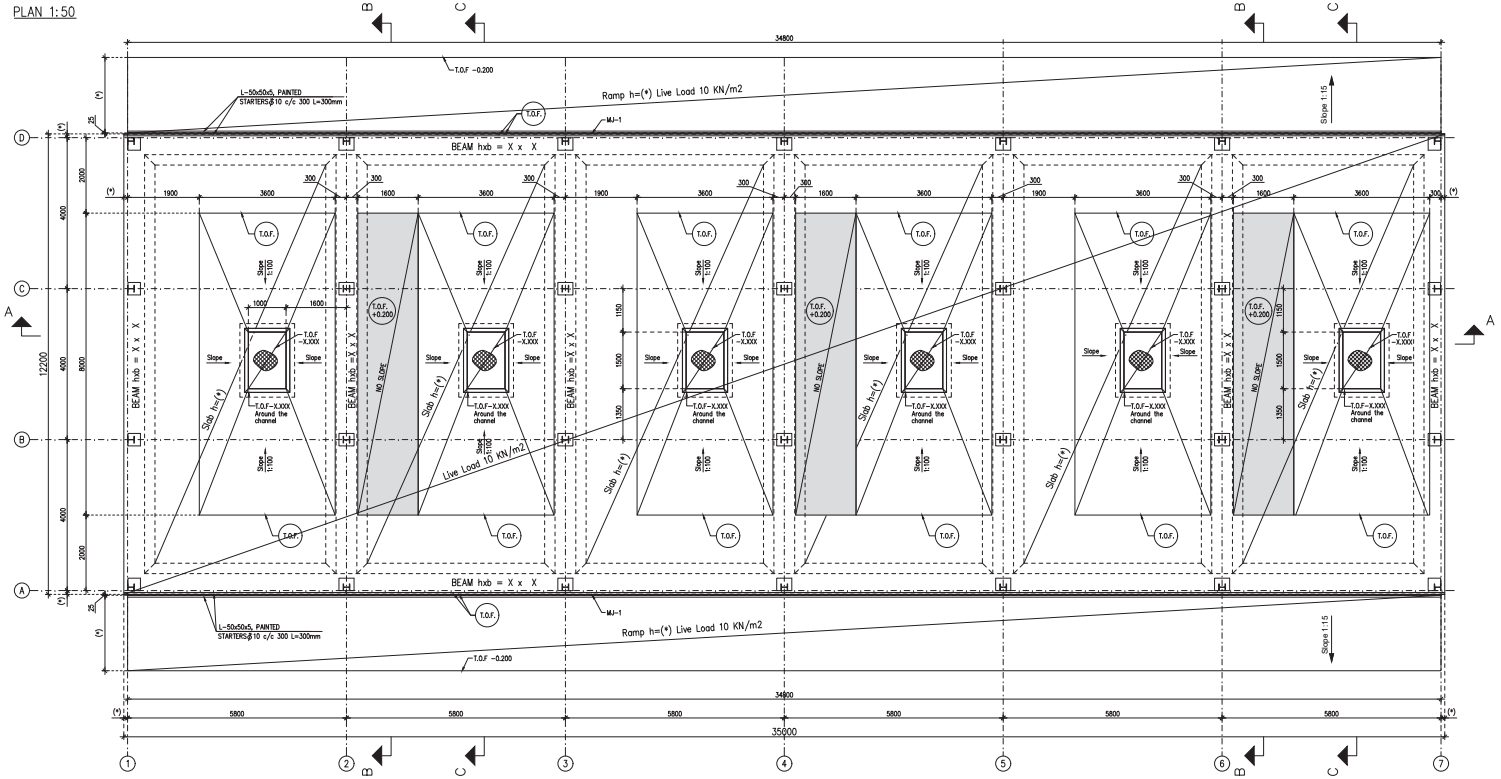


MJ-1 1:20

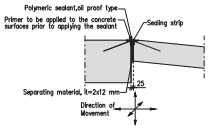


NOTE:
1) This drawing shall be mainly used for dimensional information purposes. Final construction drawing which concerns reinforcing and possible piling of the foundation to be done by the civil designer in accordance with the soil investigations at site. However below are given some points made by Wärtsilä.
2) Beam size and location according to final design
3) MJ location according to final design
4) Conduit locations according to Cable Conduit design.
5) Drain points according to Unit Location drawing
6) Location and size of the drain channels to be checked according to final design

NOTES:
1. LOCATION AND TOP OF FOUNDATION LEVEL T.O.F. ACCORDING TO FOUNDATION LOCATION DRAWING.
2. * & *FOUNDATION SIZE AND LOCATION ACCORDING TO FINAL DESIGN.


A–A 1:50

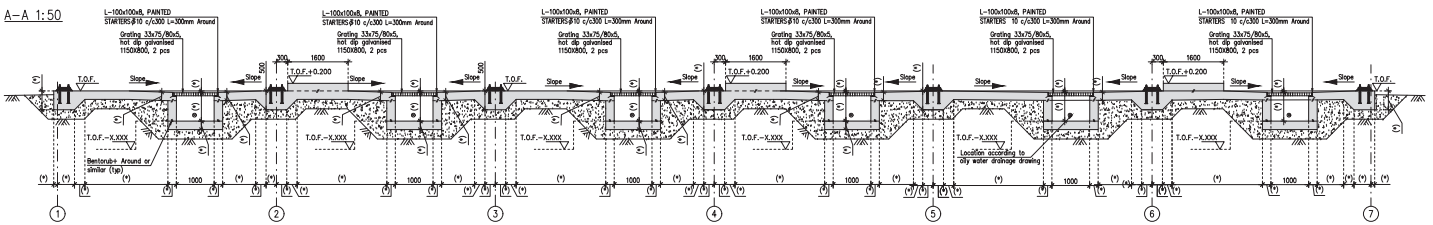

B–B 1:50

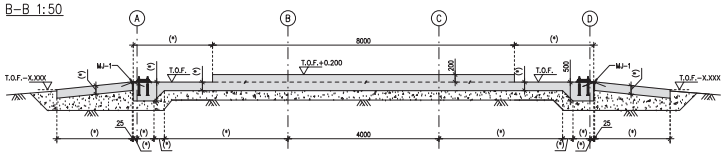

C–C 1:50

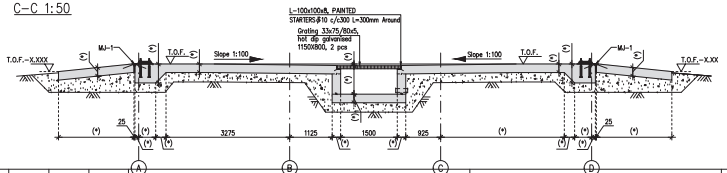

DOCUMENT NUMBER	REFERENCE DOCUMENTS	REV	DATE	REVISION DESCRIPTION	DRN	CHK	ENG	APP	EMP
		D01	17/05/2023	AS - BUILT	--	SJK	--	NBR	
		C01	12/11/2020	ISSUED FOR CONSTRUCTION	--	SJK	--	NBR	
		A03	13/10/2020	REVISED BASED ON EMPLOYER COMMENTS DATED 18/07/2020	--	SJK	--	NBR	
		A02	20/06/2020	REVISED BASED ON EMPLOYER COMMENTS DATED 10/06/2020	--	SJK	--	NBR	
		A01	20/05/2020	ISSUED FOR REFERENCE	--	SJK	--	NBR	

WÄRTSILÄ

© Wärtsilä Finland Oy
Energy Business

DRAWING NUMBER					REVISION
DBAF507548					a
DATE	12-Oct-2020	DATE	13-Oct-2020	DATE	13-Oct-2020
DRAWN	PMM	CHECKED	Giridhar	APPROVED	Amjad

LARSEN & TOUBRO DRAWING NUMBER: 019045_008_M_V_12177_001 — REVISION: 4

OUTOTEC DRAWING NUMBER: 900707_GAU01_WG01_MTL01_45072 — DOCUMENT ID: OU100686673 — REVISION: 4

LARSEN & TOUBRO
This drawing is the property of LARSEN & TOUBRO and must not be passed on to any person or body not authorized by us to receive it nor be copied or otherwise made use either in full or in part by such person or body without our prior permission in writing.

Outotec
The content of these documents are the sole property of Outotec Oyj. Any rights not expressly granted herein are reserved. Reproduction, transfer or distribution of part or all of the contents in any form without prior written permission of Outotec is prohibited.

MA'ADEN معادن
This document and the information contained herein is Ma'aden proprietary know-how. This document or any part thereof should not be reproduced, stored in a retrieval system or transmitted by any means, electronic or otherwise, or divulged without prior written permission of Ma'aden.

DRAWN	--	--	MANSOURAH-MASSARAH GOLD PROJECT
CHECKED	SJK	18/05/2020	GENERAL ARRANGEMENT DRAWING
ENGINEER	--	--	POWER GENERATION
APPROVED	NBR	20/05/2020	FUEL UNLOADING AREA-FOUNDATION
EMPLOYER			
SCALE	1:50	A1	DRAWING NUMBER: MD-216-49PR-EG-CV-GAD-V553-1056 — REV: D01