
DRAWING NUMBER MD-216-49PR-EG-CV-GAD-V553-1057 REV D01


PLAN 1:50

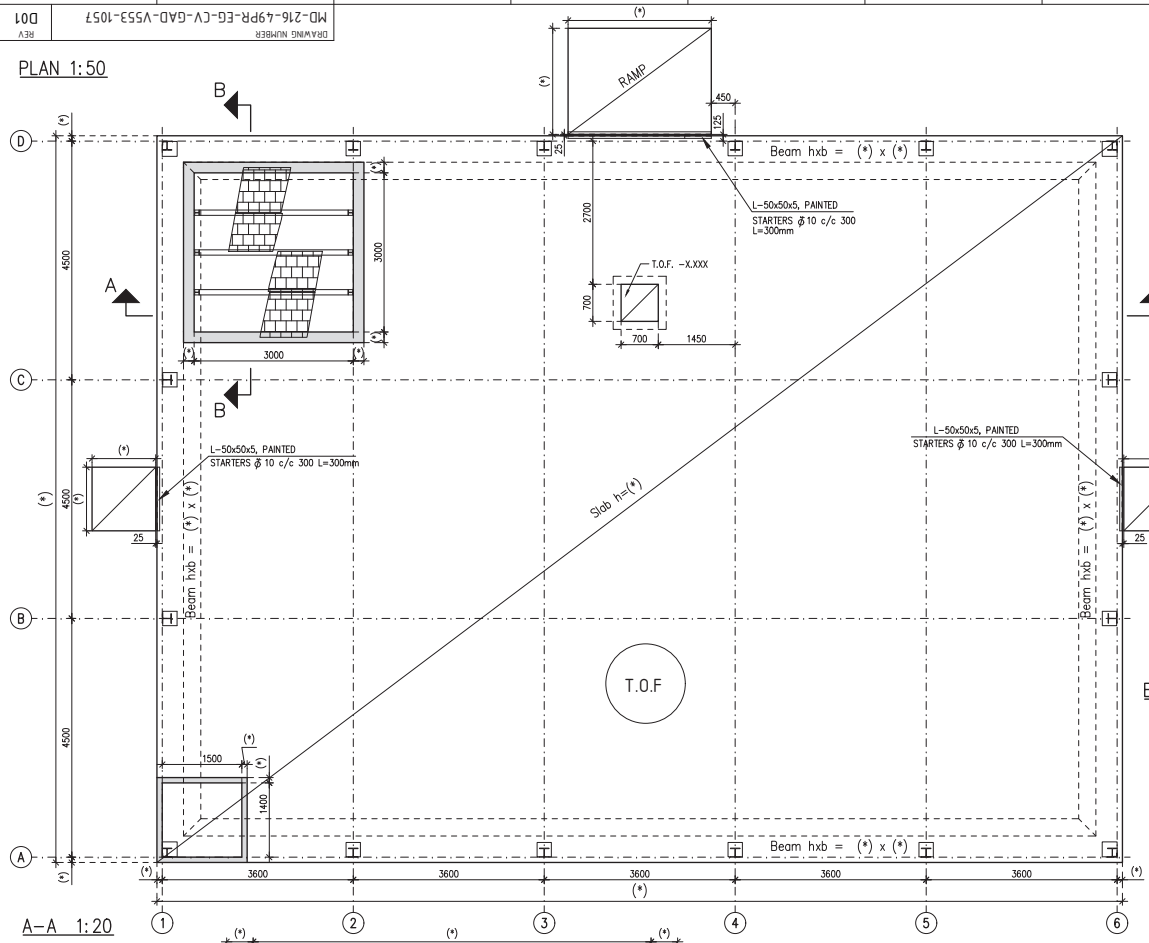


NOTE:
1) This drawing shall be mainly used for dimensional information purposes. Final construction drawing which concerns reinforcing and possible piling of the foundation to be done by the civil designer in accordance with the soil investigations at site. However below are given some points made by Wartsilg.
2) Beam size and location according to final design
3) MJ location according to final design
4) Conduit locations according to Cable Conduit design.
5) Drain points according to Unit Location drawing
6) Location and size of the drain channels to be checked according to final design

NOTES:
1. TOP OF FOUNDATIONS
   T.O.F. +0.000 = (FFL) +913.600 m
2. " * "FOUNDATION SIZE AND LOCATION ACCORDING TO FINAL DESIGN.

B–B 1:20

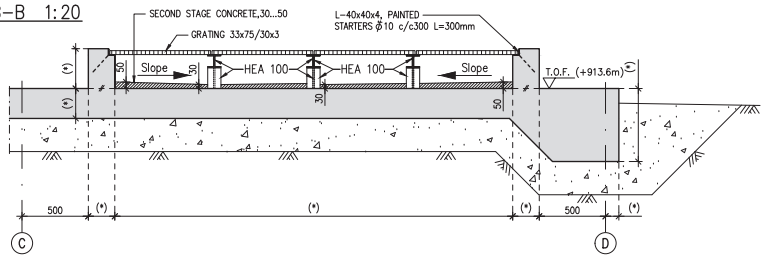

A–A 1:20

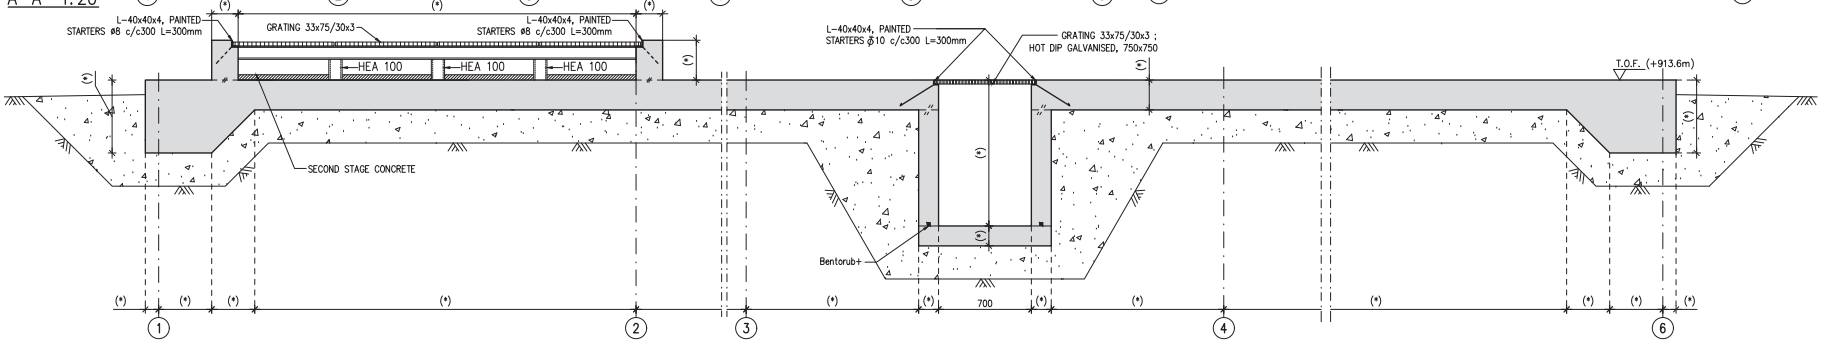

REV	DATE	REVISION DESCRIPTION	DRN	CHK	ENG	APP	EMP
D01	03/07/2023	AS - BUILT	--	SJK	--	NBR	
C01	04/07/2020	ISSUED FOR CONSTRUCTION	--	SJK	--	NBR	
A01	20/05/2020	ISSUED FOR REFERENCE	--	SJK	--	NBR	

DOCUMENT NUMBER | REFERENCE DOCUMENTS

WÄRTSILÄ

© Wärtsilä Finland Oy Energy Business

DRAWING NUMBER					REVISION
DBAF507546					-
DATE	14-Apr-2020	DATE	27-Apr-2020	DATE	27-Apr-2020
DRAWN	MPAX08	CHECKED	NCHX03	APPROVED	AKRX06

LARSEN & TOUBRO DRAWING NUMBER: O19045_008_M_V_12178_001 — REVISION 2
OUTOTEC DRAWING NUMBER: 900707_GAU01_WG01_MTL01_45073 — DOCUMENT ID: OU100686674 — REVISION 2

This drawing is the property of LARSEN & TOUBRO and must not be passed on to any person or body not authorized by us to receive it nor be copied or otherwise made use either in full or in part by such person or body without our prior permission in writing.

The content of these documents are the sole property of Outotec Oyj. Any rights not expressly granted herein are reserved. Reproduction, transfer or distribution of part or all of the contents in any form without prior written permission of Outotec is prohibited.

This document and the information contained herein is Ma'aden proprietary know-how. This document or any part thereof should not be reproduced, stored in a retrieval system or transmitted by any means, electronic or otherwise, or divulged without prior written permission of Ma'aden.

DRAWN	--	--
CHECKED	SJK	18/05/2020
ENGINEER	--	--
APPROVED	NBR	20/05/2020
EMPLOYER		
SCALE	1:50	A1

MANSOURAH - MASSARAH GOLD PROJECT
GENERAL ARRANGEMENT DRAWING
POWER GENERATION
WORKSHOP & WAREHOUSE-FOUNDATION

DRAWING NUMBER: MD-216-49PR-EG-CV-GAD-V553-1057 — REV D01