

DRAWING NUMBER MD-216-49PR-EG-CV-LAD-V553-1010 REV D01

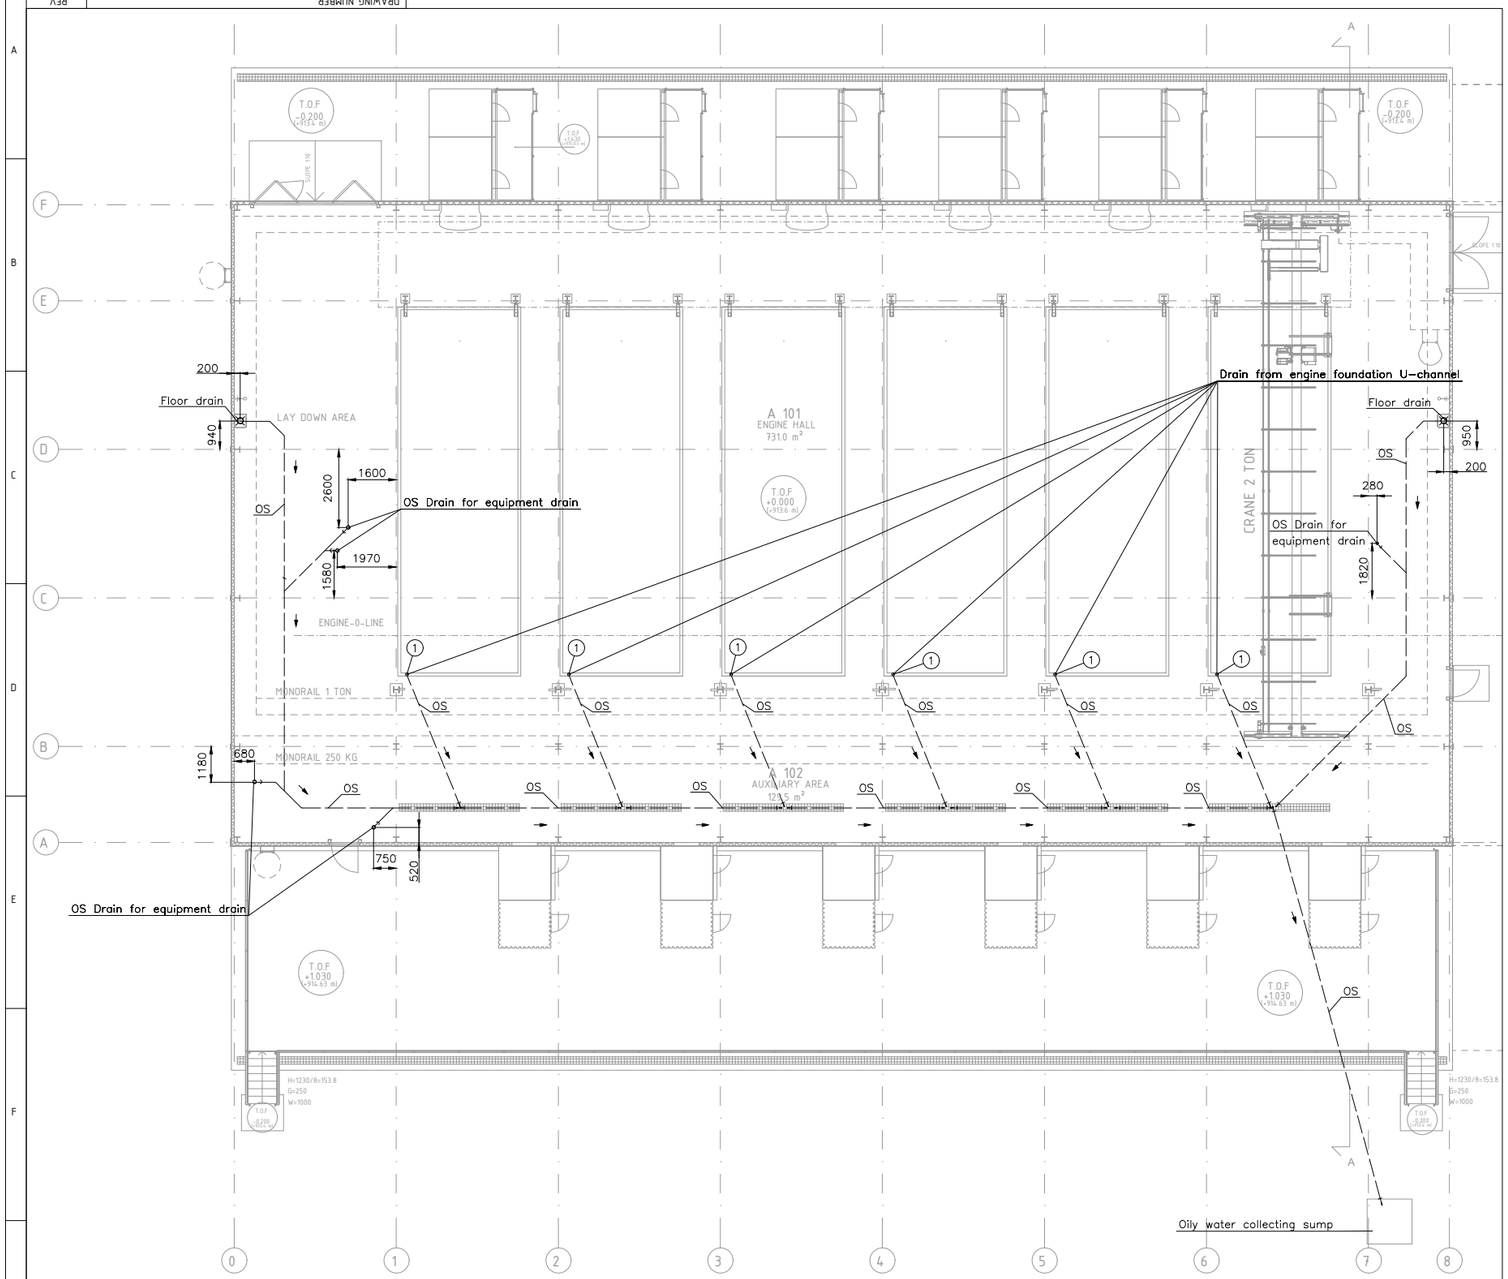


Side view

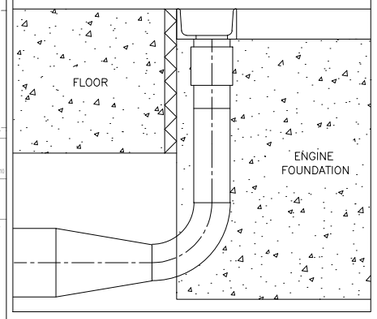


Detail A

| Name | Description |
|---|---|
| OS | Oily water drainage pipe |
| — — — — — | Pipe under floor level |

Oily water drainage to be adjusted according to site conditions.

(1) Drain from engine foundation U-channel See detail A

| REV | DATE | DESCRIPTION | DRN | CHK | ENG | APP | EMP |
|---|---|---|---|---|---|---|---|
| D01 | 02/11/2023 | D01 | NAEW | SJK | -- | NBR | |
| C01 | 17/07/2020 | ISSUED FOR CONSTRUCTION | -- | SJK | -- | NBR | |
| A02 | 20/06/2020 | REVISED BASED ON EMPLOYER COMMENTS DATED 10/06/2020 | -- | SJK | -- | NBR | |
| A01 | 20/05/2020 | ISSUED FOR REFERENCE | -- | SJK | -- | NBR | |

DOCUMENT NUMBER | REFERENCE DOCUMENTS

WÄRTSILÄ

© Wärtsilä Finland Oy
Energy Business

LARSEN & TOUBRO

This drawing is the property of LARSEN & TOUBRO and must not be passed on to any person or body not authorized by us to receive it nor be copied or otherwise made use either in full or in part by such person or body without our prior permission in writing.

Outotec

The content of these documents are the sole property of Outotec Oy. Any rights not expressly granted herein are reserved. Reproduction, transfer or distribution of part or all of the contents in any form without prior written permission of Outotec is prohibited.

MA'ADEN معادن
Saudi Arabian Mining Company شركة معادن السعودية للتعدين

This document and the information contained herein is Ma'aden proprietary know-how. This document or any part thereof should not be reproduced, stored in a retrieval system or transmitted by any means, electronic or otherwise, or divulged without prior written permission of Ma'aden.

| | | |
|---|---|---|
| DRAWING NUMBER | DBAF508429 | REVISION - |
| DATE / DRAWN | 29-Apr-2020 / rkax31 | DATE / CHECKED 29-Apr-2020 / sojx01 |
| DATE / APPROVED | 30-Apr-2020 / akrx06 | |

| | | |
|---|---|---|
| LARSEN & TOUBRO DRAWING NUMBER | 019045_008_M_V_12028_007 | REVISION 3 |
| OUTOTEC DRAWING NUMBER | 900707_GAU01_WG01_EQS03_45003 | DOCUMENT ID OU100686679 / REVISION 3 |

| | | |
|---|---|---|
| DRAWN | -- | -- |
| CHECKED | SJK | 18/05/2020 |
| ENGINEER | -- | -- |
| APPROVED | NBR | 20/05/2020 |
| EMPLOYER | | |
| SCALE | 1:100 | A1 |

MANSOURAH - MASSARAH GOLD PROJECT
LAYOUT
POWER GENERATION
ENGINE HALL-OILY WATER DRAINAGE

DRAWING NUMBER MD-216-49PR-EG-CV-LAD-V553-1010 REV D01