

DRAWING NUMBER: MD-216-3650-EG-CV-GAD-1002
REV: A02


A - A
1:50

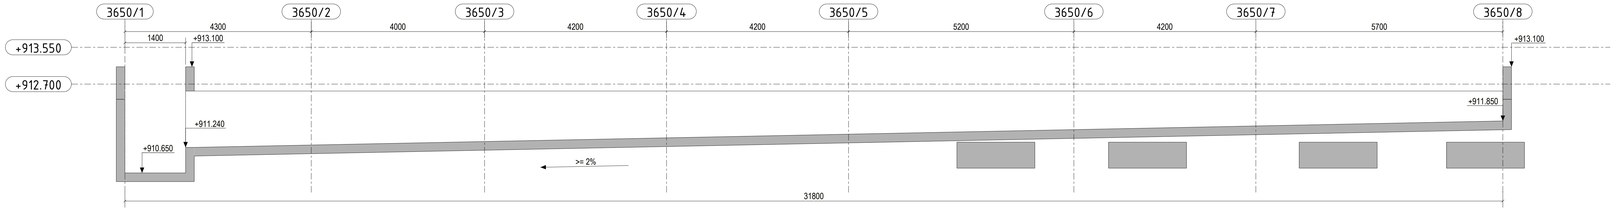

B - B
1:50

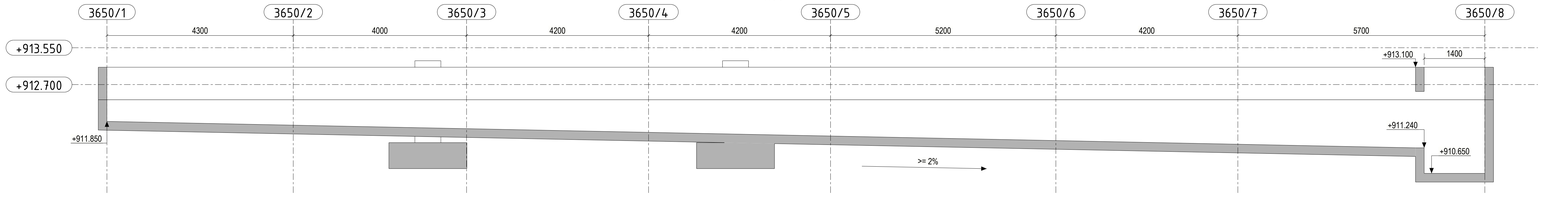

C - C
1:50

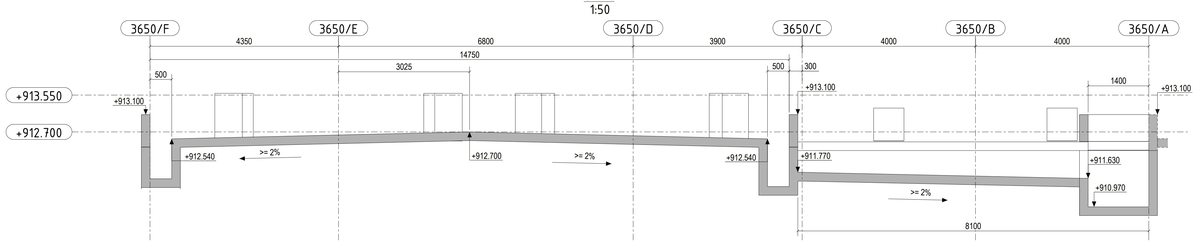

Document Number
MD-216-3650-EG-CV-QAD-1002

Revision A02

Approved

Mr Doron Golan - Bechtel Global

Jun 28, 2021, 5:34 PM GMT-4:00

Permission to proceed does not constitute acceptance or approval of design detail, calculations, analysis, test methods, or materials developed or selected by the Supplier, and does not relieve the Supplier from full compliance with contractual obligations


THIS DESIGN IS NOT ISSUED FOR CONSTRUCTION

FINISHED TOP GROUND LEVEL (F.G.L) FOR PROCESS AREA 3650 = RL(+)912.700 m

CHECKERED PLATE
GRATING
GRATING - FRP

1. ALL DIMENSIONS ARE IN MILLIMETER, ELEVATIONS ARE IN METER UNLESS OTHERWISE STATED
2. CO-ORDINATES ARE SHOWN IN GENERAL ARRENGEMENT DRAWINGS
3. GRATING TYPE (FRP OR NORMAL) IS SPECIFIED IN GENERAL ARRENGEMENT DRAWINGS
4. F.F.L, F.G.L, T.O.C = FINISHED FLOOR LEVEL, FINISHED GROUND LEVEL, TOP OF CONCRETE, T.O.S, B.O.S, B.O.B, = TOP OF STEEL, BOTTOM OF STEEL, BOTTOM OF BASE PLATE
5. BUILDING DIMENSIONS AND HEIGHTS ARE TENTATIVE, SHALL BE FINALIZED DURING DETAIL ENGINEERING SUBJECT TO MINIMUM AS SHOWN.
6. ALL MAINTENANCE FACILITIES, HANDLING PROVISIONS, ACCESS WAYS, PLATFORMS FOR MAINTENANCE SHALL BE PROVIDED DURING DETAIL ENGINEERING WHICH ARE NOT SHOWN ENTIRELY. THIS DRAWING IS TO BE CONSIDERED AS CONCEPTUAL ARRANGEMENT OF THE FACILITIES.

KEYPLAN

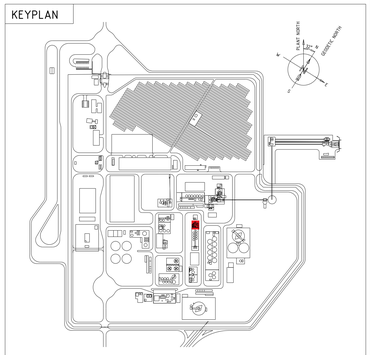

DOCUMENT NUMBER	REFERENCE DOCUMENTS
MD-216-1000-EG-ST-CRT-1001	CIVIL, STRUCTURAL AND ARCHITECTUAL DESIGN CRITERIA
MD-216-3650-EG-ME-GAD-1008-RA01	SECTION C-C
MD-216-3650-EG-ME-GAD-1006	SECTION A-A
MD-216-3650-EG-ME-GAD-1004	PLAN AT EL. +918.700 & EL. +921.300
MD-216-3650-EG-ME-GAD-1002	PLAN AT EL. +912.700
MD-216-3650-EG-ST-GAD-1001	PLAN AT EL. +912.700 GRID A-F/6-8
MD-216-3650-EG-CV-GAD-1001	PLAN AT EL. +912.700

DOCUMENT NUMBER	REFERENCE DOCUMENTS
MD-216-3650-EG-ME-GAD-1009	SECTION D-D
MD-216-3650-EG-ME-GAD-1007	SECTION B-B
MD-216-3650-EG-ME-GAD-1005	PLPLAN AT EL. +925.200 & EL. +927.400
MD-216-3650-EG-ME-GAD-1003	PLAN AT EL. +915.400
MD-216-3650-EG-ST-GAD-1002	PLAN AT EL. +912.700 GRID A-F/1-5
MD-216-3650-EG-CV-GAD-1002	PLAN AT EL. +912.700 - SECTIONS

REV	DATE	REVISION DESCRIPTION	DRN	CHK	ENG	APP	EMP
A02	01.06.2021	ISSUED FOR DETAIL DESIGN	ElKiv	MkLai	LuPiz	SouCha	
A01	15.04.2020	ISSUED FOR APPROVAL	ElKiv	MkLai	LuPiz	SouCha	

REV	DATE	REVISION DESCRIPTION	DRN	CHK	ENG	APP	EMP

RESERVED FOR VENDOR LOGO AND DRAWING NUMBER

LARSEN & TOUBRO DRAWING NUMBER: 019045-450-C-G-24971-002 — REVISION: 1

OUTOTEC DRAWING NUMBER: 900707_GAU01_EE12_CTA04_36502 — DOCUMENT ID: OU100674880 — REVISION: 1

LARSEN & TOUBRO

This drawing is the property of LARSEN & TOUBRO and must not be passed on to any person or body not authorized by us to receive it nor be copied or otherwise made use either in full or in part by such person or body without our prior permission in writing.

Outotec

The content of these documents are the sole property of Outotec Oyj. Any rights not expressly granted herein are reserved. Reproduction, transfer or distribution of part or all of the contents in any form without prior written permission of Outotec is prohibited.

MA'ADEN معادن
Saudi Arabian Mining Company شركة معادن العربية السعودية

This document and the information contained herein is Ma'aden proprietary know-how. This document or any part thereof should not be reproduced, stored in a retrieval system or transmitted by any means, electronic or otherwise, or divulged without prior written permission of Ma'aden.

DRAWN	ElKiv	15.04.2020
CHECKED	MkLai	15.04.2020
ENGINEER	LuPiz	15.04.2020
APPROVED	SouCha	15.04.2020
EMPLOYER		
SCALE	1:50	A0

MANSOURAH - MASSARAH GOLD PROJECT
CIVIL WORKS GUIDE DRAWING
3650 POX ACID WASH - ELUTION AND CARBON GENERATION
PLAN AT EL. +912.700 - SECTIONS

DRAWING NUMBER: MD-216-3650-EG-CV-GAD-1002 — REV: A02

Tekla Structures