


DRAWING NUMBER
MD-216-1800-EG-CV-GAD-1544
REV
D01

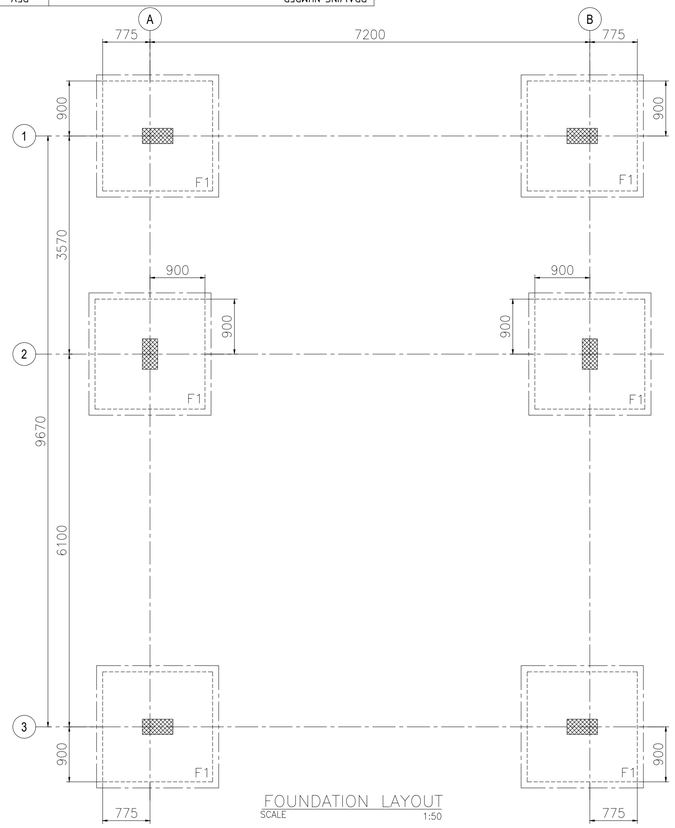

FOUNDATION LAYOUT
SCALE 1:50

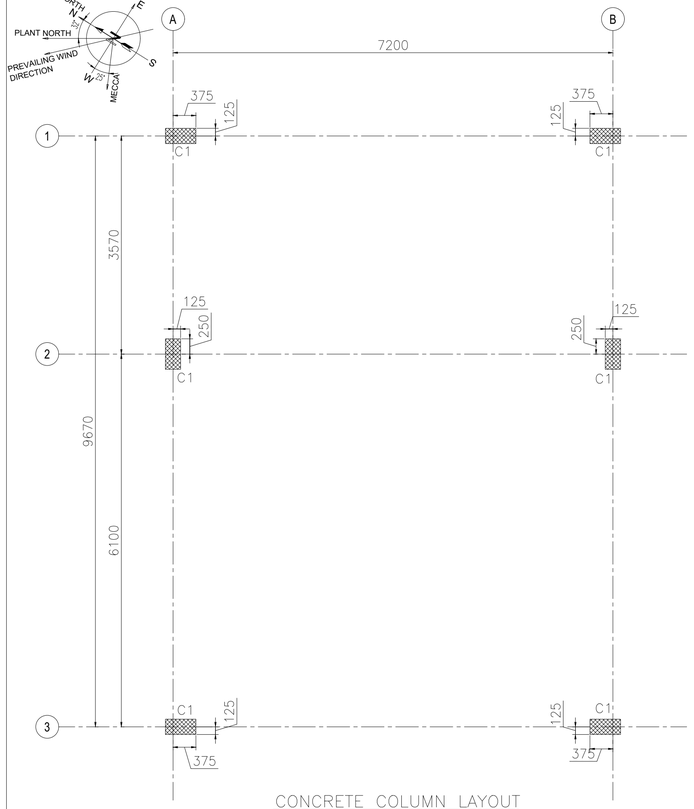


CONCRETE COLUMN LAYOUT
SCALE 1:50

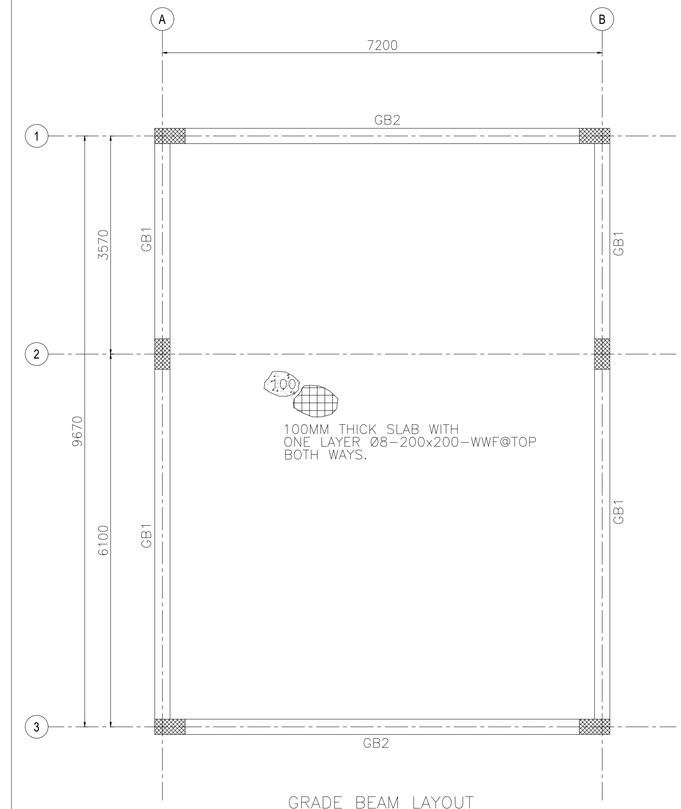


GRADE BEAM LAYOUT
SCALE 1:50

MASTER KEY PLAN

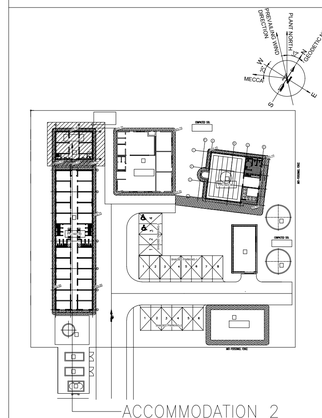

ACCOMMODATION 2

ACCOMMODATION 2
ENLARGED KEYPLAN

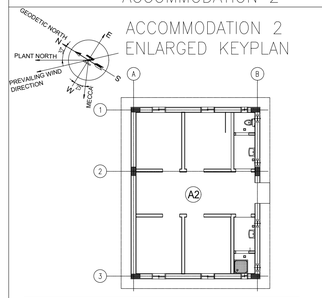

ACCOMMODATION 2			
BLDG. NO.	CORNER NO.	EASTING	NORTHING
A2	A1	E 262073.008	N 2508748.048
	B3	E 262068.622	N 2508736.818

NOTES

1.) ALL DIMENSIONS ARE GIVEN IN MILLIMETRES AND ELEVATIONS ARE IN METRES UNLESS OTHERWISE NOTED.
2.) MINIMUM REINFORCED CONCRETE GRADE TO BE USED FOR SUPERSTRUCTURE & SUBSTRUCTURES IS M35(5000 PSI).
3.) MINIMUM LEAN CONCRETE GRADE TO BE USED FOR THE SUB-STRUCTURES IS M15(2175 PSI).
4.) ALL REINFORCING STEEL SHALL BE DEFORMED BILLET STEEL BARS CONFORMING TO ASTM-A615, WITH MINIMUM YIELD STRENGTH OF FY420 MPA .
5.) THE NET SOIL BEARING CAPACITY CONSIDERED IN FOUNDATION DESIGN IS 350 KPA.(REFER DOC 216-3000-EG-CV-RPT-1008).
6.) WATER PROOFING INSULATION SHALL BE AS PER PROJECT SPECS AND ITS MATERIAL TO BE APPROVED BY ENGINEER ON SITE.
7.) THE MINIMUM CONCRETE COVER AS PER SBC-304-2018(TABLE 20.6.1.3.1) MEASURED FROM REBAR SHALL BE
a) CONCRETE CAST AGAINST & PERMANENTLY EXPOSED TO EARTH (INCLUDING FOUNDATIONS OVER SUB-SLAB) FORMED CONCRETE EXPOSED TO EARTH OR WEATHER.....50MM
b.) CONCRETE NOT EXPOSED TO WEATHER NOR IN CONTACT WITH GROUND
BEAMS, COLUMNS.....40MM
SLABS, WALLS, JOISTS.....20MM
c.) CONCRETE SLAB OVER 50MM SUB-SLAB.....20MM
8.) ALL DRAWINGS MUST BE READ IN CONJUNCTION WITH RELEVANT ARCHITECTURAL AND ENGINEERING DRAWINGS RELATED TO THE SAME SHEET AND ANY ITEM ON IT.
9.) F.F.L +0.00 MENTIONED IS EQUIVALENT TO RL 923.90 AS PER THE CIVIL DRAWING MD-216-1800-EG-CV-GAD-1565-OVERALL LAYOUT PLAN.

F-FOUNDATION
C-COLUMN
FFL-FINISH FLOOR LVL
FGL-FINISH GRADE LVL
TOS-TOP OF SCREED
WWF-WELDED WIRE FABRIC
HCS-HOLLOW CORE SLAB
GB-GRADE BEAM
IJ-ISOLATION JOINT
CJ-CONTROL JOINT
GA-GALVANIZED
S.O.G-SLAB ON GRADE
ARCH-ARCHITECTURAL
HOR.-HORIZONTAL
REINF.-REINFORCEMENT
LVL.-LEVEL
RL-REDUCED LEVEL


LEGEND/ABBREVIATIONS

SCHEDULE OF FOOTINGS


FOOTING MARK	PLAIN CONCRETE			REINFORCED CONCRETE			BOTTOM REINFORCEMENT		TOP REINFORCEMENT		Ha	REMARKS
	L	W	T	L	W	T	SHORT BARS	LONG BARS	SHORT BARS	LONG BARS		
F1	2000	2000	50	1800	1800	400	ø12@150	ø12@150	–	–	1200	

SCHEDULE OF GRADE BEAMS

BEAM MARK	DIMENSIONS		STEEL REINFORCEMENT				STIRRUPS
			BOTTOM		TOP		
	WIDTH	DEPTH	STRAIGHT	ADD.	STRAIGHT	ADD.	
GB1	250	500	3ø16	–	3ø20	–	PROVIDE ø10@150 @DISTANCE OF L/3 FROM THE SUPPORT IN END SPAN & ø10@200 IN THE MID SPAN
GB2	250	600	3ø20	–	3ø20	–	

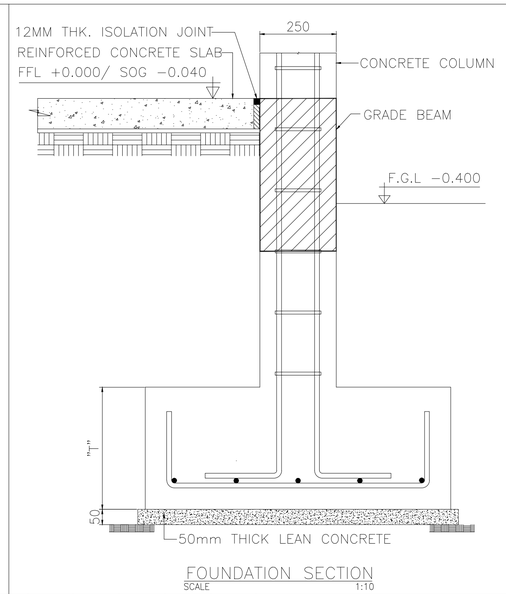


FOUNDATION SECTION
SCALE 1:10

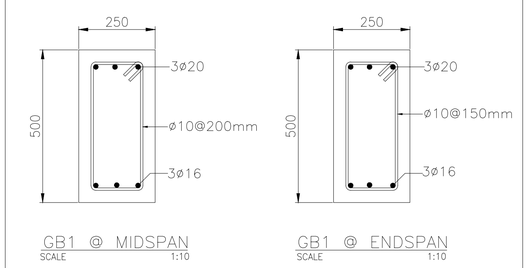


GB1 @ MIDSPAN
SCALE 1:10

GB1 @ ENDSPAN
SCALE 1:10

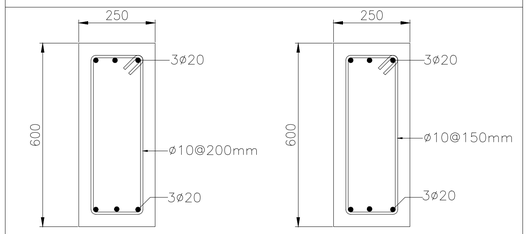

GB2 @ MIDSPAN
SCALE 1:10

GB2 @ ENDSPAN
SCALE 1:10

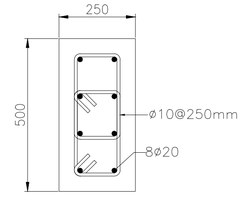

COLUMN DETAIL-C1
SCALE 1:10

MD-216-6000-EG-CV-STD-1002	HOLLOW CORE SLAB STANDARD									
MD-216-6000-EG-CV-STD-1001	REINFORCEMENT STANDARD	D01	05/03/2023	AS - BUILT	--	AVG	--	SJM		
MD-216-1800-EG-AR-GAD-3152	BUILDING PLANS	C01	23/04/2020	ISSUED FOR CONSTRUCTION	--	AVG	--	SJM		
MD-216-1800-EG-CV-GAD-1565	OVERALL LAYOUT PLAN	A01	23/03/2020	ISSUED FOR APPROVAL	--	AVG	--	SJM		
DOCUMENT NUMBER	REFERENCE DOCUMENTS	REV	DATE	REVISION DESCRIPTION	DRN	CHK	ENG	APP	EMP	

DESIGNER:
مكتب الخليج للاستشارات الهندسية
الخبر، المملكة العربية السعودية
GULF CONSULT
ARCHITECTS AND ENGINEERS

DRAWING NUMBER					REVISION
ACCO-2-ST-001					0
DATE	13/03/2020	DATE	14/03/2020	DATE	15/03/2020
DRAWN	MAH	CHECKED	MF	APPROVED	FK

LARSEN & TOUBRO DRAWING NUMBER	REVISION
019045_900_C_G_24245_001	2
OUTOTEC DRAWING NUMBER: 900707__GAU01__AN02__MTL01__18030	DOCUMENT ID: OU100668736 / REVISION: 2

LARSEN & TOUBRO

This drawing is the property of LARSEN & TOUBRO and must not be passed on to any person or body not authorized by us to receive it nor be copied or otherwise made use either in full or in part by such person or body without our prior permission in writing.

Outotec

The content of these documents are the sole property of Outotec Oyj. Any rights not expressly granted herein are reserved. Reproduction, transfer or distribution of part or all of the contents in any form without prior written permission of Outotec is prohibited.

MA'ADEN معادن
Saudi Arabian Mining Company شركة معادن العربية السعودية

This document and the information contained herein is Ma'aden proprietary know-how. This document or any part thereof should not be reproduced, stored in a retrieval system or transmitted by any means, electronic or otherwise, or divulged without prior written permission of Ma'aden.

DRAWN	--	--
CHECKED	AVG	22/03/2020
ENGINEER	--	--
APPROVED	SJM	23/03/2020
EMPLOYER		
SCALE	1:50	A1

MANSOURAH - MASSARAH GOLD PROJECT
GENERAL ARRANGEMENT
SECURITY BASE CAMP: ACCOMMODATION 2
LAYOUT & DETAILS OF FDN, COL & GRADE BEAM

DRAWING NUMBER: MD-216-1800-EG-CV-GAD-1544
REV: D01