

LEVEL +912.500
1:50

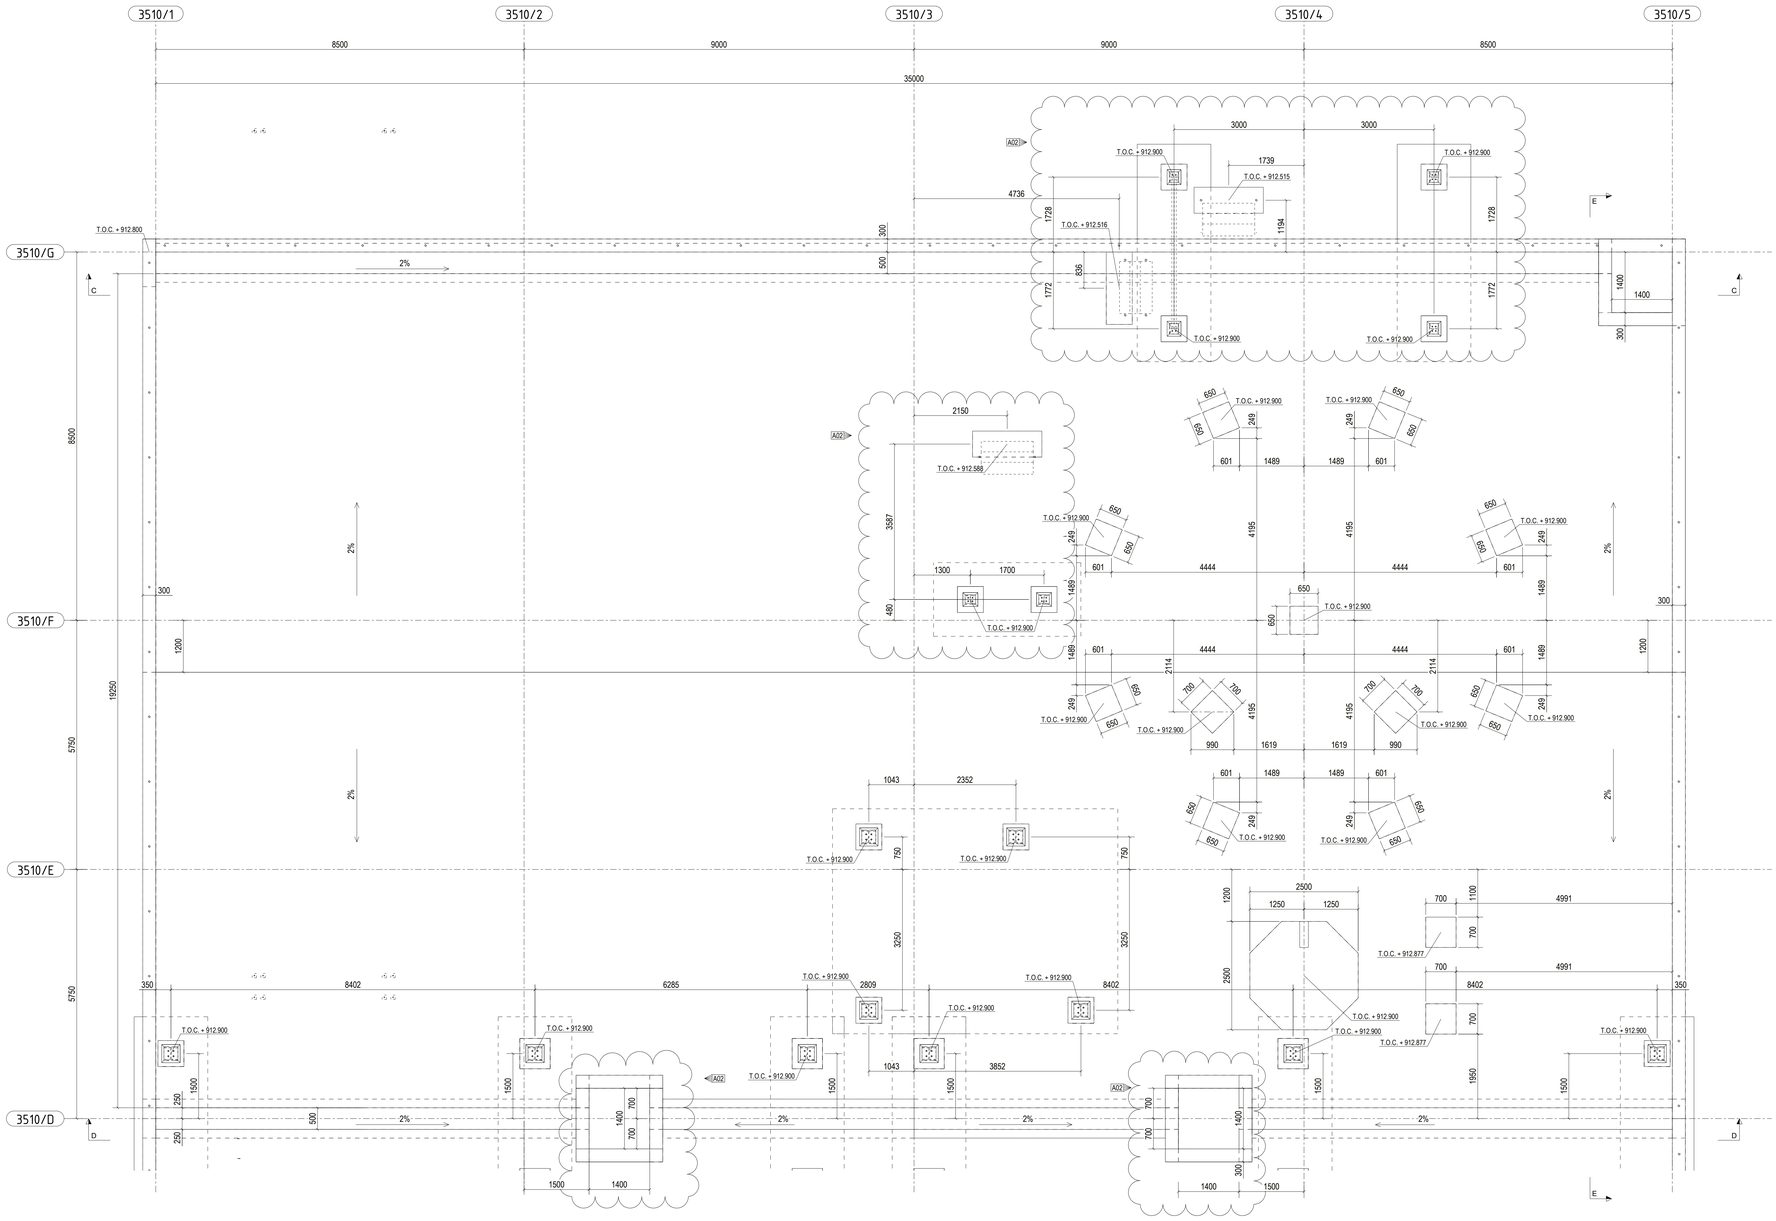

E – E
1:100

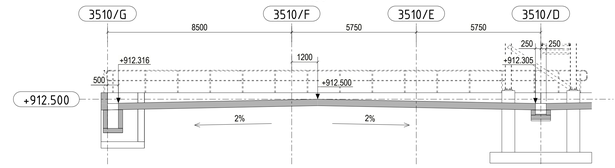


THIS DESIGN IS NOT ISSUED FOR CONSTRUCTION

FINISHED TOP GROUND LEVEL (F.G.L)
FOR PROCESS AREA 3510 = RL(+)912.500 m


CONCRETE ELEMENT FLOOR (PRE-CAST SLAB)
CONCRETE FLOOR
CONCRETE FLOOR WITH ACID RESISTANT COATING
CONCRETE WALL

1. ALL DIMENSIONS ARE IN MILLIMETER, ELEVATIONS ARE IN METER UNLESS OTHERWISE STATED
2. CO-ORDINATES ARE SHOWN IN GENERAL ARRENGEMENT DRAWINGS
3. GRATING TYPE (FRP OR NORMAL) IS SPECIFIED IN GENERAL ARRENGEMENT DRAWINGS
4. F.F.L, F.G.L, T.O.C = FINISHED FLOOR LEVEL, FINISHED GROUND LEVEL, TOP OF CONCRETE, T.O.S, B.O.S, B.O.B, = TOP OF STEEL, BOTTOM OF STEEL, BOTTOM OF BASE PLATE
5. BUILDING DIMENSIONS AND HEIGHTS ARE TENTATIVE, SHALL BE FINALIZED DURING DETAIL ENGINEERING SUBJECT TO MINIMUM AS SHOWN.
6. ALL MAINTENANCE FACILITIES, HANDLING PROVISIONS, ACCESS WAYS, PLATFORMS FOR MAINTENANCE SHALL BE PROVIDED DURING DETAIL ENGINEERING WHICH ARE NOT SHOWN ENTIRELY, THIS DRAWING IS TO BE CONSIDERED AS CONCEPTUAL ARRANGEMENT OF THE FACILITIES.


KEYPLAN

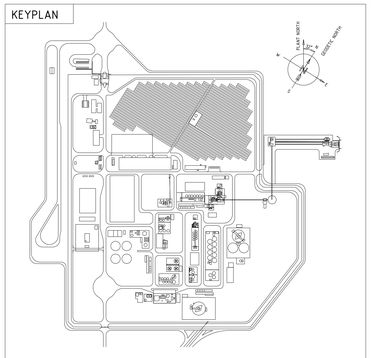

C – C
1:100

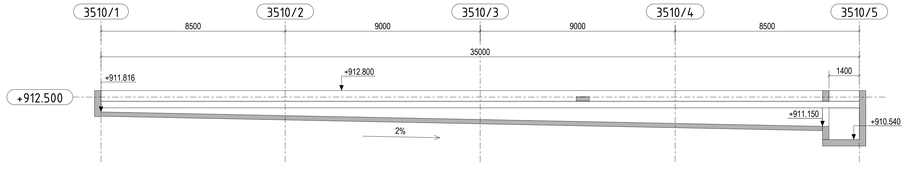

D – D
1:100

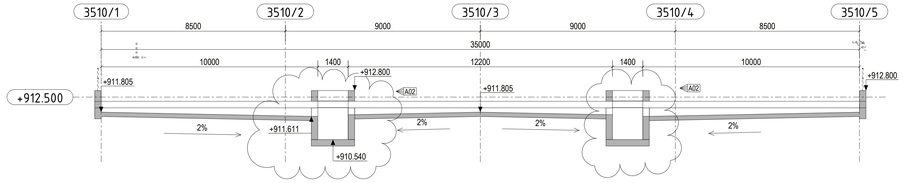

DOCUMENT NUMBER	REFERENCE DOCUMENTS	DOCUMENT NUMBER	REFERENCE DOCUMENTS
MD-216-3510-EG-ST-GAD-1001	PLAN AT EL. +912.500	MD-216-3510-EG-ST-GAD-1002	3D VIEW AT EL. +912.500
MD-216-3510-EG-ME-GAD-1019	SECTION B-B	MD-216-3510-EG-CV-GAD-1001	PLAN AT EL. +912.500 – GRID A-D/1-5
MD-216-3510-EG-ME-GAD-1017	PLAN VIEW	MD-216-3510-EG-ME-GAD-1018	SECTION A-A
MD-216-1000-EG-ST-CRT-0001	CIVIL, STRUCTURAL AND ARCHITECTURAL DESIGN BASIS	MD-216-3510-EG-ME-GAD-1016	PLAN AT EL. +912.500

REV	DATE	REVISION DESCRIPTION	DRN	CHK	ENG	APP	EMP
A02	30.03.2020	ISSUED FOR DETAIL DESIGN, STAIRCASES MOVED, CHANNELS UPDATED	NikJan	MikLai	LuiPiz	SouCha	
A01	11.12.2019	ISSUED FOR APPROVAL	NikJan	MikLai	LuiPiz	SouCha	

RESERVED FOR VENDOR LOGO AND DRAWING NUMBER

LARSEN & TOUBRO
This drawing is the property of LARSEN & TOUBRO and must not be passed on to any person or body not authorised by us to receive it nor be copied or otherwise made use either in full or in part by such person or body without our prior permission in writing.

Outotec
The content of these documents are the sole property of Outotec Oyj. Any rights not expressly granted herein are reserved. Reproduction, transfer or distribution of part or all of the contents in any form without prior written permission of Outotec is prohibited.

MA'ADEN معادن
Saudi Arabian Mining Company شركة معادن السعودية
This document and the information contained herein is Ma'aden proprietary know-how. This document or any part thereof should not be reproduced, stored in a retrieval system or transmitted by any means, electronic or otherwise, or divulged without prior written permission of Ma'aden.

LARSEN & TOUBRO DRAWING NUMBER	019045_450_C_G_24939_001		REVISION 1
OUTOTEC DRAWING NUMBER	900707_GAU01_ST61_CTA04_35102	DOCUMENT ID OU100667796	REVISION 1
DRAWN	NikJan	11.12.1970	
CHECKED	MikLai	11.12.2019	
ENGINEER	LuiPiz	11.12.2019	
APPROVED	SouCha	11.12.2019	
EMPLOYER			
SCALE	1:50	A0	

MANSOURAH – MASSARAH GOLD PROJECT
CIVIL WORKS GUIDE DRAWING
CCD CIRCUIT
PLAN AT EL. +912.500 – GRID D-G/1-5

DRAWING NUMBER MD-216-3510-EG-CV-GAD-1002 REV A02

Tekla Structures