MD-216-3640-EG-CV-GAD-1001
DRAWING NUMBER
A02
REV

LEVEL +912.200
1:100

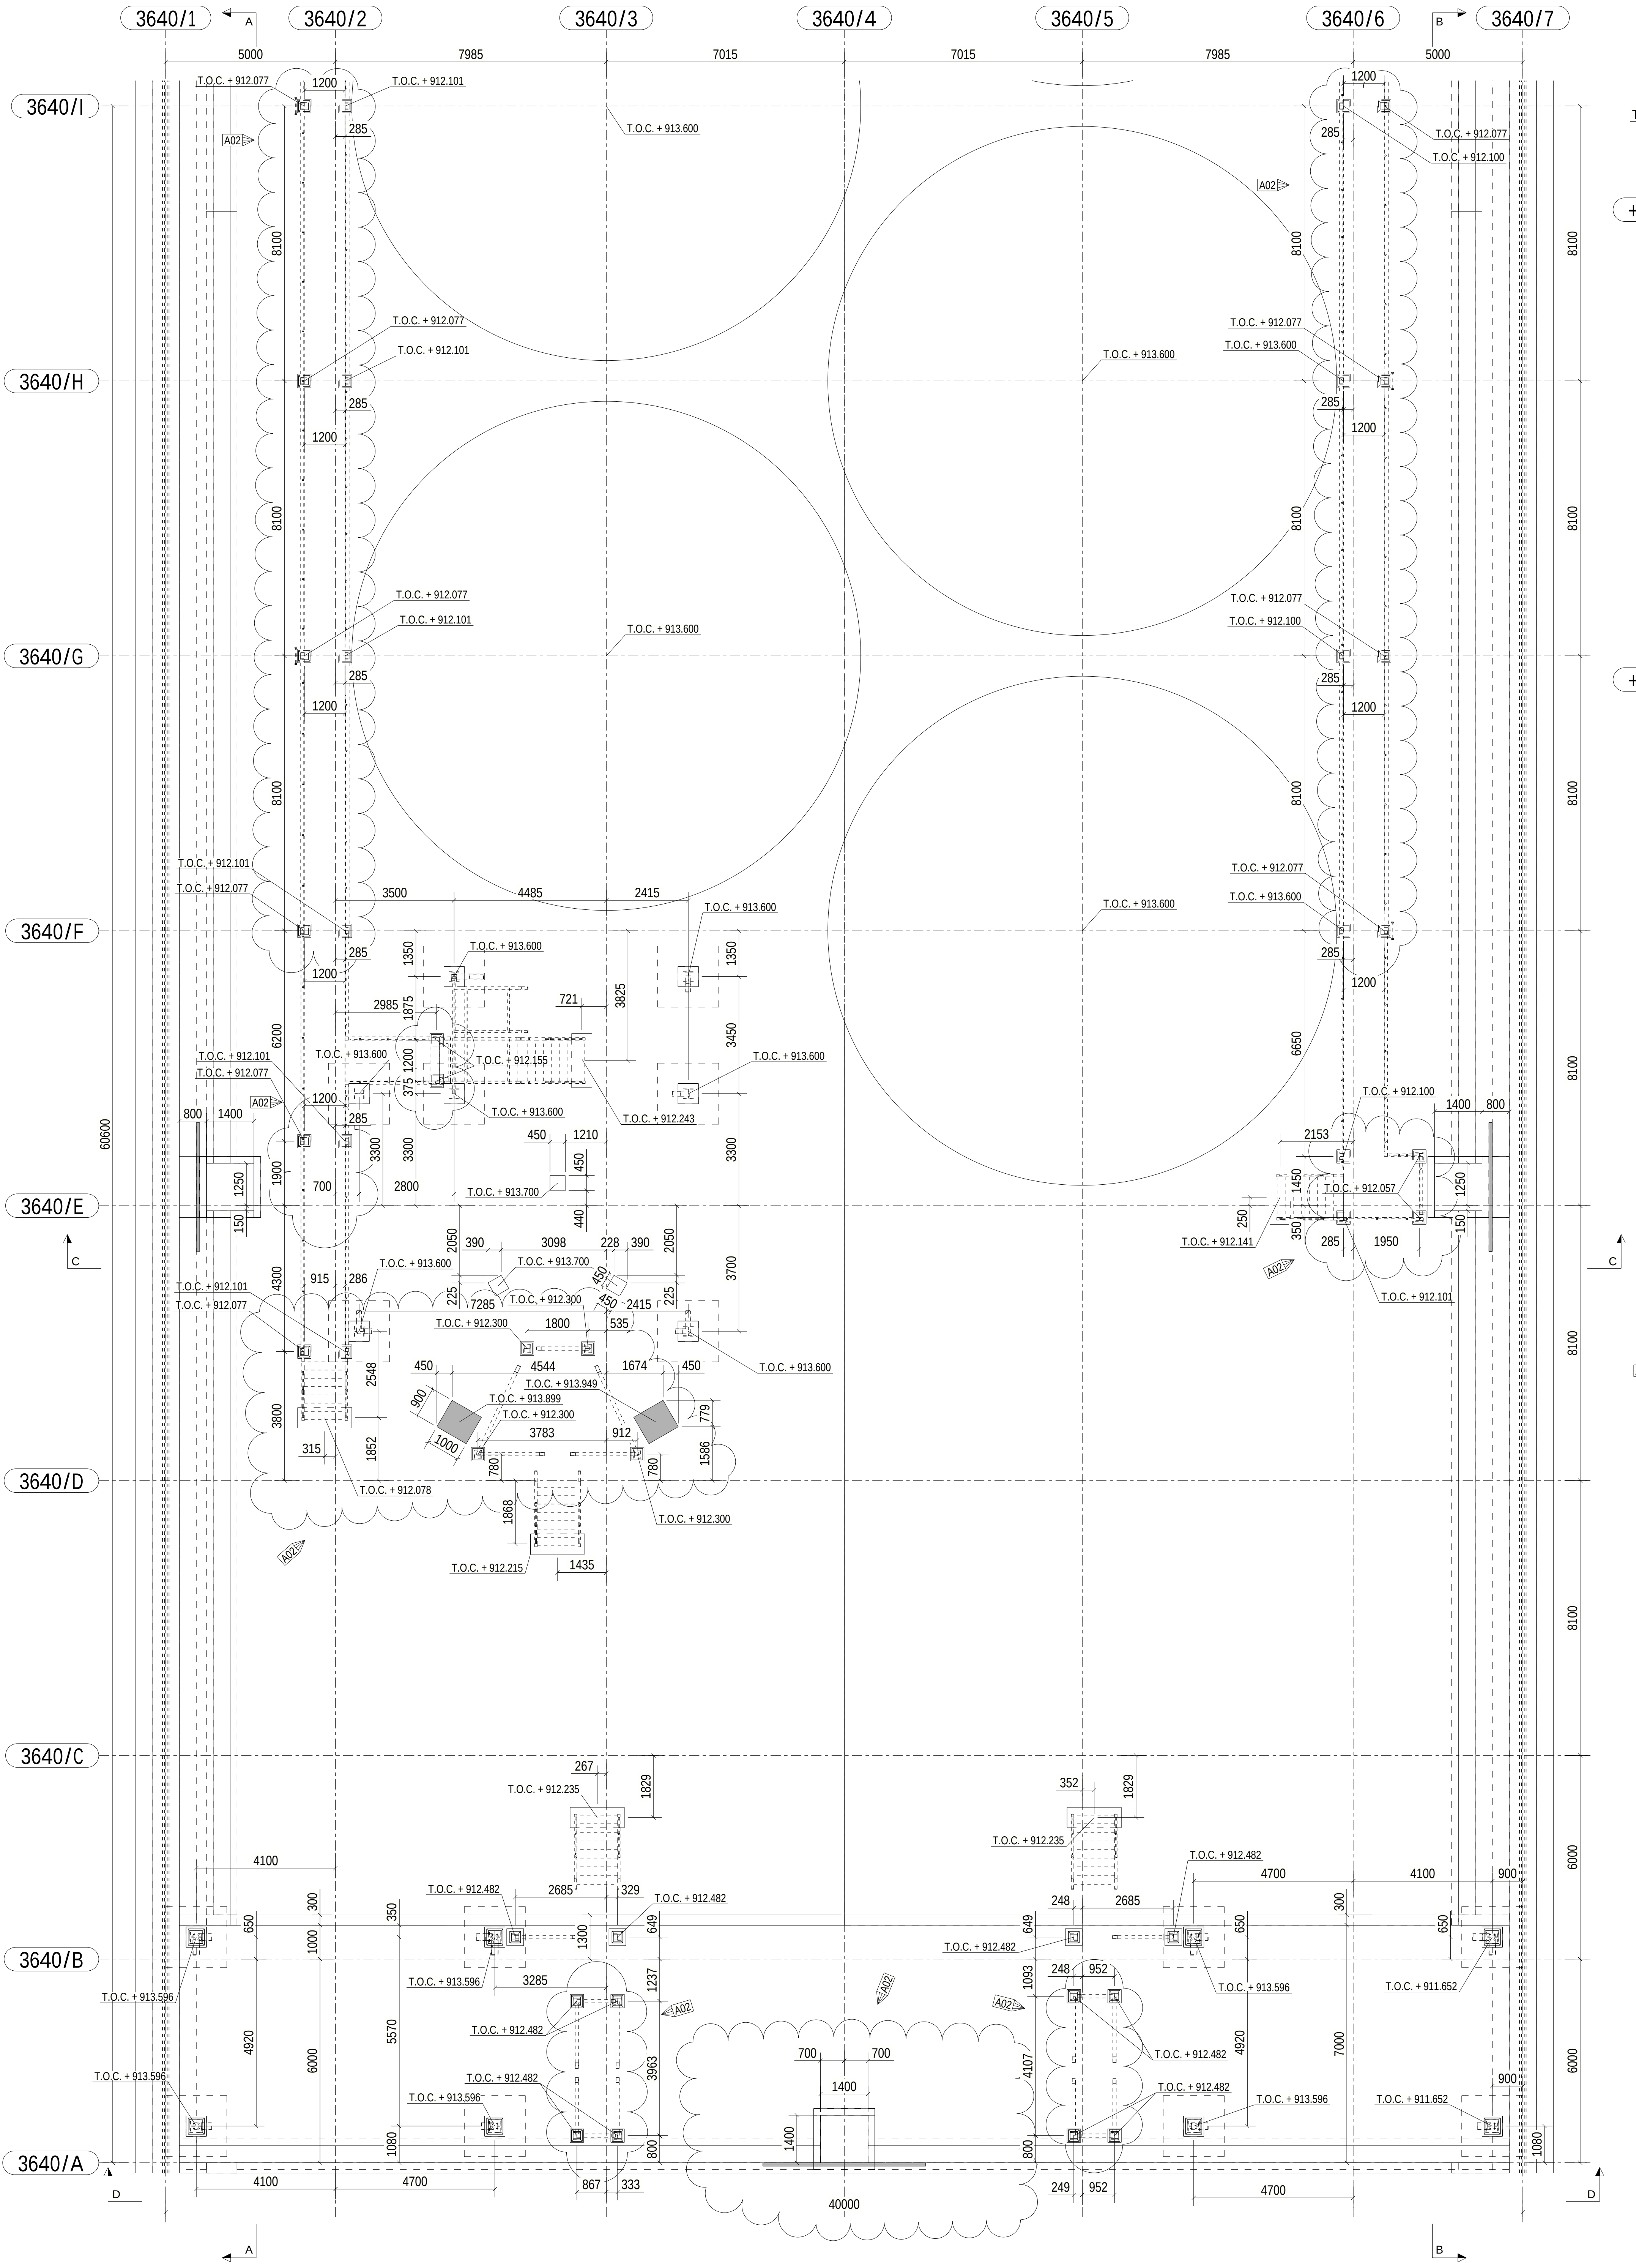

A - A
1:100

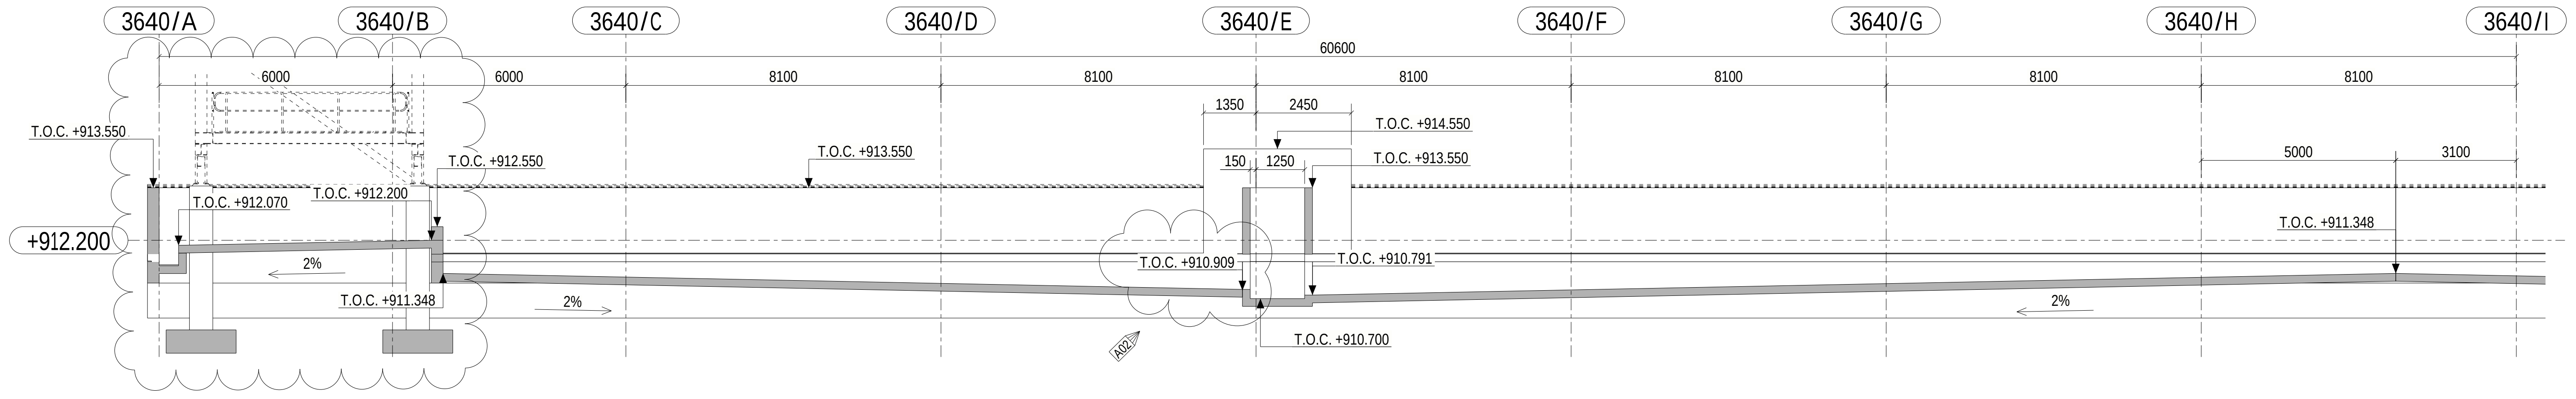

B - B
1:100

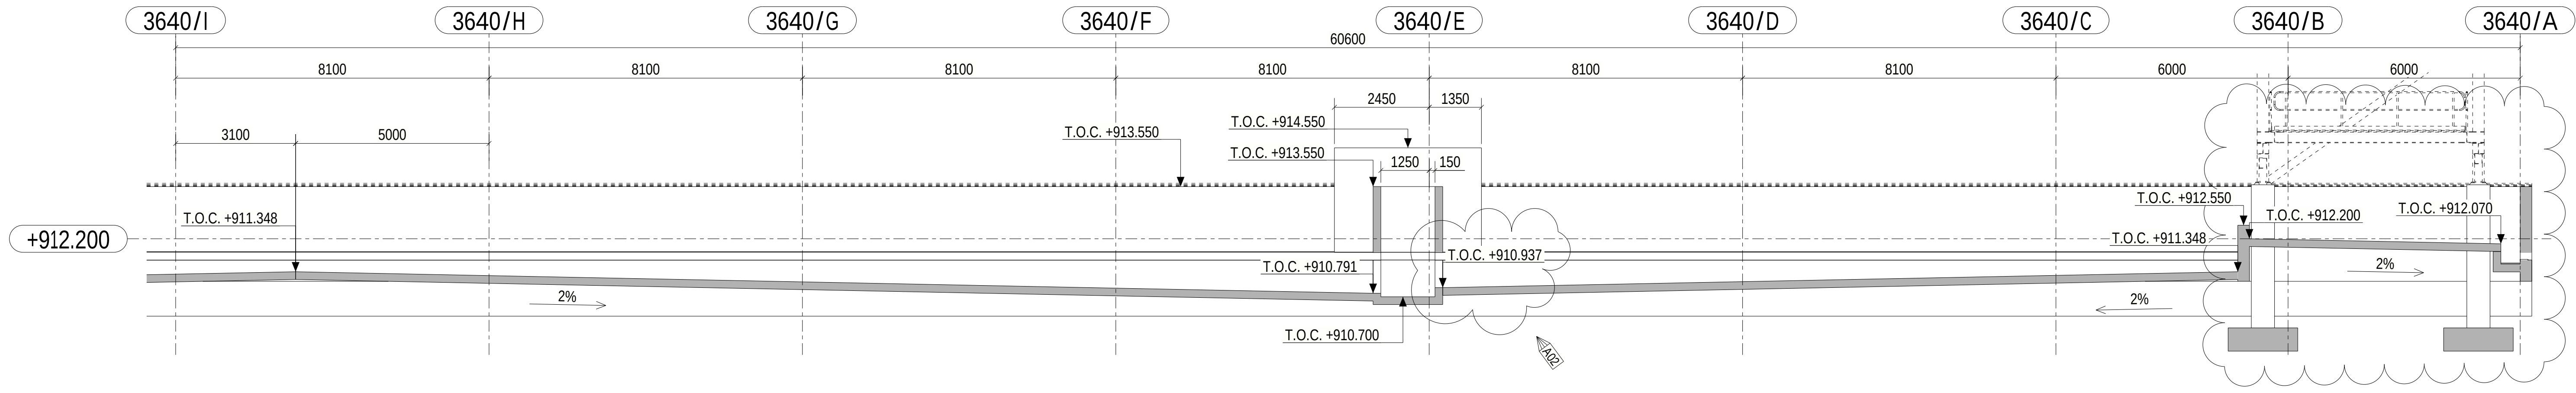

C - C
1:100

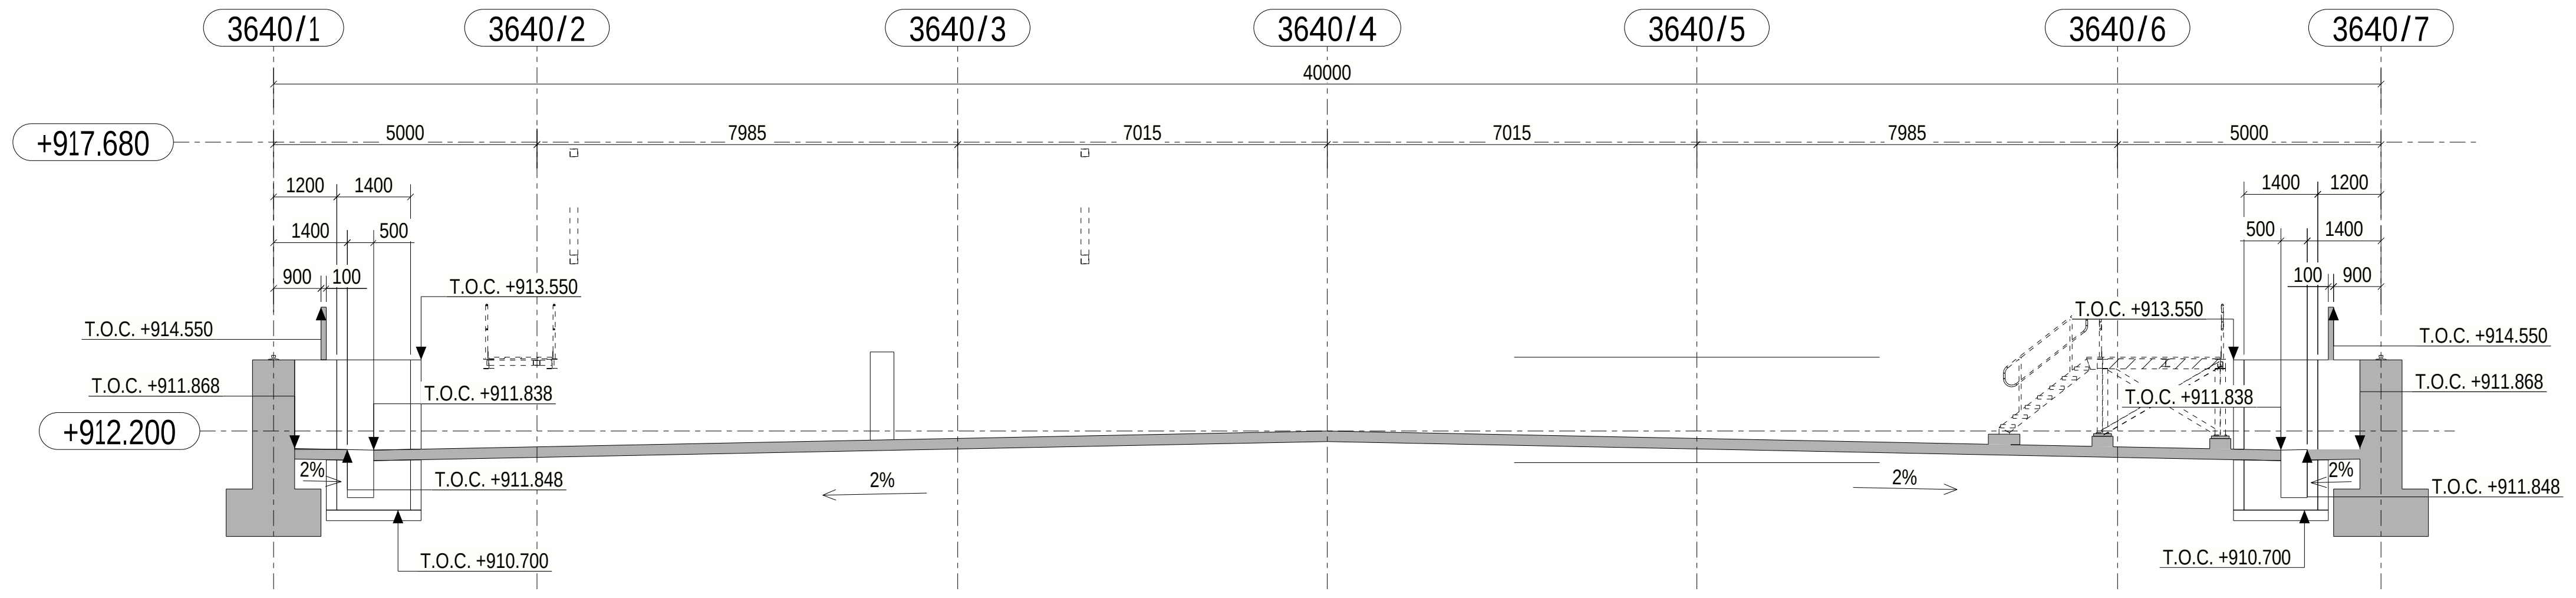

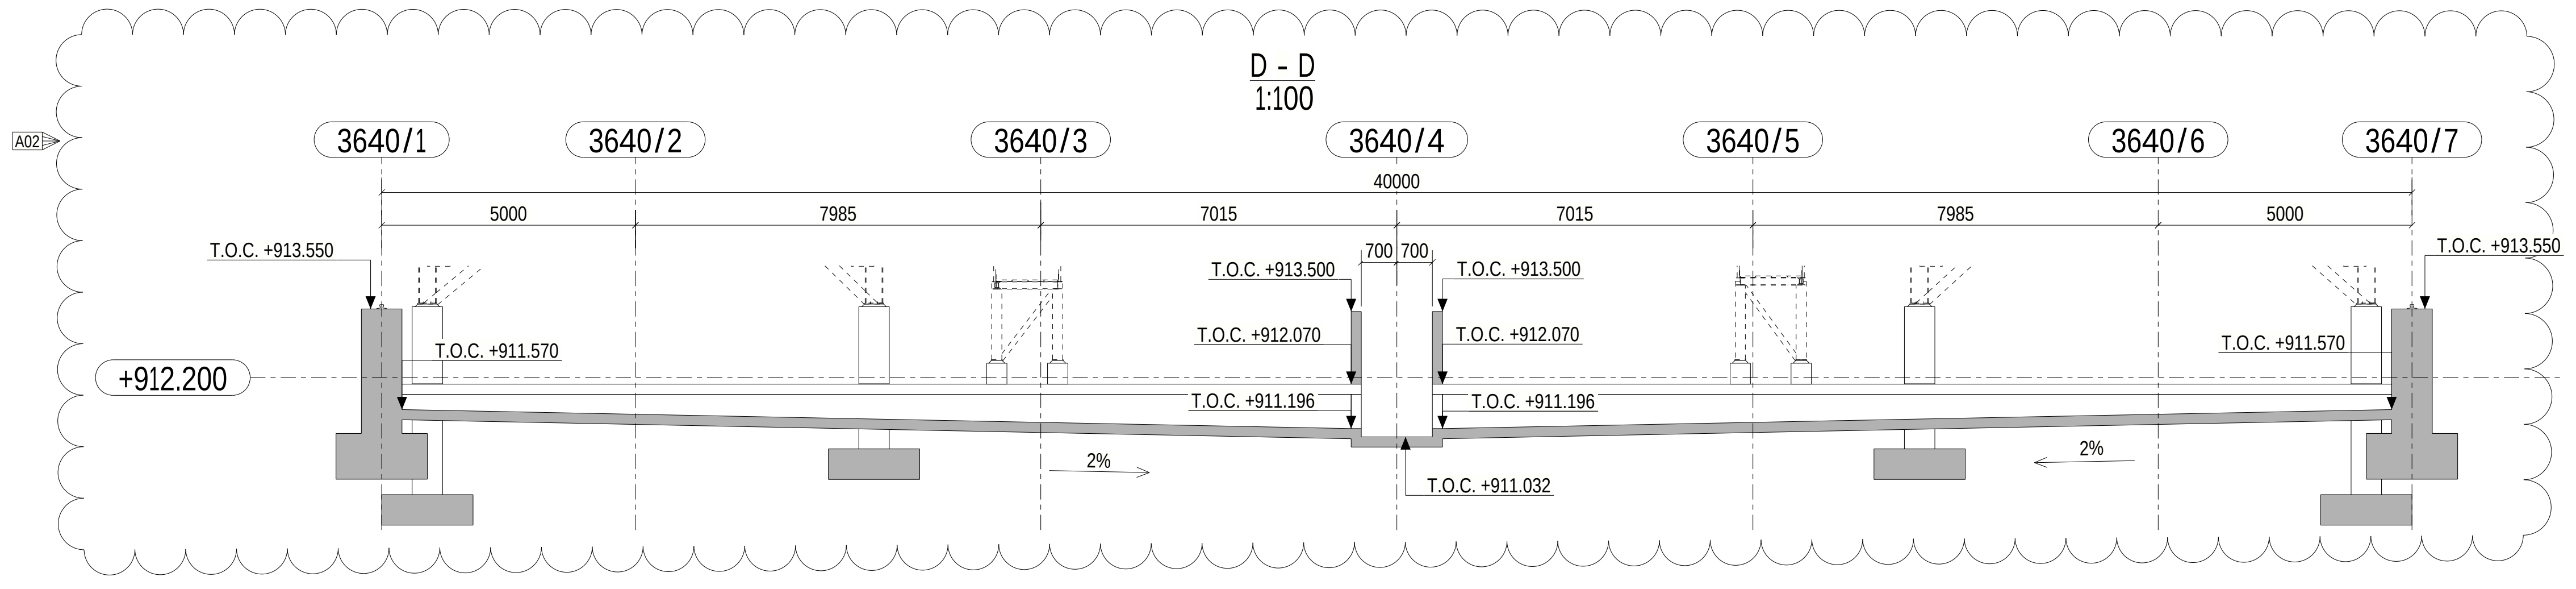

D - D
1:100

THIS DESIGN IS NOT ISSUED FOR CONSTRUCTION

FINISHED TOP GROUND LEVEL (F.G.L) FOR PROCESS AREA 3640 = RL(+)912.200 m

▥	CONCRETE ELEMENT FLOOR (PRE-CAST SLAB)
▨	CONCRETE FLOOR
▨ A	CONCRETE FLOOR WITH ACID RESISTANT COATING
▒	CONCRETE WALL

1. ALL DIMENSIONS ARE IN MILLIMETER, ELEVATIONS ARE IN METER UNLESS OTHERWISE STATED
2. CO-ORDINATES ARE SHOWN IN GENERAL ARRENGEMENT DRAWINGS
3. GRATING TYPE (FRP OR NORMAL) IS SPECIFIED IN GENERAL ARRENGEMENT DRAWINGS
4. F.F.L, F.G.L, T.O.C = FINISHED FLOOR LEVEL, FINISHED GROUND LEVEL, TOP OF CONCRETE, T.O.S, B.O.S, B.O.B, = TOP OF STEEL, BOTTOM OF STEEL, BOTTOM OF BASE PLATE
5. BUILDING DIMENSIONS AND HEIGHTS ARE TENTATIVE, SHALL BE FINALIZED DURING DETAIL ENGINEERING SUBJECT TO MINIMUM AS SHOWN.
6. ALL MAINTENANCE FACILITIES, HANDLING PROVISIONS, ACCESS WAYS, PLATFORMS FOR MAINTENANCE SHALL BE PROVIDED DURING DETAIL ENGINEERING WHICH ARE NOT SHOWN ENTIRELY. THIS DRAWING IS TO BE CONSIDERED AS CONCEPTUAL ARRANGEMENT OF THE FACILITIES.

KEYPLAN

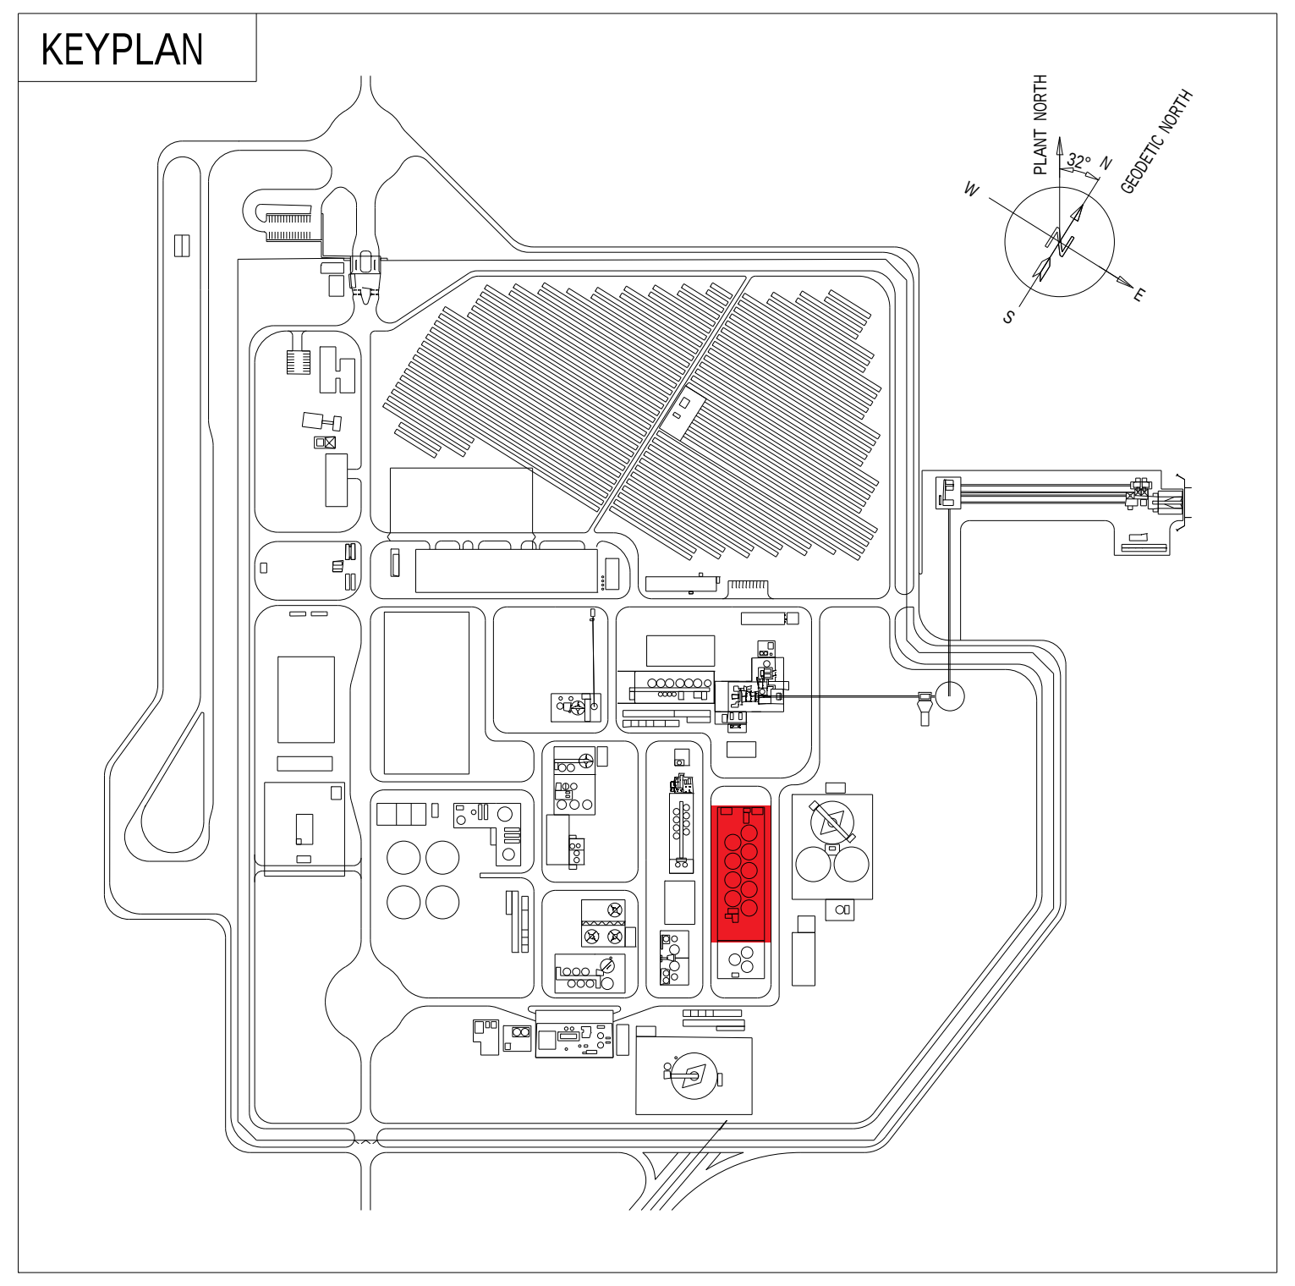

DOCUMENT NUMBER	REFERENCE DOCUMENTS	DOCUMENT NUMBER	REFERENCE DOCUMENTS
MD-216-3640-EG-ST-GAD-1003	PLAN AT EL. +912.200...+914.070 - GRID I-P/1-7	MD-216-3640-EG-ST-GAD-1004	3D-VIEW AT EL. +912.000
MD-216-3640-EG-ST-GAD-1001	PLAN AT EL. +922.700...+938.350	MD-216-3640-EG-ST-GAD-1002	PLAN AT EL. +912.200...+917.680 - GRID A-I/1-7
MD-216-3640-EG-ME-GAD-1036	SECTION D-D	MD-216-3640-EG-CV-GAD-1002	PLAN AT EL. +912.200 GRID I-P/1-7
MD-216-3640-EG-ME-GAD-1034	SECTION B-B	MD-216-3640-EG-ME-GAD-1035	SECTION C-C
MD-216-3640-EG-ME-GAD-1032	PLAN VIEW	MD-216-3640-EG-ME-GAD-1033	SECTION A-A
MD-216-1000-EG-ST-CRT-1001	CIVIL, STRUCTURAL AND ARCHITECTURAL DESIGN BASIS	MD-216-3640-EG-ME-GAD-1031	PLAN AT EL. +912.200

REV	DATE	REVISION DESCRIPTION	DRN	CHK	ENG	APP	EMP
A02	20.04.2020	ISSUED FOR DETAIL DESIGN, FOUNDATIONS, WELL AND INCLINATION UPDATED	SebMuu	MikLai	LuiPiz	SouCha	
A01	18.02.2020	ISSUED FOR APPROVAL	ElIKiv	MikLai	LuiPiz	SouCha	

RESERVED FOR VENDOR LOGO AND DRAWING NUMBER

LARSEN & TOUBRO

This drawing is the property of LARSEN & TOUBRO and must not be passed on to any person or body not authorized by us to receive it nor be copied or otherwise made use either in full or in part by such person or body without our prior permission in writing.

Outotec

The content of these documents are the sole property of Outotec Oyj. Any rights not expressly granted herein are reserved. Reproduction, transfer or distribution of part or all of the contents in any form without prior written permission of Outotec is prohibited.

MA'ADEN معادن
Saudi Arabian Mining Company شركة التعدين العربية السعودية

This document and the information contained herein is Ma'aden proprietary know-how. This document or any part thereof should not be reproduced, stored in a retrieval system or transmitted by any means, electronic or otherwise, or divulged without prior written permission of Ma'aden.

LARSEN & TOUBRO DRAWING NUMBER
REVISION 1

OUTOTEC DRAWING NUMBER 900707_GAU01_HL13_CTA04_36402
DOCUMENT ID OU100668207
REVISION 1

DRAWN	ElIKiv	18.02.2020
CHECKED	MikLai	18.02.2020
ENGINEER	LuiPiz	18.02.2020
APPROVED	SouCha	18.02.2020
EMPLOYER		
SCALE	1:100	A0

MANSOURAH - MASSARAH GOLD PROJECT
CIVIL WORKS GUIDE DRAWING
LOW GRADE CONDITIONING
PLAN AT EL. +912.200 - GRID A-I/1-7

DRAWING NUMBER MD-216-3640-EG-CV-GAD-1001
REV A02

Tekla Structures