


DRAWING NUMBER
MD - 216 - 3640 - EG - CV - GAD - 1316
REV
D01

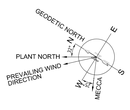




LAYOUT OF MISCELLANEOUS FOUNDATION
SCALE 1:150

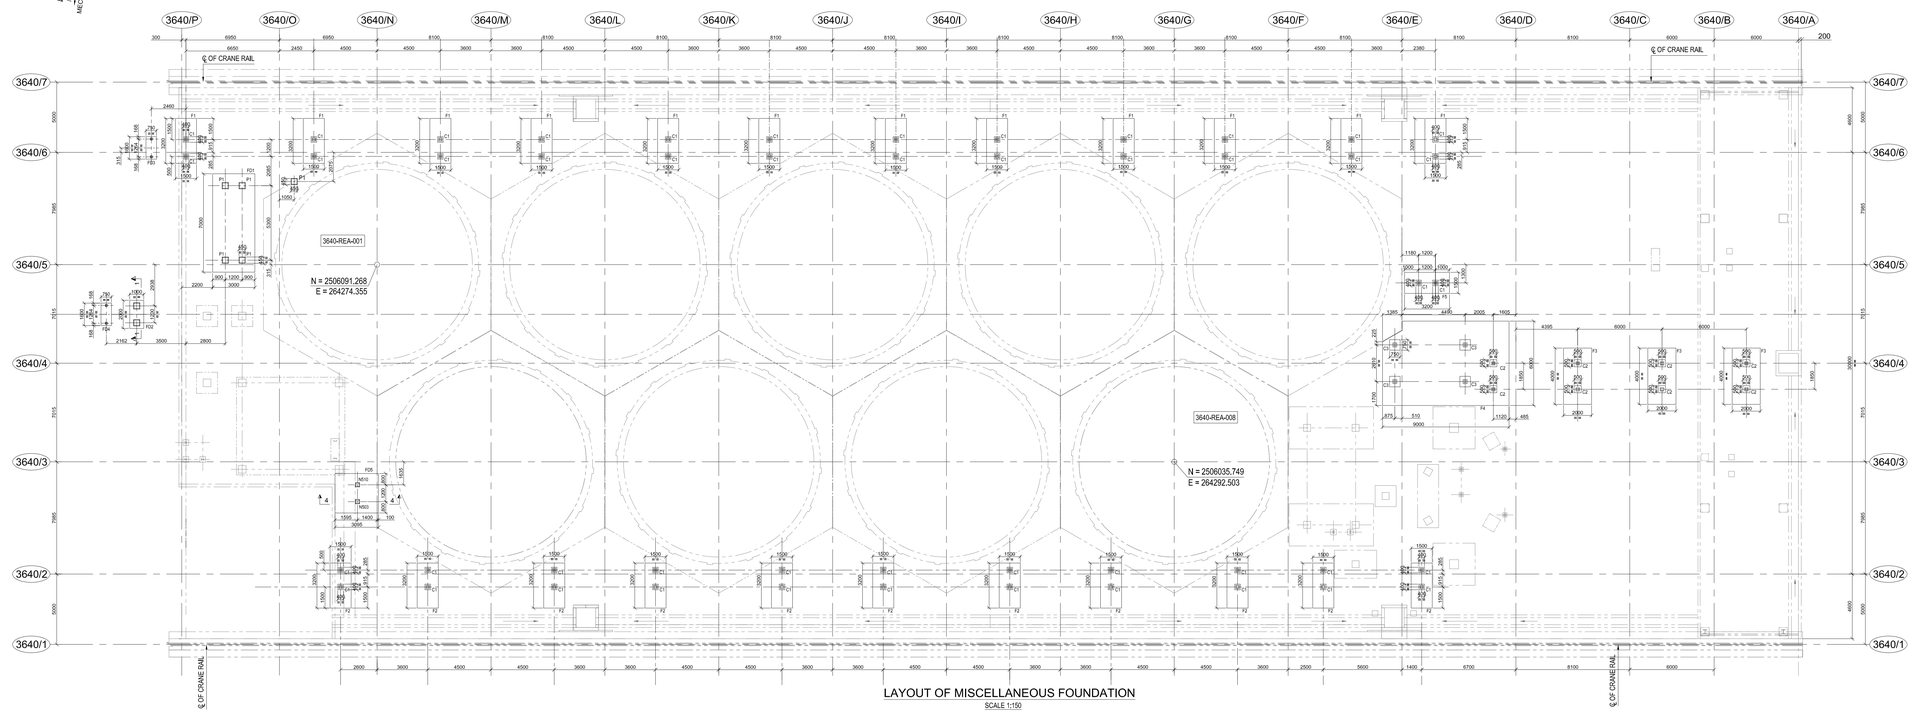



KEY PLAN
SCALE 1:1000

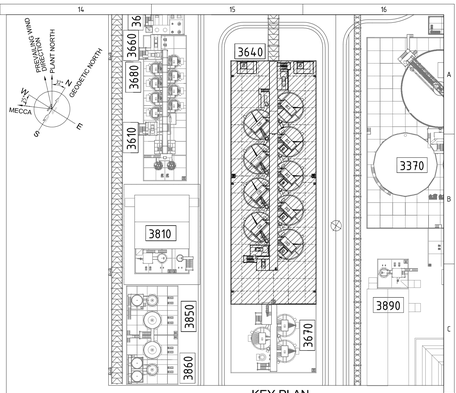

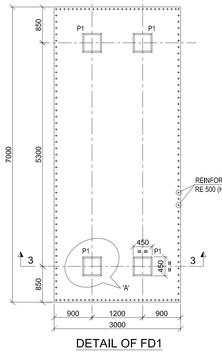

DETAIL OF FD1
SCALE 1:150

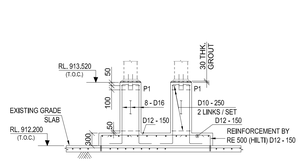


SECTION : 3-3
SCALE 1:50

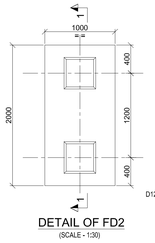


DETAIL OF FD2
SCALE 1:30

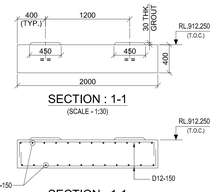



SECTION : 1-1
SCALE 1:30

SECTION : 1-1
(R.C DETAIL)
SCALE 1:30

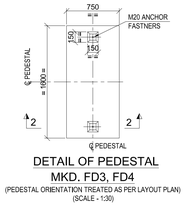



DETAIL OF PEDESTAL
MKD. FD3, FD4
(PEDESTAL ORIENTATION TREATED AS PER LAYOUT PLAN)
SCALE 1:30

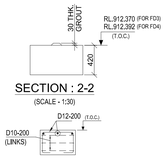



SECTION : 2-2
(SCALE - 1:30)


SECTION : 2-2
(R.C DETAIL)
(SCALE - 1:30)

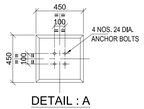



DETAIL : A
(DETAIL OF P1)
SCALE 1:20

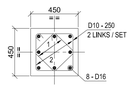



RCC. DET. OF P1
SCALE 1:20

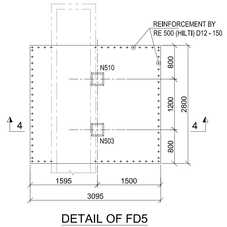


DETAIL OF FD5
SCALE 1:150

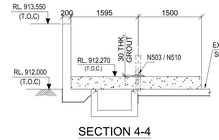


SECTION 4-4
SCALE 1:50

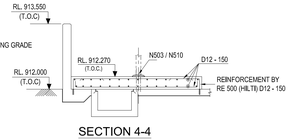


SECTION 4-4
(R.C DETAIL)
SCALE 1:50

## LEGEND :-

R.L. - REDUCED LEVEL
℄ - CENTRE LINE
T.O.C. - TOP OF CONCRETE
T.O.G. - TOP OF GROUT
TYP. - TYPICAL
F.G.L. - FINISHED GROUND LEVEL
F.F.L. - FINISHED FLOOR LEVEL
B.O.F. - BOTTOM OF FOUNDATION
MKD. - MARKED
P.C.C - PLAIN CEMENT CONCRETE

## NOTES:-

1. ALL DIMENSIONS ARE IN MILLIMETRES AND LEVELS AND CO-ORDINATES ARE IN METRES UNLESS OTHERWISE STATED.
2. NET SAFE BEARING CAPACITY OF SOIL AT BOTTOM OF FOUNDATION CONSIDERED AS 450KN/ SQ. M
3. GRADE OF CONCRETE SHALL BE C35 (35MPa) FOR FOUNDATION & C15 (15MPa) FOR BLINDING CONCRETE.
4. GRADE OF REINFORCEMENT SHALL BE DEFORMED BAR 420 MPa (GRADE 60) - ASTM A615/A615M.
5. IF ANY PART OF FOUNDATION COMES ON BACKFILL ZONE OF ADJACENT FOUNDATION OR ANY LOOSE SOIL ARE ENCOUNTERED BELOW FOUNDATION LEVEL THE SAME SHALL BE REMOVED AND FILLED WITH PCC.
6. FOR DETAIL OF ANCHOR BOLTS, REFER DRAWING NO. MD-216-1000-EG-CV-DED-1003.
7. FOR DETAILS OF FOUNDATION REFER DRAWING NO. MD-216-3640-EG-CV-GAD-1317, MD-216-3640-EG-CV-DED-1322.

| DOCUMENT NUMBER | REFERENCE DOCUMENTS | REV | DATE | REVISION DESCRIPTION | DRN | CHK | ENG | APP | EMP |
|---|---|---|---|---|---|---|---|---|---|
| MD-216-3640-EG-CV-GAD-1313 | LAYOUT & DETAIL OF MISCELLANEOUS FOUNDATION | | | | | | | | |
| MD-216-3640-EG-CV-GAD-1311 | LAYOUT & DETAIL OF TANK FOUNDATIONS | D01 | 05/05/2023 | AS - BUILT | ABS | SJM | AVG | AG | |
| MD-216-3640-EG-CV-GAD-1314 | LAYOUT OF GRADE SLAB | C02 | 16/09/2021 | ISSUED FOR CONSTRUCTION & REVISED AS MKD. (1/04) | ABS | SJM | AVG | AG | |
| MD-216-3640-EG-ME-GAD-1038 | LOW GRADE CONDITIONING, LEACHING PLAN AT EL.+912.200 | C01 | 26/11/2020 | ISSUED FOR CONSTRUCTION | ABS | SJM | AVG | AG | |
| MD-216-1000-EG-ST-CRT-1001 | CIVIL, STRUCTURAL & ARCHITECTURAL - DESIGN CRITERIA | A01 | 21/10/2020 | ISSUED FOR REFERENCE | RM | SJM | AVG | AG | |

RESERVED FOR VENDOR LOGO AND DRAWING NUMBER

LARSEN & TOUBRO

This drawing is the property of LARSEN & TOUBRO and must not be passed on to any person or body not authorised by us to receive it nor be copied or otherwise made use either in full or in part by such person or body without our prior permission in writing.

Outotec

The content of these documents are the sole property of Outotec Oy. Any rights not expressly granted herein are reserved. Reproduction, transfer or distribution of part or all of the contents in any form without prior written permission of Outotec is prohibited.

MA'ADEN معادن
Saudi Arabian Mining Company شركة معادن العربية السعودية

This document and the information contained herein is Ma'aden proprietary know-how. This document or any part thereof should not be reproduced, stored in a retrieval system or transmitted by any means, electronic or otherwise, or divulged without prior written permission of Ma'aden.

| | | | |
|---|---|---|---|
| LARSEN & TOUBRO DRAWING NUMBER | | | REVISION |
| 019045_450_C_G_24382_001 | | | 3 |
| OUTOTEC DRAWING NUMBER | | DOCUMENT ID | REVISION |
| 900707 __ GAU01 __ HL13 __ MTL01 __ 36437 | | OU100695966 | 3 |
| DRAWN | RM | 13/10/2020 | MANSOURAH - MASSARAH GOLD PROJECT |
| CHECKED | SJM | 19/10/2020 | GENERAL ARRANGEMENT DRAWING |
| ENGINEER | AVG | 19/10/2020 | LOW GRADE CONDITIONING,LEACHING & ADSORPTION |
| APPROVED | AG | 21/10/2020 | LAYOUT OF MISCELLANEOUS FOUNDATION |
| EMPLOYER | | | |
| SCALE 1:150 | A0 | | DRAWING NUMBER: MD - 216 - 3640 - EG - CV - GAD - 1316 |
| | | | REV: D01 |