


DRAWING NUMBER: MD-216-49PQ-EG-CV-GAD-1614 | REV: D01

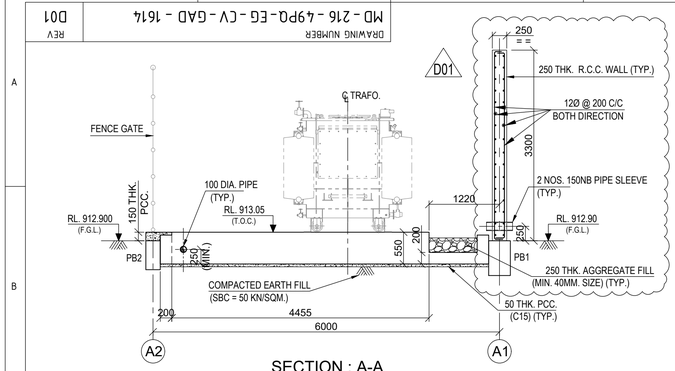


SECTION : A-A
SCALE 1:50

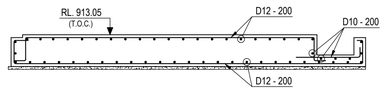

SECTION : A-A
(RC. DETAIL)
SCALE 1:50

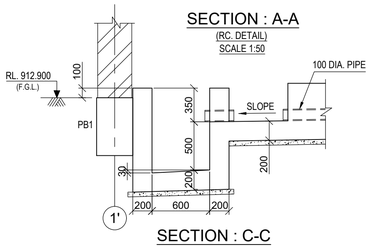


SECTION : C-C
SCALE 1:30

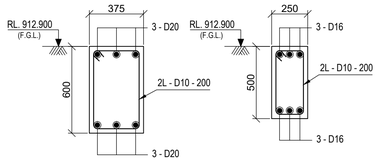


RC. DET. OF PB1
SCALE 1:20


RC. DET. OF PB2
SCALE 1:20

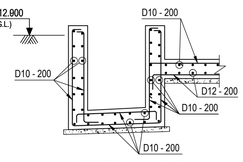

SECTION : C-C
(RC. DETAIL)
SCALE 1:30

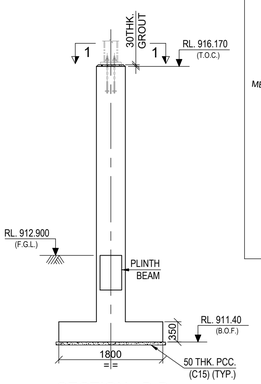


SECTION : B-B
SCALE 1:50

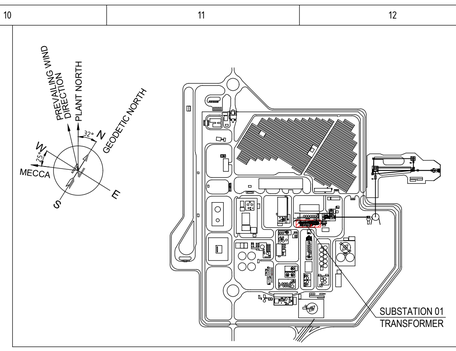


KEY PLAN


ALL CABLE CONDUITS SHALL BE LAID AS PER ELECTRICAL DWG. MD-216-49PQ-EG-EL-LAD-1013

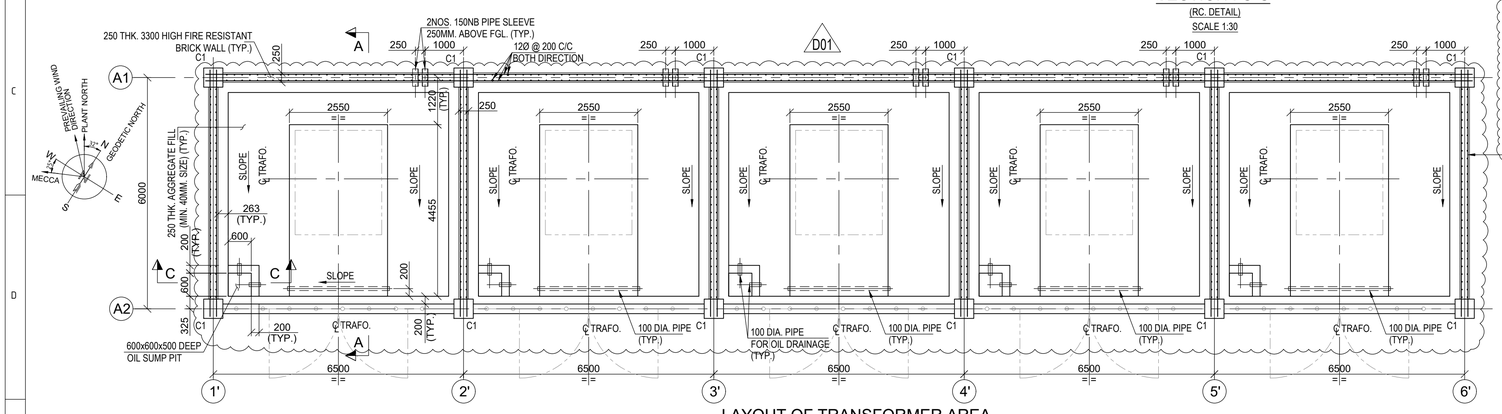


LAYOUT OF TRANSFORMER AREA
SCALE 1:75

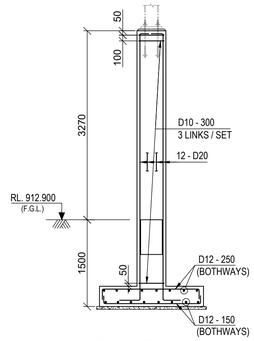


SECTION : A'-A'
SCALE 1:50

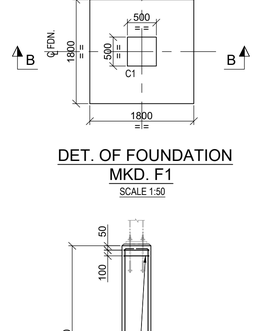


RC. DET. OF FOUNDATION
MKD. F1
SCALE 1:50

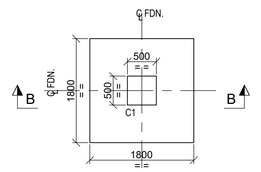


DET. OF FOUNDATION
MKD. F1
SCALE 1:50

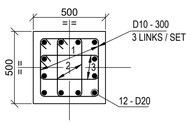

RC. DET. OF COLUMN
MKD. C1
SCALE 1:20

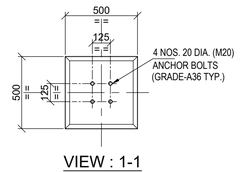

VIEW : 1-1
(DETAIL OF COL. MKD. C1)
SCALE 1:20

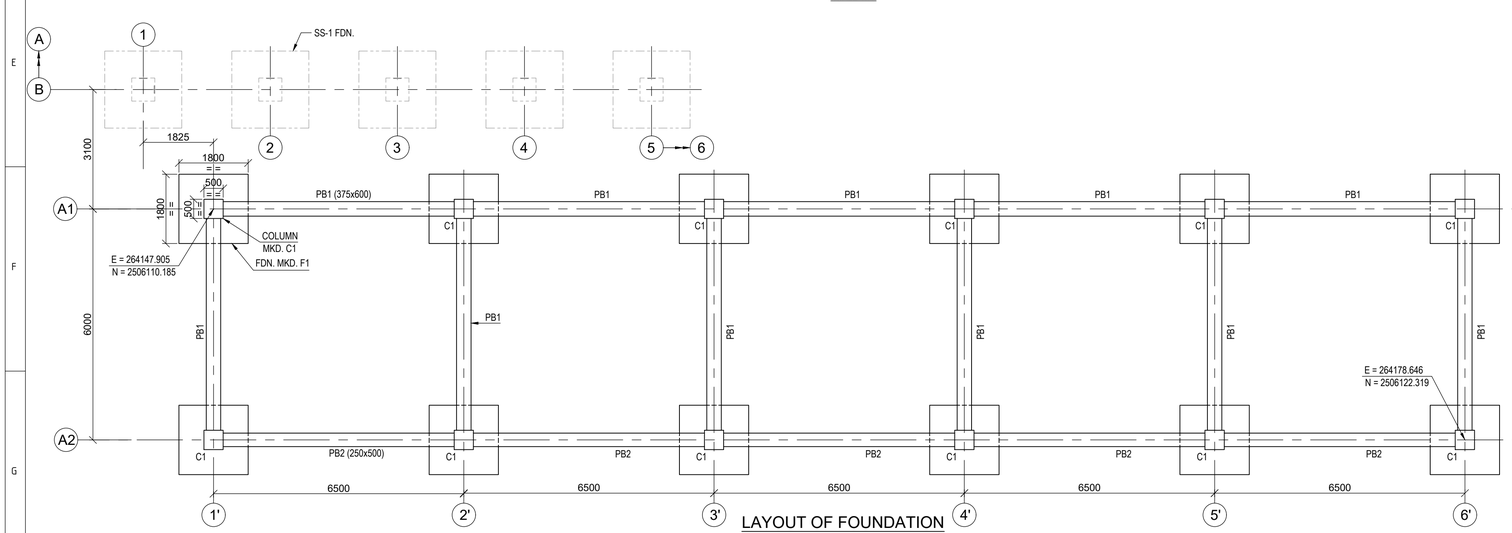

LAYOUT OF FOUNDATION
SCALE 1:75

LEGENDS :-

R.L. - REDUCED LEVEL
℄ - CENTRE LINE
T.O.C. - TOP OF CONCRETE
TYP. - TYPICAL
T.O.G. - TOP OF GROUT
B.O.F. - BOTTOM OF FOUNDATION
F.G.L. - FINISHED GROUND LEVEL.
F.F.L. - FINISHED FLOOR LEVEL
P.C.C - PLAIN CEMENT CONCRETE
DET. - DETAIL
FDN. - FOUNDATION
THK. - THICK
R.C. - REINFORCED CONCRETE
MKD. - MARKED
TRAFO. - TRANSFORMER
MIN. - MINIMUM
DIA. - DIAMETER
BOTTOM REINFORCEMENT (B) - – – – – –
TOP REINFORCEMENT (T) - ———

NOTES:-

1. ALL DIMENSIONS ARE IN MILLIMETRES AND LEVELS AND CO-ORDINATES ARE IN METRES UNLESS OTHERWISE STATED.
2. NET SAFE BEARING CAPACITY OF SOIL AT BOTTOM OF FOUNDATION IS CONSIDERED AS 450KN/ SQ. M.
3. GRADE OF CONCRETE SHALL BE C35 (35Mpa) FOR FOUNDATION, C30 (30Mpa) FOR GRADE SLAB & C15 (15Mpa) FOR BLINDING CONCRETE.
4. GRADE OF REINFORCEMENT SHALL BE DEFORMED BAR 420 MPa (GRADE 60) - ASTM A615/A615M.
5. CLEAR COVER TO REINFORCEMENT SHALL BE FOUNDATIONS = 50 MM., COLUMNS = 50 MM., BEAM = 25 MM.
6. FOR STANDARD REINFORCEMENT DETAIL & GENERAL NOTES FOR CIVIL WORKS REFER DRAWING NO. MD-216-1000-EG-CV-DED-1005 & 1001.

DOCUMENT NUMBER	REFERENCE DOCUMENTS	REV	DATE	REVISION DESCRIPTION	DRN	CHK	ENG	APP	EMP
		D01	12/04/2023	AS - BUILT - REVISED AS MKD. (001)	ABS	SJM	AVG	AG	
		C02	23/02/2021	ISSUED FOR CONSTRUCTION & REVISED AS MKD. (C02)	ABS	SJM	AVG	AG	
MD-216-49PQ-EG-CV-GAD-1623	LAYOUT OF FOUNDATIONS	C01	02/01/2021	ISSUED FOR CONSTRUCTION	MNS	SJM	AVG	AG	
MD-216-1000-EG-ST-CRT-1001	CIVIL, STRUCTURAL & ARCHITECTURAL - DESIGN CRITERIA	A01	28/11/2020	ISSUED FOR APPROVAL	MNS	SJM	AVG	AG	

RESERVED FOR VENDOR LOGO AND DRAWING NUMBER

LARSEN & TOUBRO DRAWING NUMBER: 019045_950_C_G_24304__002 | REVISION: 3

OUTOTEC DRAWING NUMBER: 900707__GAU01__WD01__MTL01__45028 | DOCUMENT ID: OU100684605 | REVISION: 3

LARSEN & TOUBRO

This drawing is the property of LARSEN & TOUBRO and must not be passed on to any person or body not authorized by us to receive it nor be copied or otherwise made use either in full or in part by such person or body without our prior permission in writing.

Outotec

The content of these documents are the sole property of Outotec Oyj. Any rights not expressly granted herein are reserved. Reproduction, transfer or distribution of part or all of the contents in any form without prior written permission of Outotec is prohibited.

MA'ADEN معادن
Saudi Arabian Mining Company شركة التعدين العربية السعودية

This document and the information contained herein is Ma'aden proprietary know-how. This document or any part thereof should not be reproduced, stored in a retrieval system or transmitted by any means, electronic or otherwise, or divulged without prior written permission of Ma'aden.

DRAWN	MNS	24/11/2020	
CHECKED	SJM	26/11/2020	
ENGINEER	AVG	25/11/2020	
APPROVED	AG	28/11/2020	
EMPLOYER			
SCALE	1:20, 1:30, 1:50, 1:75		A1

MANSOURAH - MASSARAH GOLD PROJECT
GENERAL ARRANGEMENT
PROCESS PLANT SUBSTATION 01
DETAIL OF TRANSFORMER AREA

DRAWING NUMBER: MD-216-49PQ-EG-CV-GAD-1614 | REV: D01