


DRAWING NUMBER MD-216-39MA-EG-CV-GAD-1030 REV D01

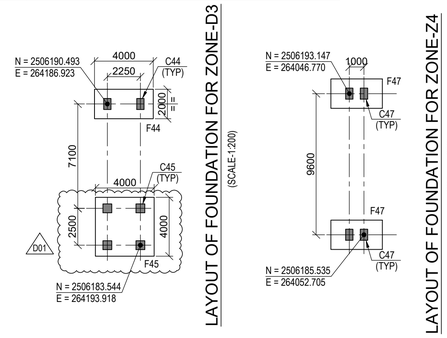


LAYOUT OF FOUNDATION FOR ZONE-D3 (SCALE-1:200)

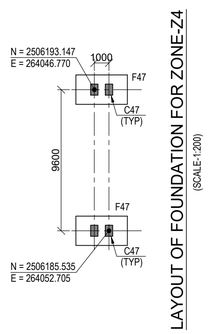


LAYOUT OF FOUNDATION FOR ZONE-Z4 (SCALE-1:200)

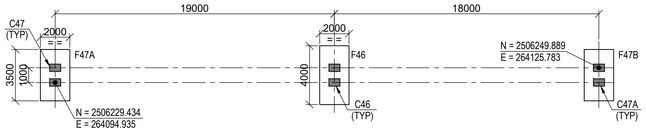


LAYOUT OF FOUNDATION FOR ZONE-Z5
(SCALE-1:200)

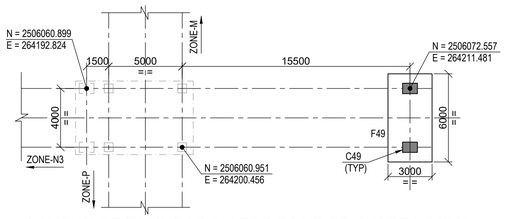


LAYOUT OF FOUNDATION FOR ZONE-PB-1 (AREA-3610)
(SCALE-1:200)

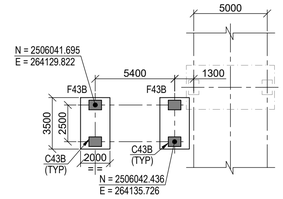


LAYOUT OF FOUNDATION FOR ZONE-PB-2 (AREA-3410)
(SCALE-1:200)

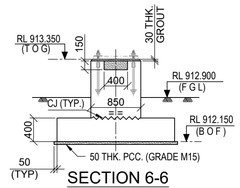


SECTION 6-6
(SCALE-1:50)

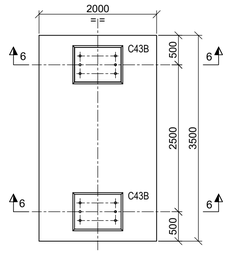


FOUNDATION PLAN MKD. F43B
(2 NOS. REQD.)
SCALE-1:50

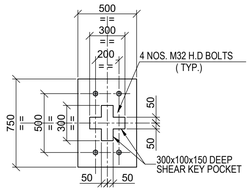


DETAIL OF COLUMN MKD. C44, C46, C47, C47A & C47B
(SCALE-1:25)

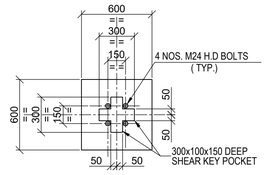


DETAIL OF COLUMN MKD. C45
(SCALE-1:25)

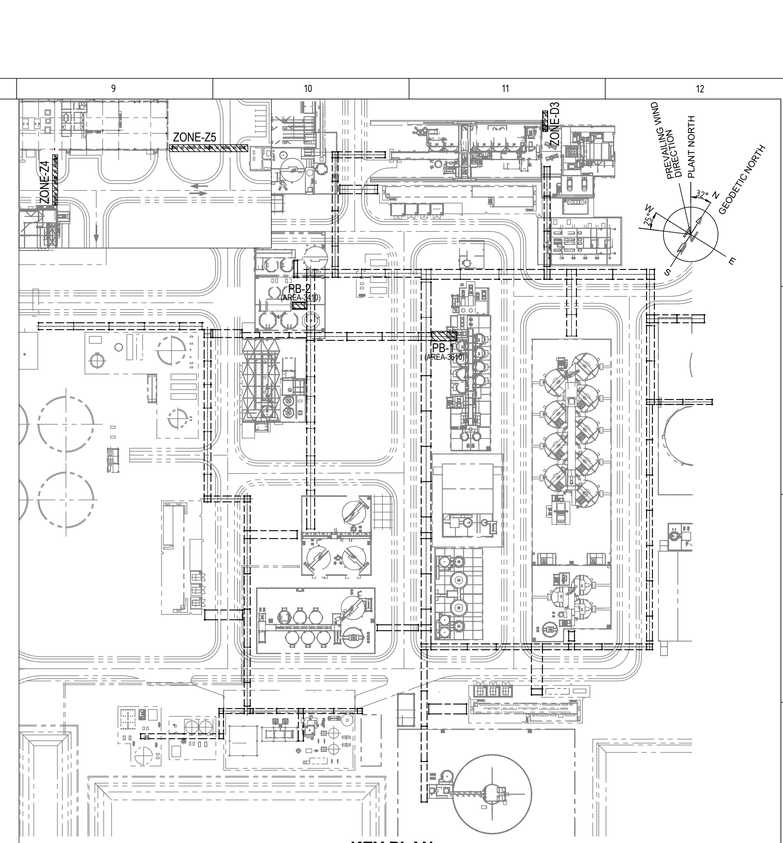


KEY PLAN
(SCALE - 1:1500)

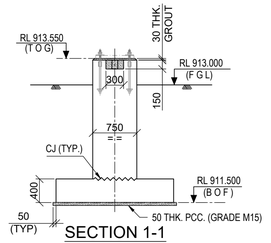


SECTION 1-1
(SCALE-1:50)

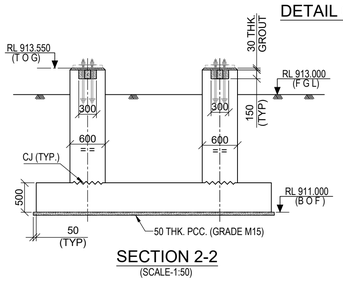


SECTION 2-2
(SCALE-1:50)

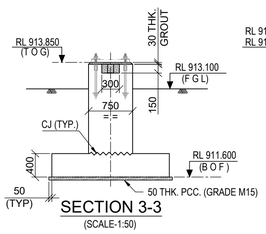


SECTION 3-3
(SCALE-1:50)

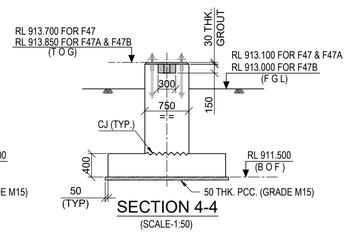


SECTION 4-4
(SCALE-1:50)

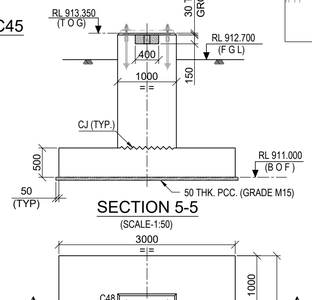


SECTION 5-5
(SCALE-1:50)

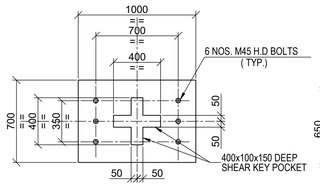


DETAIL OF COLUMN MKD. C49
(SCALE-1:25)

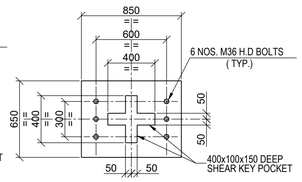


DETAIL OF COLUMN MKD. C43B
(SCALE-1:25)

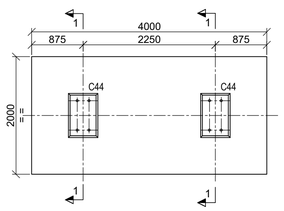


FOUNDATION PLAN MKD. F44
(1 NO. REQD.)
SCALE-1:50

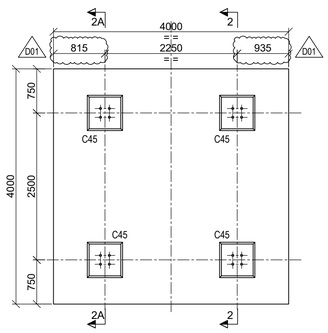


FOUNDATION PLAN MKD. F45
(1 NO. REQD.)
SCALE-1:50

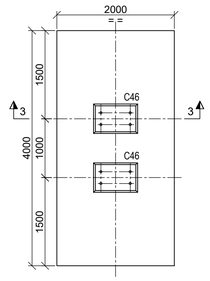

FOUNDATION PLAN MKD. F46
(1 NO. REQD.)
SCALE-1:50

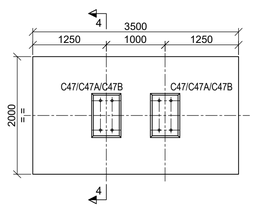

FOUNDATION PLAN MKD. F47,F47A & F47B
(4 NOS. REQD.)
SCALE-1:50

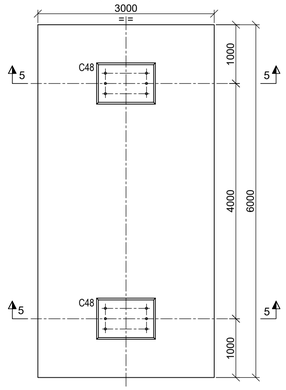

FOUNDATION PLAN MKD. F49
(1 NO. REQD.)
SCALE-1:50

LEGEND :-

R L - REDUCED LEVEL
T O G - TOP OF GROUT
C J - CONSTRUCTION JOINT
F G L - FINISHED GROUND LEVEL
P C C - PLAIN CEMENT CONCRETE
FDN. - FOUNDATION
B O F - BOTTOM OF FOUNDATION
THK. - THICK
N T S - NOT TO SCALE
MKD. - MARKED
TYP. - TYPICAL
DIA. - DIAMETER
REQD. - REQUIRED
DOC. - DOCUMENT

NOTES:-

1. ALL DIMENSIONS ARE IN MILLIMETRES AND LEVELS AND CO-ORDINATES ARE IN METRES UNLESS OTHERWISE STATED.
2. NET SAFE BEARING CAPACITY OF SOIL AT BOTTOM OF FOUNDATION CONSIDERED 450KN/ SQ. M
3. IF ANY PART OF FOUNDATION COMES ON BACKFILL ZONE OF ADJACENT FOUNDATION OR ANY LOOSE SOIL ARE ENCOUNTERED BELOW FOUNDATION LEVEL THE SAME SHALL BE REMOVED AND FILLED WITH PCC (M15).
4. THE CONTENT OF THIS DRAWING SHALL CONFORM TO THE PROVISIONS OF CIVIL, STRUCTURAL AND ARCHITECTURAL DESIGN CRITERIA DOC. NO. MD-216-1000-EG-ST-CRT-1001.
5. CO-ORDINATE TO BE CHECKED & VERIFIED FROM 3D MODEL & DRAWING NO. MD-216-39MA-EG-ST-GAD-2001 BEFORE CONSTRUCTION
6. FOR FOUNDATION BOLT DETAILS REFER DRAWING NO : MD-216-1000-EG-CV-DED-1003.

DOCUMENT NUMBER	REFERENCE DOCUMENTS	REV	DATE	REVISION DESCRIPTION	DRN	CHK	ENG	APP	EMP
		D01	26/04/2023	AS - BUILT - REVISED AS MKD. D01	AMT	BDA	SML	AG	
		C04	05/01/2021	ISSUED FOR CONSTRUCTION AND REVISED AS MKD. C04	AMT	BDA	SML	AG	
		C03	02/11/2020	ISSUED FOR CONSTRUCTION AND REVISED AS MKD. C03	AMT	BDA	SML	AG	
MD-216-39MA-EG-ME-GAD-1001	LAYOUT WITH ZONE MARKINGS	C02	07/10/2020	ISSUED FOR CONSTRUCTION AND REVISED AS MKD. C02	AMT	BDA	SML	AG	
MD-216-3000-EG-CV-GAD-1001	PROCESS PLANT EARTHWORKS	C01	25/09/2020	ISSUED FOR CONSTRUCTION AND REVISED AS MKD. C01	AMT	BDA	SML	AG	
MD-216-39MA-EG-ST-GAD-2001	PROCESS PLANT PIPE RACK CUM CABLE RACK	A01	28/08/2020	ISSUED FOR REFERENCE	AMT	BDA	SML	AG	

RESERVED FOR VENDOR LOGO AND DRAWING NUMBER

LARSEN & TOUBRO

This drawing is the property of LARSEN & TOUBRO and must not be passed on to any person or body not authorized by us to receive it nor be copied or otherwise made use either in full or in part by such person or body without our prior permission in writing.

Outotec

The content of these documents are the sole property of Outotec Oyj. Any rights not expressly granted herein are reserved. Reproduction, transfer or distribution of part or all of the contents in any form without prior written permission of Outotec is prohibited.

MA'ADEN معادن
Saudi Arabian Mining Company شركة معادن العربية السعودية

This document and the information contained herein is Ma'aden proprietary know-how. This document or any part thereof should not be reproduced, stored in a retrieval system or transmitted by any means, electronic or otherwise, or divulged without prior written permission of Ma'aden.

LARSEN & TOUBRO DRAWING NUMBER	O19045_080_C_G_24012_016		REVISION 5
OUTOTEC DRAWING NUMBER	900707__GAU01__ZZ01__MTL01__00103	DOCUMENT ID OU100695764	REVISION 5
DRAWN	AMT	22/08/2020	MANSOURAH - MASSARAH GOLD PROJECT
CHECKED	BDA	25/08/2020	GENERAL ARRANGEMENT
ENGINEER	SML	22/08/2020	PROCESS PLANT PIPE RACK CUM CABLE RACK
APPROVED	AG	28/08/2020	PLAN & SECTIONS
EMPLOYER			
SCALE 1:200,1:50,1:25	A1		DRAWING NUMBER MD-216-39MA-EG-CV-GAD-1030 REV D01