| DRAWING NUMBER | REV |
|---|---|
| MD-216-3320-EG-CV-GAD-1001 | A02 |

## LEVEL +912.000
1:100

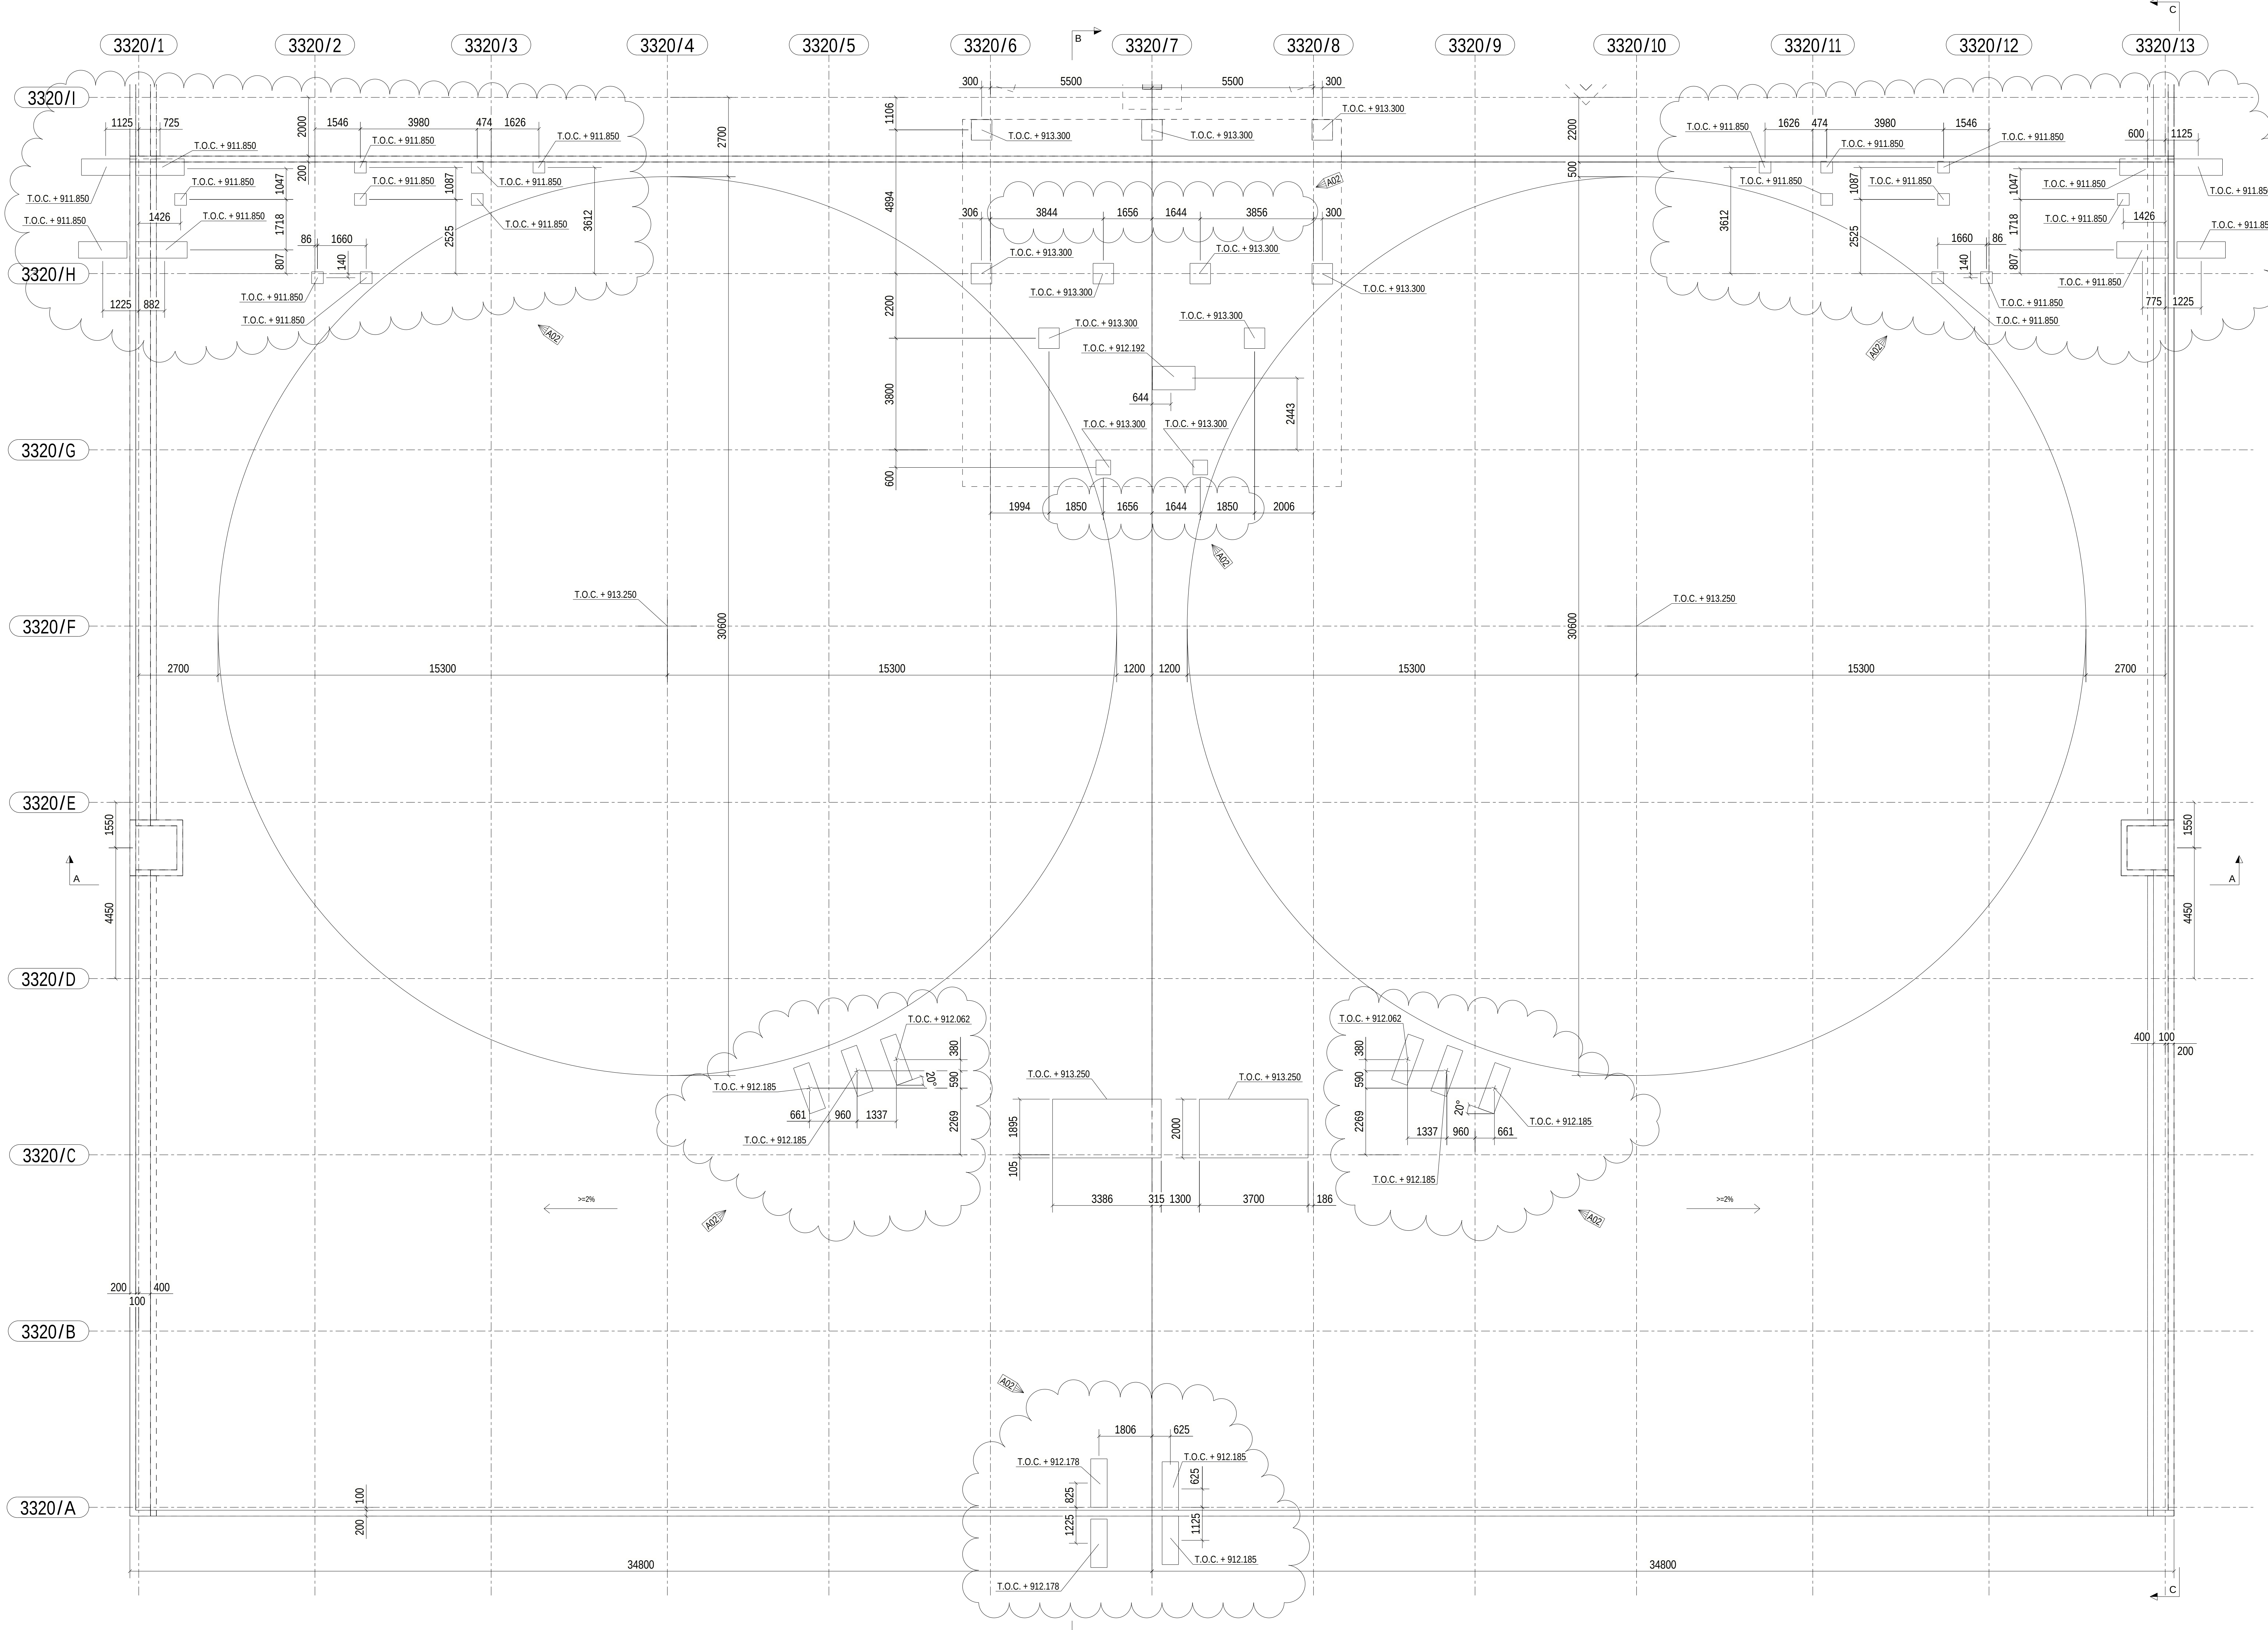
3320/1
3320/2
3320/3
3320/4
3320/5
3320/6
3320/7
3320/8
3320/9
3320/10
3320/11
3320/12
3320/13
3320/I
3320/H
3320/G
3320/F
3320/E
3320/D
3320/C
3320/B
3320/A
B
C
A
T.O.C. + 911.850
T.O.C. + 913.300
T.O.C. + 912.192
T.O.C. + 913.250
T.O.C. + 912.062
T.O.C. + 912.185
T.O.C. + 912.178
2700
15300
1200
30600
34800
5500
300
>=2%
A02

## C - C
1:100

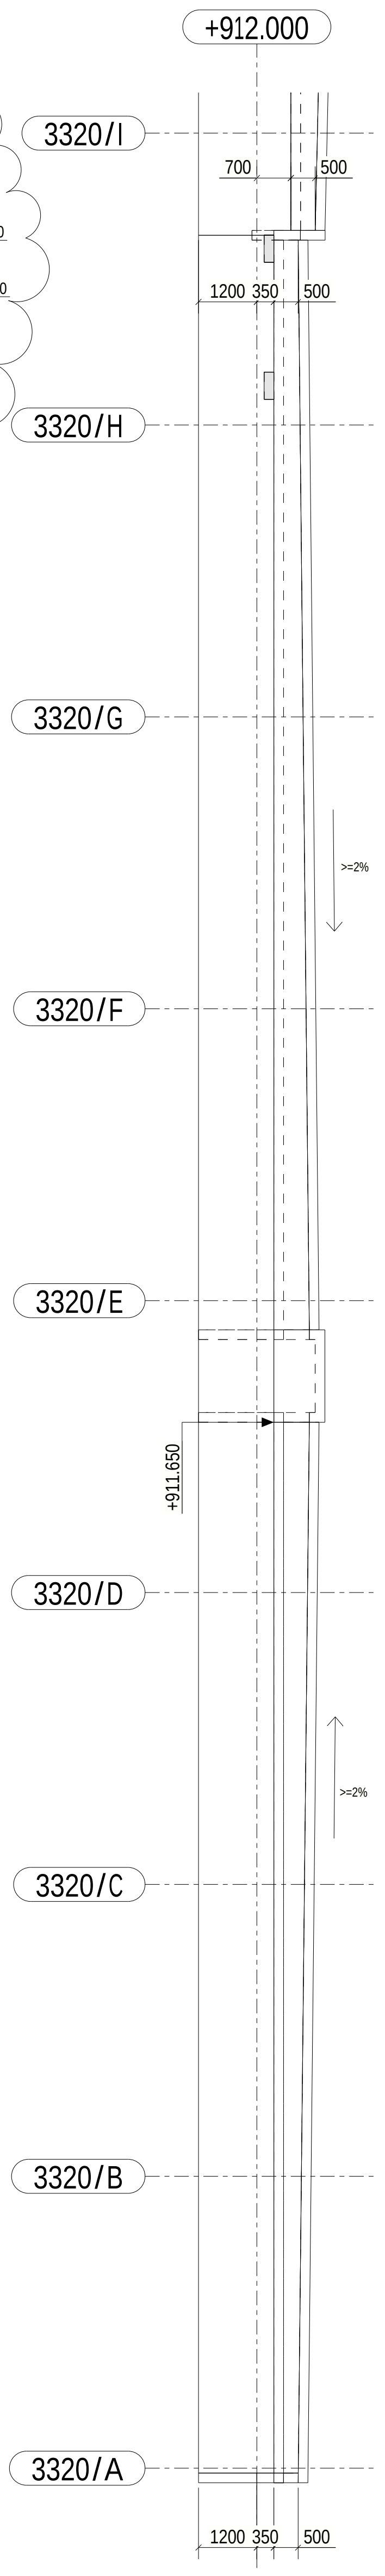
+912.000
3320/I
3320/H
3320/G
3320/F
3320/E
3320/D
3320/C
3320/B
3320/A
700
500
1200
350
+911.650
>=2%

## A - A
1:100

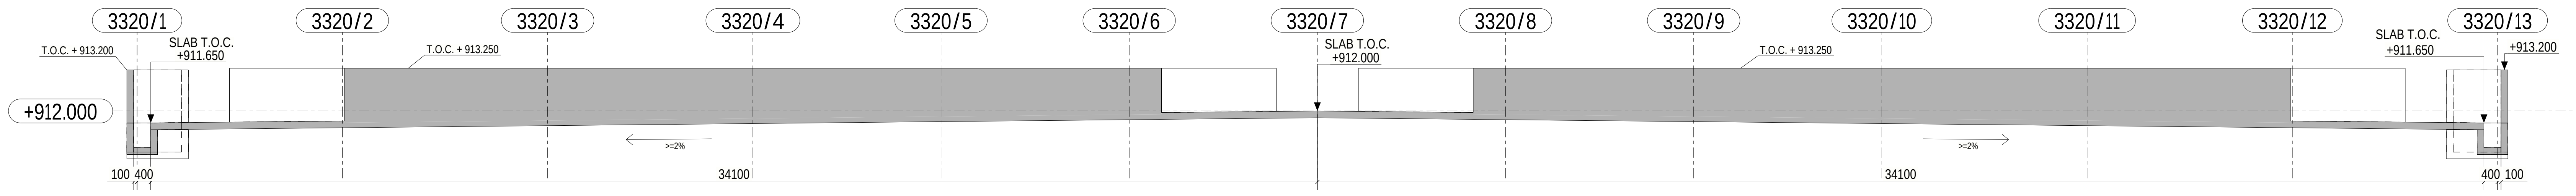
3320/1
3320/2
3320/3
3320/4
3320/5
3320/6
3320/7
3320/8
3320/9
3320/10
3320/11
3320/12
3320/13
T.O.C. + 913.200
SLAB T.O.C. +911.650
T.O.C. + 913.250
SLAB T.O.C. +912.000
+913.200
+912.000
>=2%
100
400
34100

## B - B
1:100

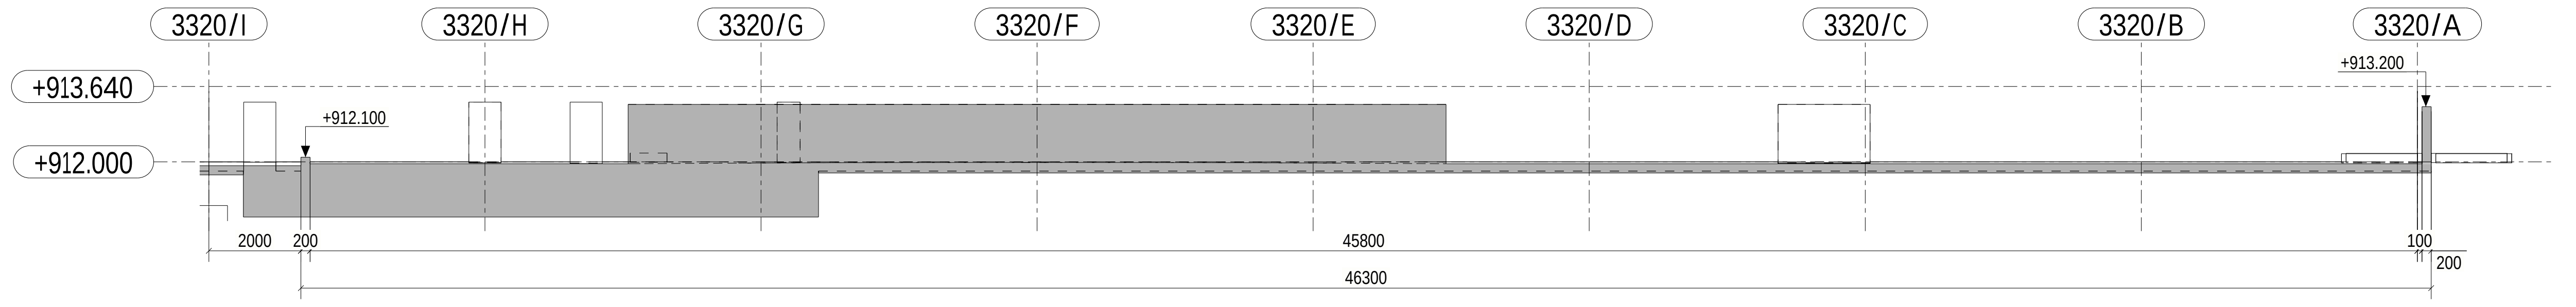
3320/I
3320/H
3320/G
3320/F
3320/E
3320/D
3320/C
3320/B
3320/A
+913.640
+912.000
+912.100
+913.200
2000
200
45800
46300
100

THIS DESIGN IS NOT ISSUED FOR CONSTRUCTION

FINISHED TOP GROUND LEVEL (F.G.L) FOR PROCESS AREA 3320 = RL(+)912.000 m

| | |
|---|---|
| ▥ | CONCRETE ELEMENT FLOOR (PRE-CAST SLAB) |
| ▨ | CONCRETE FLOOR |
| ▨ A | CONCRETE FLOOR WITH ACID RESISTANT COATING |
| ▤ | CONCRETE WALL |

1. ALL DIMENSIONS ARE IN MILLIMETER, ELEVATIONS ARE IN METER UNLESS OTHERWISE STATED
2. CO-ORDINATES ARE SHOWN IN GENERAL ARRENGEMENT DRAWINGS
3. GRATING TYPE (FRP OR NORMAL) IS SPECIFIED IN GENERAL ARRENGEMENT DRAWINGS
4. F.F.L, F.G.L, T.O.C = FINISHED FLOOR LEVEL, FINISHED GROUND LEVEL, TOP OF CONCRETE, T.O.S, B.O.S, B.O.B, = TOP OF STEEL, BOTTOM OF STEEL, BOTTOM OF BASE PLATE
5. BUILDING DIMENSIONS AND HEIGHTS ARE TENTATIVE, SHALL BE FINALIZED DURING DETAIL ENGINEERING SUBJECT TO MINIMUM AS SHOWN.
6. ALL MAINTENANCE FACILITIES, HANDLING PROVISIONS, ACCESS WAYS, PLATFORMS FOR MAINTENANCE SHALL BE PROVIDED DURING DETAIL ENGINEERING WHICH ARE NOT SHOWN ENTIRELY. THIS DRAWING IS TO BE CONSIDERED AS CONCEPTUAL ARRANGEMENT OF THE FACILITIES.

## KEYPLAN

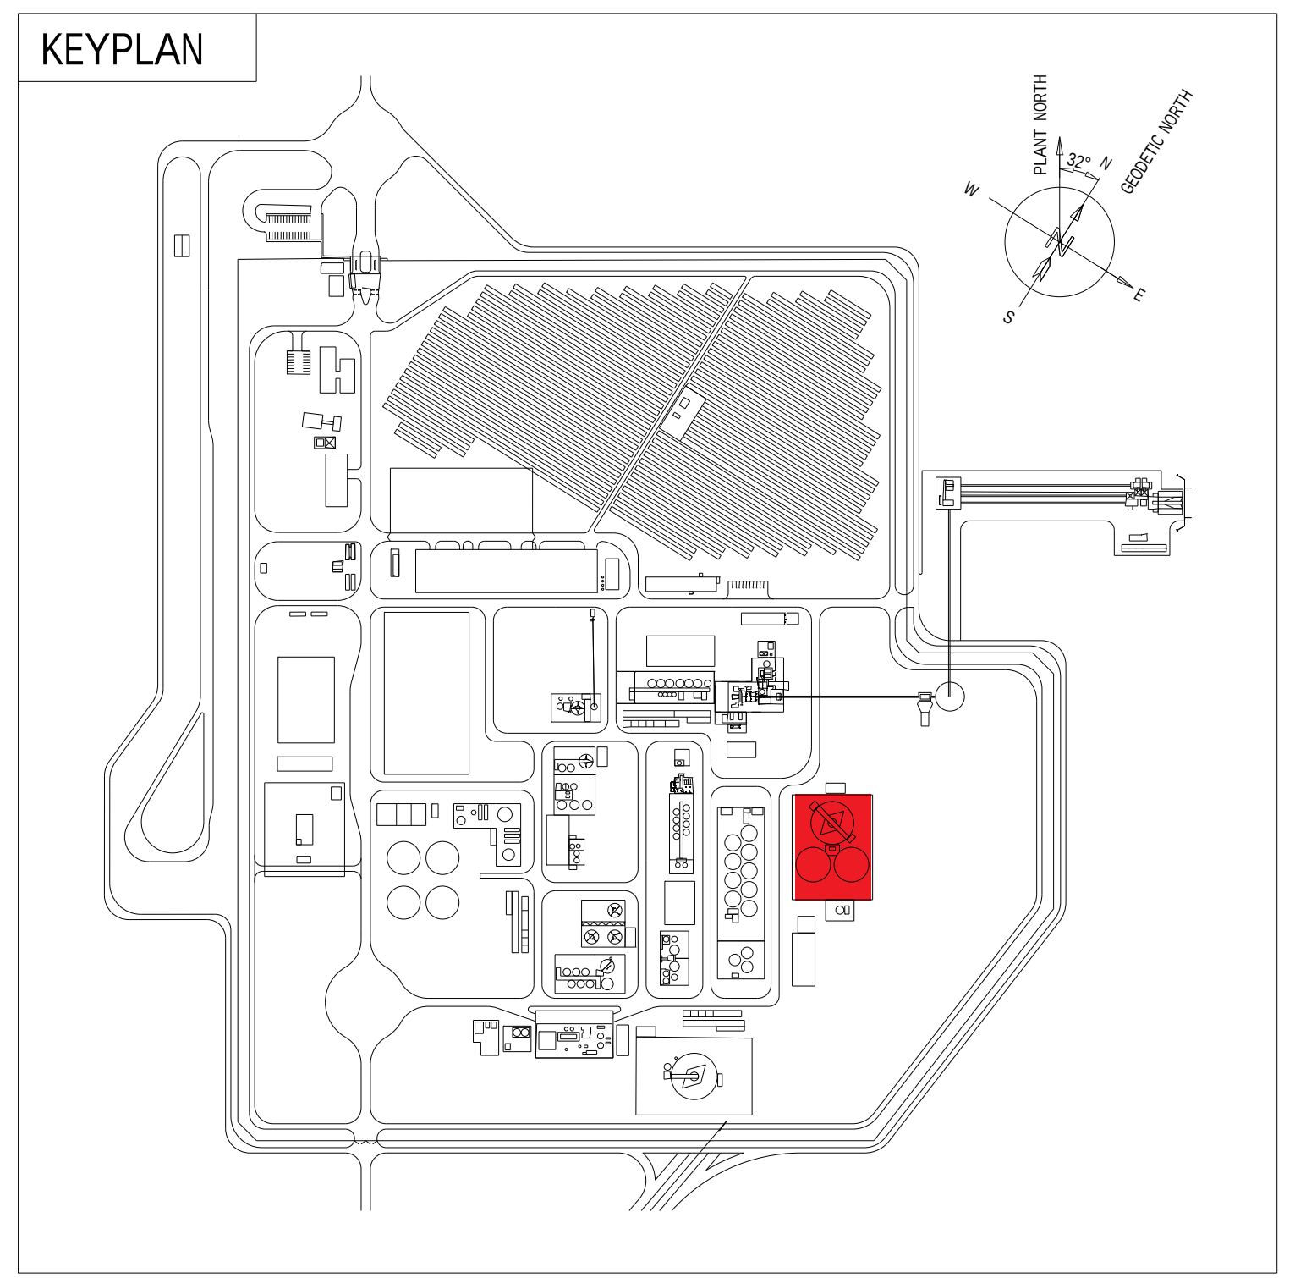
PLANT NORTH
GEODETIC NORTH
32°
N
W

| DOCUMENT NUMBER | REFERENCE DOCUMENTS | DOCUMENT NUMBER | REFERENCE DOCUMENTS | REV | DATE | REVISION DESCRIPTION | DRN | CHK | ENG | APP | EMP | REV | DATE | REVISION DESCRIPTION | DRN | CHK | ENG | APP | EMP |
|---|---|---|---|---|---|---|---|---|---|---|---|---|---|---|---|---|---|---|---|
| MD-216-3320-EG-ST-GAD-1001 | PLAN AND SECTIONS | | | | | | | | | | | | | | | | | | |
| MD-216-1000-EG-ST-CRT-0001 | CIVIL,STRUCTURAL AND ARCHITECTURAL DESIGN BASIS | MD-216-3320-EG-CV-GAD-1002 | PLAN AT EL. +912.000 | | | | | | | | | | | | | | | | |
| MD-216-3320-EG-ME-GAD-1009 | SECTION A-A AND B-B | MD-216-3320-EG-ME-GAD-1010 | SECTION C-C AND D-D | | | | | | | | | A02 | 18.02.2020 | ISSUED FOR DETAIL DESIGN, FOUNDATIONS ADDED AND UPDATED | KirJok | MikLai | LuiPiz | SouCha | |
| MD-216-3320-EG-ME-GAD-1007 | PLAN AT EL. +912.000 | MD-216-3320-EG-ME-GAD-1008 | PLAN VIEW | | | | | | | | | A01 | 11.12.2019 | ISSUED FOR APPROVAL | AnnFor | MikLai | LuiPiz | SouCha | |

RESERVED FOR VENDOR LOGO AND DRAWING NUMBER

LARSEN & TOUBRO

This drawing is the property of LARSEN & TOUBRO and must not be passed on to any person or body not authorized by us to receive it nor be copied or otherwise made use either in full or in part by such person or body without our prior permission in writing.

Outotec

The content of these documents are the sole property of Outotec Oyj. Any rights not expressly granted herein are reserved. Reproduction, transfer or distribution of part or all of the contents in any form without prior written permission of Outotec is prohibited.

MA'ADEN معادن
Saudi Arabian Mining Company شركة التعدين العربية السعودية

This document and the information contained herein is Ma'aden proprietary know-how. This document or any part thereof should not be reproduced, stored in a retrieval system or transmitted by any means, electronic or otherwise, or divulged without prior written permission of Ma'aden.

| | | | |
|---|---|---|---|
| LARSEN & TOUBRO DRAWING NUMBER | 019045_450_C_G_24924_001 | REVISION | 1 |
| OUTOTEC DRAWING NUMBER | 900707_GAU01_ST02_CTA04_33201 | DOCUMENT ID<br>OU100667775 | REVISION<br>1 |
| DRAWN | AnnFor | 11.12.2019 | |
| CHECKED | MikLai | 11.12.2019 | |
| ENGINEER | LuiPiz | 11.12.2019 | |
| APPROVED | SouCha | 11.12.2019 | |
| EMPLOYER | | | |
| SCALE | 1:100 | A0 | |

MANSOURAH - MASSARAH GOLD PROJECT
CIVIL WORKS GUIDE DRAWING
3320 LOW GRADE THICKENING
PLAN AT EL. +912.000

| DRAWING NUMBER | REV |
|---|---|
| MD-216-3320-EG-CV-GAD-1001 | A02 |

Tekla Structures