

DRAWING NUMBER MD-216-3320-EG-CV-GAD-1002 REV A03


LEVEL +912.000
1:100

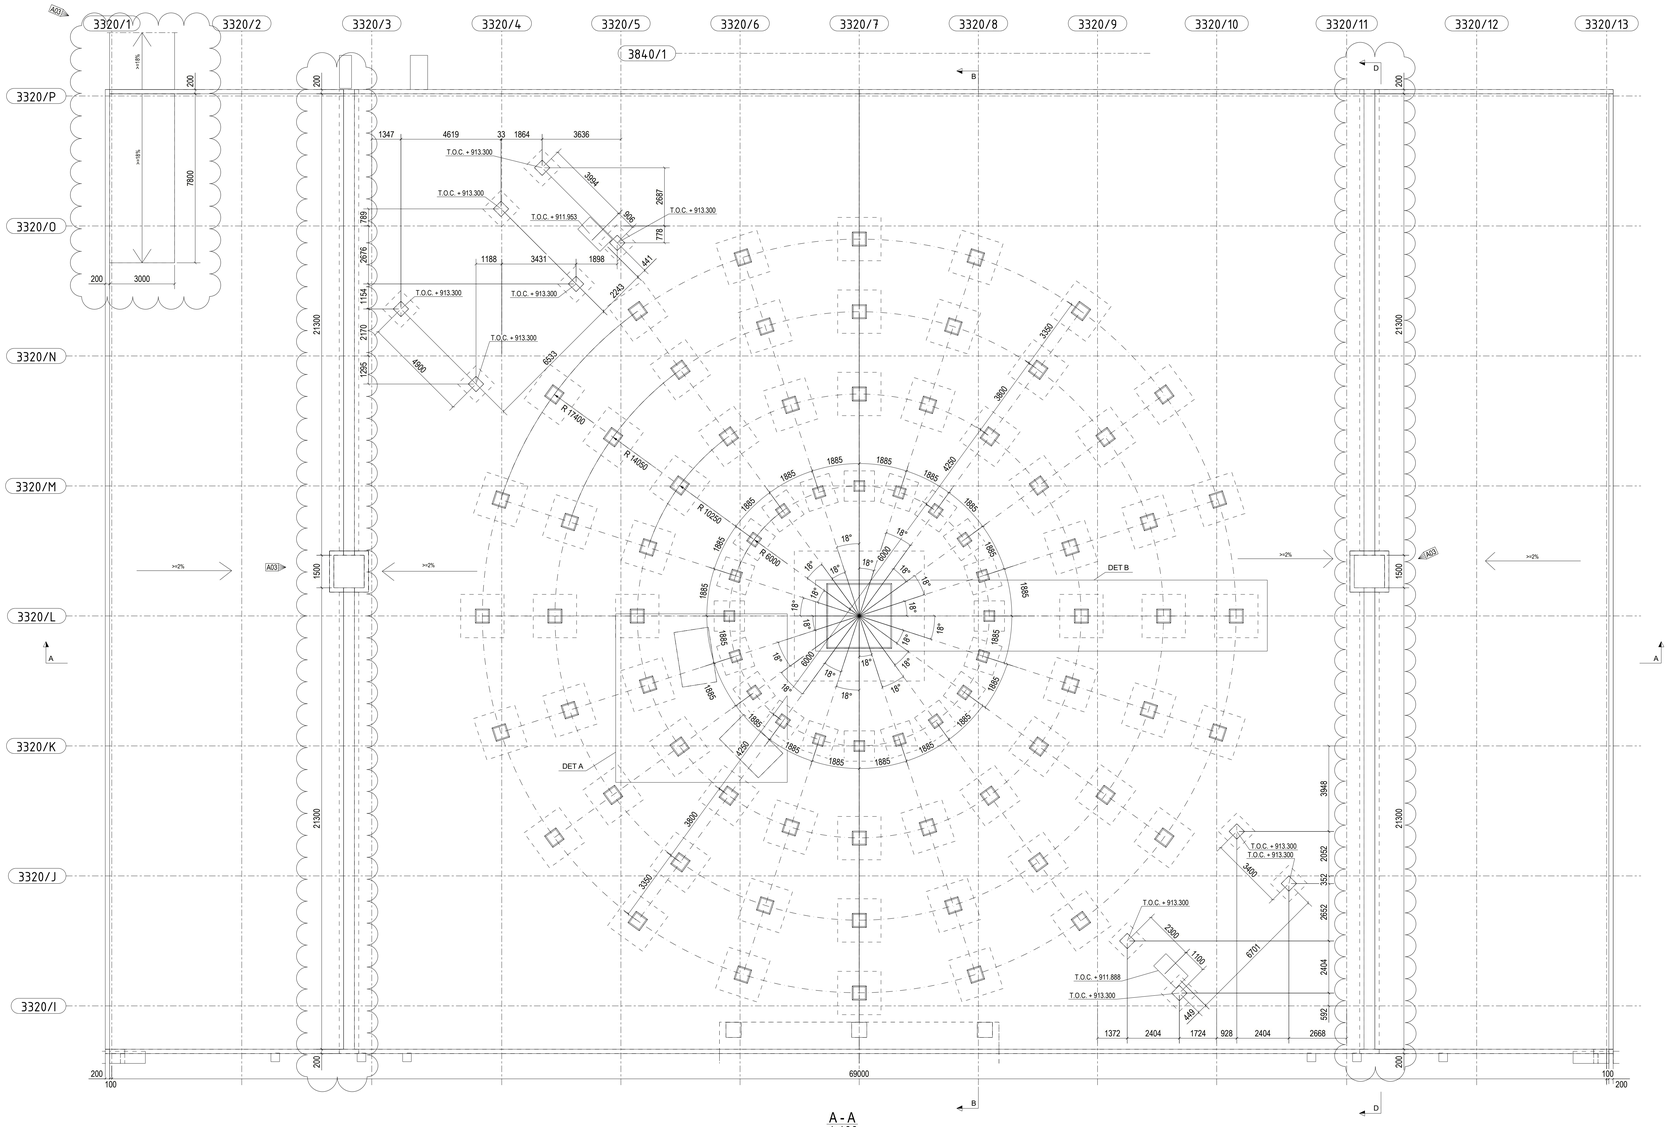

B - B
1:100

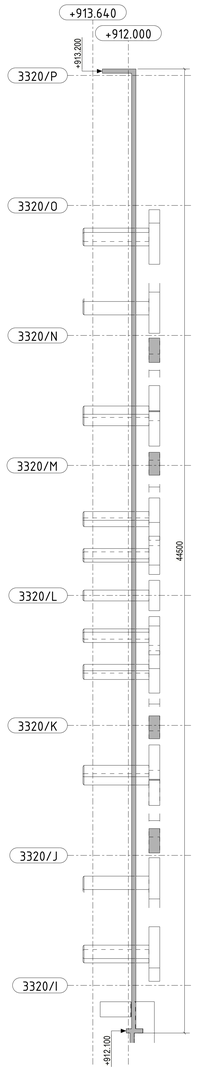

A - A
1:100

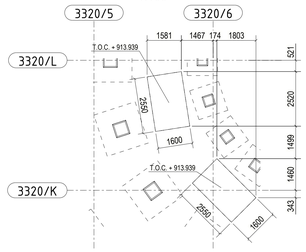


THIS DESIGN IS NOT ISSUED FOR CONSTRUCTION

FINISHED TOP GROUND LEVEL (F.G.L) FOR PROCESS AREA 3320 = RL(+)912.000 m


CONCRETE ELEMENT FLOOR (PRE-CAST SLAB)
CONCRETE FLOOR
CONCRETE FLOOR WITH ACID RESISTANT COATING
CONCRETE WALL

1. ALL DIMENSIONS ARE IN MILLIMETER, ELEVATIONS ARE IN METER UNLESS OTHERWISE STATED
2. CO-ORDINATES ARE SHOWN IN GENERAL ARRENGEMENT DRAWINGS
3. GRATING TYPE (FRP OR NORMAL) IS SPECIFIED IN GENERAL ARRENGEMENT DRAWINGS
4. F.F.L, F.G.L, T.O.C = FINISHED FLOOR LEVEL, FINISHED GROUND LEVEL, TOP OF CONCRETE, T.O.S, B.O.S, B.O.B, = TOP OF STEEL, BOTTOM OF STEEL, BOTTOM OF BASE PLATE
5. BUILDING DIMENSIONS AND HEIGHTS ARE TENTATIVE, SHALL BE FINALIZED DURING DETAIL ENGINEERING SUBJECT TO MINIMUM AS SHOWN.
6. ALL MAINTENANCE FACILITIES, HANDLING PROVISIONS, ACCESS WAYS, PLATFORMS FOR MAINTENANCE SHALL BE PROVIDED DURING DETAIL ENGINEERING WHICH ARE NOT SHOWN ENTIRELY. THIS DRAWING IS TO BE CONSIDERED AS CONCEPTUAL ARRANGEMENT OF THE FACILITIES.


A - A
1:100

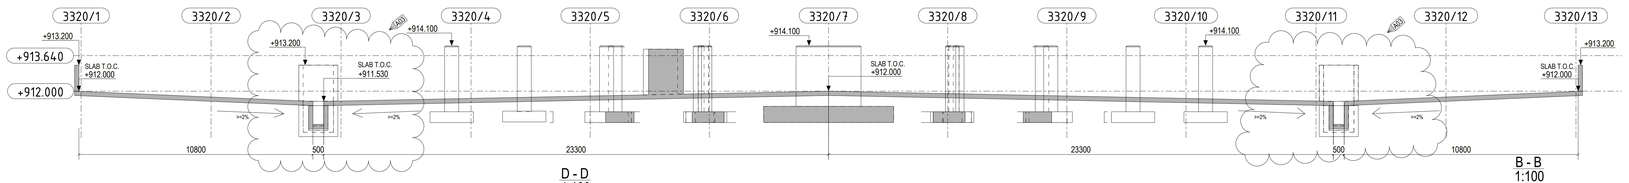


D - D
1:100

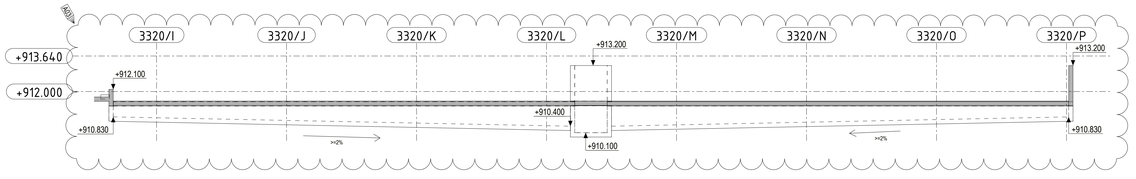

TYPICAL DIMENSIONS AND LEVELS

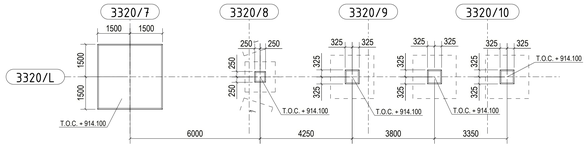

KEYPLAN

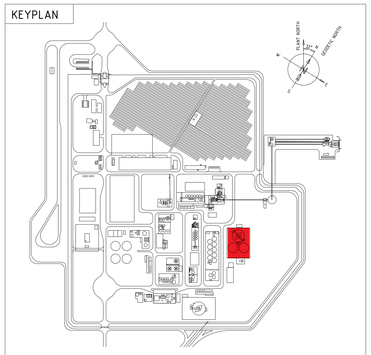

DOCUMENT NUMBER	REFERENCE DOCUMENTS	DOCUMENT NUMBER	REFERENCE DOCUMENTS	REV	DATE	REVISION DESCRIPTION	DRN	CHK	ENG	APP	EMP
MD-216-3320-EG-ST-GAD-1001	PLAN AND SECTIONS										
MD-216-1000-EG-ST-CRT-0001	CIVIL,STRUCTURAL AND ARCHITECTURAL DESIGN BASIS	MD-216-3320-EG-CV-GAD-1002	PLAN AT EL +912.000								
MD-216-3320-EG-ME-GAD-1009	SECTION A-A AND B-B	MD-216-3320-EG-ME-GAD-1010	SECTION C-C AND D-D								
MD-216-3320-EG-ME-GAD-1007	PLAN AT EL. +912.000	MD-216-3320-EG-ME-GAD-1008	PLAN VIEW								

REV	DATE	REVISION DESCRIPTION	DRN	CHK	ENG	APP	EMP
A03	31.03.2020	CHANNELS UPDATED	ElAlv	MaLai	LuPiz	SouCha	
A02	18.02.2020	ISSUED FOR DETAIL DESIGN, FOUNDATIONS UPDATED	Kir Jak	MaLai	LuPiz	SouCha	
A03	18.02.2020	ISSUED FOR DETAIL DESIGN, FOUNDATIONS UPDATED	Kir Jak	MaLai	LuPiz	SouCha	

RESERVED FOR VENDOR LOGO AND DRAWING NUMBER

LARSEN & TOUBRO

This drawing is the property of LARSEN & TOUBRO and must not be passed on to any person or body not authorized by us to receive it nor be copied or otherwise made use either in full or in part by such person or body without our prior permission in writing.

Outotec

The content of these documents are the sole property of Metso Oy. Any rights not expressly granted herein are reserved. Reproduction, transfer or distribution of part or all of the contents in any form without prior written permission of Outotec is prohibited.

MA'ADEN معادن
Saudi Arabian Mining Company شركة معادن السعودية

This document and the information contained herein is Ma'aden proprietary know-how. This document or any part thereof should not be reproduced, stored in a retrieval system or transmitted by any means, electronic or otherwise, or divulged without prior written permission of Ma'aden.

LARSEN & TOUBRO DRAWING NUMBER: 019045_450_C_G_24925_001 — REVISION: 2
OUTOTEC DRAWING NUMBER: 900707_GAU01_ST02_CTA04_33202 — DOCUMENT ID: OU100667776 — REVISION: 2

DRAWN	AmFor	11.12.2019
CHECKED	MaLai	11.12.2019
ENGINEER	LuPiz	11.12.2019
APPROVED	SouCha	11.12.2019
EMPLOYER		
SCALE	1:100	A0

MANSOURAH - MASSARAH GOLD PROJECT
CIVIL WORKS GUIDE DRAWING
3320 LOW GRADE THICKENING
PLAN AT EL. +912.000

DRAWING NUMBER: MD-216-3320-EG-CV-GAD-1002 — REV: A03

Tekla Structures