MD-216-3340-EG-CV-GAD-1001
DRAWING NUMBER
A02
REV

LEVEL +913.000
1:100

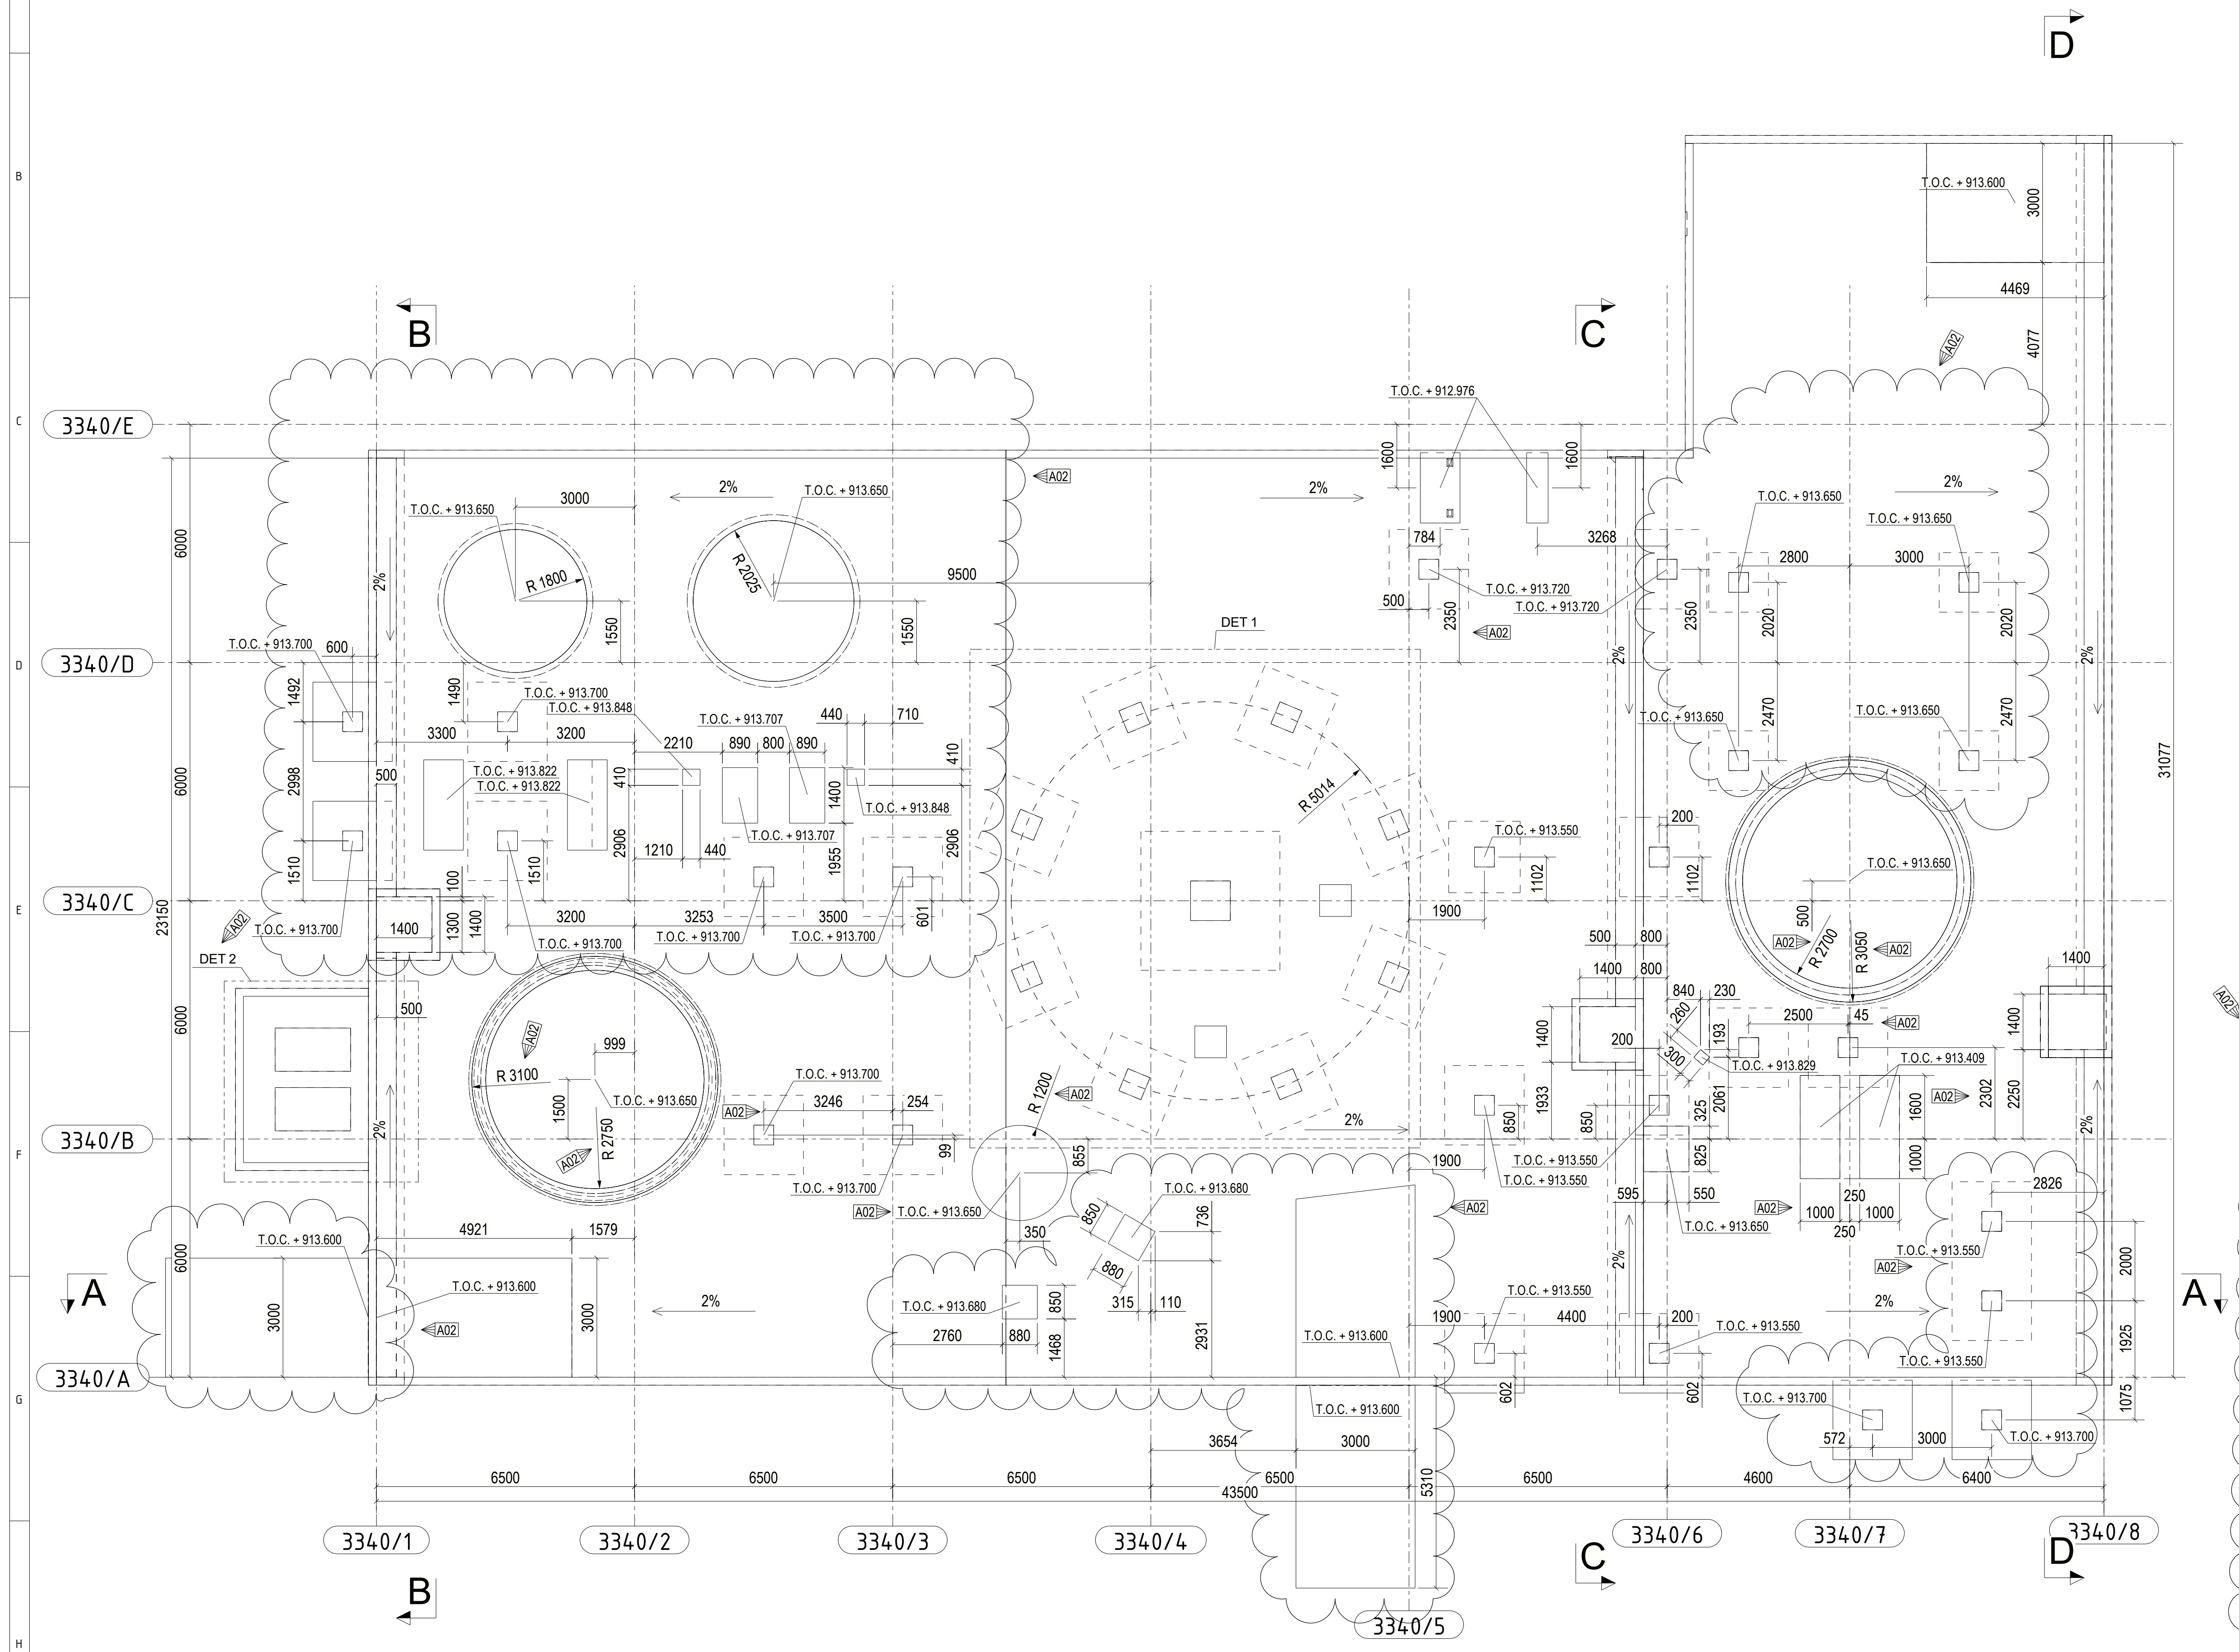
A
B
C
D
3340/E
3340/D
3340/C
3340/B
3340/A
3340/1
3340/2
3340/3
3340/4
3340/5
3340/6
3340/7
3340/8
DET 1
DET 2
A02
2%
T.O.C. + 913.650
T.O.C. + 913.700
T.O.C. + 913.600
T.O.C. + 913.550
R 1800
R 2025
R 3100
R 2750
R 5014
R 2700
6500
4600
6400
43500
23150
31077

DET 1
1:50

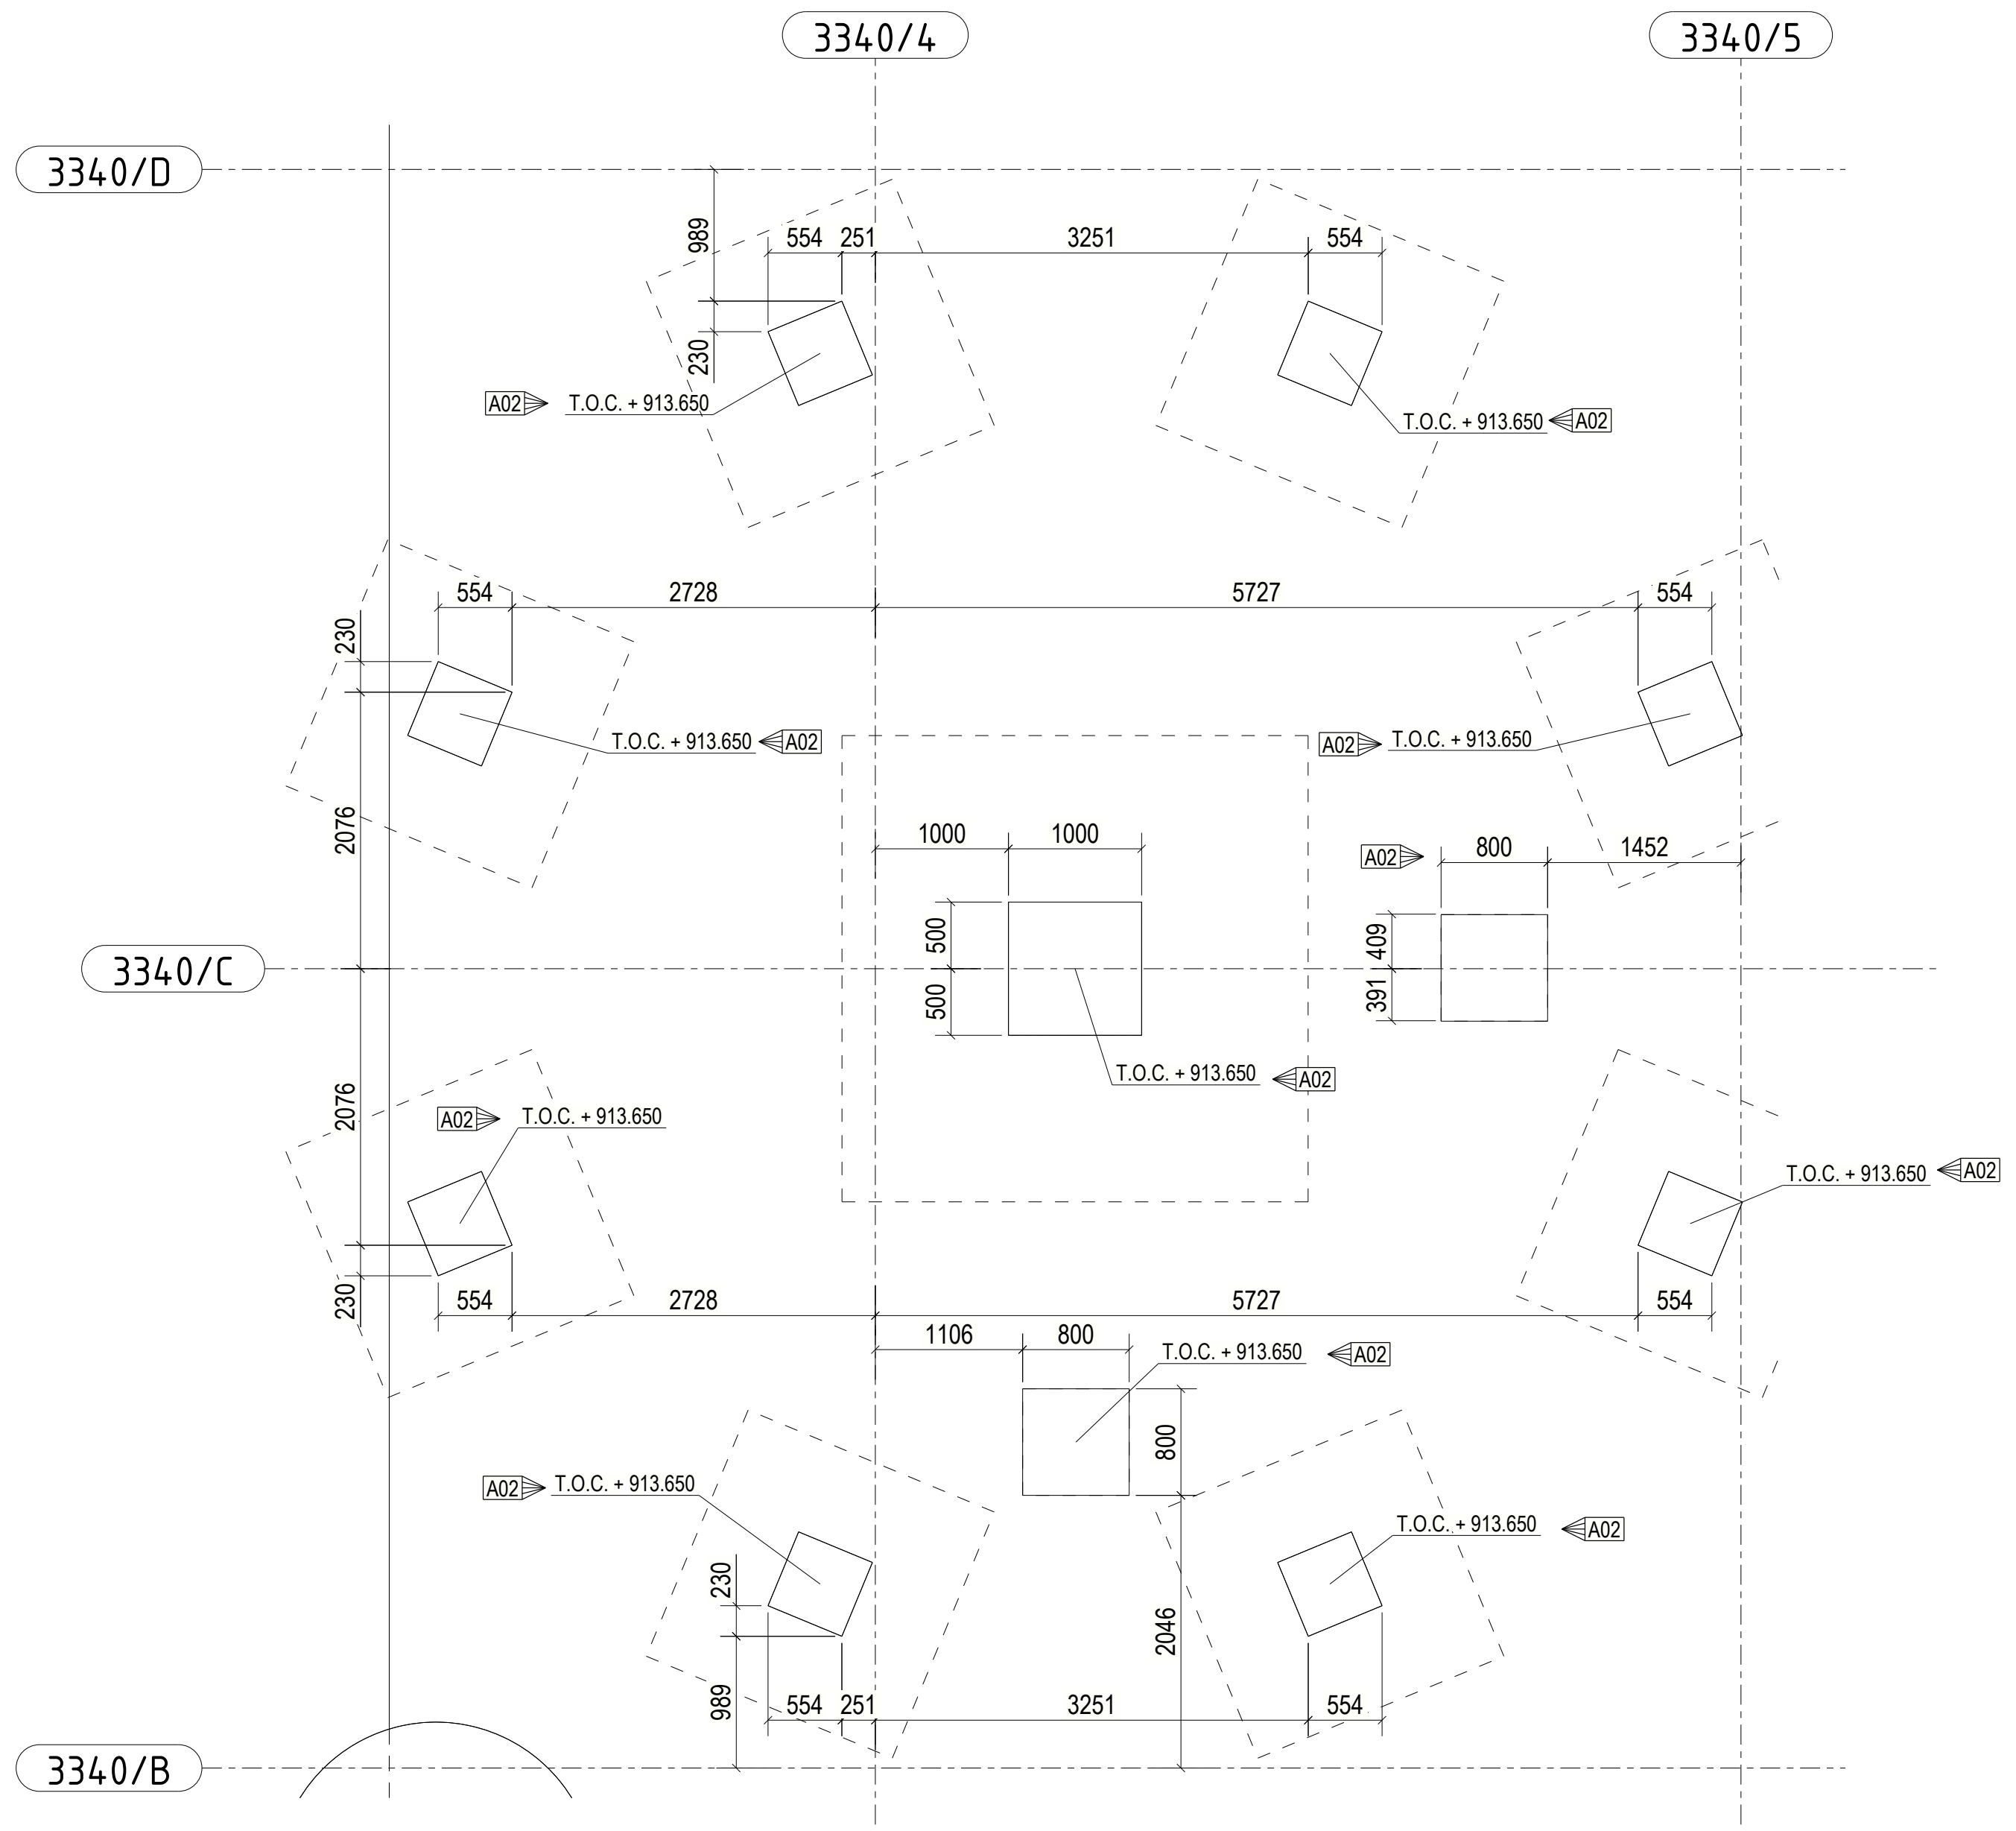
3340/4
3340/5
3340/D
3340/C
3340/B
T.O.C. + 913.650
A02
554
251
3251
2728
5727
1000
800
1452
1106

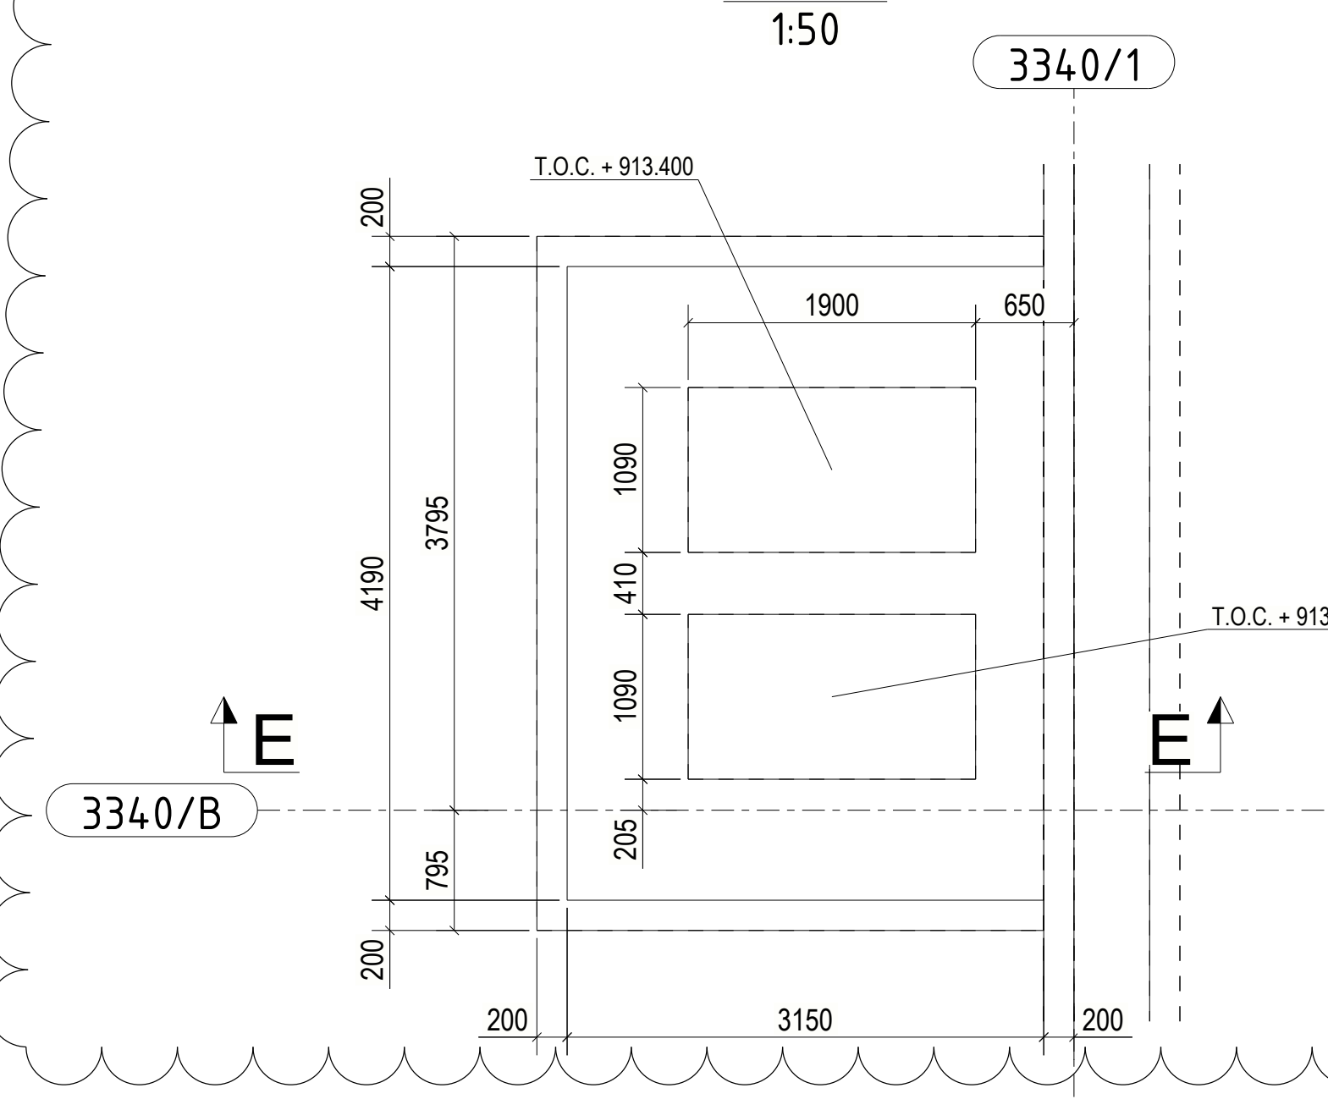

DET 2
1:50

3340/1
3340/B
E
T.O.C. + 913.400
1900
650
4190
3795
3150
200

E – E
1:50

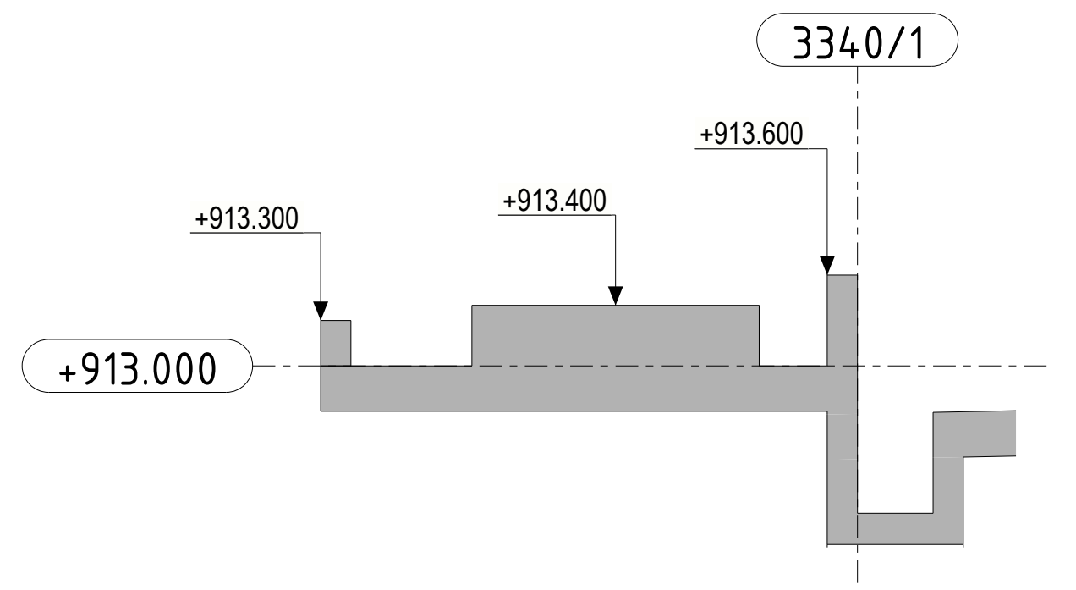
3340/1
+913.300
+913.400
+913.600
+913.000

THIS DESIGN IS NOT ISSUED FOR CONSTRUCTION

FINISHED TOP GROUND LEVEL (F.G.L) FOR PROCESS AREA 3340 = RL(+)913.000 m

▥	CONCRETE ELEMENT FLOOR (PRE-CAST SLAB)
▨	CONCRETE FLOOR
▨ A	CONCRETE FLOOR WITH ACID RESISTANT COATING
▤	CONCRETE WALL

1. ALL DIMENSIONS ARE IN MILLIMETER, ELEVATIONS ARE IN METER UNLESS OTHERWISE STATED
2. CO-ORDINATES ARE SHOWN IN GENERAL ARRENGEMENT DRAWINGS
3. GRATING TYPE (FRP OR NORMAL) IS SPECIFIED IN GENERAL ARRENGEMENT DRAWINGS
4. F.F.L, F.G.L, T.O.C = FINISHED FLOOR LEVEL, FINISHED GROUND LEVEL, TOP OF CONCRETE, T.O.S, B.O.S, B.O.B, = TOP OF STEEL, BOTTOM OF STEEL, BOTTOM OF BASE PLATE
5. BUILDING DIMENSIONS AND HEIGHTS ARE TENTATIVE, SHALL BE FINALIZED DURING DETAIL ENGINEERING SUBJECT TO MINIMUM AS SHOWN.
6. ALL MAINTENANCE FACILITIES, HANDLING PROVISIONS, ACCESS WAYS, PLATFORMS FOR MAINTENANCE SHALL BE PROVIDED DURING DETAIL ENGINEERING WHICH ARE NOT SHOWN ENTIRELY. THIS DRAWING IS TO BE CONSIDERED AS CONCEPTUAL ARRANGEMENT OF THE FACILITIES.

B – B
1:100

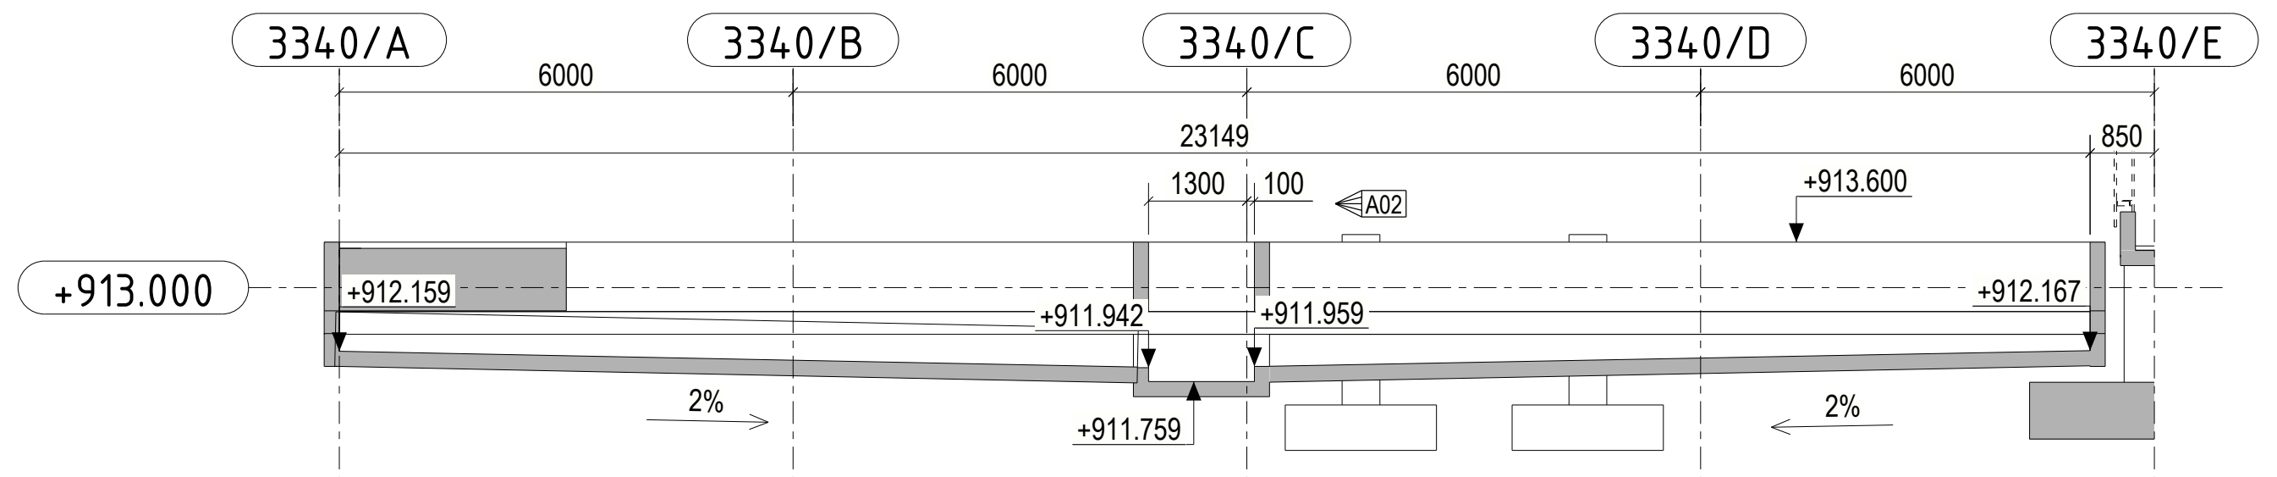
3340/A
3340/B
3340/C
3340/D
3340/E
+913.000
+912.159
+911.942
+911.959
+911.759
+912.167
+913.600
6000
23149
2%

A – A
1:100

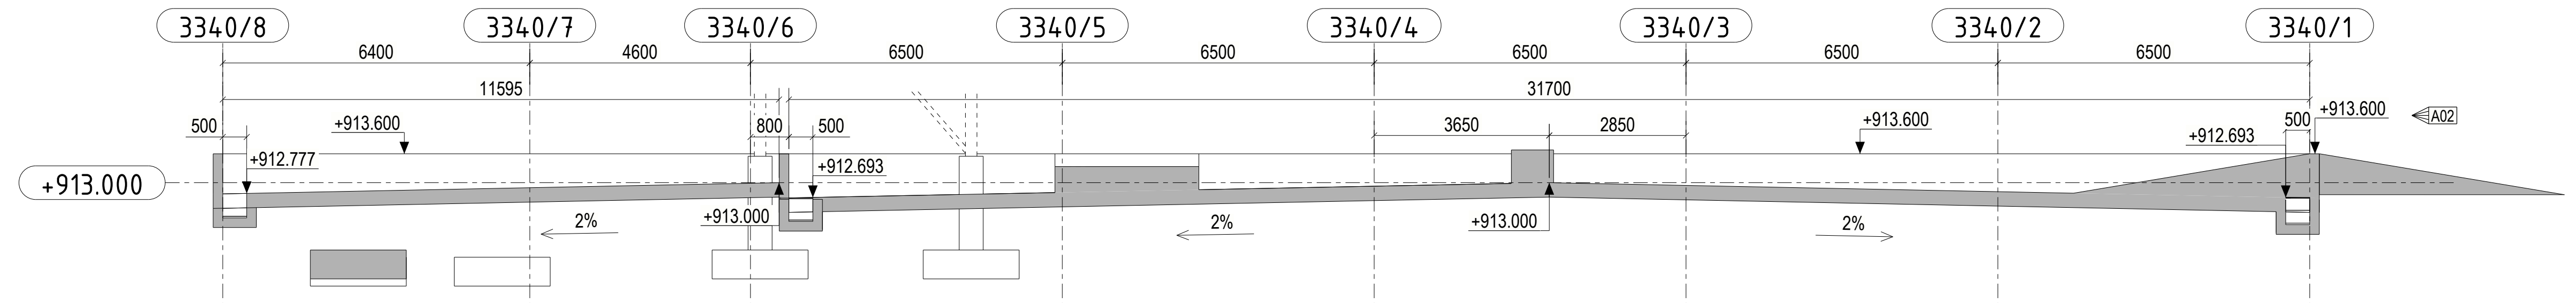
3340/8
3340/7
3340/6
3340/5
3340/4
3340/3
3340/2
3340/1
+913.000
+912.777
+912.693
+913.600
11595
31700
2%

KEYPLAN

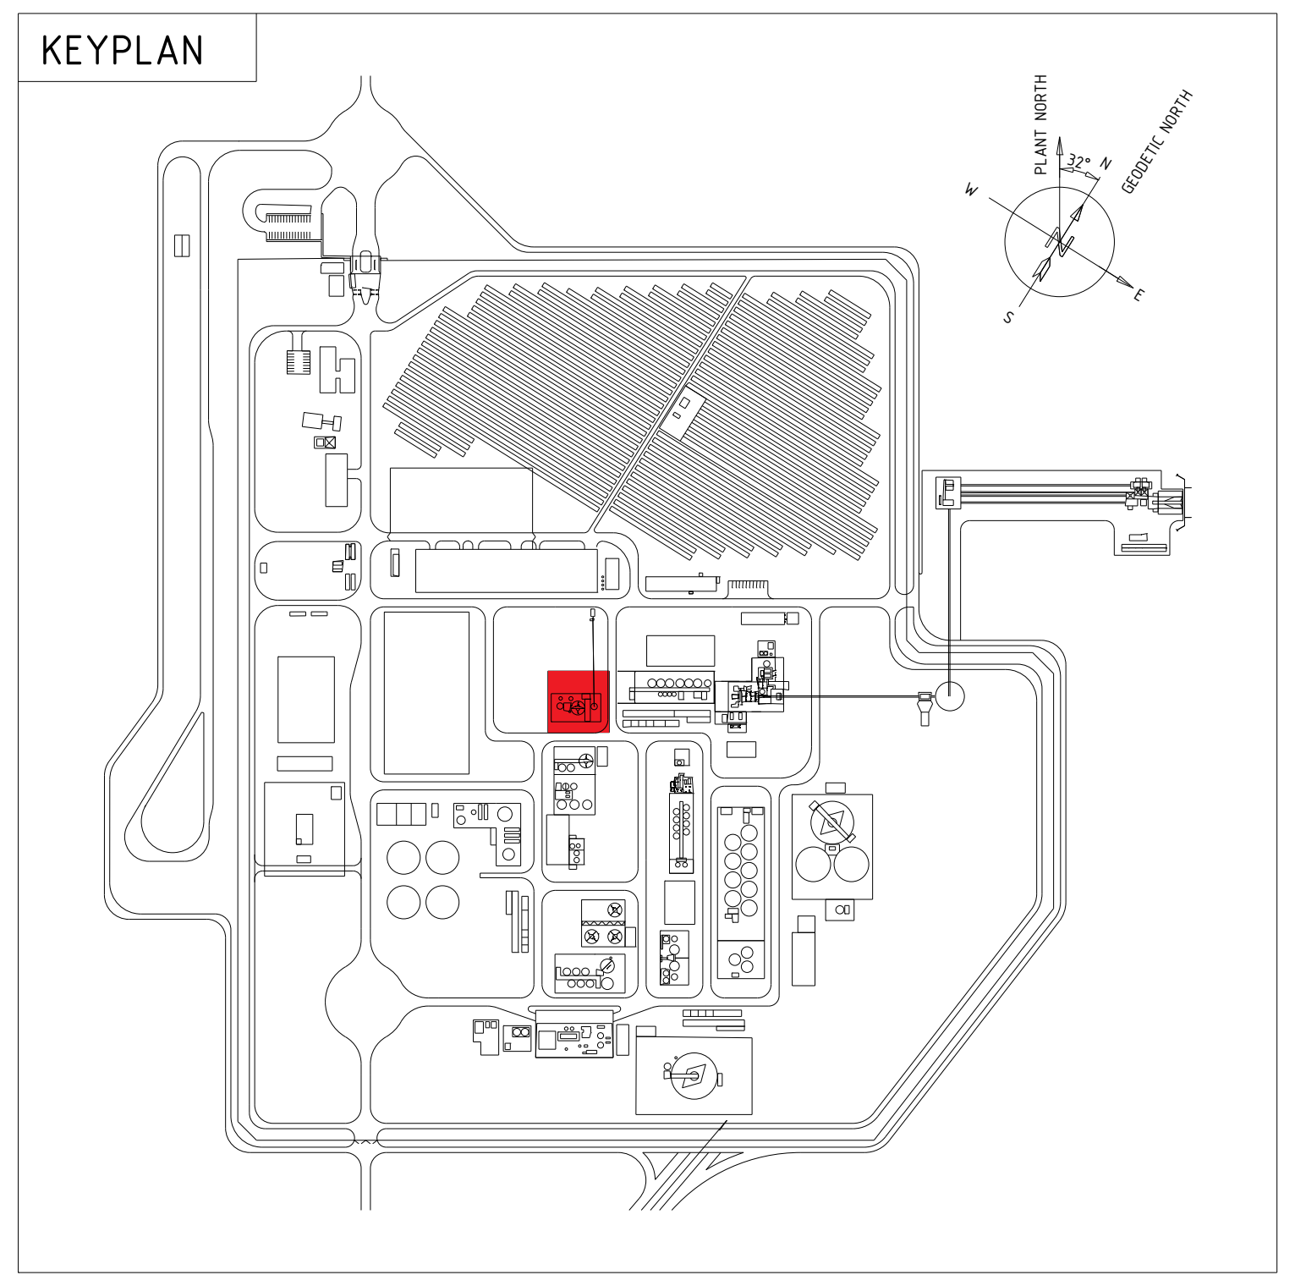
PLANT NORTH
GEODETIC NORTH
32°
N
W

C – C
1:100

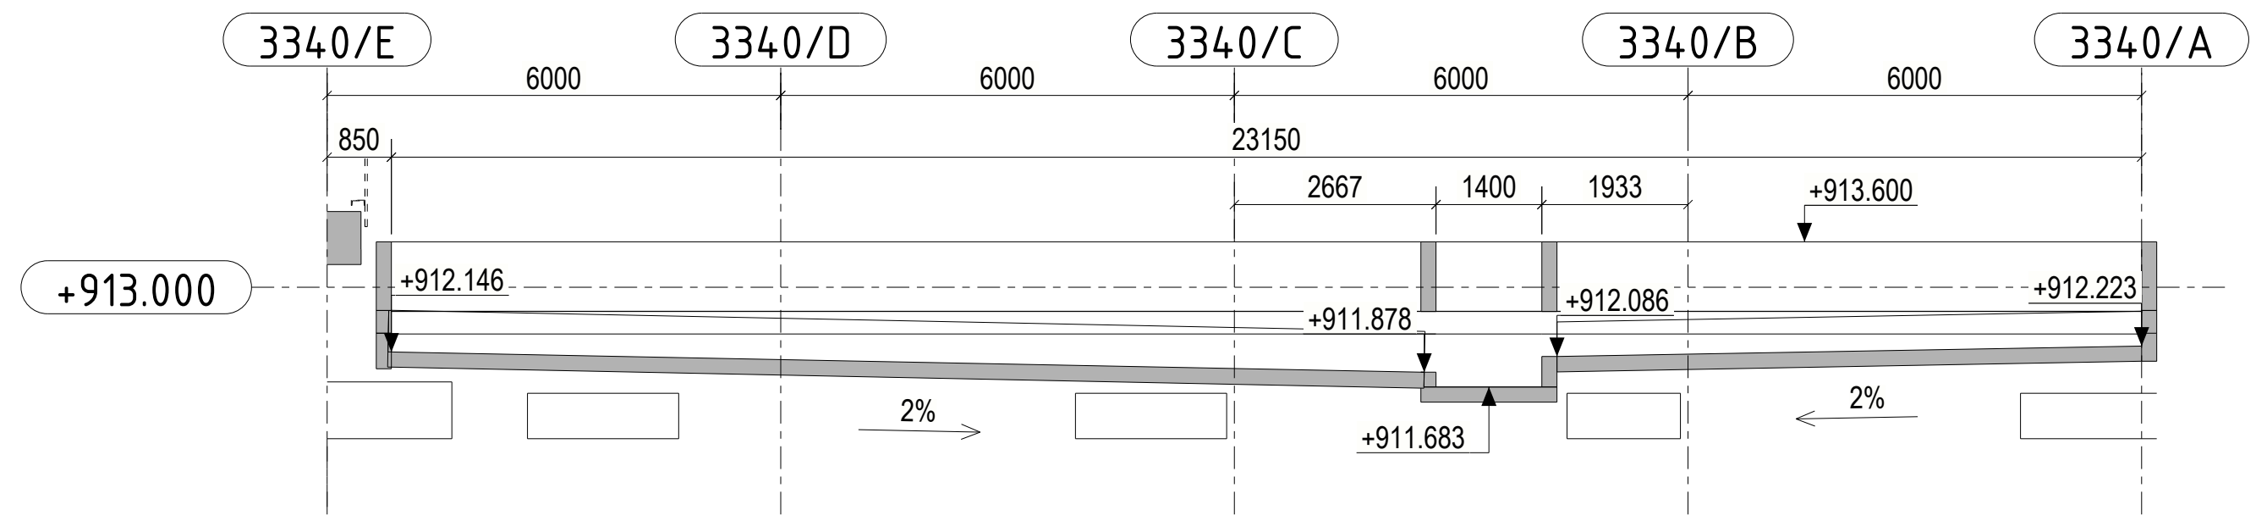
3340/E
3340/D
3340/C
3340/B
3340/A
+913.000
+912.146
+911.878
+912.086
+911.683
+912.223
+913.600
23150
2%

D – D
1:100

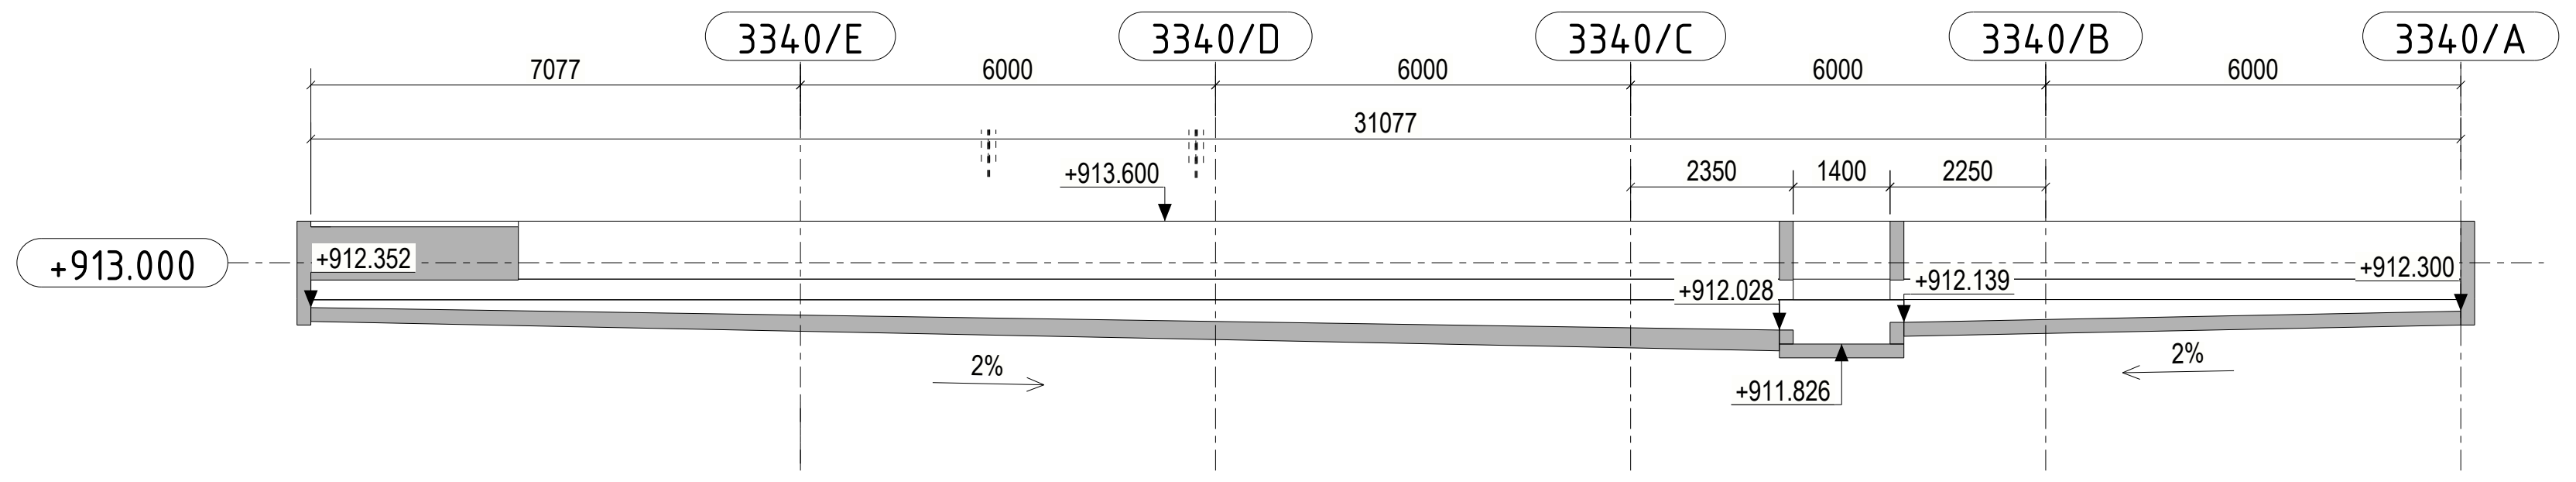
3340/E
3340/D
3340/C
3340/B
3340/A
+913.000
+912.352
+912.028
+912.139
+911.826
+912.300
+913.600
7077
31077
2%

DOCUMENT NUMBER	REFERENCE DOCUMENTS	DOCUMENT NUMBER	REFERENCE DOCUMENTS	REV	DATE	REVISION DESCRIPTION	DRN	CHK	ENG	APP	EMP
MD-216-3340-EG-ME-GAD-1020	SECTION D-D	MD-216-3340-EG-ST-GAD-1001	PLAN VIEW								
MD-216-3340-EG-ME-GAD-1018	SECTION A-A	MD-216-3340-EG-ME-GAD-1019	SECTION C-C								
MD-216-3340-EG-ME-GAD-1016	PLAN VIEW	MD-216-3340-EG-ME-GAD-1017	SECTION A-A								
MD-216-1000-EG-ST-CRT-1001	CIVIL, STRUCTURAL AND ARCHITECTURAL DESIGN BASIS	MD-216-3340-EG-ME-GAD-1015	PLAN AT EL. +913.000								

REV	DATE	REVISION DESCRIPTION	DRN	CHK	ENG	APP	EMP
A02	17.04.2020	ISSUED FOR DETAIL DESIGN. DIMENSIONS AND TOP OF CONCRETE CHANGED. RAMPS ADDED.	EllKiv	MikLai	LuiPiz	SouCha	
A01	20.12.2019	ISSUED FOR APPROVAL.	BabHam	MikLai	LuiPiz	SouCha	

RESERVED FOR VENDOR LOGO AND DRAWING NUMBER

LARSEN & TOUBRO

This drawing is the property of LARSEN & TOUBRO and must not be passed on to any person or body not authorized by us to receive it nor be copied or otherwise made use either in full or in part by such person or body without our prior permission in writing.

Outotec

The content of these documents are the sole property of Outotec Oyj. Any rights not expressly granted herein are reserved. Reproduction, transfer or distribution of part or all of the contents in any form without prior written permission of Outotec is prohibited.

MA'ADEN معادن
Saudi Arabian Mining Company شركة التعدين العربية السعودية

This document and the information contained herein is Ma'aden proprietary know-how. This document or any part thereof should not be reproduced, stored in a retrieval system or transmitted by any means, electronic or otherwise, or divulged without prior written permission of Ma'aden.

LARSEN & TOUBRO DRAWING NUMBER	019045_450_C_G_24912_001	REVISION 1
OUTOTEC DRAWING NUMBER	900707_GAU01_ST01_CTA04_33401	DOCUMENT ID 0U100667763 — REVISION 1

DRAWN	NikJan	20.12.2019
CHECKED	MikLai	20.12.2019
ENGINEER	LuiPiz	20.12.2019
APPROVED	SouCha	20.12.2019
EMPLOYER		
SCALE	1:100	A0

MANSOURAH – MASSARAH GOLD PROJECT
CIVIL WORKS GUIDE DRAWING
CONCENTRATE THICKENING
PLAN AT EL. +913.000

DRAWING NUMBER
MD-216-3340-EG-CV-GAD-1001
REV
A02

Tekla Structures