

DRAWING NUMBER: MD-216-3360-EG-CV-GAD-1001
REV: A02


LEVEL +913.500
1:100

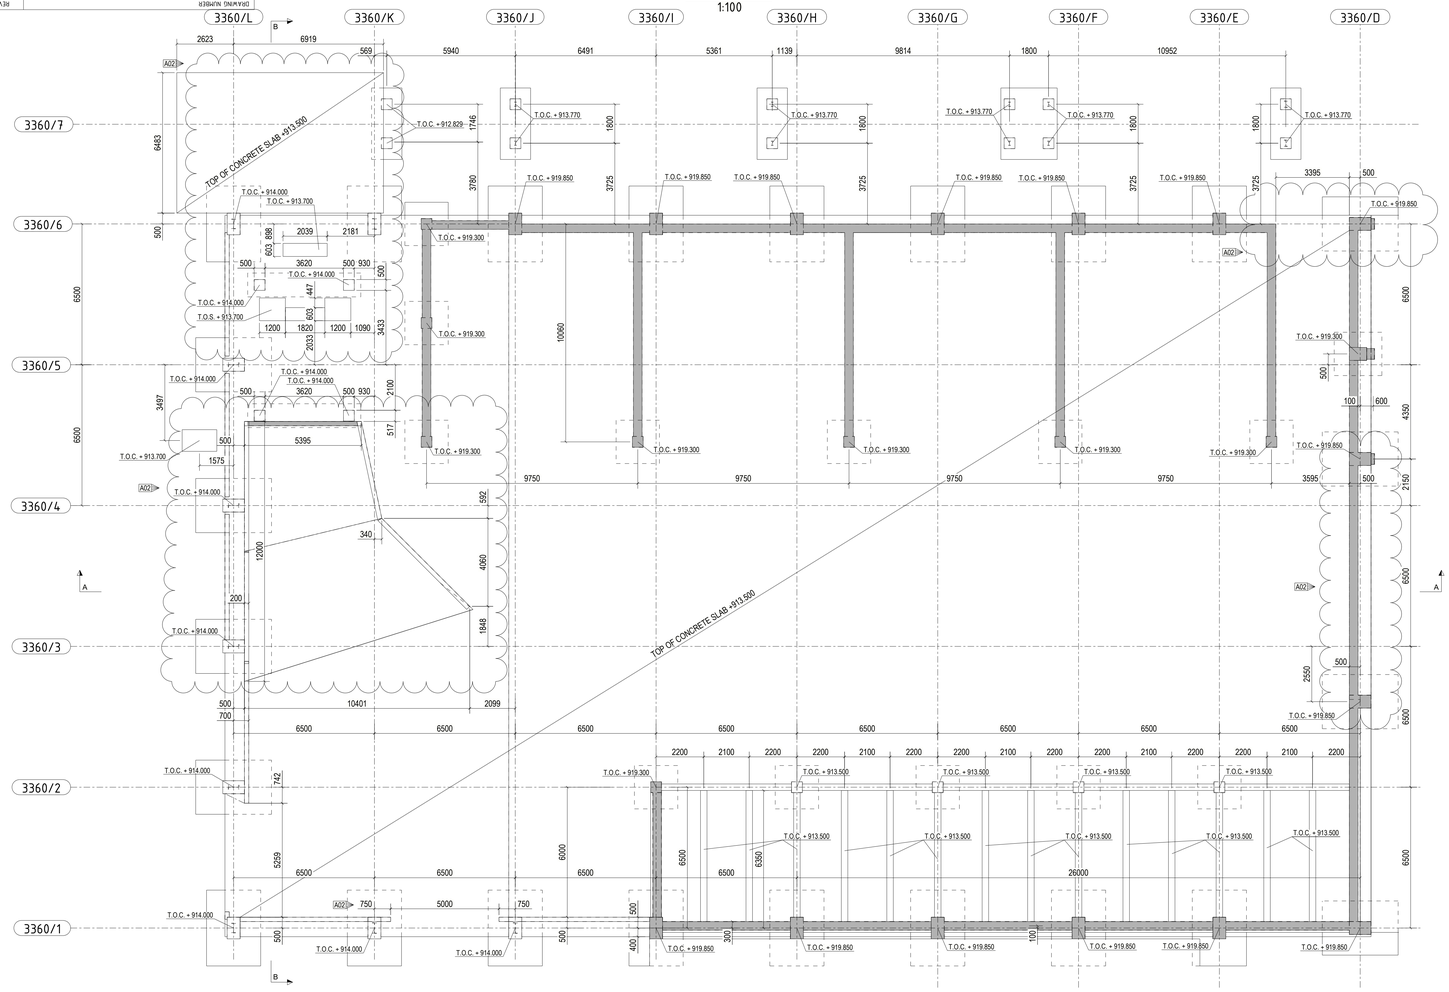


LEVEL +913.000
1:100

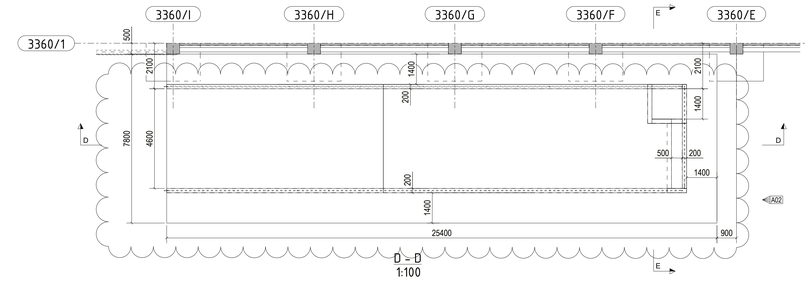


D – D
1:100

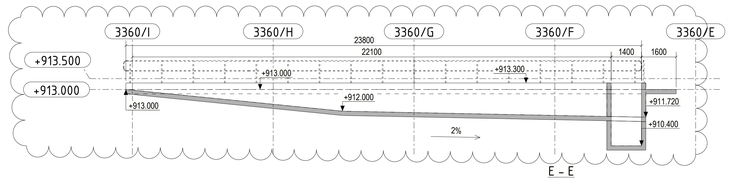


E – E
1:100

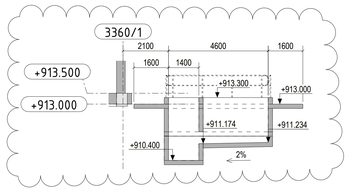


C – C
1:100

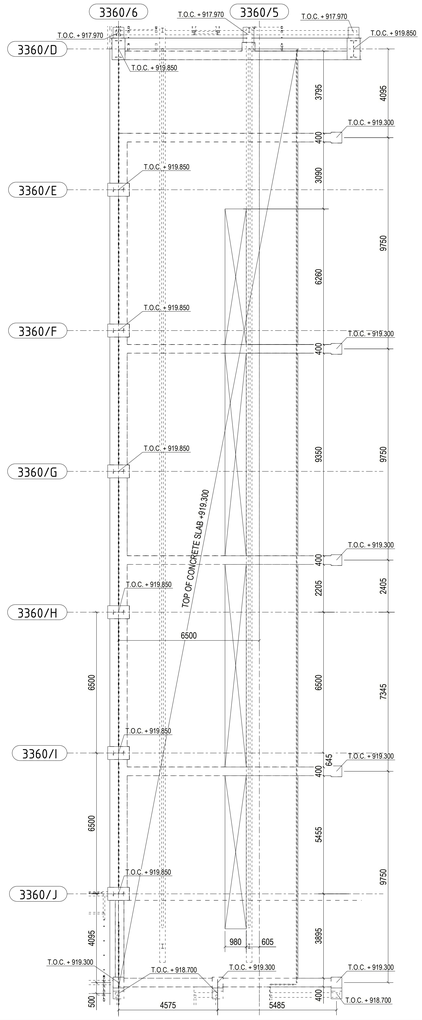

A – A
1:100

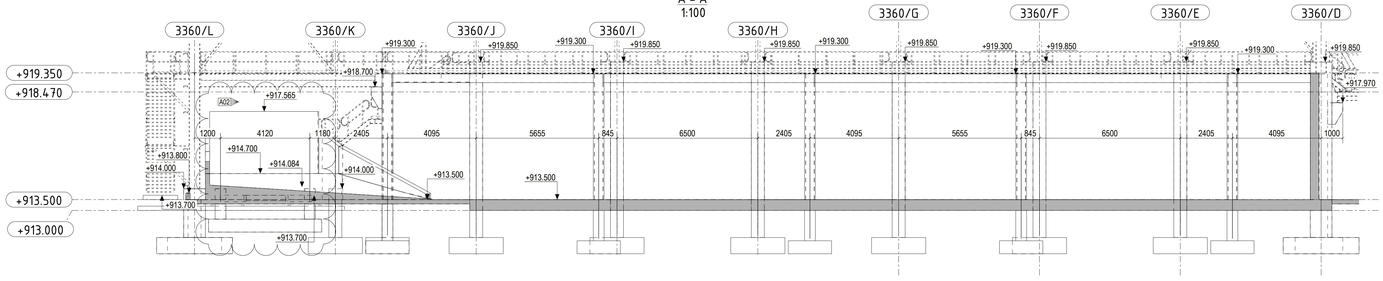

B – B
1:100

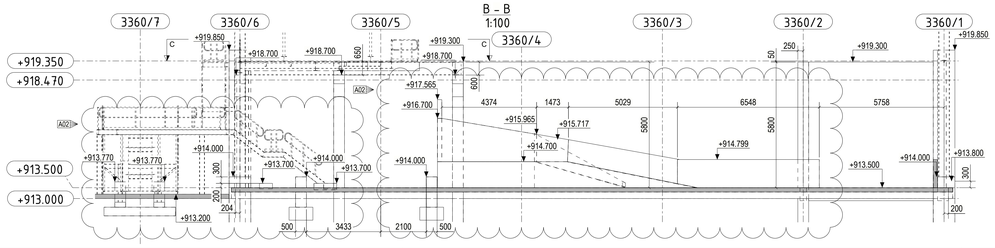


THIS DESIGN IS NOT ISSUED FOR CONSTRUCTION

FINISHED TOP GROUND LEVEL (F.G.L)
FOR PROCESS AREA 3520 = RL(+)913.500 m

CONCRETE ELEMENT FLOOR (PRE-CAST SLAB)
CONCRETE FLOOR
CONCRETE FLOOR WITH ACID RESISTANT COATING
CONCRETE WALL

1. ALL DIMENSIONS ARE IN MILLIMETER, ELEVATIONS ARE IN METER UNLESS OTHERWISE STATED
2. CO-ORDINATES ARE SHOWN IN GENERAL ARRENGEMENT DRAWINGS
3. GRATING TYPE (FRP OR NORMAL) IS SPECIFIED IN GENERAL ARRENGEMENT DRAWINGS
4. F.F.L, F.G.L, T.O.C = FINISHED FLOOR LEVEL, FINISHED GROUND LEVEL, TOP OF CONCRETE, T.O.S, B.O.S, B.O.B, = TOP OF STEEL, BOTTOM OF STEEL, BOTTOM OF BASE PLATE
5. BUILDING DIMENSIONS AND HEIGHTS ARE TENTATIVE, SHALL BE FINALIZED DURING DETAIL ENGINEERING SUBJECT TO MINIMUM AS SHOWN.
6. ALL MAINTENANCE FACILITIES, HANDLING PROVISIONS, ACCESS WAYS, PLATFORMS FOR MAINTENANCE SHALL BE PROVIDED DURING DETAIL ENGINEERING WHICH ARE NOT SHOWN ENTIRELY. THIS DRAWING IS TO BE CONSIDERED AS CONCEPTUAL ARRANGEMENT OF THE FACILITIES.

KEYPLAN

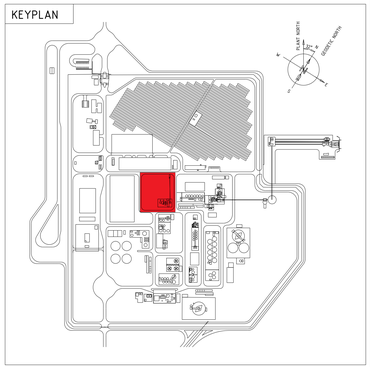

DOCUMENT NUMBER	REFERENCE DOCUMENTS	DOCUMENT NUMBER	REFERENCE DOCUMENTS	REV	DATE	REVISION DESCRIPTION	DRN	CHK	ENG	APP	EMP
MD-216-3350-EG-ME-GAD-1040	SECTION D-D										
MD-216-3350-EG-ME-GAD-1038	SECTION A-A AND B-B	MD-216-3350-EG-ME-GAD-1039	SECTION C-C								
MD-216-3350-EG-ME-GAD-1036	PLAN AT EL. +923.900	MD-216-3350-EG-ME-GAD-1037	PLAN AT EL. +927.330								
MD-216-1000-EG-ST-CRT-1001	CIVIL, STRUCTURAL AND ARCHITECTURAL DESIGN BASIS	MD-216-3350-EG-ME-GAD-1034	PLAN AT EL. +913.500	A02	17.04.2020	ISSUED FOR DETAIL DESIGN, COLUMNS & EQUIP. FOUND. UPDATED, HOLES IN SLAB ADDED	Nikitin	MsLai	LuPiz	SouCha	
				A01	20.12.2019	ISSUED FOR APPROVAL	Babham	MsLai	LuPiz	SouCha	

REVISION DESCRIPTION	DRN	CHK	ENG	APP	EMP

RESERVED FOR VENDOR LOGO AND DRAWING NUMBER

LARSEN & TOUBRO

This drawing is the property of LARSEN & TOUBRO and must not be passed on to any person or body not authorised by us to receive it nor be copied or otherwise made use either in full or in part by such person or body without our prior permission in writing.

Outotec

The content of these documents are the sole property of Outotec Oyj. Any rights not expressly granted herein are reserved. Reproduction, transfer or distribution of part or all of the contents in any form without prior written permission of Outotec is prohibited.

MA'ADEN معادن
Saudi Arabian Mining Company شركة معادن العربية السعودية

This document and the information contained herein is Ma'aden proprietary know-how. This document or any part thereof should not be reproduced, stored in a retrieval system or transmitted by any means, electronic or otherwise, or divulged without prior written permission of Ma'aden.

LARSEN & TOUBRO DRAWING NUMBER	O19045_450_C_G_24920_001	REVISION	1
OUTOTEC DRAWING NUMBER	900707_GAU01_US02_CTA04_33601	DOCUMENT ID	OU100667771
		REVISION	1

DRAWN	Babham	20.12.2019
CHECKED	MsLai	20.12.2019
ENGINEER	LuPiz	20.12.2019
APPROVED	SouCha	20.12.2019
EMPLOYER		
SCALE	1:100	A0

MANSOURAH - MASSARAH GOLD PROJECT
CIVIL WORKS GUIDE DRAWING
CONCENTRATE STORAGE AND REPULP
PLAN AT EL. +913.500

DRAWING NUMBER	REV
MD-216-3360-EG-CV-GAD-1001	A02

Tekla Structures