




DETAIL 1 - SLAB EDGE (SLAB ON GRADE)

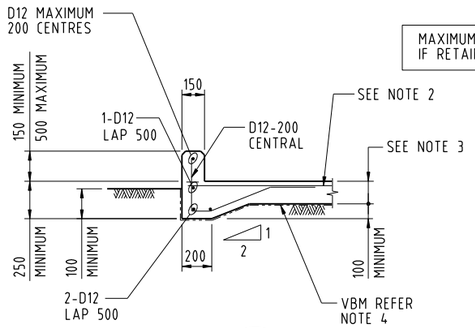


DETAIL 2 - KERB

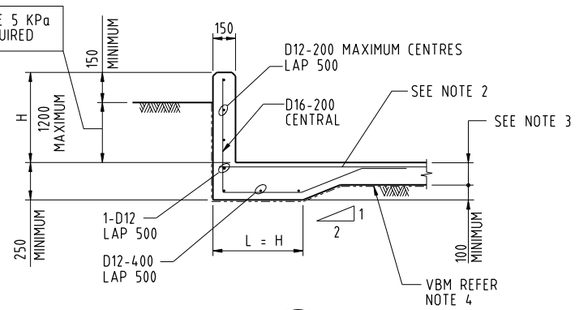


DETAIL 3 - HIGH KERB

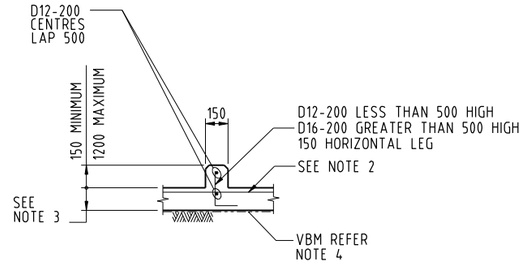


DETAIL 4 - INTERNAL KERB

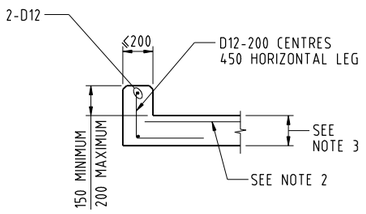

DETAIL 5 - SUSPENDED SLAB KERB

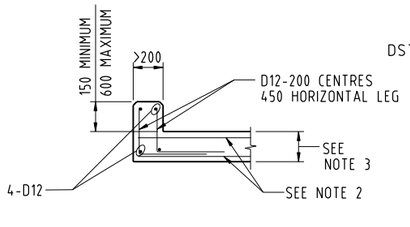


DETAIL 6 - SUSPENDED SLAB KERB

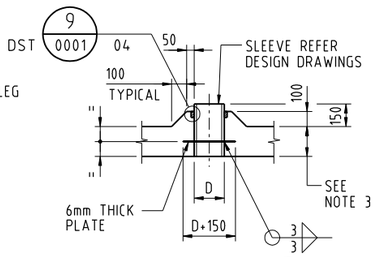


DETAIL 7 - FLOOR PENETRATION

REINFORCEMENT NOT SHOWN FOR CLARITY REFER NOTE 2.

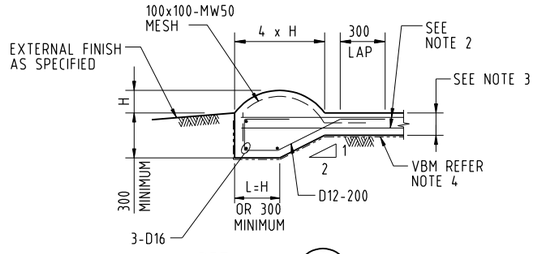


DETAIL 8 - TRAFFICABLE SLAB HUMP

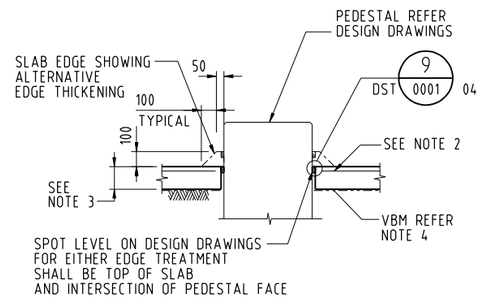


DETAIL 13 - SLAB EDGE AT PEDESTAL


D12-200 IN ROWS OF 600 APART - DRILL AND EPOXY FIX INTO EXISTING CONCRETE - DEPTH TO SUIT EXISTING SLAB THICKNESS

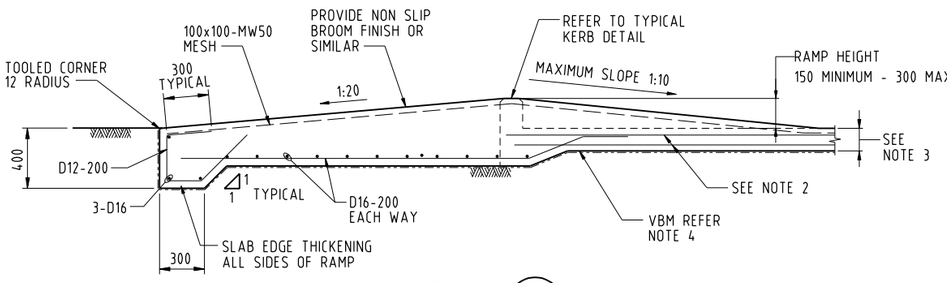


DETAIL 9 - RAMP

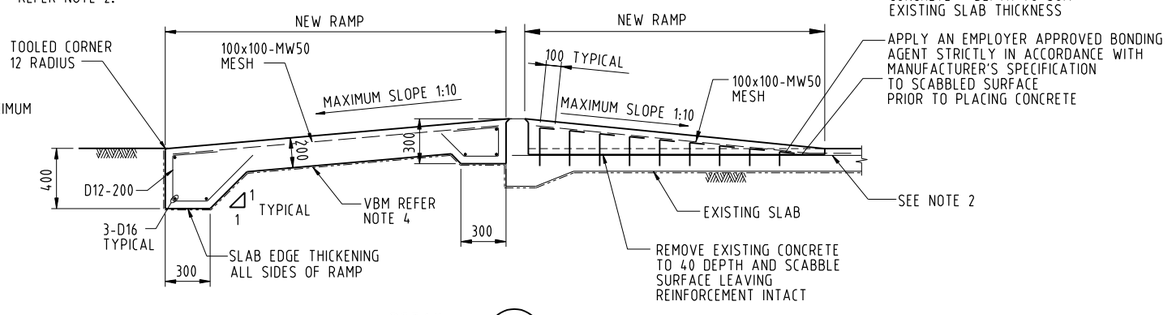

DETAIL 10 - RAMP TO EXISTING SLAB

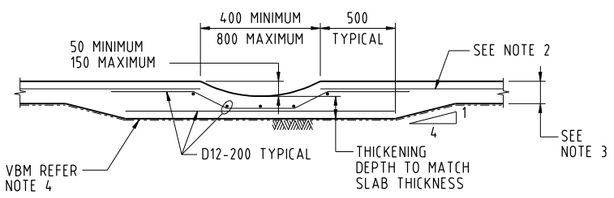

DETAIL 11 - SPOON DRAIN

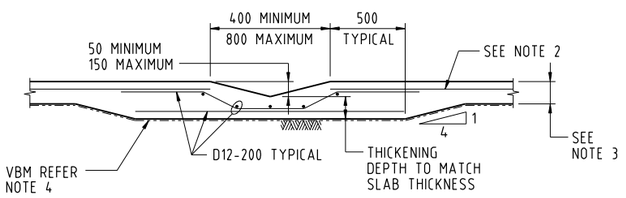

DETAIL 12 - VEE DRAIN

NOTE:
REFERENCES TO DRAWINGS ON DETATILS PRE-FIXED MD-101-SMEM-EG-ST UNLESS NOTED OTHERWISE

NOTES:

1. FOR CONCRETE GENERAL NOTES REFER DRAWING MD-101-SMEM-EG-ST-DST-0001.
2. FOR DETAILS OF REINFORCEMENT REFER TO DESIGN DRAWINGS.
3. FOR SLAB THICKNESS REFER TO DESIGN DRAWINGS.
4. VBM INDICATES POLYTHENE VAPOUR BARRIER MEMBRANE REFER CONCRETE NOTES ON DRAWING MD-101-SMEM-EG-ST-DST-0001.

DOCUMENT NUMBER	REFERENCE DOCUMENTS	REV	DATE	REVISION DESCRIPTION	DRN	CHK	ENG	APP	MD

This drawing and all the information contained herein it is the proprietary property of Ma'aden and is subject to confidentiality restrictions between Ma'aden and the recipent. The information contained herein is provided for a limited purpose and must be returned on request. Ma'aden makes no respresentations or warranties that this information is complete or fit for any particular purpose. Neither this drawing nor any information concerning it may be copied, exhibited or furnished to others. Nor may photographs be taken of any article fabricated or assembled from this drawing, without Ma'aden prior written consent.

REV C01 PREPARED FOR MA'ADEN BY HATCH ASSOCIATES H332701-0000-35-041-0002_C

MA'ADEN معادن Saudi Arabian Mining Company

DRAWN	J BADAL	01.03.11
CHECKED	J EDWARDS	31.03.11
ENGINEER	D KIRKWOOD	31.03.11
APPROVED	R COVELLA	11.05.11
MA'ADEN		

SCALE NTS | A1

MA'ADEN ENGINEERING MANUAL
ALL AREAS
STRUCTURAL STANDARDS
CONCRETE DETAILS SHEET 1

DRAWING NUMBER MD-101-SMEM-EG-ST-DST-0002 | REV C01

MA'ADEN PHOSPHATE PROJECT-A1 BORDER-REV A02

$FILE$ $TIME$ $DATE$