




DETAIL 1 - IJ - ISOLATION JOINT

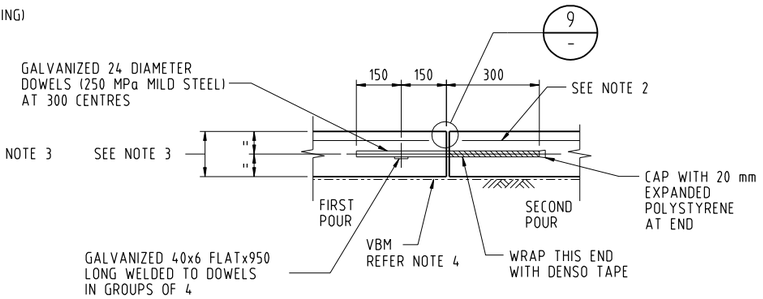


DETAIL 2 - DIJ - DOWELLED ISOLATION JOINT

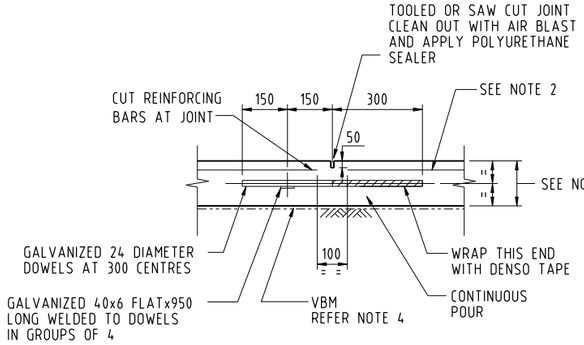


DETAIL 3 - DSJ - DOWELLED SHRINKAGE JOINT

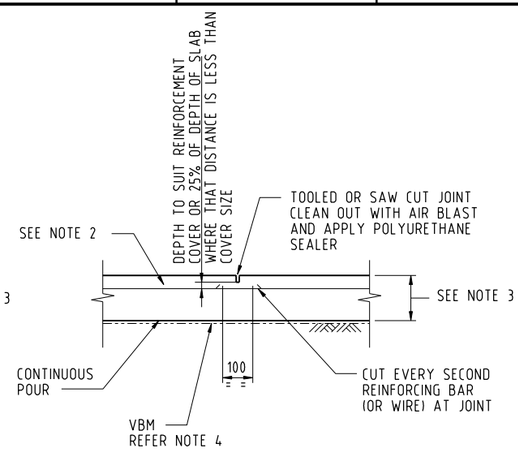


DETAIL 4 - SJ - SHRINKAGE JOINT

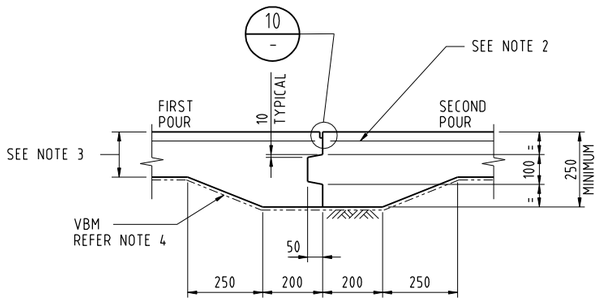


DETAIL 5 - KCJ - KEYED CONSTRUCTION JOINT

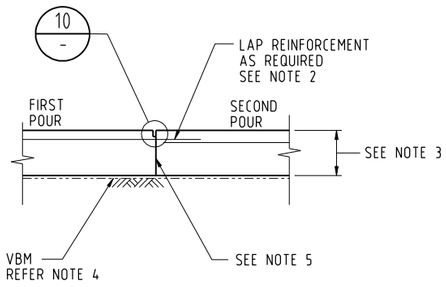


DETAIL 6 - CJ - CONSTRUCTION JOINT

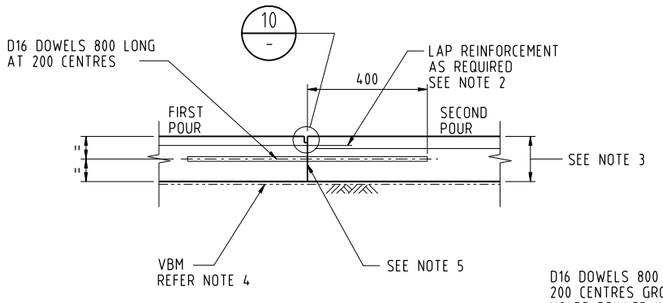

DETAIL 7 - DCJ - DOWELLED CONSTRUCTION JOINT

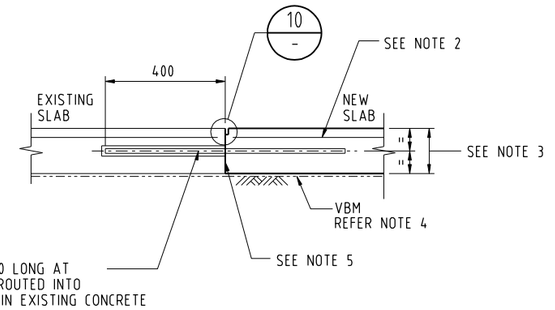


DETAIL 8 - DCJ - DOWELLED CONSTRUCTION JOINT
BETWEEN NEW AND EXISTING GROUND SLABS

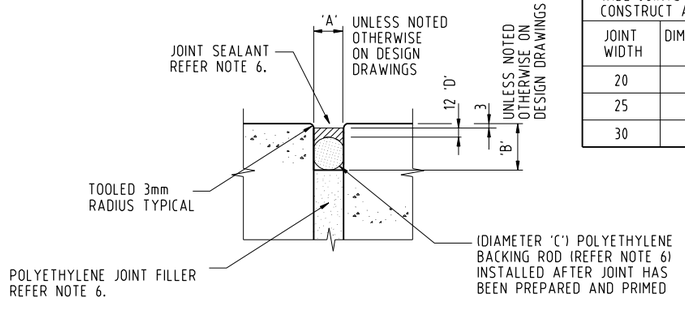

DETAIL 9

FOR 20,25 OR 30 WIDE JOINTS CONSTRUCT AS BELOW				
JOINT WIDTH	DIMENSION A	DIMENSION B	DIAMETER C	DIMENSION D
20	20	40	25	12
25	25	50	30	15
30	30	60	40	18

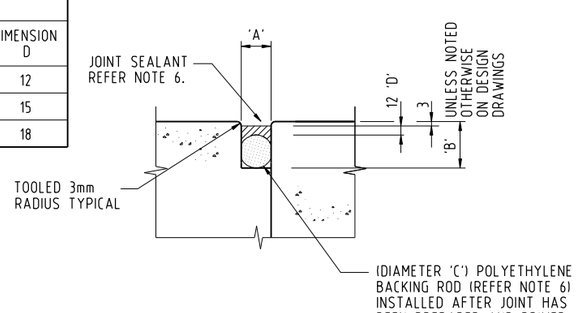

DETAIL 10

NOTES:

1. FOR CONCRETE GENERAL NOTES REFER DRAWING MD-101-SMEM-EG-ST-DST-0001.
2. FOR DETAILS OF REINFORCEMENT REFER DESIGN DRAWINGS.
3. FOR SLAB THICKNESS REFER DESIGN DRAWINGS.
4. VBM INDICATES POLYTHENE VAPOUR BARRIER MEMBRANE REFER CONCRETE NOTES ON DRAWING MD-101-SMEM-EG-ST-DST-0001.
5. CONTACT SURFACE AT ALL CONSTRUCTION JOINTS SHALL BE SCABBLED OR WATER JET BLASTED TO EXPOSE A CLEAN ROUGH SURFACE WITH COARSE AGGREGATE PROTRUDING 5mm MIN BUT FIRMLY FIXED IN THE CONCRETE MATRIX. APPLY AN EMPLOYER APPROVED WET TO DRY EPOXY COATING BONDING AGENT TO CONTACT FACE BY AIRLESS SPRAY IMMEDIATELY PRIOR TO POURING NEW CONCRETE.
6. ALL CONCRETE JOINTING MATERIAL SHALL BE APPROVED BY THE EMPLOYER, PRIOR TO USE, AND INSTALLED / APPLIED STRICTLY IN ACCORDANCE WITH THE MANUFACTURER'S RECOMMENDATIONS.

DOCUMENT NUMBER	REFERENCE DOCUMENTS	REV	DATE	REVISION DESCRIPTION	DRN	CHK	ENG	APP	MD

This drawing and all the information contained herein it is the proprietary property of Ma'aden and is subject to confidentiality restrictions between Ma'aden and the recipent. The information contained herein is provided for a limited purpose and must be returned on request. Ma'aden makes no respresentations or warranties that this information is complete or fit for any particular purpose. Neither this drawing nor any information concerning it may be copied, exhibited or furnished to others. Nor may photographs be taken of any article fabricated or assembled from this drawing, without Ma'aden prior written consent.

REV C01 PREPARED FOR MA'ADEN
BY HATCH ASSOCIATES
H332701-0000-35-041-0004

MA'ADEN معادن
Saudi Arabian Mining Company

DRAWN	J BADAL	01.03.11
CHECKED	J EDWARDS	31.03.11
ENGINEER	D KIRKWOOD	31.03.11
APPROVED	R COVELLA	11.05.11
MA'ADEN		
SCALE NTS	A1	

MA'ADEN ENGINEERING MANUAL
ALL AREAS
STRUCTURAL STANDARDS
CONCRETE DETAILS SHEET 3

DRAWING NUMBER MD-101-SMEM-EG-ST-DST-0004 REV C01

$FILE$ $TIME$ $DATE$