

MA'ADEN PHOSPHATE PROJECT-A1 BORDER-REV A02

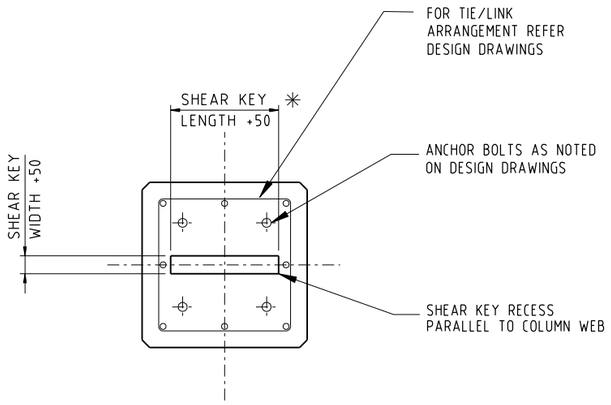


SINGLE SHEAR KEY RECESS TYPE R1

✳ MAXIMUM PERMISSABLE LENGTH WITH RESPECT TO THE COLUMN DIMENSIONS TO BE DETERMINED BY DESIGNER

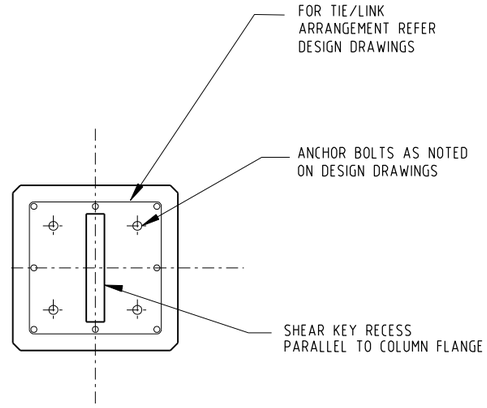


SINGLE SHEAR KEY RECESS TYPE R2

FOR SHEAR KEY DIMENSIONS REFER TYPE R1

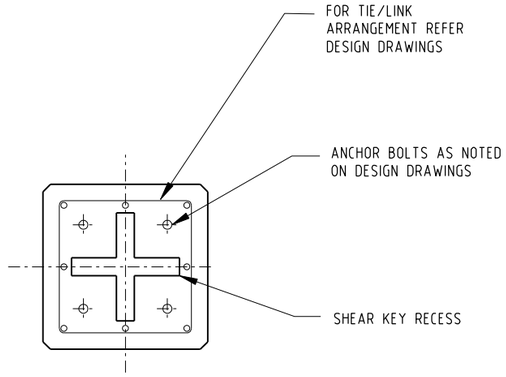

DOUBLE SHEAR KEY RECESS TYPE R3

FOR SHEAR KEY DIMENSIONS REFER TYPE R1

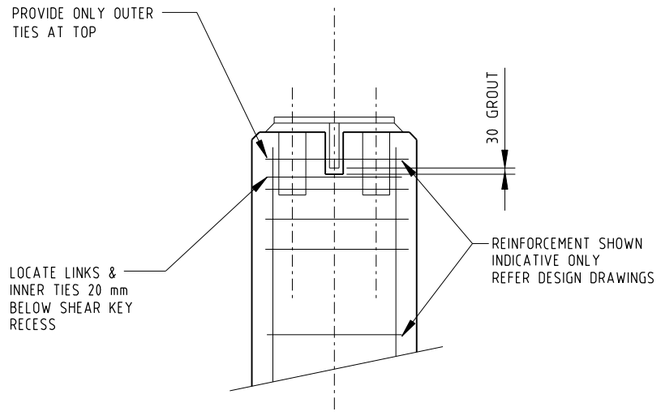

TYPICAL SECTION THROUGH PEDESTAL SHEAR KEY RECESS

NOTES:

1. FOR CONCRETE GENERAL NOTES REFER DRG MD-101-SMEM-EG-ST-DST-0001.
2. FOR DETAILS OF REINFORCEMENT REFER DESIGN DRAWINGS.
3. FOR SHEAR ORIENTATION REFER DESIGN DRAWINGS.

DOCUMENT NUMBER	REFERENCE DOCUMENTS	REV	DATE	REVISION DESCRIPTION	DRN	CHK	ENG	APP	MD

This drawing and all the information contained herein it is the proprietary property of Ma'aden and is subject to confidentiality restrictions between Ma'aden and the recipent. The information contained herein is provided for a limited purpose and must be returned on request. Ma'aden makes no respresentations or warranties that this information is complete or fit for any particular purpose. Neither this drawing nor any information concerning it may be copied, exhibited or furnished to others. Nor may photographs be taken of any article fabricated or assembled from this drawing, without Ma'aden prior written consent.

REV C01 PREPARED FOR MA'ADEN BY HATCH ASSOCIATES H332701-0000-35-041-0008_C

MA'ADEN معادن Saudi Arabian Mining Company

DRAWN	J BADAL	01.03.11
CHECKED	J EDWARDS	31.03.11
ENGINEER	D KIRKWOOD	31.03.11
APPROVED	R COVELLA	11.05.11
MA'ADEN		
SCALE NTS		A1

MA'ADEN ENGINEERING MANUAL
ALL AREAS
STRUCTURAL STANDARDS
SHEAR KEY TO PEDESTAL DETAILS

DRAWING NUMBER MD-101-SMEM-EG-ST-DST-0008 REV C01

$FILE$ $TIME$ $DATE$