
WEB SIDE PLATES

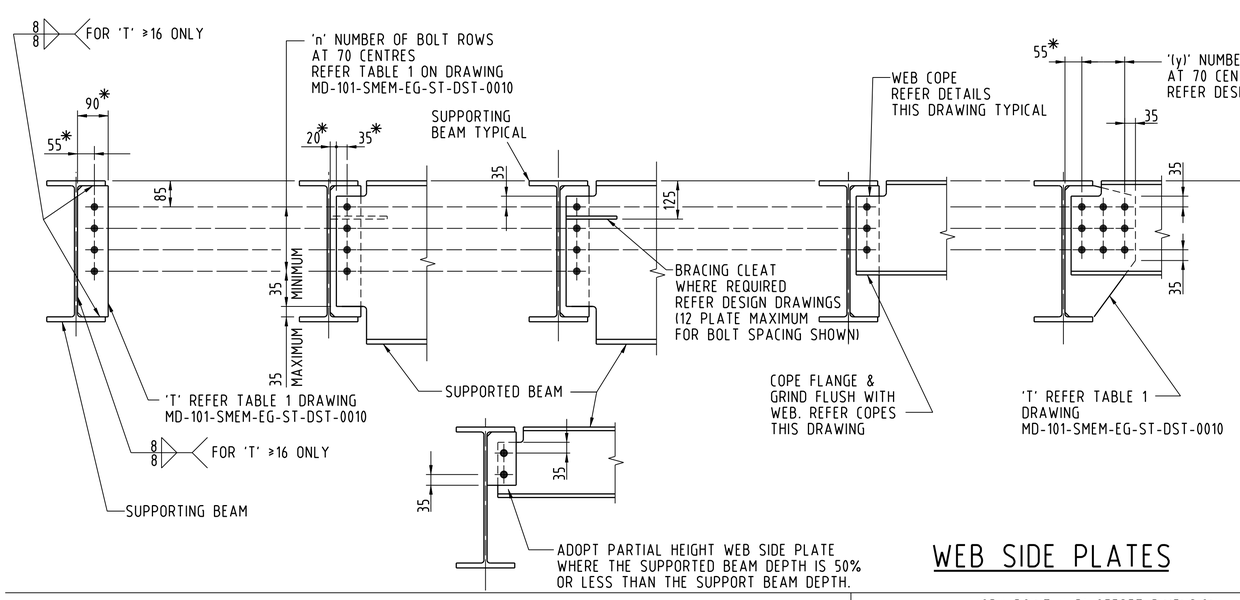


TYPICAL CONNECTION FOR C6 & W6

(TABLE 1 ON DRAWING MD-101-SMEM-EG-ST-0010)


TYPICAL CONNECTION FOR C7, C8 & W8

(TABLE 1 ON DRAWING MD-101-SMEM-EG-ST-0010)


TYPICAL CONNECTION FOR BEAMS NOT AT RIGHT ANGLES

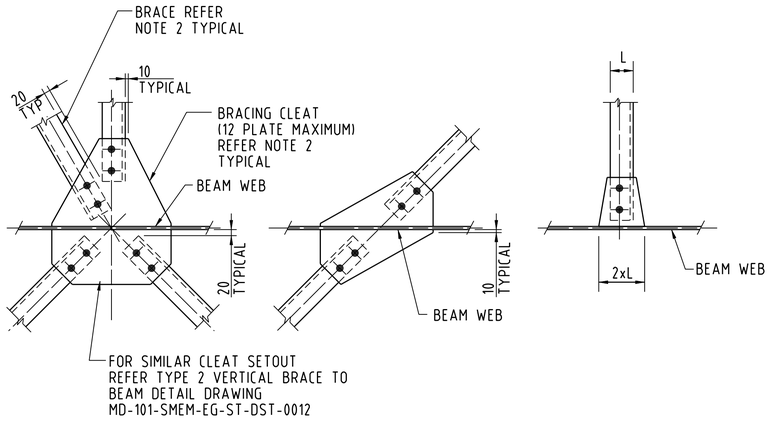


TYPICAL HORIZONTAL BRACING DETAILS

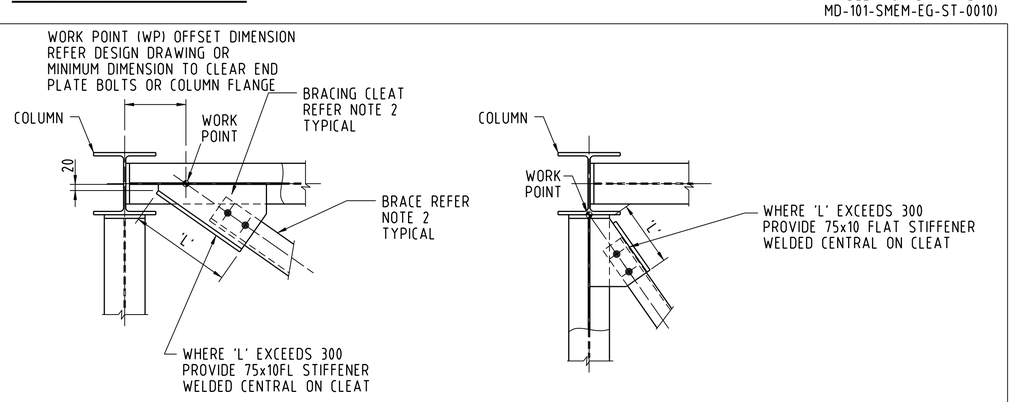


TYPICAL HORIZONTAL BRACING AT BEAM TO COLUMN INTERSECTION

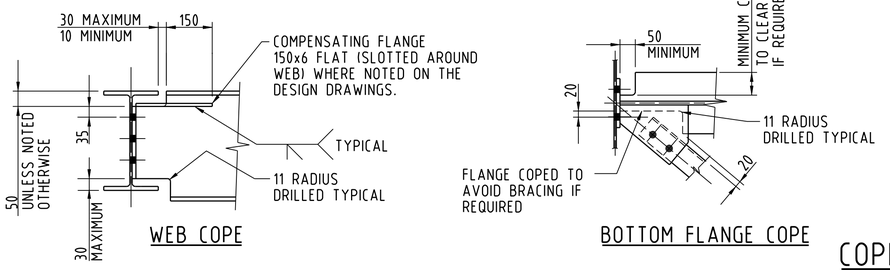


WEB COPE

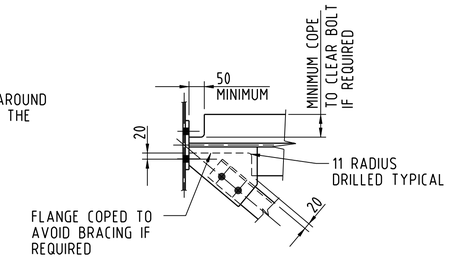


BOTTOM FLANGE COPE

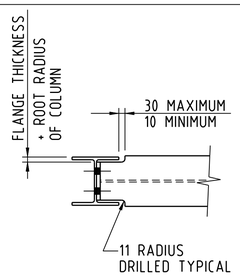

FLANGE COPE

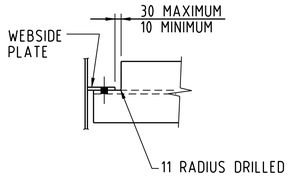

FLANGE COPE FOR WEB SIDE PLATES

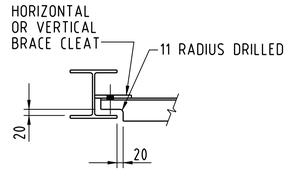

BRACE COPE

COPE DETAILS

LEGEND

AS DESIGNATED ON DESIGN DRAWING FOR NON-STANDARD CONNECTIONS

WS/n/(y)/p/T

- 'T' FOLLOWED BY A NUMBER DENOTES WEB SIDE PLATE THICKNESS
- DENOTES BOLTING PROCEDURE (OTHER THAN S)
- DENOTES NUMBER OF BOLT LINES (IF GREATER THAN 1)
- DENOTES NUMBER OF BOLT ROWS OTHER THAN STANDARD
- DENOTES WEB SIDE PLATE

* INDICATES DIMENSION VARIES FOR BEAM CONNECTION NOT AT RIGHT ANGLES

NOTES

1. FOR STEELWORK GENERAL NOTES REFER DRAWING. MD-101-SMEM-EG-ST-DST-0009.
2. FOR TYPICAL BRACING CLEAT AND BRACE DETAILS REFER DRAWING MD-101-SMEM-EG-ST-DST-0013.
3. STRUCTURAL CAPACITIES OF THE CONNECTIONS SHOWN ON THIS DRAWING SHALL BE CHECKED BY THE CONTRACTOR TO DETERMINE THEIR SUITABILITY FOR THE INTENDED USE.
4. ALL GUSSET PLATES SHALL BE WELDED USING 6 mm FILLET WELD UNLESS SHOWN OTHERWISE ON THE DESIGN DRAWINGS.

DOCUMENT NUMBER	REFERENCE DOCUMENTS	REV	DATE	REVISION DESCRIPTION	DRN	CHK	ENG	APP	MD

This drawing and all the information contained herein it is the proprietary property of Ma'aden and is subject to confidentiality restrictions between Ma'aden and the recipient. The information contained herein is provided for a limited purpose and must be returned on request. Ma'aden makes no respresentations or warranties that this information is complete or fit for any particular purpose. Neither this drawing nor any information concerning it may be copied, exhibited or furnished to others. Nor may photographs be taken of any article fabricated or assembled from this drawing, without Ma'aden prior written consent.

REV C01 PREPARED FOR MA'ADEN BY HATCH ASSOCIATES H332701-0000-35-041-0011_C

MA'ADEN معادن Saudi Arabian Mining Company

DRAWN	J BADAL	01.03.11
CHECKED	J EDWARDS	18.04.12
ENGINEER	D KIRKWOOD	18.04.12
APPROVED	R COVELLA	18.04.12
MA'ADEN		
SCALE NTS		A1

MA'ADEN ENGINEERING MANUAL
ALL AREAS
STRUCTURAL STANDARDS
BEAM AND BRACING CONNECTIONS SHT 2

DRAWING NUMBER MD-101-SMEM-EG-ST-DST-0011 REV C01

$DATE$ $TIME$ $FILE$