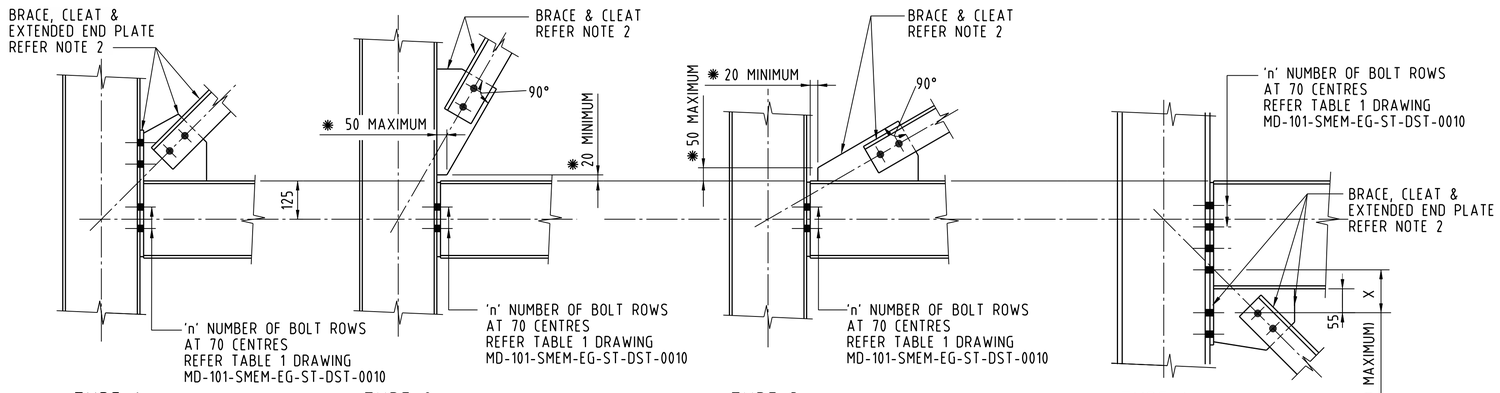


TYPE 1 TYPE 2 TYPE 3


NOTE:
USE TYPE 1 ONLY WHERE SETTING OUT CRITERIA DOES NOT PERMIT USE OF TYPES 2 AND 3

TYPE 4

NOTE:
USE TYPE 4 ONLY WHERE SETTING OUT CRITERIA DOES NOT PERMIT USE OF TYPES 2 AND 3


VERTICAL BRACE TO COLUMN FLANGE DETAILS


ALL BEAM TO COLUMN CONNECTIONS AT VERTICAL BRACE LOCATIONS SHALL BE FULL HEIGHT END PLATE TYPE FEP REFER DRAWING MD-101-SMEM-EG-ST-DST-0010

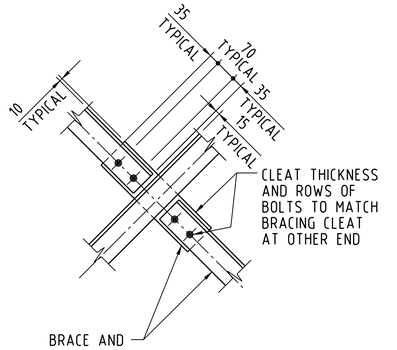

NOTE:
WHERE ANGLES ARE BACK TO BACK PROVIDE PACKER OF THICKNESS OF CLEATS AT OTHER END.
BOLT ON CENTRE LINE WITH 1-M20


ANGLE CROSS BRACING DETAILS

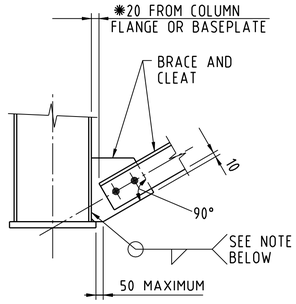

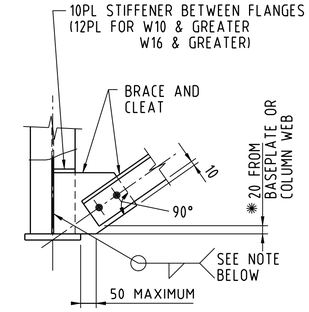

NOTE:
FOR WELD SIZE INFORMATION REFER NOTE 5.4 ON DRG MD-101-SMEM-EG-ST-DST-0009

VERTICAL BRACE TO COLUMN BASEPLATE DETAIL

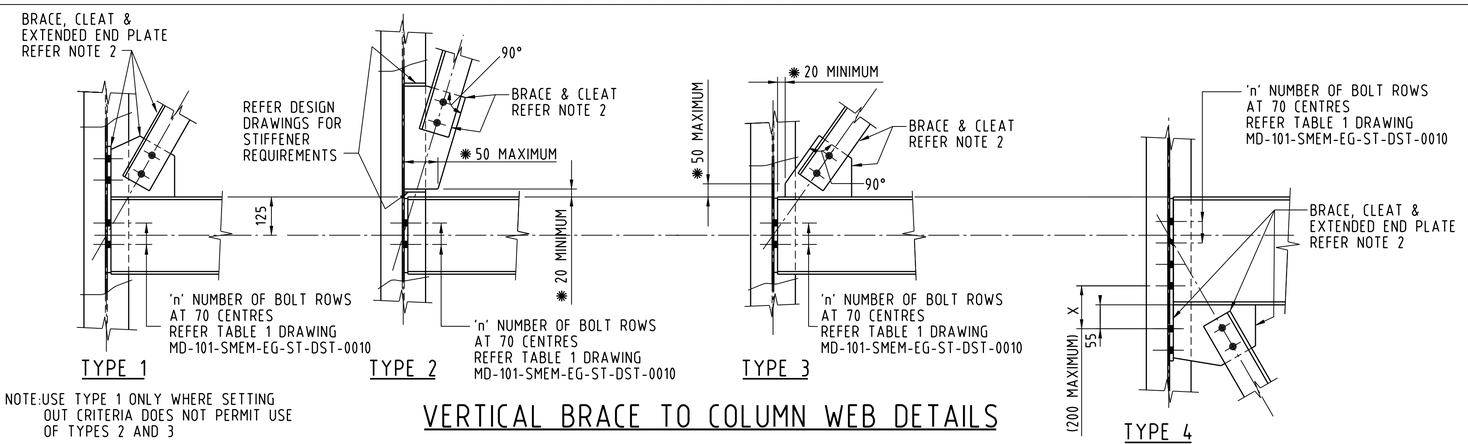

TYPE 1 TYPE 2 TYPE 3


NOTE:USE TYPE 1 ONLY WHERE SETTING OUT CRITERIA DOES NOT PERMIT USE OF TYPES 2 AND 3

TYPE 4


NOTE:
USE TYPE 4 ONLY WHERE SETTING OUT CRITERIA DOES NOT PERMIT USE OF TYPES 2 AND 3

VERTICAL BRACE TO COLUMN WEB DETAILS

ALL BEAM TO COLUMN CONNECTIONS AT VERTICAL BRACE LOCATIONS SHALL BE END PLATE TYPE FEP REFER DRAWING MD-101-SMEM-EG-ST-DST-0010

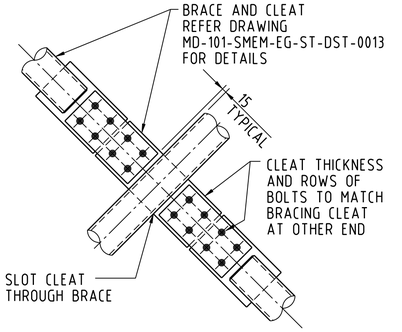

PIPE CROSS BRACING DETAIL

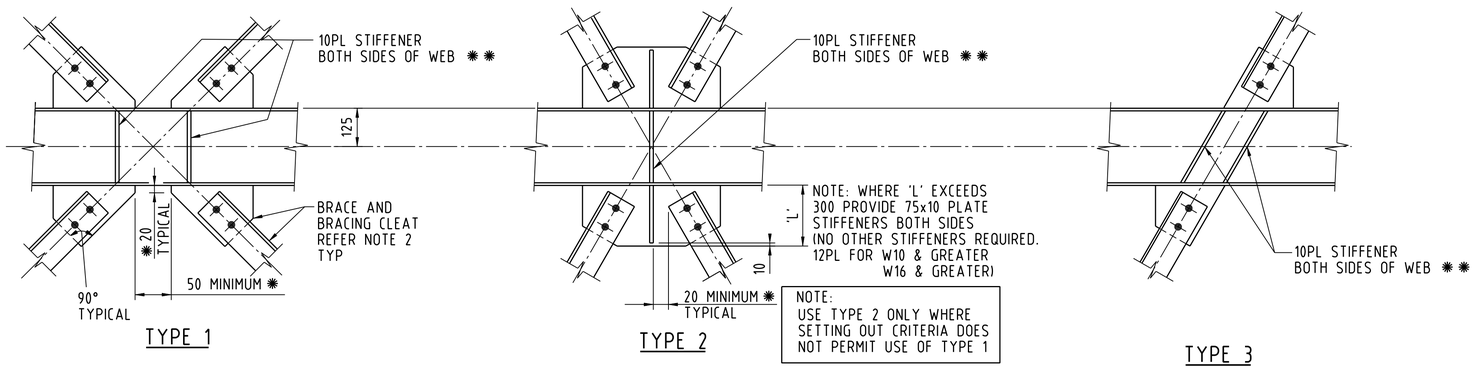


TYPE 1 TYPE 2

NOTE:
USE TYPE 2 ONLY WHERE SETTING OUT CRITERIA DOES NOT PERMIT USE OF TYPE 1

TYPE 3

VERTICAL BRACE TO BEAM DETAIL

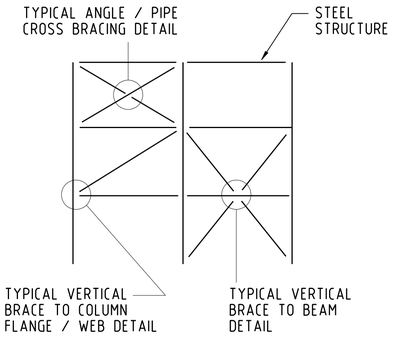

TYPICAL APPLICATIONS

LEGEND:

✱ DENOTES SETTING OUT CRITERIA

✱✱ DENOTES STIFFENERS MAY BE DISPLACED BY 50 MAX TO PROVIDE CLEARANCE TO FLOOR BEAM CONNECTIONS. STIFFENER MAY BE DELETED WHERE DISPLACEMENT MUST BE GREATER THAN 50. STIFFENERS SHALL BE 12PL FOR W10 & GREATER, W16 & GREATER

NOTES:

1. FOR STEELWORK GENERAL NOTES REFER DRAWING MD-101-SMEM-EG-ST-DST-0009.
2. FOR TYPICAL BRACE CLEAT DETAILS REFER DRAWING MD-101-SMEM-EG-ST-DST-0013.
3. STRUCTURAL CAPACITIES OF THE CONNECTIONS SHOWN ON THIS DRAWING SHALL BE CHECKED BY THE CONTRACTOR TO DETERMINE THEIR SUITABILITY FOR THE INTENDED USE.

DOCUMENT NUMBER	REFERENCE DOCUMENTS	REV	DATE	REVISION DESCRIPTION	DRN	CHK	ENG	APP	MD

This drawing and all the information contained herein it is the proprietary property of Ma'aden and is subject to confidentiality restrictions between Ma'aden and the recipient. The information contained herein is provided for a limited purpose and must be returned on request. Ma'aden makes no respresentations or warranties that this information is complete or fit for any particular purpose. Neither this drawing nor any information concerning it may be copied, exhibited or furnished to others. Nor may photographs be taken of any article fabricated or assembled from this drawing, without Ma'aden prior written consent.

REV C01 PREPARED FOR MA'ADEN BY HATCH ASSOCIATES H332701-0000-35-041-0012_C

MA'ADEN معادن Saudi Arabian Mining Company

DRAWN	J BADAL	04.03.11
CHECKED	J EDWARDS	18.04.12
ENGINEER	D KIRKWOOD	18.04.12
APPROVED	R COVELLA	18.04.12
MA'ADEN		
SCALE NTS		A1

MA'ADEN ENGINEERING MANUAL
ALL AREAS
STRUCTURAL STANDARDS
BRACE CONNECTIONS SHEET 1

DRAWING NUMBER MD-101-SMEM-EG-ST-DST-0012 REV C01

MA'ADEN PHOSPHATE PROJECT-A1 BORDER-REV A02

$FILE$ $TIME$ $DATE$