




W6x20 SPLICE
M20 BOLT FIXINGS

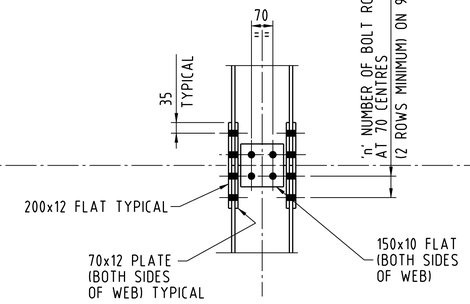


W8x35 SPLICE
M20 BOLT FIXINGS

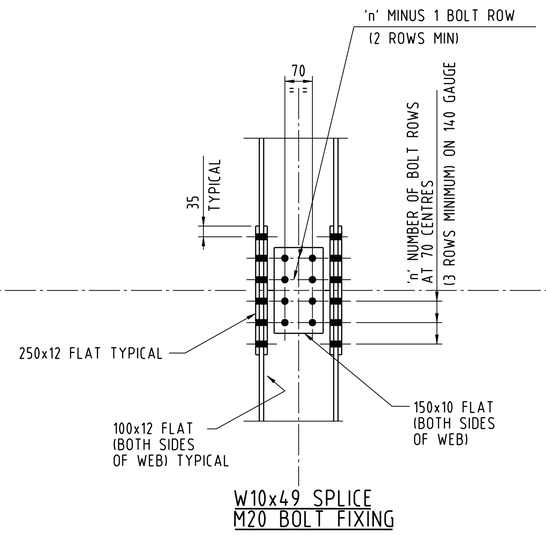

W10x49 SPLICE
M20 BOLT FIXING

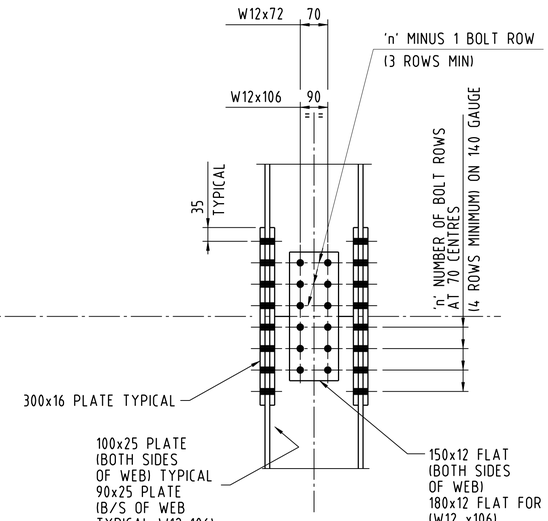

W12x72 SPLICE
M24 BOLT FIXINGS
W12x106 SPLICE (AS NOTED)
M24 BOLT FIXINGS

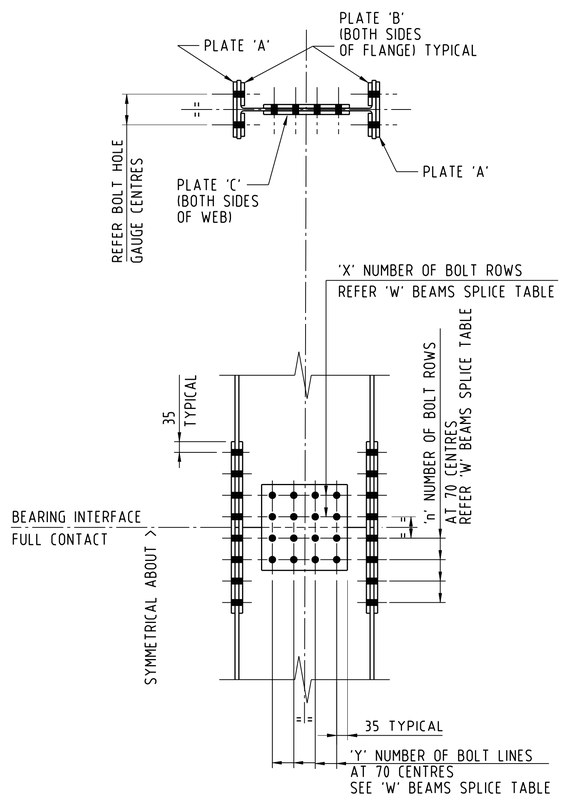

'W' BEAM SPLICE

'W' BEAMS SPLICE TABLE

COLUMN	FLANGE					WEB			
	PLATE 'A'		PLATE 'B'		BOLT HOLE GAUGE CENTRES	PLATE 'C'			
	WIDTH	THICK-NESS	WIDTH	THICK-NESS		THICK-NESS	n	X	Y
W8x18	130	10	-	-	70	8	2	2	2
W10x22	140	12	-	-	140	8	2	2	2
W10x26	140	12	-	-	140	8	2	2	2
W12x26	140	16	-	-	140	8	3	2	2
W12x30	140	16	-	-	140	8	3	2	2
W14x34	170	12	70	12	200	8	3	2	3
W16x40	170	12	70	12	200	8	3	2	3
W18x46	160	20	-	-	180	8	3	2	3
W21x50	170	12	70	12	200	10	3	2	4
W21x62	210	16	70	16	140	10	4	2	4
W24x68	210	16	90	16	140	12	4	2	5
W24x84	210	16	90	20	140	12	4	2	5
W27x94	250	20	90	20	160	12	4	2	4
W30x116	250	20	90	25	160	12	4	2	5
W33x118	250	25	90	25	160	12	5	2	6
W36x150	300	32	110	32	190	12	4	2	6
W36x170	300	32	110	32	190	12	4	2	6
W40x183	300	32	110	32	190	12	4	2	6

LEGEND AS DENOTED ON DESIGN DRAWINGS

S/n/p
- S — DENOTES BOLTING PROCEDURE (OTHER THAN PT)
- n — DENOTES NUMBER OF BOLT ROWS OTHER THAN STANDARD
- p — DENOTES SPLICE

NOTES:

1. FOR STEELWORK GENERAL NOTES AND INDEX REFER DRAWING MD-101-SMEM-EG-ST-DST-0009.
2. STRUCTURAL CAPACITIES OF THE CONNECTIONS SHOWN ON THIS DRAWING SHALL BE CHECKED BY THE CONTRACTOR TO DETERMINE THEIR SUITABILITY FOR THE INTENDED USE.
3. WHERE SAME SIZE COLUMNS OF DIFFERENT WEIGHTS ARE SPLICED, PROVIDE PACKING PLATES, THICKNESS TO SUIT, DIMENSIONS TO MATCH SPLICE PLATES.
4. BOLTING PROCEDURE FOR ALL SPLICE CONNECTIONS SHALL BE FULLY TENSIONED BEARING (PT) UNLESS NOTED OTHERWISE ON DESIGN DRAWING.
5. FOR DETAILS OF SPLICE / CONNECTION OF COLUMNS OF DIFFERENT SECTIONS REFER TO THE DESIGN DRAWINGS.
6. FOR 'W' BEAM SPLICE TABLE REFER TO MD-101-SMEM-EG-ST-SPC-0001

DOCUMENT NUMBER	REFERENCE DOCUMENTS	REV	DATE	REVISION DESCRIPTION	DRN	CHK	ENG	APP	MD

This drawing and all the information contained herein it is the proprietary property of Ma'aden and is subject to confidentiality restrictions between Ma'aden and the recipient. The information contained herein is provided for a limited purpose and must be returned on request. Ma'aden makes no respresentations or warranties that this information is complete or fit for any particular purpose. Neither this drawing nor any information concerning it may be copied, exhibited or furnished to others. Nor may photographs be taken of any article fabricated or assembled from this drawing, without Ma'aden prior written consent.

REV C01 PREPARRED FOR MA'ADEN BY HATCH ASSOCIATES H332701-0000-35-041-0015_C

MA'ADEN معادن Saudi Arabian Mining Company

DRAWN	J BADAL	04.03.11
CHECKED	J EDWARDS	18.04.12
ENGINEER	K KIRKWOOD	18.04.12
APPROVED	R COVELLA	18.04.12
MA'ADEN		
SCALE NTS		A1

MA'ADEN ENGINEERING MANUAL
ALL AREAS
STRUCTURAL STANDARDS
COLUMN SPLICES

DRAWING NUMBER MD-101-SMEM-EG-ST-DST-0015 REV C01

$DATE$ $TIME$ $FILE$