


ENDSTOP

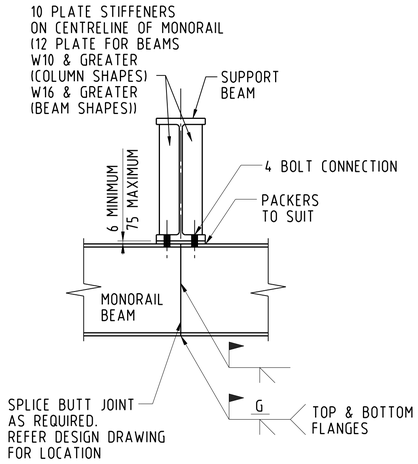

SUPPORT TYPE MS1

TABLE 1


MONORAIL SIZE	MS2 & MS3		MS4		END STOP	
	STUB COL	END PLATE	STUB COL	END PLATE	DIM 'X'	ANGLE SIZE
W8x18	W6x20	12mm	W6x20	12mm	30	L3x3x0.375
W10x22/26	W6x20	12mm	W6x20	12mm	30	L3x3x0.375
W12x26/30	W8x31	12mm	W8x31	16mm	30	L3x3x0.375
W14x34	W8x31	12mm	W8x31	16mm	30	L3x3x0.375
W16x40	W8x31	16mm	W8x31	16mm	30	L3x3x0.375
W18x46	W8x31	16mm	W8x31	20mm	35	L4x4x0.375
W21x50/62	W8x31	16mm	W8x31	20mm	35	L4x4x0.375
W24x68/84	W8X31	16mm	W8x31	20mm	35	L4x4x0.375
W8x35	W8x31	12mm	W8x31	16mm	30	L4x4x0.375
W10x49	W8x31	12mm	W8x31	20mm	35	L6x4x0.375 *
W12x72/106	W8x31	12mm	W8x31	20mm	60	L6x4x0.375 *

* 100 LEG IN LINE WITH WEB OF MONORAIL


LEGEND AS DENOTED ON DESIGN DRAWINGS

MS1
└ DENOTES MONORAIL SUPPORT TYPE

NOTE: STRUCTURAL CAPACITIES OF THE MONORAIL CONNECTIONS SHOWN ON THIS DRAWING SHALL BE CHECKED BY THE DESIGN ENGINEER TO DETERMINE SUITABILITY PRIOR TO USE.

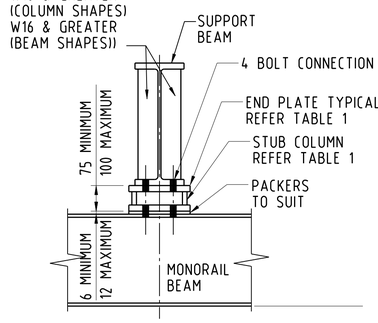


SUPPORT TYPE MS2

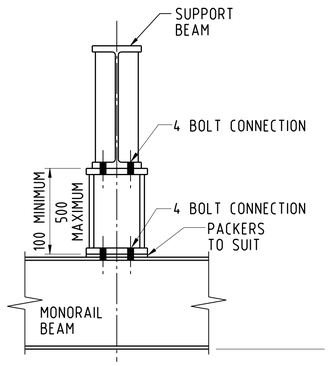

DETAILS NOT SHOWN AS PER SUPPORT TYPE MS2

SUPPORT TYPE MS3

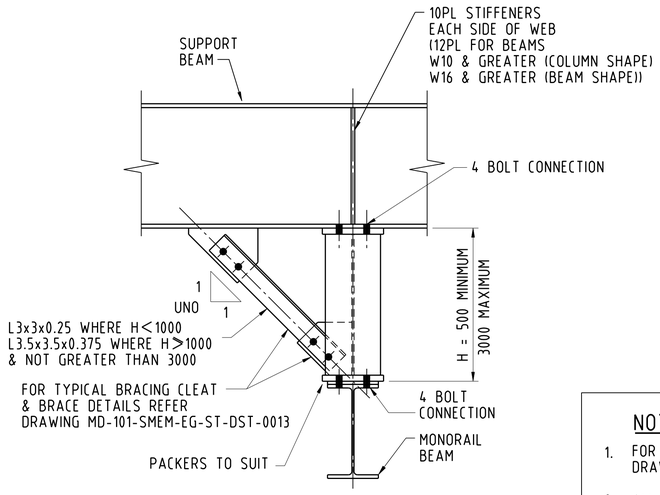

SUPPORT TYPE MS4

NOTES:

1. FOR STEELWORK GENERAL NOTES REFER DRAWING MD-101-SMEM-EG-ST-DST-0009.
2. ALL BOLTED MONORAIL CONNECTIONS TO BE M20 HIGH STRENGTH SNUG TIGHT COMPLETE WITH LOCKNUTS & WASHERS UNLESS NOTED OTHERWISE.
3. STRUCTURAL CAPACITIES OF THE CONNECTIONS SHOWN ON THIS DRAWING SHALL BE CHECKED BY THE CONTRACTOR TO DETERMINE THEIR SUITABILITY FOR THE INTENDED USE.
4. FOR TABLE 1, REFER TO MD-101-SMEM-EG-ST-SPC-000)

MONORAIL DETAILS

DOCUMENT NUMBER	REFERENCE DOCUMENTS	REV	DATE	REVISION DESCRIPTION	DRN	CHK	ENG	APP	MD

This drawing and all the information contained herein it is the proprietary property of Ma'aden and is subject to confidentiality restrictions between Ma'aden and the recipent. The information contained herein is provided for a limited purpose and must be returned on request. Ma'aden makes no respresentations or warranties that this information is complete or fit for any particular purpose. Neither this drawing nor any information concerning it may be copied, exhibited or furnished to others. Nor may photographs be taken of any article fabricated or assembled from this drawing, without Ma'aden prior written consent.

REV C01 PREPARED FOR MA'ADEN
BY HATCH ASSOCIATES
H332701-0000-35-041-0016_C

MA'ADEN معادن
Saudi Arabian Mining Company

DRAWN	J. BADAL	04.03.11
CHECKED	J EDWARDS	18.04.12
ENGINEER	D KIRKWOOD	18.04.12
APPROVED	R COVELLA	18.04.12
MA'ADEN		
SCALE NTS		A1

MA'ADEN ENGINEERING MANUAL
ALL AREAS
STRUCTURAL STANDARDS
MONORAIL DETAILS

DRAWING NUMBER MD-101-SMEM-EG-ST-DST-0016 REV C01

MA'ADEN PHOSPHATE PROJECT-A1 BORDER-REV A02
$DATE$ $TIME$ $FILE$