




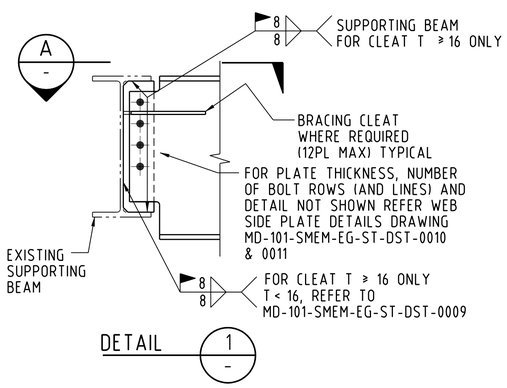


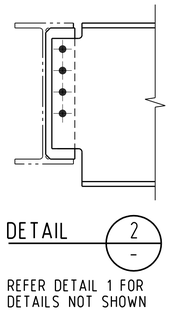


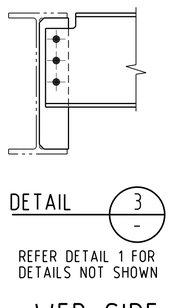


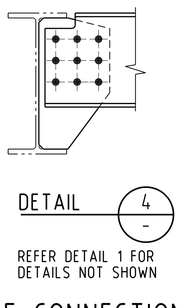

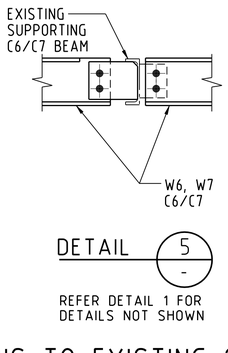


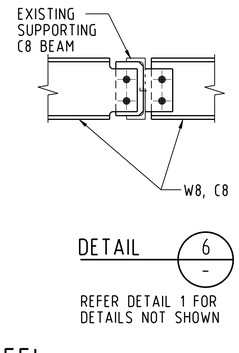


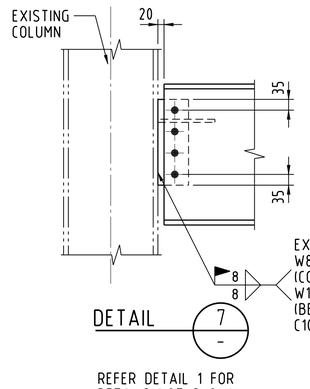


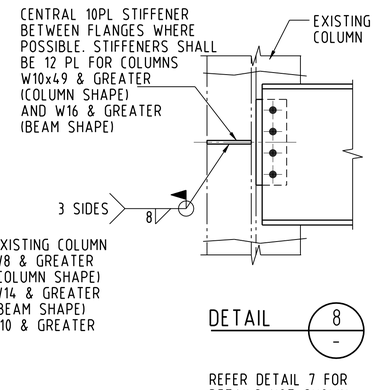



WEB SIDE PLATE CONNECTIONS TO EXISTING STEEL

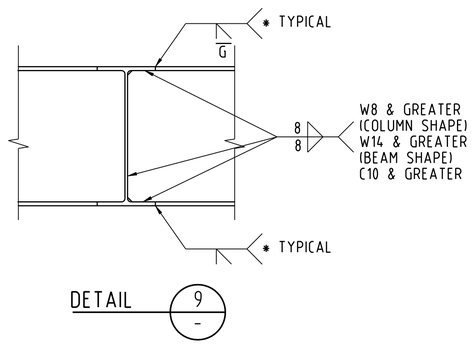


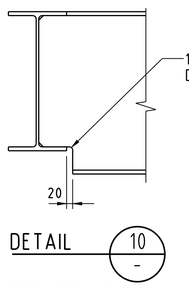

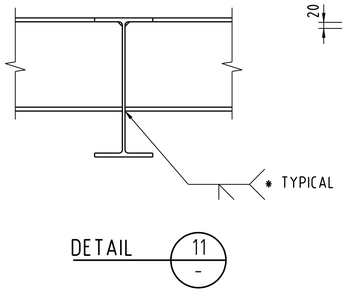


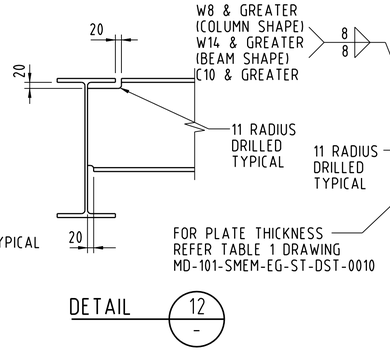

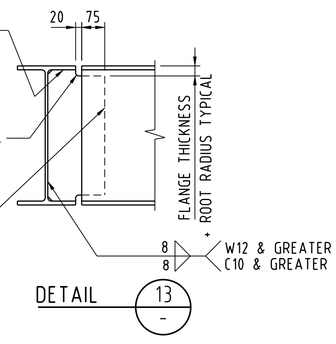


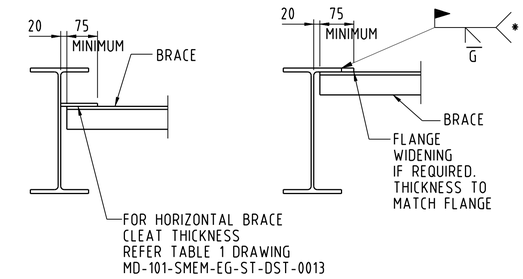


WELDED HORIZONTAL BRACE CONNECTIONS

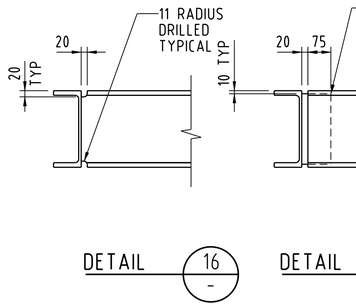


WELDED BEAM TO BEAM CONNECTIONS

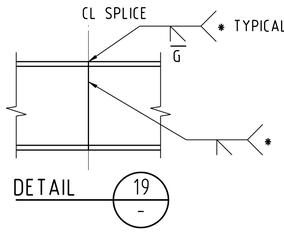


WELDED BEAM SPLICE

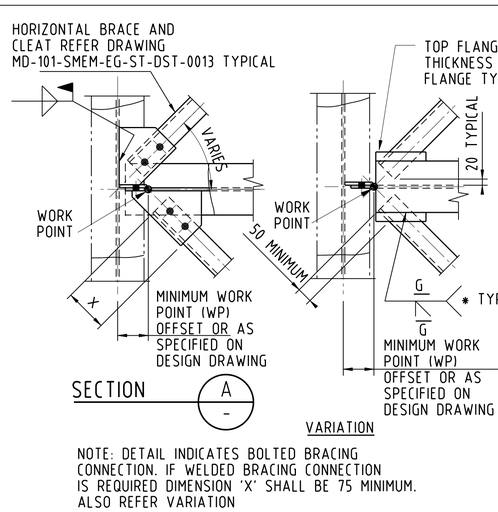

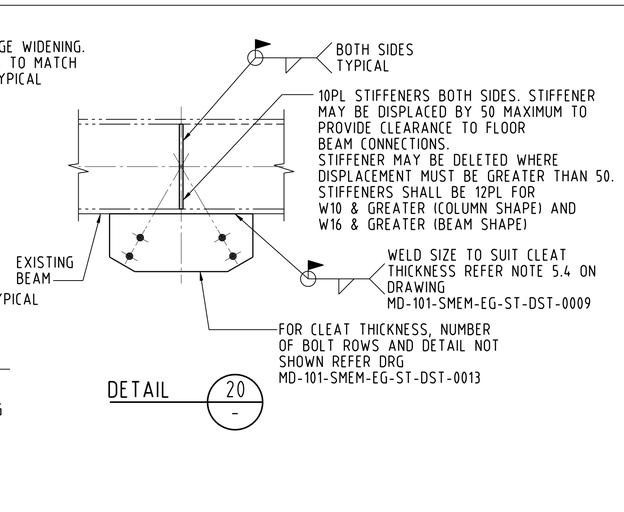

BRACE CONNECTIONS TO EXISTING STEEL

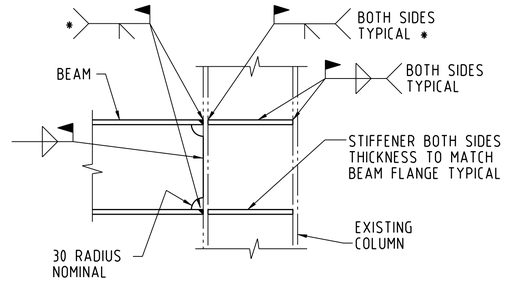

WELDED MOMENT CONNECTIONS TO EXISTING STEEL

NOTES:

1. FOR STEELWORK GENERAL NOTES REFER DRAWING MD-101-SMEM-EG-ST-DST-0009
2. DETAILS 9 TO 19 MAY ALSO BE USED FOR CONNECTING NEW STEELWORK TO EXISTING STEELWORK.
3. * DENOTES USE FULLY PREPARED DOUBLE BUTT WELD WHERE PLATE OR FLANGE THICKNESS >16.
4. STRUCTURAL CAPACITIES OF THE CONNECTIONS SHOWN ON THIS DRAWING SHALL BE CHECKED BY THE CONTRACTOR TO DETERMINE THEIR SUITABILITY FOR THE INTENDED USE.

DOCUMENT NUMBER	REFERENCE DOCUMENTS	REV	DATE	REVISION DESCRIPTION	DRN	CHK	ENG	APP	MD

This drawing and all the information contained herein it is the proprietary property of Ma'aden and is subject to confidentiality restrictions between Ma'aden and the recipent. The information contained herein is provided for a limited purpose and must be returned on request. Ma'aden makes no respresentations or warranties that this information is complete or fit for any particular purpose. Neither this drawing nor any information concerning it may be copied, exhibited or furnished to others. Nor may photographs be taken of any article fabricated or assembled from this drawing, without Ma'aden prior written consent.

REV C01 PREPARED FOR MA'ADEN BY HATCH ASSOCIATES H332701-0000-35-041-0018_C

MA'ADEN معادن Saudi Arabian Mining Company

DRAWN	J BADAL	09.03.11
CHECKED	J EDWARDS	18.04.12
ENGINEER	D KIRKWOOD	18.04.12
APPROVED	R COVELLA	18.04.12
MA'ADEN		
SCALE NTS		A1

MA'ADEN ENGINEERING MANUAL
ALL AREAS
STRUCTURAL STANDARDS
WELDED CONNECTIONS

DRAWING NUMBER MD-101-SMEM-EG-ST-DST-0018 REV C01

MA'ADEN PHOSPHATE PROJECT-A1 BORDER-REV A02
$FILE$ $TIME$ $DATE$