
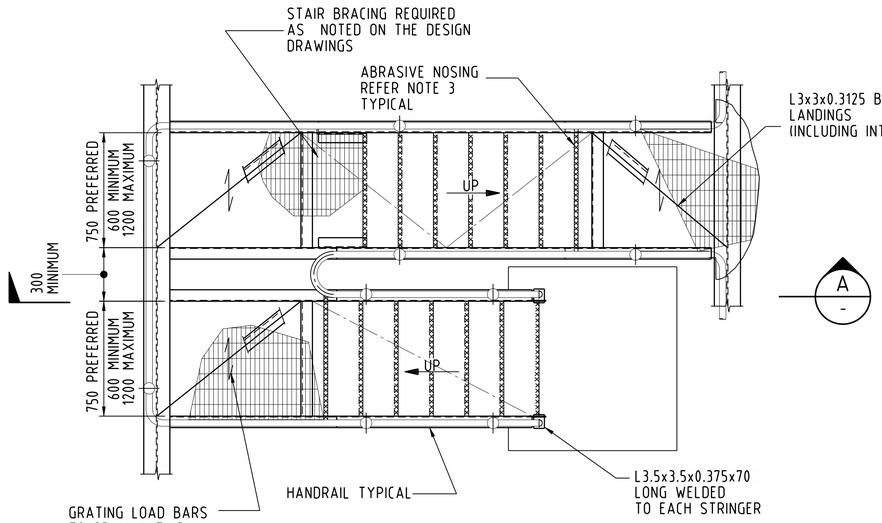


TYPICAL STAIRWAY PLAN


THE EXTENT OF STAIRS AND HANDRAILS ARE SHOWN ON THE DESIGN DRAWINGS

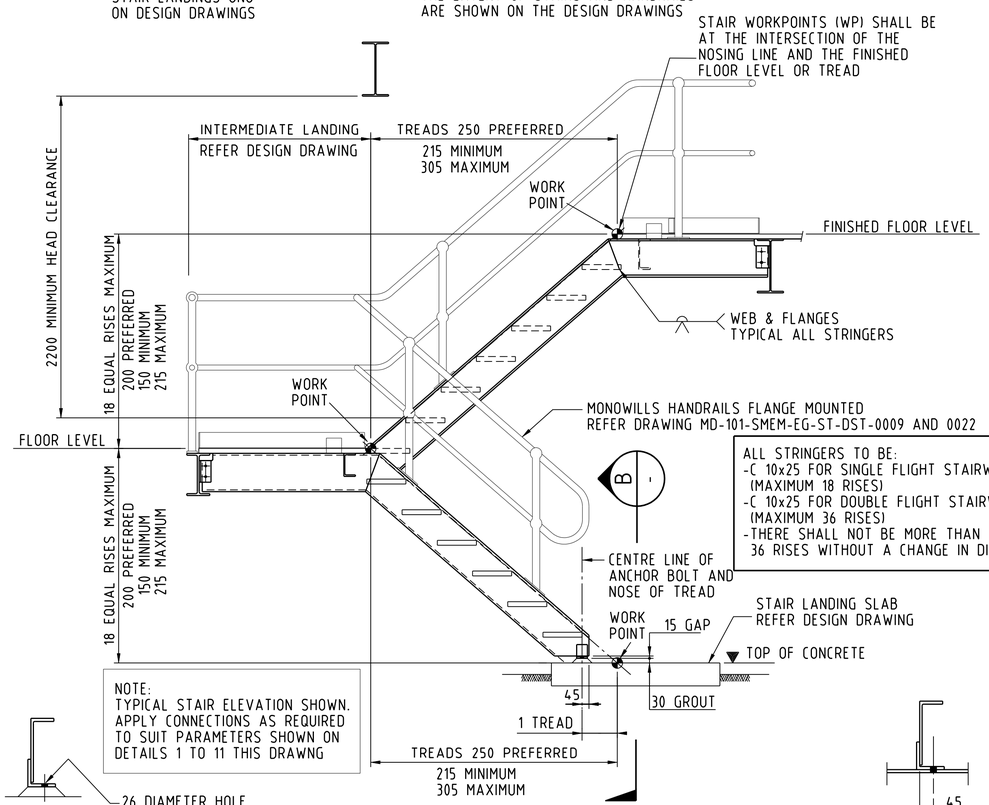


SECTION A -

SECTION B -


SECTION C -

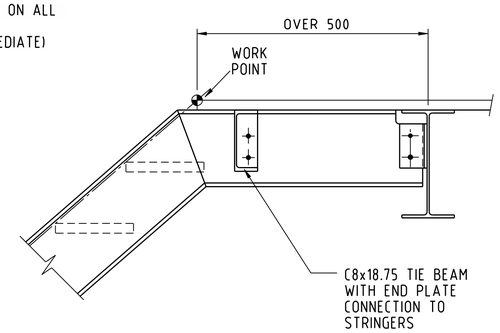


DETAIL 1 -

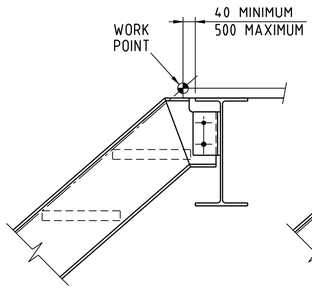


DETAIL 2 -

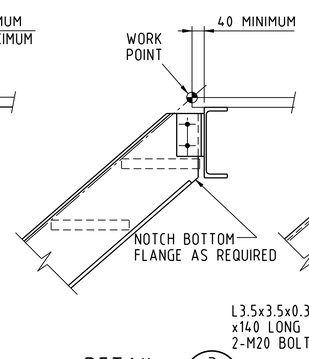


DETAIL 3 -

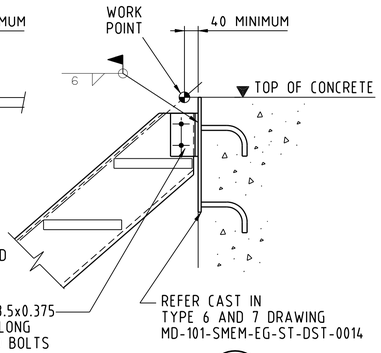


DETAIL 4 -

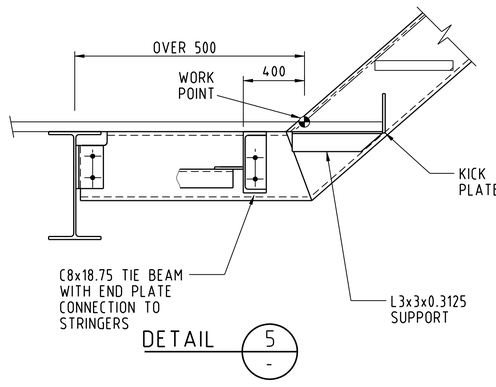


DETAIL 5 -

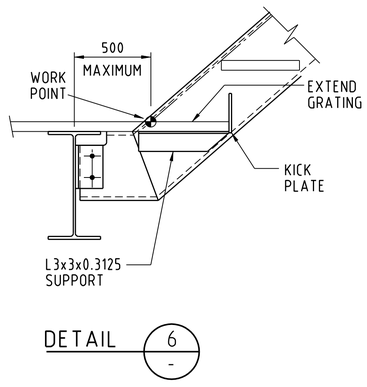


DETAIL 6 -

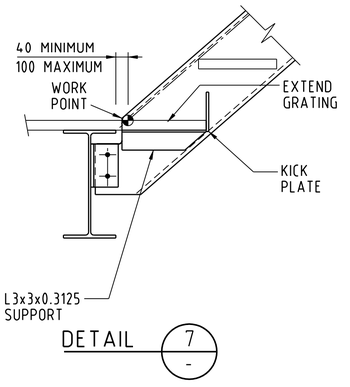


DETAIL 7 -

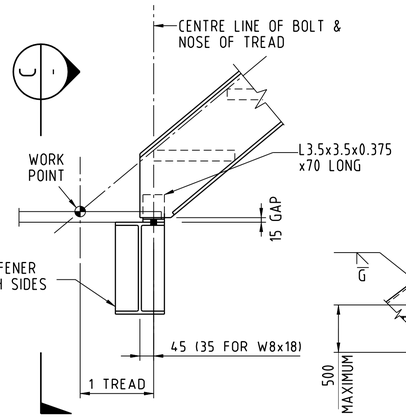

DETAIL 8 -

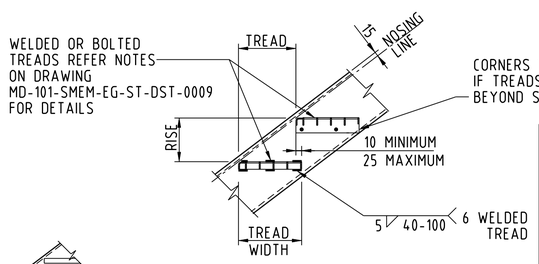

DETAIL 9 - WELDED TREAD

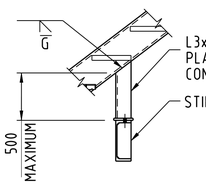

DETAIL 10 -

DETAIL 11 - BOLTED TREAD (PREFERRED)

NOTES:

1. FOR STEELWORK GENERAL NOTES REFER DRAWING MD-101-SMEM-EG-ST-DST-0009.
2. THE DETAILS SHOWN IN THIS DRAWING ARE BASED ON THE REQUIREMENTS OUTLINED IN PROCESS INDUSTRY PRACTICES PIP STF05511 "FIXED INDUSTRIAL STAIRS" AND ARE THE MINIMUM ACCEPTABLE.
3. ABRASIVE NOSING, WHERE SPECIFIED ON DESIGN DRAWINGS SHALL BE 50x25 REMOVABLE TYPE, COLOURED YELLOW AND ATTACHED TO TOP LANDING & STAIR TREADS WITH 3 SS CLIPS & M8x35 LONG CHEESE HEAD STAINLESS STEEL BOLTS.
4. STAIR TREADS, STRINGER AND BRACING TO BE ASSEMBLED AND DELIVERED AS ONE ITEM.
5. THE PRODUCT OF THE RISE x PROJECTED TREAD MUST FALL BETWEEN 45000 MINIMUM AND 50000 MAXIMUM. DESIGN DRAWINGS TO INDICATE BOTH RISE AND THE PROJECTED TREAD DIMENSIONS.

DOCUMENT NUMBER	REFERENCE DOCUMENTS	REV	DATE	REVISION DESCRIPTION	DRN	CHK	ENG	APP	MD

This drawing and all the information contained herein it is the proprietary property of Ma'aden and is subject to confidentiality restrictions between Ma'aden and the recipient. The information contained herein is provided for a limited purpose and must be returned on request. Ma'aden makes no respresentations or warranties that this information is complete or fit for any particular purpose. Neither this drawing nor any information concerning it may be copied, exhibited or furnished to others. Nor may photographs be taken of any article fabricated or assembled from this drawing, without Ma'aden prior written consent.

REV C01 PREPARED FOR MA'ADEN BY HATCH ASSOCIATES H332701-0000-35-041-0019_C

MA'ADEN معادن Saudi Arabian Mining Company

DRAWN	J BADAL	04.03.11
CHECKED	J EDWARDS	18.04.12
ENGINEER	D KIRKWOOD	18.04.12
APPROVED	R COVELLA	18.04.12
MA'ADEN		
SCALE NTS		A1

MA'ADEN ENGINEERING MANUAL
ALL AREAS
STRUCTURAL STANDARDS
STAIR DETAILS

DRAWING NUMBER MD-101-SMEM-EG-ST-DST-0019 REV C01

MA'ADEN PHOSPHATE PROJECT-A1 BORDER-REV A02
$FILE$ $TIME$ $DATE$