

STEELWORK NOTES:


1. FOR STEELWORK GENERAL NOTES REFER DRAWING NUMBER MD-101-SMEM-EG-ST-DST-0009.
2. ON ELEVATED PLATFORMS. WHERE THE BOTTOM OF THE LADDER TERMINATES AT A PLATFORM FITTED WITH A HANDRAIL WHICH IS LESS THAN 900mm FROM THE LADDER, OR FROM THE CENTRE OF THE LADDER TO EITHER SIDE, HIGH HANDRAILING SHALL BE PROVIDED AS REQUIRED OR TO A MAXIMUM OF 2100mm
3. THE DETAILS SHOWN ON THIS DRAWING ARE THE MINIMUM ACCEPTABLE. MODIFICATION AS NECESSARY SHALL BE MADE TO COMPLY WITH ANY LOCAL REGULATIONS THAT ARE MORE STRINGENT.
4. ALWAYS USE SELF CLOSING GATES UNLESS NOTED OTHERWISE

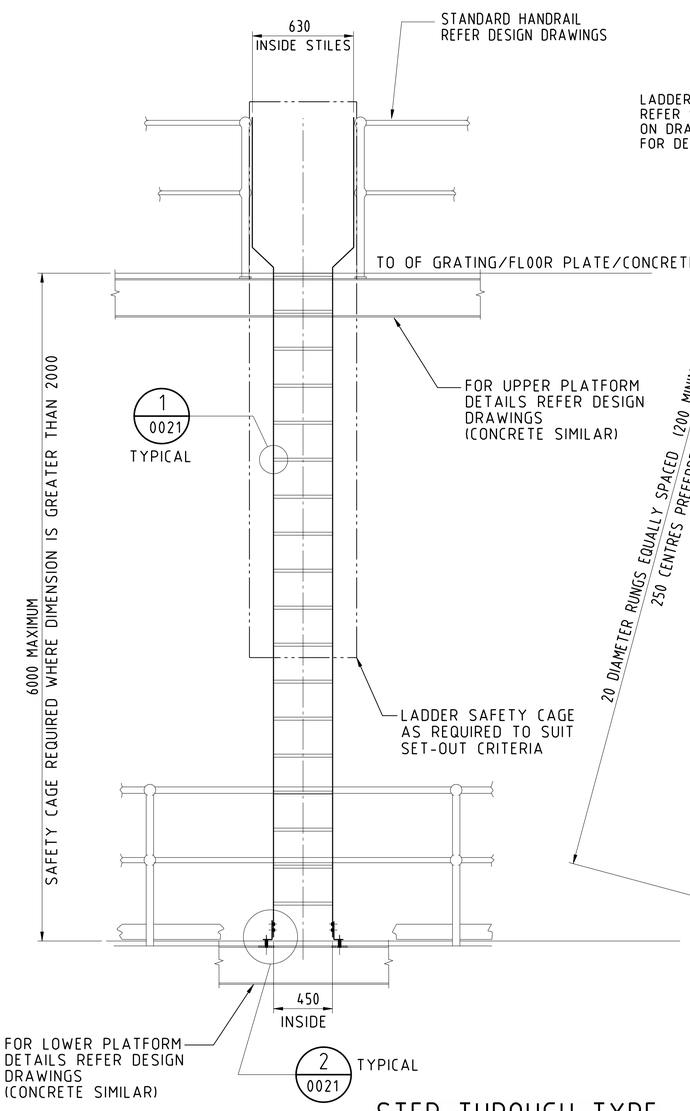


STEP THROUGH TYPE

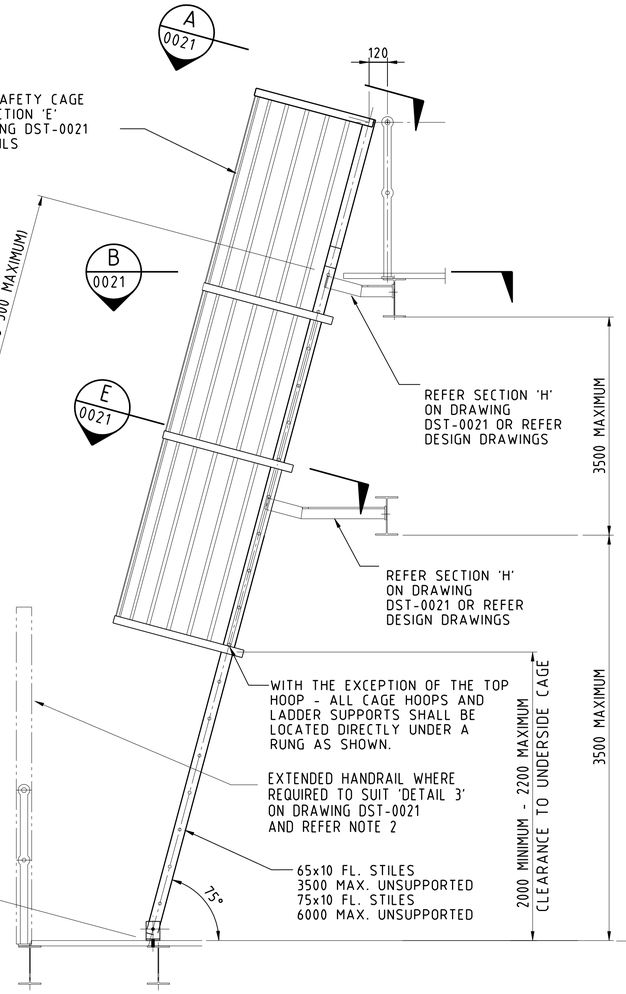

NOTE:
REFERENCES TO DRAWINGS
ON DETAILS PREFIXED:
MD-101-SMEM-EG-ST-DST-
UNLESS NOTED OTHERWISE.

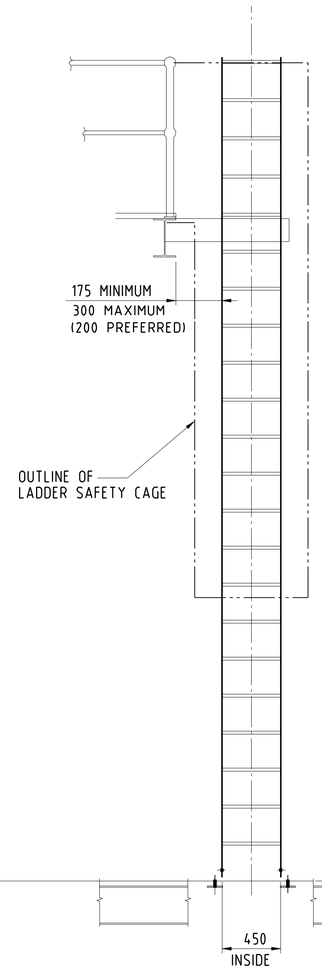

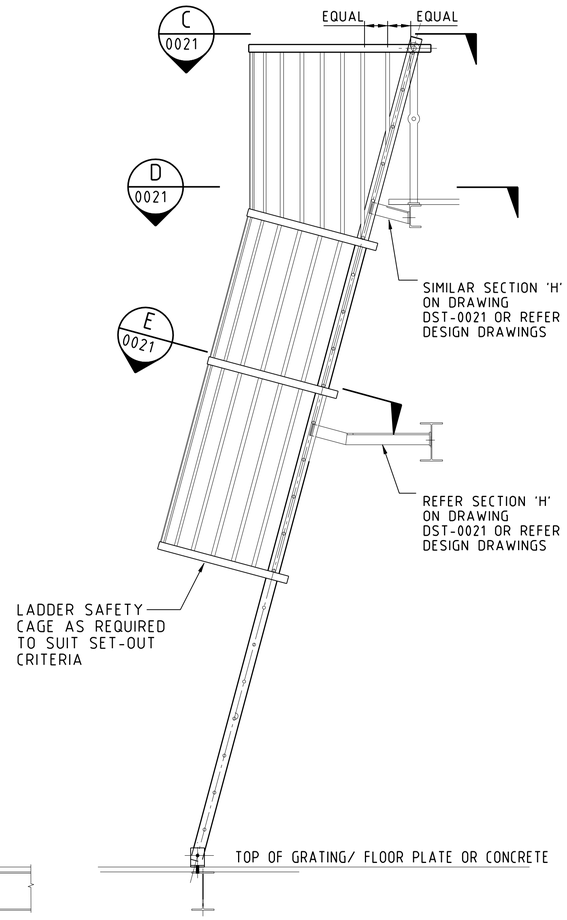

SIDE ACCESS TYPE (PREFERRED)

DETAILS NOT SHOWN ARE
AS PER 'STEP THROUGH TYPE'

DOCUMENT NUMBER	REFERENCE DOCUMENTS	REV	DATE	REVISION DESCRIPTION	DRN	CHK	ENG	APP	MD

This drawing and all the information contained herein it is the proprietary property of Ma'aden and is subject to confidentiality restrictions between Ma'aden and the recipient. The information contained herein is provided for a limited purpose and must be returned on request. Ma'aden makes no respresentations or warranties that this information is complete or fit for any particular purpose. Neither this drawing nor any information concerning it may be copied, exhibited or furnished to others. Nor may photographs be taken of any article fabricated or assembled from this drawing, without Ma'aden prior written consent.

REV C01 PREPARED FOR MA'ADEN
BY HATCH ASSOCIATES
H332701-0000-35-041-0020_C

MA'ADEN معادن
Saudi Arabian Mining Company

DRAWN	J BADAL	03/03/11
CHECKED	J EDWARDS	18.04.12
ENGINEER	D KIRKWOOD	18.04.12
APPROVED	R COVELLA	18.04.12
MA'ADEN		
SCALE NTS		A1

MA'ADEN ENGINEERING MANUAL
ALL AREAS
STRUCTURAL STANDARDS
SLOPING LADDER ARRANGEMENT

DRAWING NUMBER MD-101-SMEM-EG-ST-DST-0020 REV C01

$FILE$ $TIME$ $DATE$