

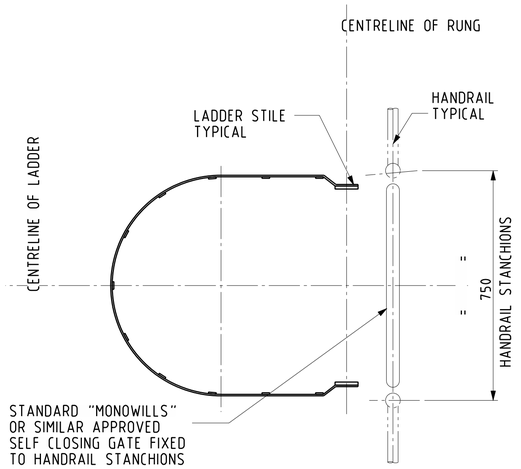



SECTION A 0020

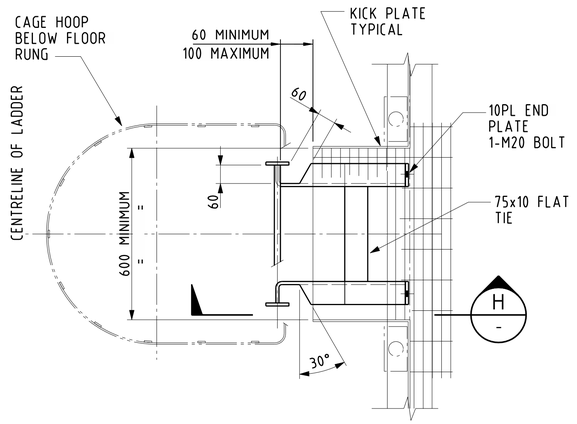

SECTION B 0020

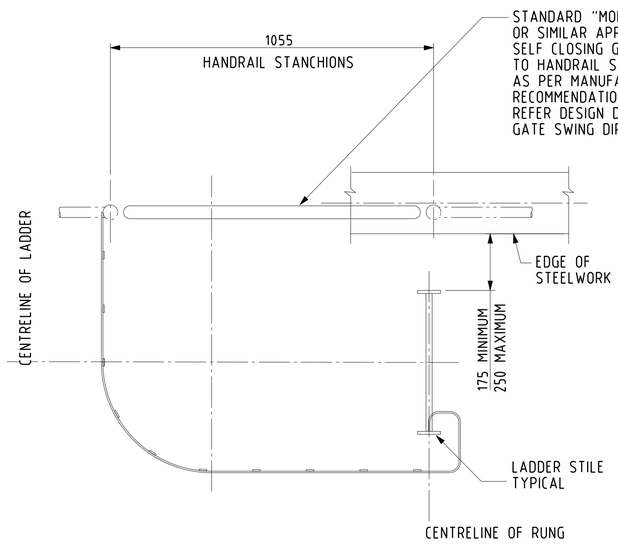


SECTION C 0020

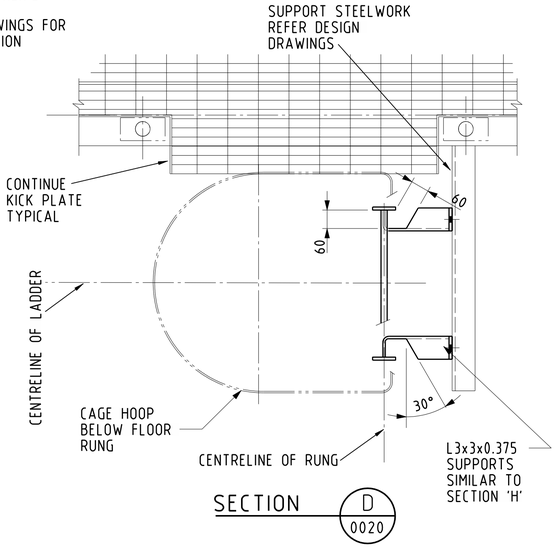


SECTION D 0020

STEP THROUGH TYPE

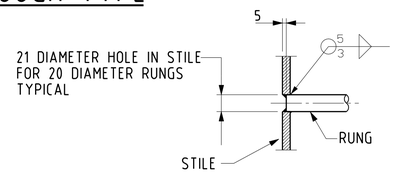


DETAIL 1 0020

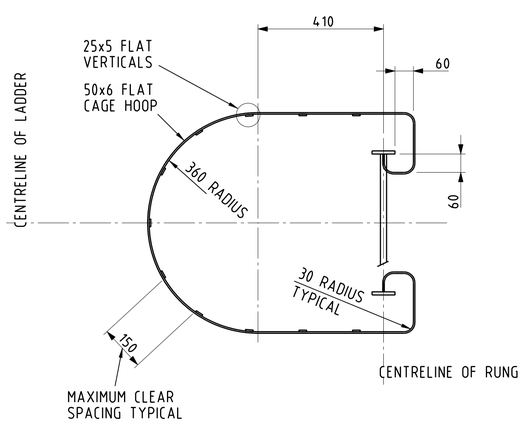


SECTION E 0020

SYMMETRICAL ABOUT LADDER CENTRE LINE

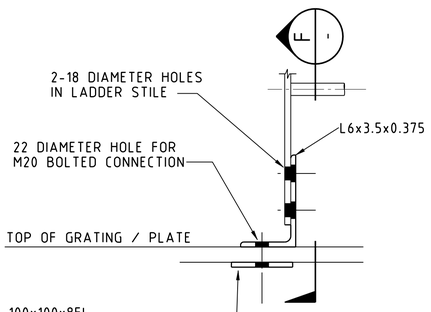

DETAIL 2 1:5

TYPICAL - BOTH TYPES

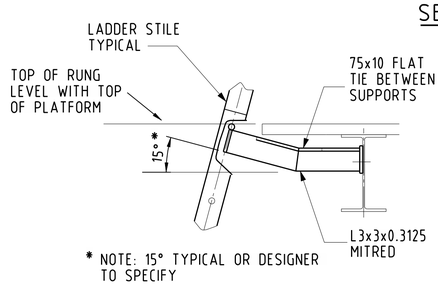


* NOTE: 15° TYPICAL OR DESIGNER TO SPECIFY

SECTION H -

SIDE ACCESS TYPE


NOTE:
REFERENCES TO DRAWINGS ON DETAILS PREFIXED
MD-101-SMEM-EG-ST-DST-
UNLESS OTHERWISE NOTED

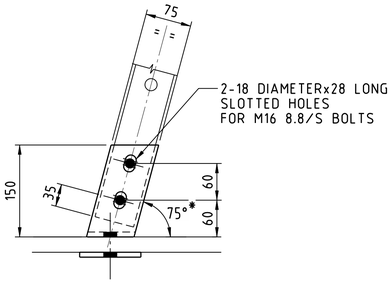

FOR CONNECTION TO FLOOR PLATE
SITE DRILL 22 DIAMETER HOLE IN PLATE FOR M20 BOLT.
FOR CONNECTION TO CONCRETE SLAB
USE M20 CHEMICAL ANCHOR (30 GROUT)


* NOTE: 75° TYPICAL OR DESIGNER TO SPECIFY

SECTION F 1:5

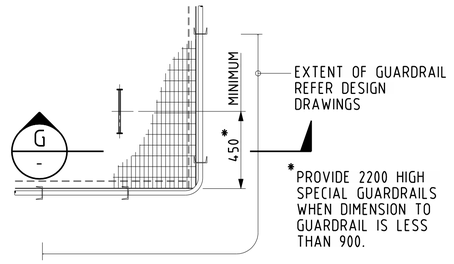

DETAIL 3 -

SPECIAL HEIGHT GUARDRAIL FOR LADDER/PLATFORM.

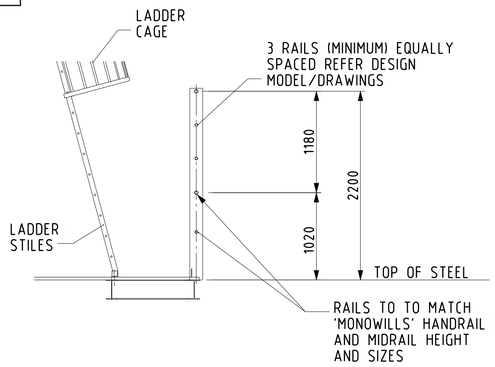

SECTION G -

NOTES:

1. FOR STEELWORK GENERAL NOTES REFER DRAWING MD-101-SMEM-EG-ST-DST-0009.
2. FOR LADDER TYPES REFER DRAWING MD-101-SMEM-EG-ST-DST-0020 & 0025.

DOCUMENT NUMBER	REFERENCE DOCUMENTS	REV	DATE	REVISION DESCRIPTION	DRN	CHK	ENG	APP	MD

This drawing and all the information contained herein it is the proprietary property of Ma'aden and is subject to confidentiality restrictions between Ma'aden and the recipient. The information contained herein is provided for a limited purpose and must be returned on request. Ma'aden makes no respresentations or warranties that this information is complete or fit for any particular purpose. Neither this drawing nor any information concerning it may be copied, exhibited or furnished to others. Nor may photographs be taken of any article fabricated or assembled from this drawing, without Ma'aden prior written consent.

REV C01 PREPARED FOR MA'ADEN BY HATCH ASSOCIATES H332701-0000-35-041-0021_C

MA'ADEN معادن Saudi Arabian Mining Company

DRAWN	J BADAL	04.03.11
CHECKED	J EDWARDS	18.04.12
ENGINEER	D KIRKWOOD	18.04.12
APPROVED	R COVELLA	18.04.12
MA'ADEN		
SCALE 1:10 UNO		A1

MA'ADEN ENGINEERING MANUAL
ALL AREAS
STRUCTURAL STANDARDS
SLOPING LADDER DETAILS

DRAWING NUMBER MD-101-SMEM-EG-ST-DST-0021 REV C01

$FILE$ $TIME$ $DATE$