

DRAWING NUMBER MD-101-SMEM-EG-ST-DST-0022 REV C01

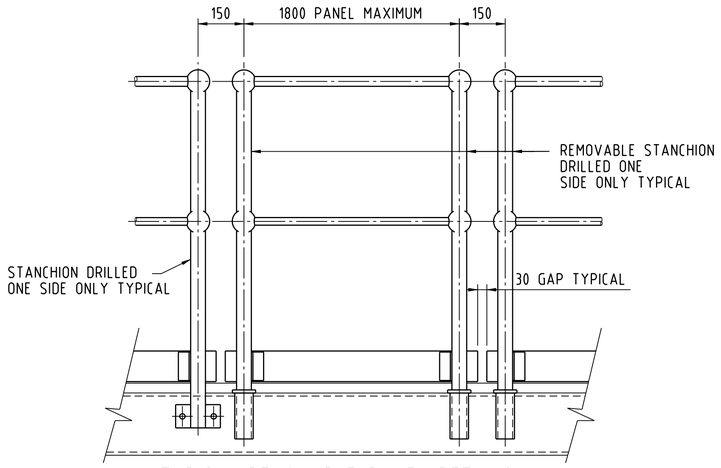


TYPICAL REMOVABLE PANEL DETAILS

(SEE TYPICAL FIXED HANDRAIL DETAILS UNLESS NOTED OTHERWISE)

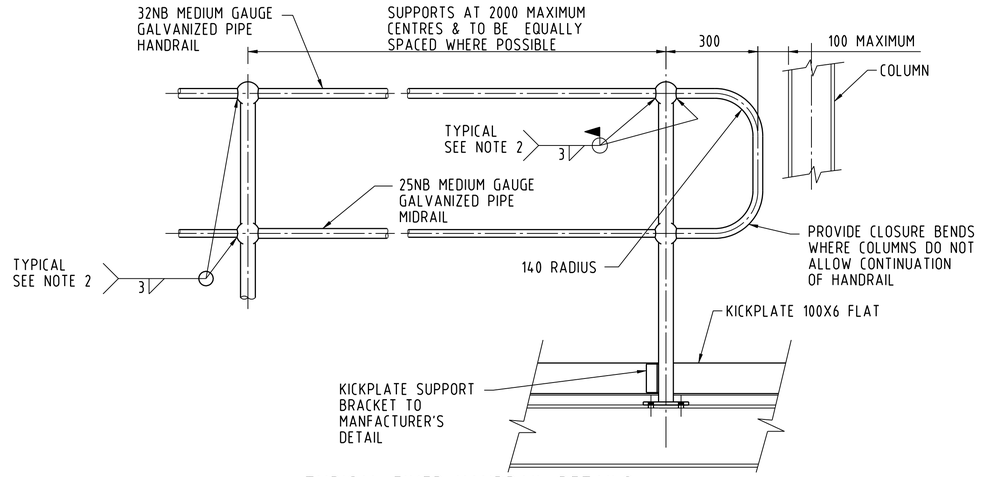


TYPICAL FIXED HANDRAIL DETAILS


FOR GENERAL HANDRAIL REQUIREMENTS ON STAIRS SEE DRAWING MD-101-SMEM-EG-ST-DST-0019

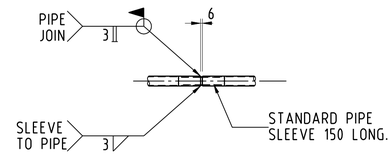

TYPICAL HANDRAIL SPLICE

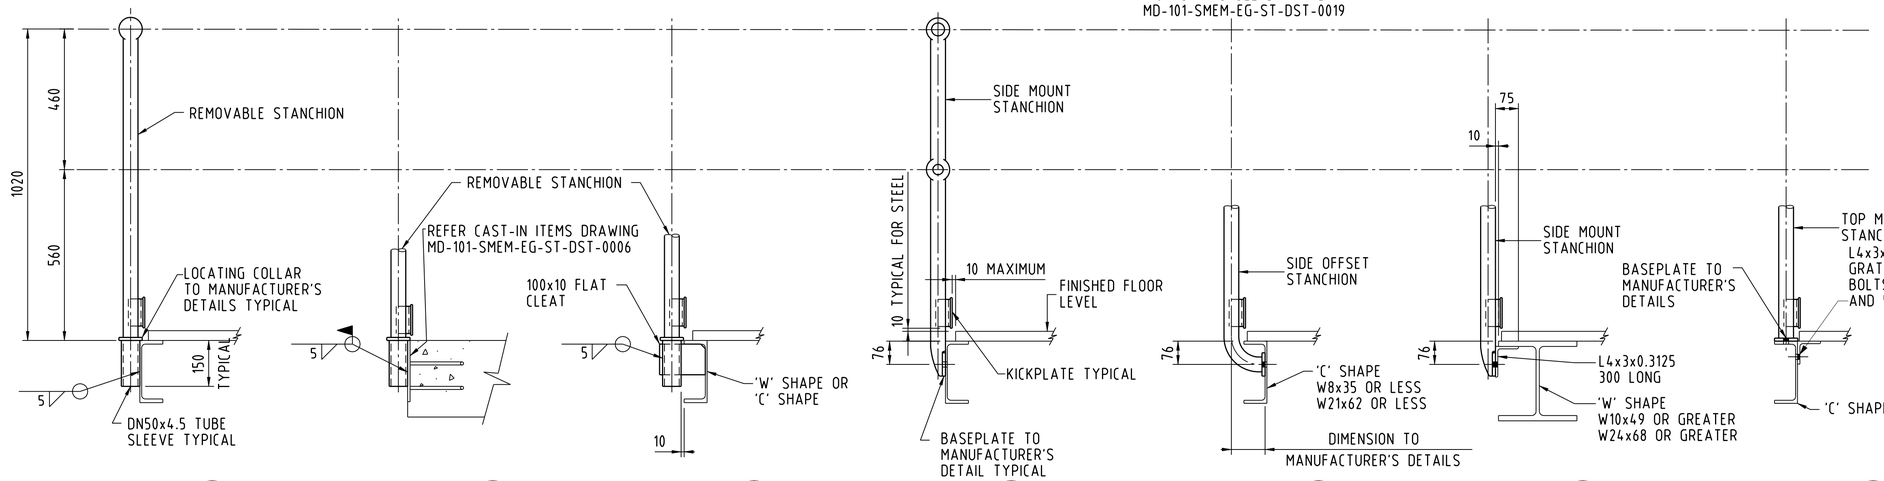

DETAIL 1 – | DETAIL 2 – | DETAIL 3 – | DETAIL 4 – | DETAIL 5 – | DETAIL 6 – | DETAIL 7 –

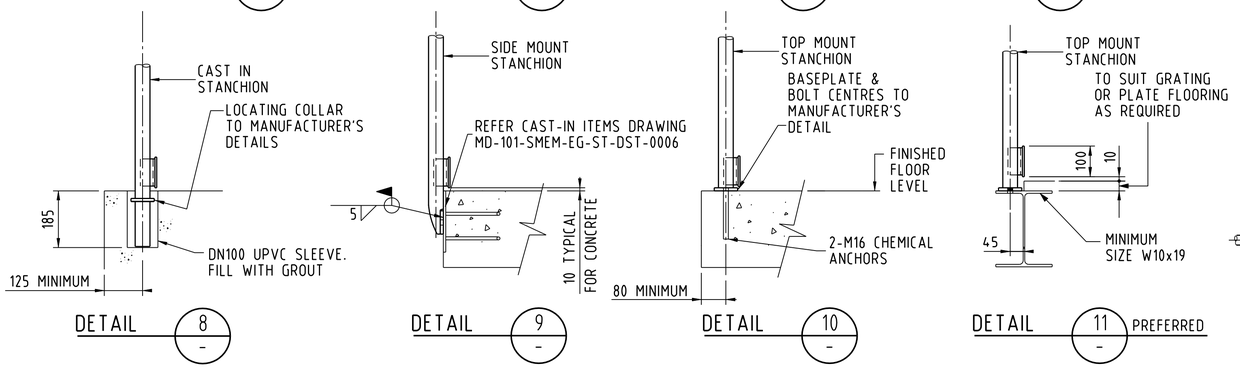

DETAIL 8 – | DETAIL 9 – | DETAIL 10 – | DETAIL 11 – PREFERRED

HANDRAIL CORNER DETAIL TYPICAL

HANDRAIL CORNER DETAIL ALTERNATIVE

NOTES:

1. FOR STEELWORK GENERAL NOTES REFER DRAWING MD-101-SMEM-EG-ST-DST-0009
2. WHENEVER WELDING IS CARRIED OUT AFTER GALVANIZING, MAKE GOOD TO COATING IN ACCORDANCE WITH NOTE 9.3 DRAWING MD-101-SMEM-EG-ST-DST-0009

DOCUMENT NUMBER	REFERENCE DOCUMENTS	REV	DATE	REVISION DESCRIPTION	DRN	CHK	ENG	APP	MD

This drawing and all the information contained herein it is the proprietary property of Ma'aden and is subject to confidentiality restrictions between Ma'aden and the recipent. The information contained herein is provided for a limited purpose and must be returned on request. Ma'aden makes no respresentations or warranties that this information is complete or fit for any particular purpose. Neither this drawing nor any information concerning it may be copied, exhibited or furnished to others. Nor may photographs be taken of any article fabricated or assembled from this drawing, without Ma'aden prior written consent.

REV C01 PREPARED FOR MA'ADEN BY HATCH ASSOCIATES H332701-0000-35-041-0022_C

MA'ADEN معادن Saudi Arabian Mining Company

DRAWN	J BADAL	04.03.11
CHECKED	J EDWARDS	18.04.12
ENGINEER	D KIRKWOOD	18.04.12
APPROVED	R COVELLA	18.04.12
MA'ADEN		
SCALE NTS		A1

MA'ADEN ENGINEERING MANUAL
ALL AREAS
STRUCTURAL STANDARDS
HANDRAIL DETAILS

DRAWING NUMBER MD-101-SMEM-EG-ST-DST-0022 REV C01

$FILE$ $TIME$ $DATE$