
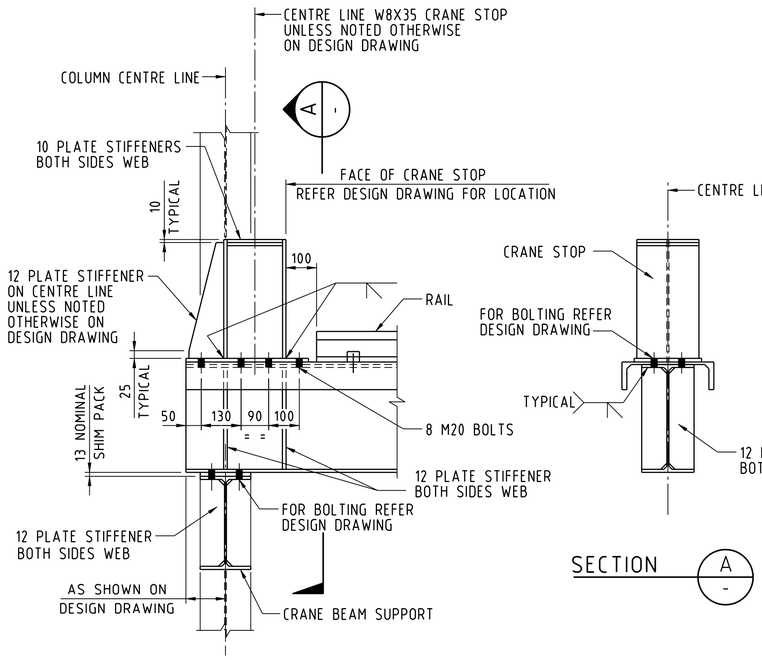


DETAIL 1 -


CRANE BEAM END AND STOP DETAIL

SECTION A -

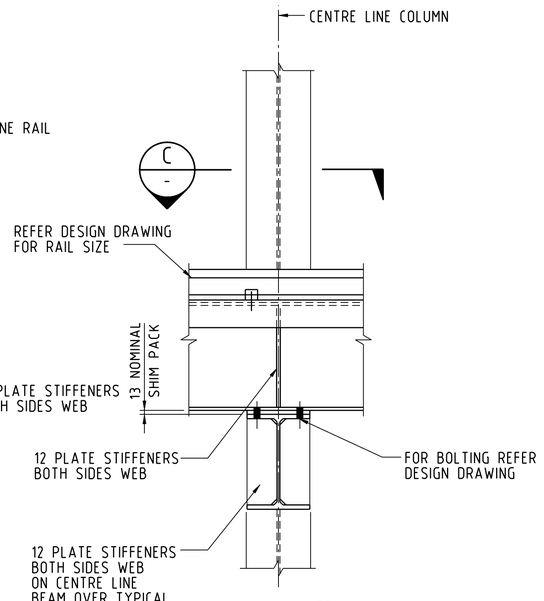


DETAIL 2 -

CONTINUOUS CRANE BEAM

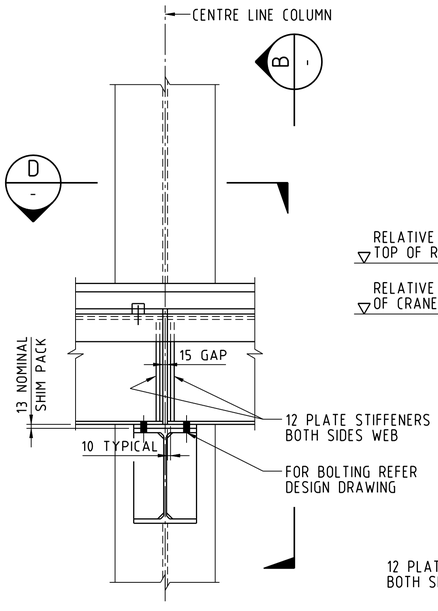


DETAIL 3 -

DISCONTINUOUS CRANE BEAM

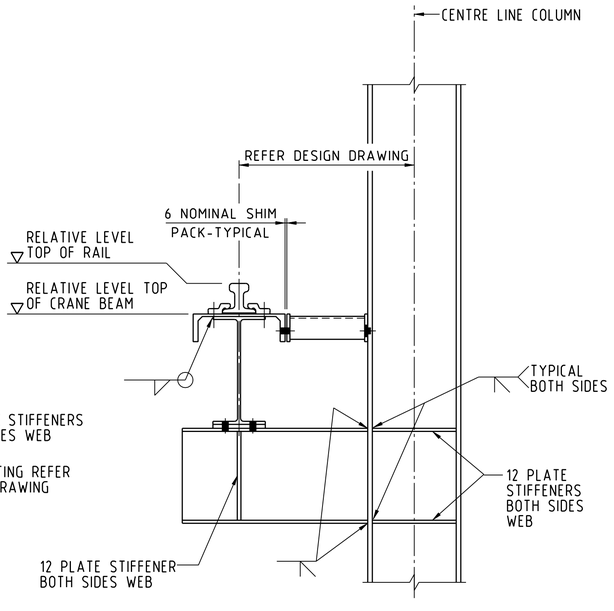

SECTION B -

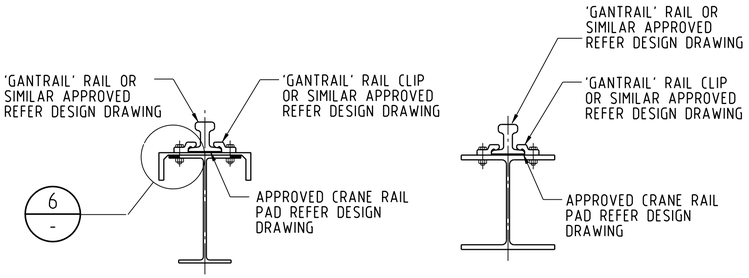


DETAIL 4 -


TYPICAL FIXING TO COMPOSITE CRANE BEAM

DETAIL 5 -

TYPICAL FIXING TO SINGLE SECTION CRANE BEAM

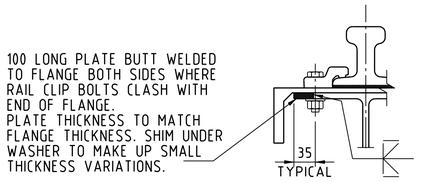


DETAIL 6 1:5 -

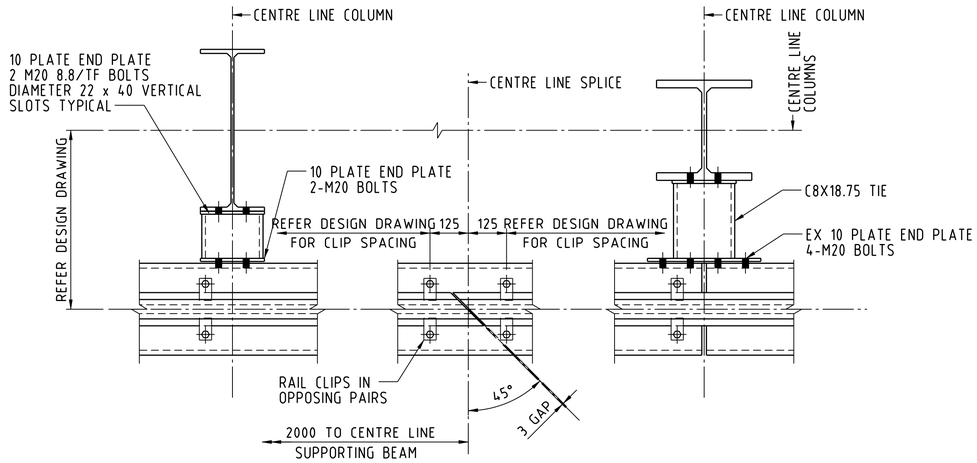

RAIL FIXING AND SPLICE

SECTION C -

SECTION D -

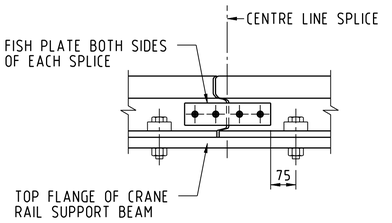

DETAIL 7 1:5 -

RAIL SPLICE WITH FISH PLATE

NOTES:

1. FOR STEELWORK GENERAL NOTES REFER DRAWING MD-101-SMEM-EG-ST-DST-0009.
2. LONGITUDINAL RESTRAINT OF THE CRANE BEAM SHALL BE AS SHOWN ON THE DESIGN DRAWING.
3. RAIL SPLICES SHALL BE BUTT WELDED OR NON WELDED WITH BOLTED FISH PLATES BOTH SIDES. NON WELDED SPLICES SHALL BE 45 DEGREE BEVELLED SPLICES. FISH PLATES SHALL HAVE EXPANSION SLOTS WHERE SHOWN ON THE DESIGN DRAWINGS.
4. ALL DETAILS SHOWN SHALL BE CHECKED BY THE DESIGN ENGINEER.
5. STRUCTURAL CAPACITIES OF THE CONNECTIONS SHOWN ON THIS DRAWING SHALL BE CHECKED BY THE CONTRACTOR TO DETERMINE THEIR SUITABILITY FOR THE INTENDED USE.
6. THIS STANDARD DRAWING MUST BE REFERENCED ON THE DESIGN DRAWING.

DOCUMENT NUMBER	REFERENCE DOCUMENTS	REV	DATE	REVISION DESCRIPTION	DRN	CHK	ENG	APP	MD

This drawing and all the information contained herein it is the proprietary property of Ma'aden and is subject to confidentiality restrictions between Ma'aden and the recipient. The information contained herein is provided for a limited purpose and must be returned on request. Ma'aden makes no respresentations or warranties that this information is complete or fit for any particular purpose. Neither this drawing nor any information concerning it may be copied, exhibited or furnished to others. Nor may photographs be taken of any article fabricated or assembled from this drawing, without Ma'aden prior written consent.

REV C01 PREPARED FOR MA'ADEN BY HATCH ASSOCIATES H332701-0000-35-041-0024_C

MA'ADEN معادن Saudi Arabian Mining Company

DRAWN	J BADAL	04.03.11
CHECKED	J EDWARDS	18.04.12
ENGINEER	D KIRKWOOD	18.04.12
APPROVED	R COVELLA	18.04.12
MA'ADEN		
SCALE NTS		A1

MA'ADEN ENGINEERING MANUAL
ALL AREAS
STRUCTURAL STANDARDS
OVERHEAD CRANE DETAILS

DRAWING NUMBER MD-101-SMEM-EG-ST-DST-0024 REV C01

$DATE$ $TIME$ $FILE$