

MA'ADEN PHOSPHATE PROJECT-A1 BORDER-REV A02

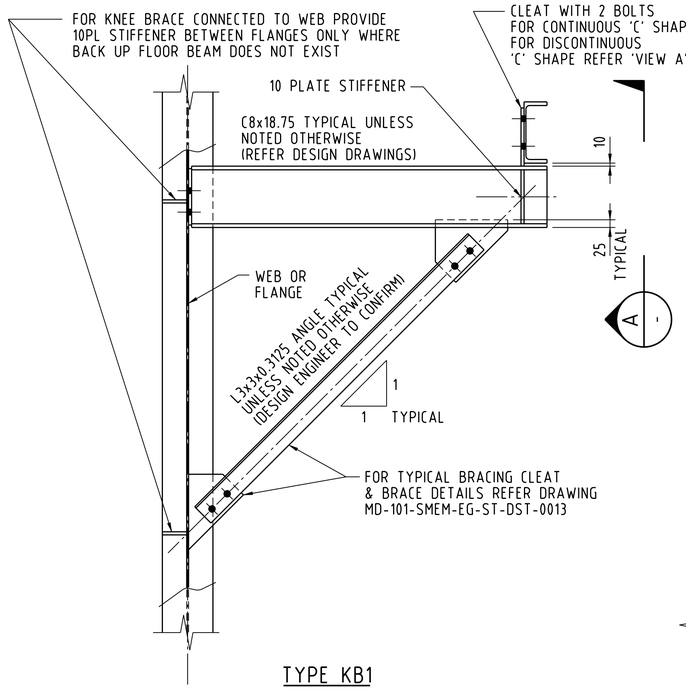


TYPE KB1


CONNECTION TO FLANGE SIMILAR
NO COLUMN STIFFENERS REQUIRED

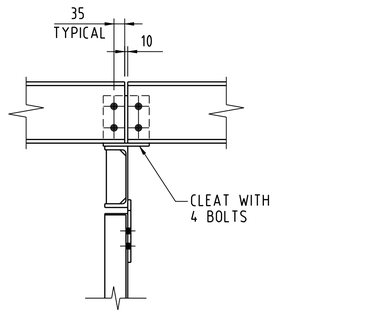


VIEW A - DISCONTINUOUS 'C' SHAPE

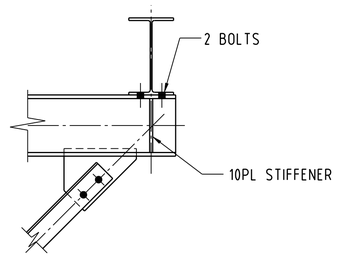


TYPE KB2

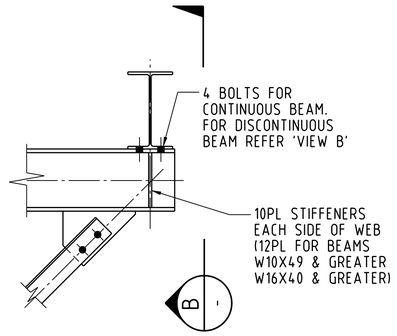


TYPE KB3

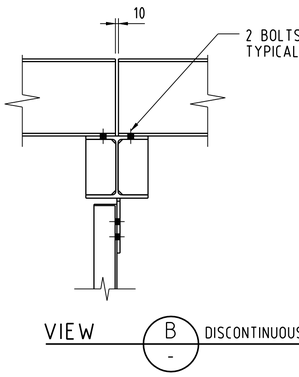


VIEW B - DISCONTINUOUS BEAM

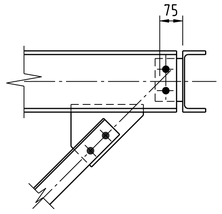


TYPE KB4

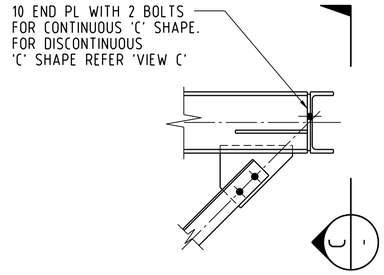


TYPE KB5

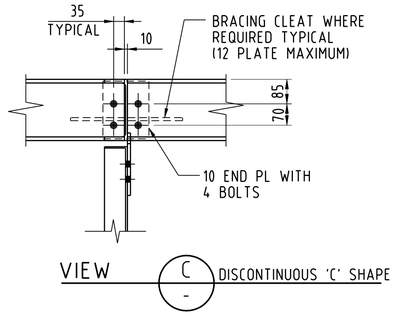

VIEW C - DISCONTINUOUS 'C' SHAPE

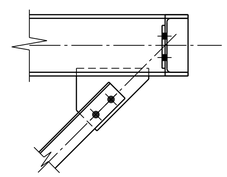

TYPE KB6

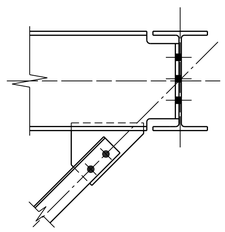

TYPE KB7

KNEE BRACE DETAILS

DETAILS FOR KB2, 3, 4, 5, 6 AND 7
AS FOR KB1 UNLESS NOTED OTHERWISE

LEGEND

KB1/ L3.5X3.5X0.3125 ANGLE
- DENOTES BRACE SIZE (OTHER THAN L3X3X0.3125 ANGLE)
- DENOTES KNEE BRACE TYPE

NOTES:

1. FOR STEELWORK GENERAL NOTE REFER DRAWING MD-101-SMEM-EG-ST-DST-0009

DOCUMENT NUMBER	REFERENCE DOCUMENTS	REV	DATE	REVISION DESCRIPTION	DRN	CHK	ENG	APP	MD

This drawing and all the information contained herein it is the proprietary property of Ma'aden and is subject to confidentiality restrictions between Ma'aden and the recipient. The information contained herein is provided for a limited purpose and must be returned on request. Ma'aden makes no respresentations or warranties that this information is complete or fit for any particular purpose. Neither this drawing nor any information concerning it may be copied, exhibited or furnished to others. Nor may photographs be taken of any article fabricated or assembled from this drawing, without Ma'aden prior written consent.

REV C01 PREPARED FOR MA'ADEN
BY HATCH ASSOCIATES
H332701-0000-35-041-0027_C

MA'ADEN معادن
Saudi Arabian Mining Company

DRAWN	J BADAL	07.03.11
CHECKED	J EDWARDS	18.04.12
ENGINEER	D KIRKWOOD	18.04.12
APPROVED	R COVELLA	18.04.12
MA'ADEN		
SCALE NTS		A1

MA'ADEN ENGINEERING MANUAL
ALL AREAS
STRUCTURAL STANDARDS
KNEE BRACE DETAILS

DRAWING NUMBER MD-101-SMEM-EG-ST-DST-0027 REV C01

$DATE$ $TIME$ $FILE$