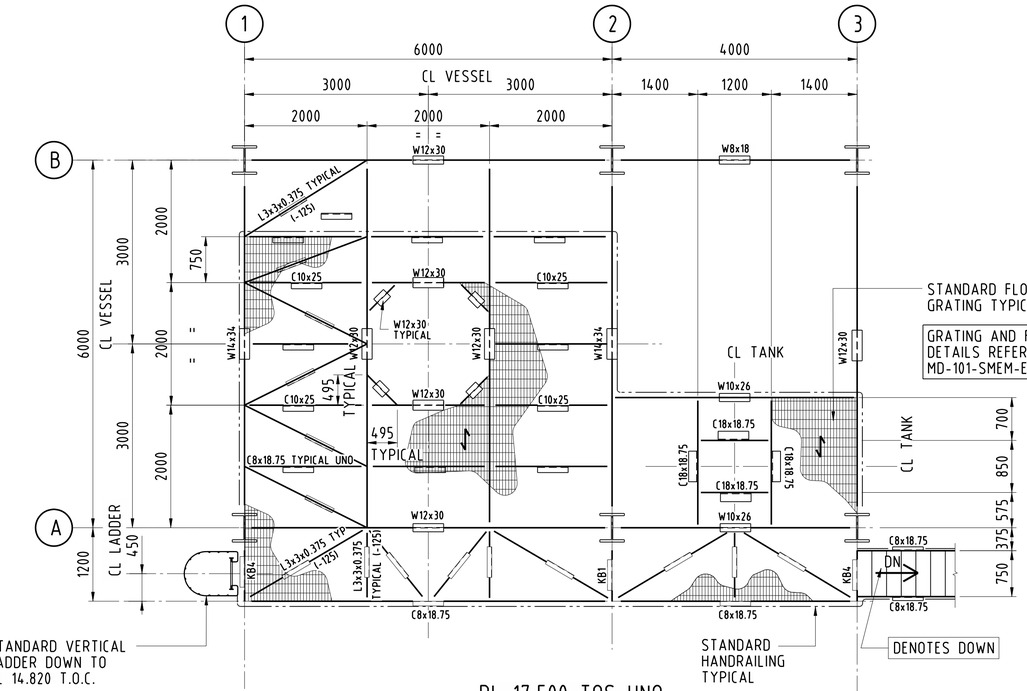


STANDARD FLOOR GRATING TYPICAL

GRATING AND FLOOR PLATE DETAILS REFER STANDARD DRAWING MD-101-SMEM-EG-ST-DST-0023

STANDARD VERTICAL LADDER DOWN TO RL 14.820 T.O.C.

VERTICAL LADDER DETAIL REFER STANDARD DRAWING MD-101-SMEM-EG-ST-DST-0025


STANDARD HANDRAILING TYPICAL

DENOTES DOWN

HANDRAIL DETAILS REFER STANDARD DRAWING MD-101-SMEM-EG-ST-DST-0022

RL 17.500 TOS UNO

SAMPLE ONLY

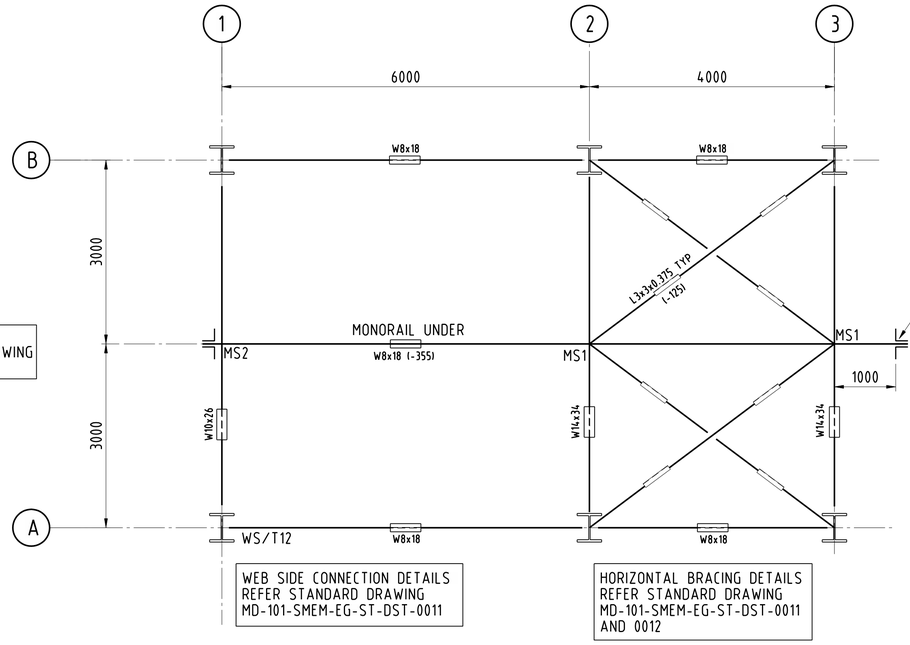

END STOPS BOTH ENDS

WEB SIDE CONNECTION DETAILS REFER STANDARD DRAWING MD-101-SMEM-EG-ST-DST-0011

HORIZONTAL BRACING DETAILS REFER STANDARD DRAWING MD-101-SMEM-EG-ST-DST-0011 AND 0012


RL 21.000 TOS UNO

SAMPLE ONLY

LEGEND:

TOS	TOP OF STEEL
TYP	TYPICAL
U/S	UNDER SIDE
WP	WORK POINT
TOC	TOP OF CONCRETE
RL	RELATIVE LEVEL
CL	CENTRE LINE

PIPE BRACE CONNECTION DETAIL REFER STANDARD DRAWING MD-101-SMEM-EG-ST-DST-0013

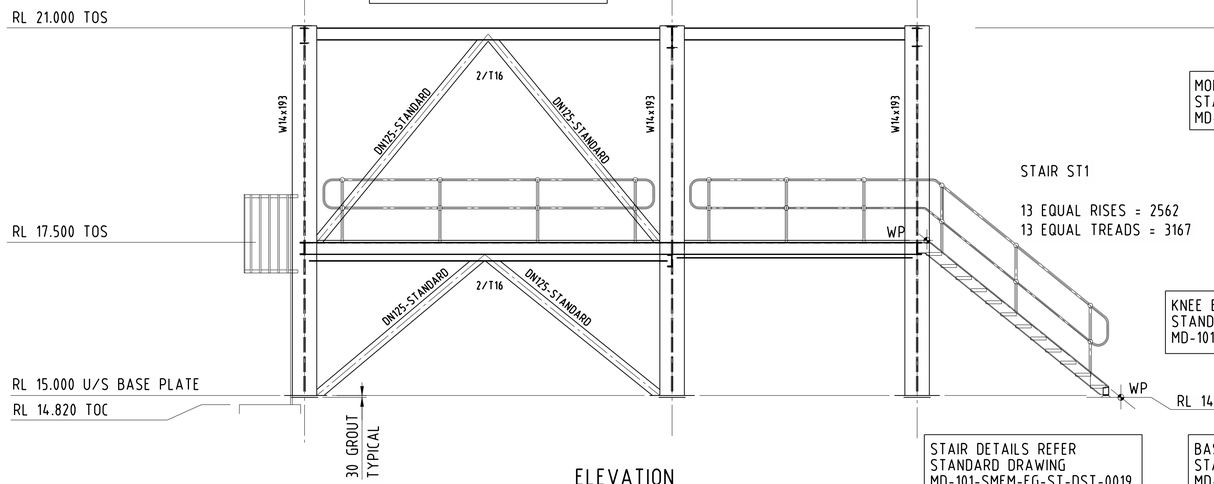

MOMENT CONNECTIONS REFER STANDARD DRAWING MD-101-SMEM-EG-ST-DST-0017


KNEE BRACE DETAILS REFER STANDARD DRAWING MD-101-SMEM-EG-ST-DST-0027

STAIR DETAILS REFER STANDARD DRAWING MD-101-SMEM-EG-ST-DST-0019

BASE PLATE DETAILS REFER STANDARD DRAWING MD-101-SMEM-EG-ST-DST-0014

ELEVATION

SAMPLE ONLY

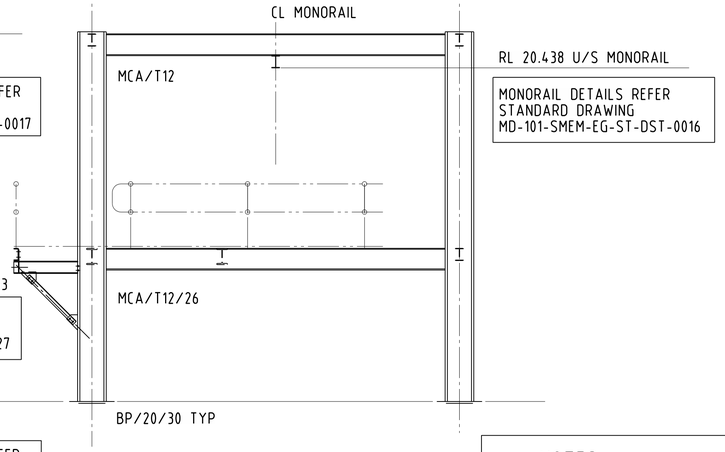

MONORAIL DETAILS REFER STANDARD DRAWING MD-101-SMEM-EG-ST-DST-0016

ELEVATION ON GRID (2)

SAMPLE ONLY

NOTES:

1. FOR STEELWORK GENERAL NOTES REFER DRAWING MD-101-SMEM-EG-ST-DST-0009
2. THIS DRAWING ILLUSTRATES SAMPLE ANNOTATION OF STEELWORK DRAWINGS FOR MA'ADEN PROJECTS. THE DESIGN INFORMATION IS SHOWN ONLY FOR EXAMPLE.

DOCUMENT NUMBER	REFERENCE DOCUMENTS	REV	DATE	REVISION DESCRIPTION	DRN	CHK	ENG	APP	MD

This drawing and all the information contained herein it is the proprietary property of Ma'aden and is subject to confidentiality restrictions between Ma'aden and the recipient. The information contained herein is provided for a limited purpose and must be returned on request. Ma'aden makes no respresentations or warranties that this information is complete or fit for any particular purpose. Neither this drawing nor any information concerning it may be copied, exhibited or furnished to others. Nor may photographs be taken of any article fabricated or assembled from this drawing, without Ma'aden prior written consent.

REV C01 PREPARED FOR MA'ADEN BY HATCH ASSOCIATES H332701-0000-35-041-0025_C

MA'ADEN معادن Saudi Arabian Mining Company

DRAWN	J BADAL	08.03.11
CHECKED	J EDWARDS	18.04.12
ENGINEER	D KIRKWOOD	18.04.12
APPROVED	R COVELLA	18.04.12
MA'ADEN		
SCALE 1:50 UNO		A1

MA'ADEN ENGINEERING MANUAL
ALL AREAS
STRUCTURAL STANDARDS
SAMPLE STEELWORK ANNOTATION

DRAWING NUMBER MD-101-SMEM-EG-ST-DST-0028 REV C01

MA'ADEN PHOSPHATE PROJECT-A1 BORDER-REV A02

$DATE$ $TIME$ $FILE$