DRAWING NUMBER MD-216-2500-EG-CV-GAD-2003 | REV D01

LEGEND AND DESCRIPTION


FGL	FINISH GRADE LEVEL
FFL	FINISH FLOOR LEVEL
SSL	STRUCTURE SLAB LEVEL
CMU	CONCRETE MASONARY UNIT
TOP	TOP OF PARAPET
CH	CEILING HEIGHT
TYP.	TYPICAL
SWL	SIDE WALK LEVEL


LEGEND AND DESCRIPTION

LEGEND OF HATCHES


FINISHES	SAMPLE
COMPACTED FILL	
INSULATED ROOF PANEL	
CONCRETE BEAM AND SLAB	
INTERLOCK PAVER SIDEWALK	

KEY PLAN

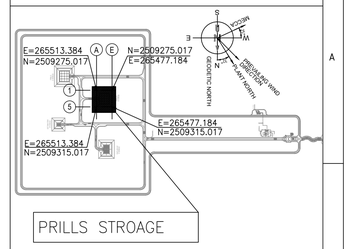


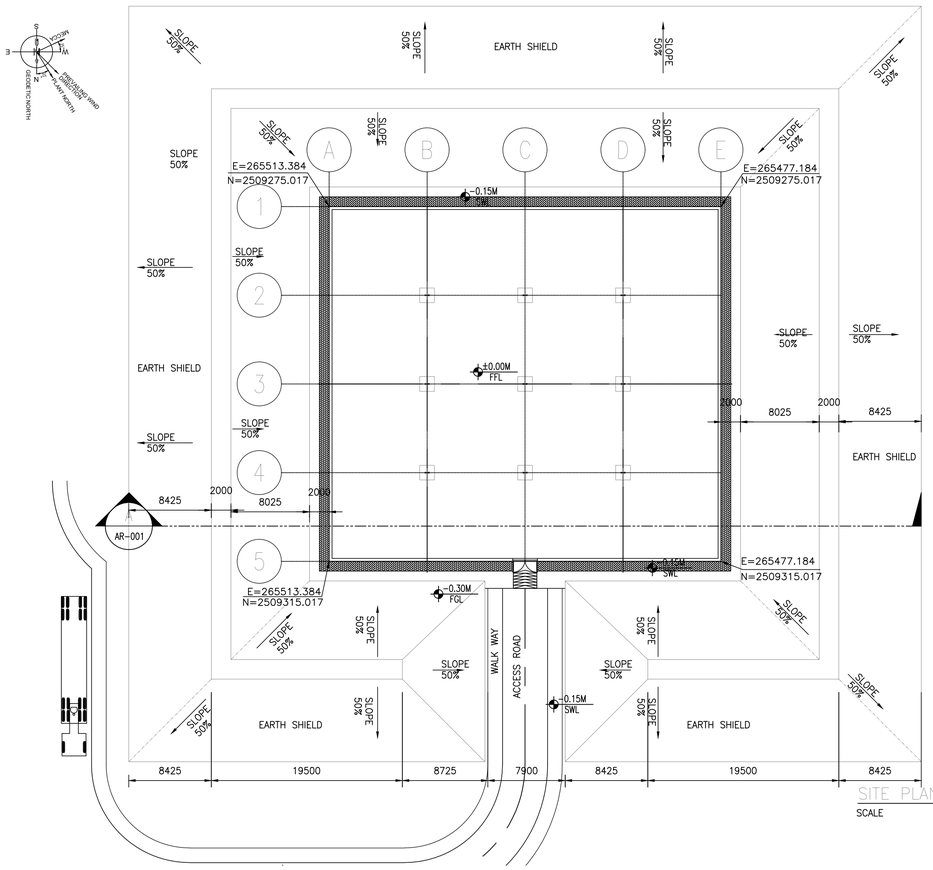

SITE PLAN — SCALE 1:300 — 1

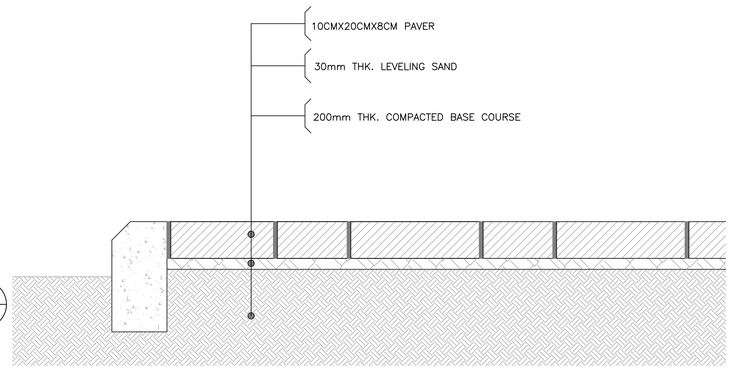

ENLARGED SECTION — SCALE 1:8 — 3

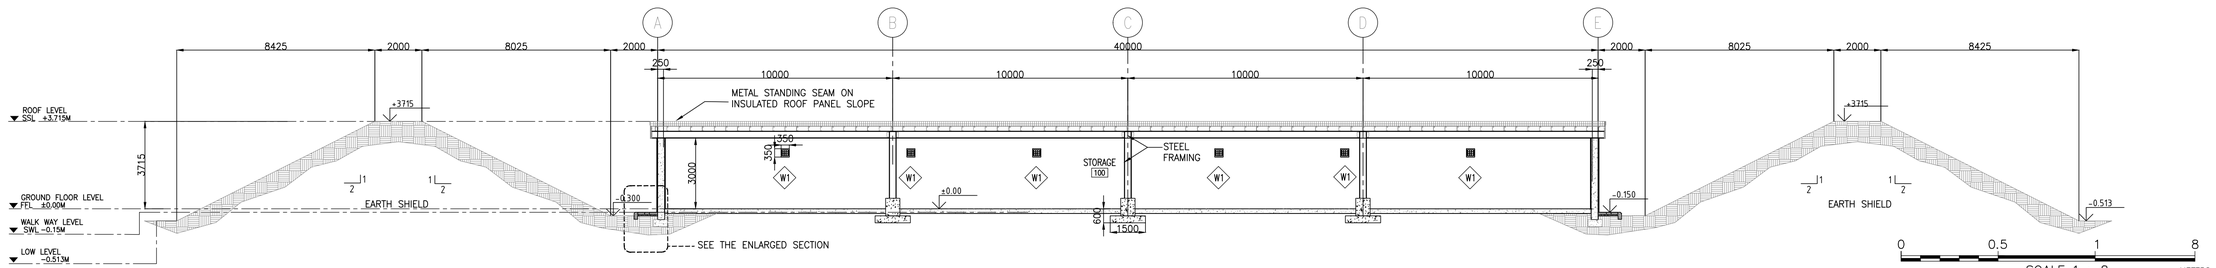

CROSS SECTION-A — SCALE 1:125 — 2

SCALE 1 : 8 METERS

SCALE 1 : 125 METERS

SCALE 1 : 300 METERS

REV	REFERENCE DOCUMENTS	DATE	REVISION DESCRIPTION	DRN	CHK	ENG	APP	EMP
D01		13/06/2023	AS- BUILT	--	SNM	--	SJM	
C01		07/12/2020	ISSUED FOR CONSTRUCTION	--	SNM	--	SJM	
A02		02/11/2020	REVISED AS PER EMPLOYER COMMENTS ON 26/08/2020	--	SNM	--	SJM	
A01	PRILLS STORAGE SITE PLAN VIEW	01/08/2020	ISSUED FOR APPROVAL	--	SNM	--	SJM	
DOCUMENT NUMBER	MD-216-2500-EG-AR-LAD-2001							

ADVACON

DRAWING NUMBER MD-216-1800-EG-CV-DDE-1014 | REVISION C01

DATE	5/12/2020	DATE	6/12/2020	DATE	7/12/2020
DRAWN	ABDUL	CHECKED	LARA	APPROVED	IHAB

LARSEN & TOUBRO DRAWING NUMBER 019045_900_C_G_24453_001 | REVISION 3

OUTOTEC DRAWING NUMBER 900707__GAU01__ZZ01__MTL01__25007 | DOCUMENT ID OU100691787 | REVISION 3

LARSEN & TOUBRO

This drawing is the property of *LARSEN & TOUBRO* and must not be passed on to any person or body not authorized by us to receive it nor be copied or otherwise made use either in full or in part by such person or body without our prior permission in writing.

Outotec

The content of these documents are the sole property of Outotec Oyj. Any rights not expressly granted herein are reserved. Reproduction, transfer or distribution of part or all of the contents in any form without prior written permission of Outotec is prohibited.

MA'ADEN معادن
Saudi Arabian Mining Company شركة التعدين العربية السعودية

This document and the information contained herein is Ma'aden proprietary know-how. This document or any part thereof should not be reproduced, stored in a retrieval system or transmitted by any means, electronic or otherwise, or divulged without prior written permission of Ma'aden.

DRAWN	--	--
CHECKED	SNM	31/07/2020
ENGINEER	--	--
APPROVED	SJM	01/08/2020
EMPLOYER		
SCALE	1:300	A1

MANSOURAH - MASSARAH GOLD PROJECT
GENERAL ARRANGMENT
EXPLOSIVE MAGAZINE
PRILLS STORAGE WALKWAY DETAILS

DRAWING NUMBER MD-216-2500-EG-CV-GAD-2003 | REV D01