

DRAWING NUMBER MD-216-3210-EG-CV-GAD-1002 | REV D01

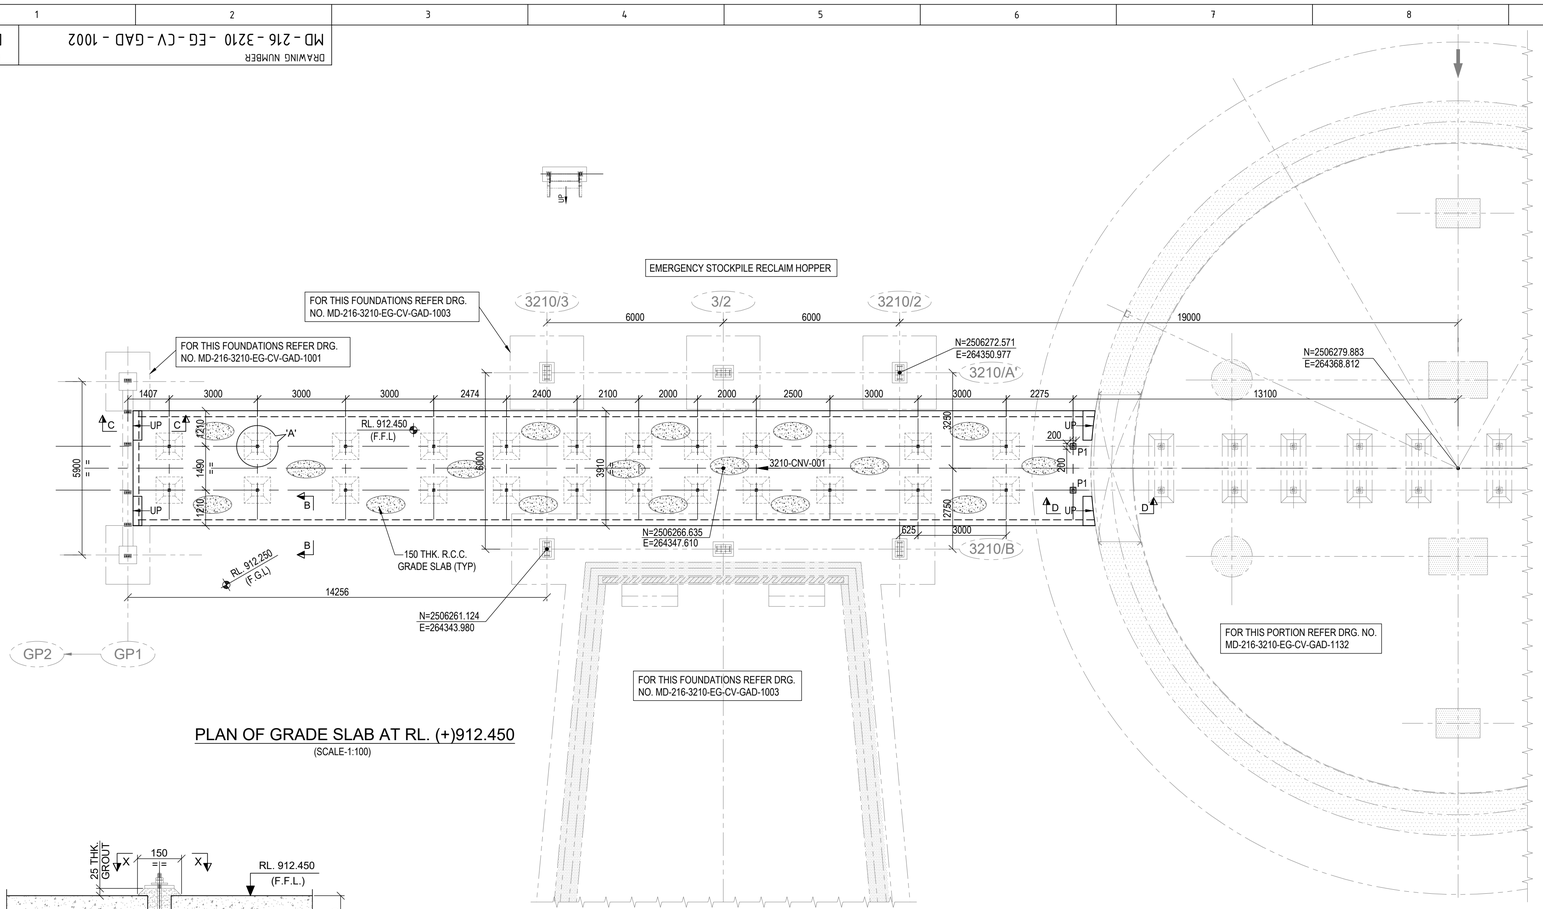


PLAN OF GRADE SLAB AT RL. (+)912.450

(SCALE-1:100)

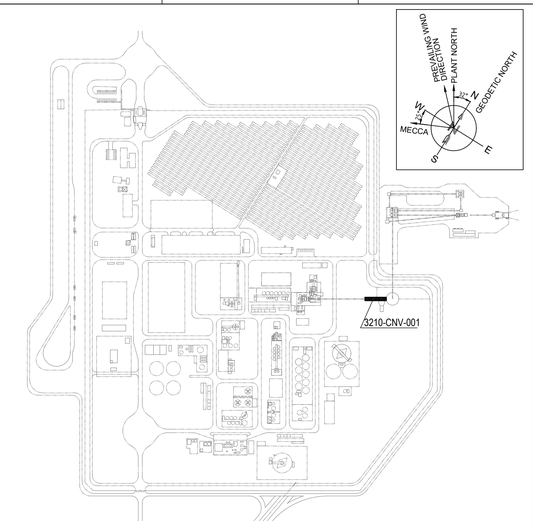

KEY PLAN

SCALE–(1:1000)

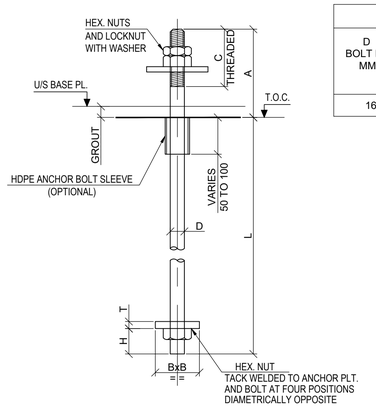

TYP. DETAIL OF BOLT


(SCALE-1:20)

SCHEDULE OF BOLTS

D BOLT DIA. MM	BxB BOTTOM PLATE (SQUARE) SQ MM	DIMENSIONS (MM)				
		L	A	C	T	H
16	50x50	350	120	100	10	30


LEGENDS :-

R.L. - REDUCED LEVEL
℄ - CENTRE LINE
CJ - CONSTRUCTION JOINT
FDN. - FOUNDATION.
T.O.C. - TOP OF CONCRETE.
F.G.L. - FINISHED GROUND LEVEL.
F.F.L. - FINISHED FLOOR LEVEL.
B.O.F. - BOTTOM OF FOUNDATION
TYP. - TYPICAL.
R.C.C - REINFORCED CEMENT CONCRETE
P.C.C - PLAIN CEMENT CONCRETE
MKD. - MARKED.
THK. - THICK
NTS. - NOT TO SCALE

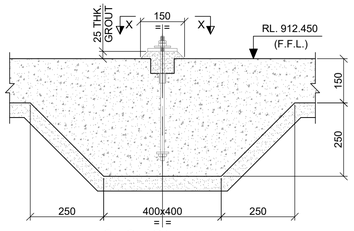


SECTION A1-A1

(SCALE 1:10)

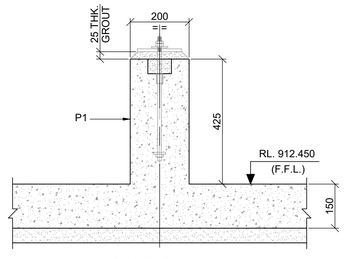


SECTION A-A

(SCALE 1:10)

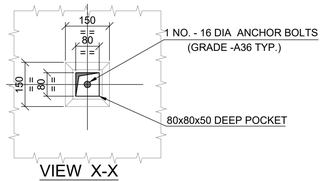


VIEW X-X

(SCALE 1:10)

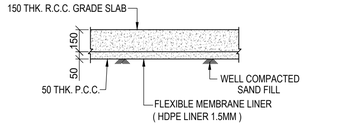


TYP. DETAIL OF 150 THK. GRADE SLAB

SCALE 1:20

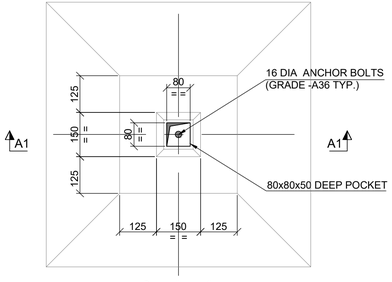


DETAIL 'A'

(SCALE 1:10)

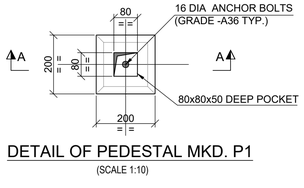


DETAIL OF PEDESTAL MKD. P1

(SCALE 1:10)

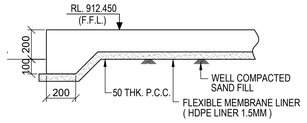


SECTION B-B

(SCALE-1:20)

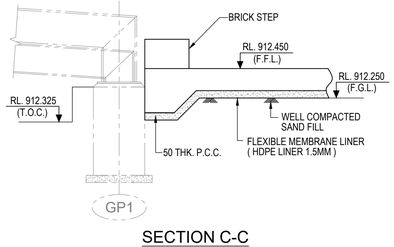

SECTION C-C

(SCALE-1:20)

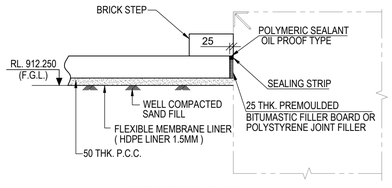

SECTION D-D

(SCALE-1:20)

NOTES :-

1. ALL DIMENSIONS ARE IN MILLIMETRES AND LEVELS AND CO-ORDINATES ARE IN METRES. UNLESS OTHERWISE STATED.
2. GRADE OF CONCRETE SHALL BE C35 FOR FOUNDATION.
3. GRADE OF REINFORCEMENT SHALL BE DEFORMED BAR ASTM A615 - GRADE 60 (fy = 420 MPa).
4. NET SAFE BEARING CAPACITY OF SOIL AT BOTTOM OF FOUNDATION CONSIDERED 500KN/ SQ. M.
5. CLEAR COVER TO MAIN REINFORCEMENT SHALL BE AS
   a) FOUNDATION = 75 mm (BOTTOM & SIDE) 50 mm. (TOP)
   b) COLUMN & PEDESTAL = 50mm
   c) BEAM = 50mm
   d) SLAB = 40mm
6. FOR MINIMUM LAP LENGTH OF REINFORCEMENT AND OTHER GENERAL NOTES FOR CIVIL WORKS REFER STANDARD DRG : MD-216-1000-EG-CV-DED-1001
7. THIS DRG. SHALL BE READ IN CONJUNCTION WITH DRG. NO. MD-216-3210-EG-CV-DED-1002
8. ALL STRUCTURAL WORK SHALL CONFORM TO CIVIL STRUCTURAL DESIGN CRITERIA NO. MD - 216 - 1000 -EG -ST - CRT - 1001
9. FOR OTHER STANDARD REINFORCEMENT DETAILS REFER DRG : MD-216-1000-EG-CV-DED-1005

DOCUMENT NUMBER	REFERENCE DOCUMENTS	REV	DATE	REVISION DESCRIPTION	DRN	CHK	ENG	APP	EMP
MD-216-3210-EG-CV-GAD-1132	GRINDING & CLASSIFICATION								
	CRUSHED ORE STORAGE BIN - LAYOUT & DETAIL								
MD-216-3210-EG-CV-GAD-1001	GA OF CONVEYOR 3210-CNV-001 LAYOUT & DETAIL								
MD-216-3210-EG-CV-GAD-1003	G&C-EMERGENCY STOCKPILE RECLAIM HOPPER								
	FDN. & RAMP PLAN, ELEVATIONS & DETAILS	D01	31/05/2023	AS - BUILT	JKM	SBY	APL	PRI	
MD-216-3210-EG-ME-LPX-1001	GRINDING & CLASSIFICATION	C01	28/12/2020	ISSUED FOR CONSTRUCTION	JKM	SBY	APL	PRI	
	CONV.3210-CNV-001 - PLAN VIEW	A01	17/11/2020	ISSUED FOR REVIEW	JKM	SBY	APL	PRI	

RESERVED FOR VENDOR LOGO AND DRAWING NUMBER

LARSEN & TOUBRO
This drawing is the property of LARSEN & TOUBRO and must not be passed on to any person or body not authorized by us to receive it nor be copied or otherwise made use either in full or in part by such person or body without our prior permission in writing.

Outotec
The content of these documents are the sole property of Outotec Oyj. Any rights not expressly granted herein are reserved. Reproduction, transfer or distribution of part or all of the contents in any form without prior written permission of Outotec is prohibited.

MA'ADEN معادن
Saudi Arabian Mining Company شركة معادن العربية السعودية
This document and the information contained herein is Ma'aden proprietary know-how. This document or any part thereof should not be reproduced, stored in a retrieval system or transmitted by any means, electronic or otherwise, or divulged without prior written permission of Ma'aden.

LARSEN & TOUBRO DRAWING NUMBER	O19045_450_C_G_24570_001	REVISION 2
OUTOTEC DRAWING NUMBER	900707__GAU01__US01__MTL01__32149	DOCUMENT ID OU100706079 / REVISION 2

DRAWN	JKM	13/11/2020
CHECKED	SBY	16/11/2020
ENGINEER	APL	11/11/2020
APPROVED	PRI	17/11/2020
EMPLOYER		
SCALE	1:50,25	A1

MANSOURAH - MASSARAH GOLD PROJECT
GENERAL ARRANGEMENT DRAWING
GA OF CONVEYOR 3210 CNV-001
GRADE SLAB LAYOUT & DETAIL

DRAWING NUMBER MD-216-3210-EG-CV-GAD-1002 | REV D01