


DRAWING NUMBER MD-216-3310-EG-CV-GAD-1173 | REV D01

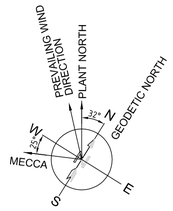

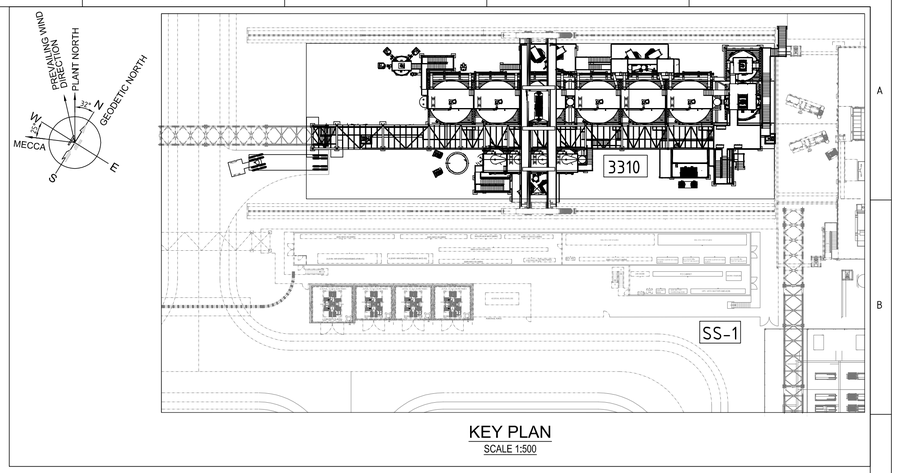

KEY PLAN
SCALE 1:500

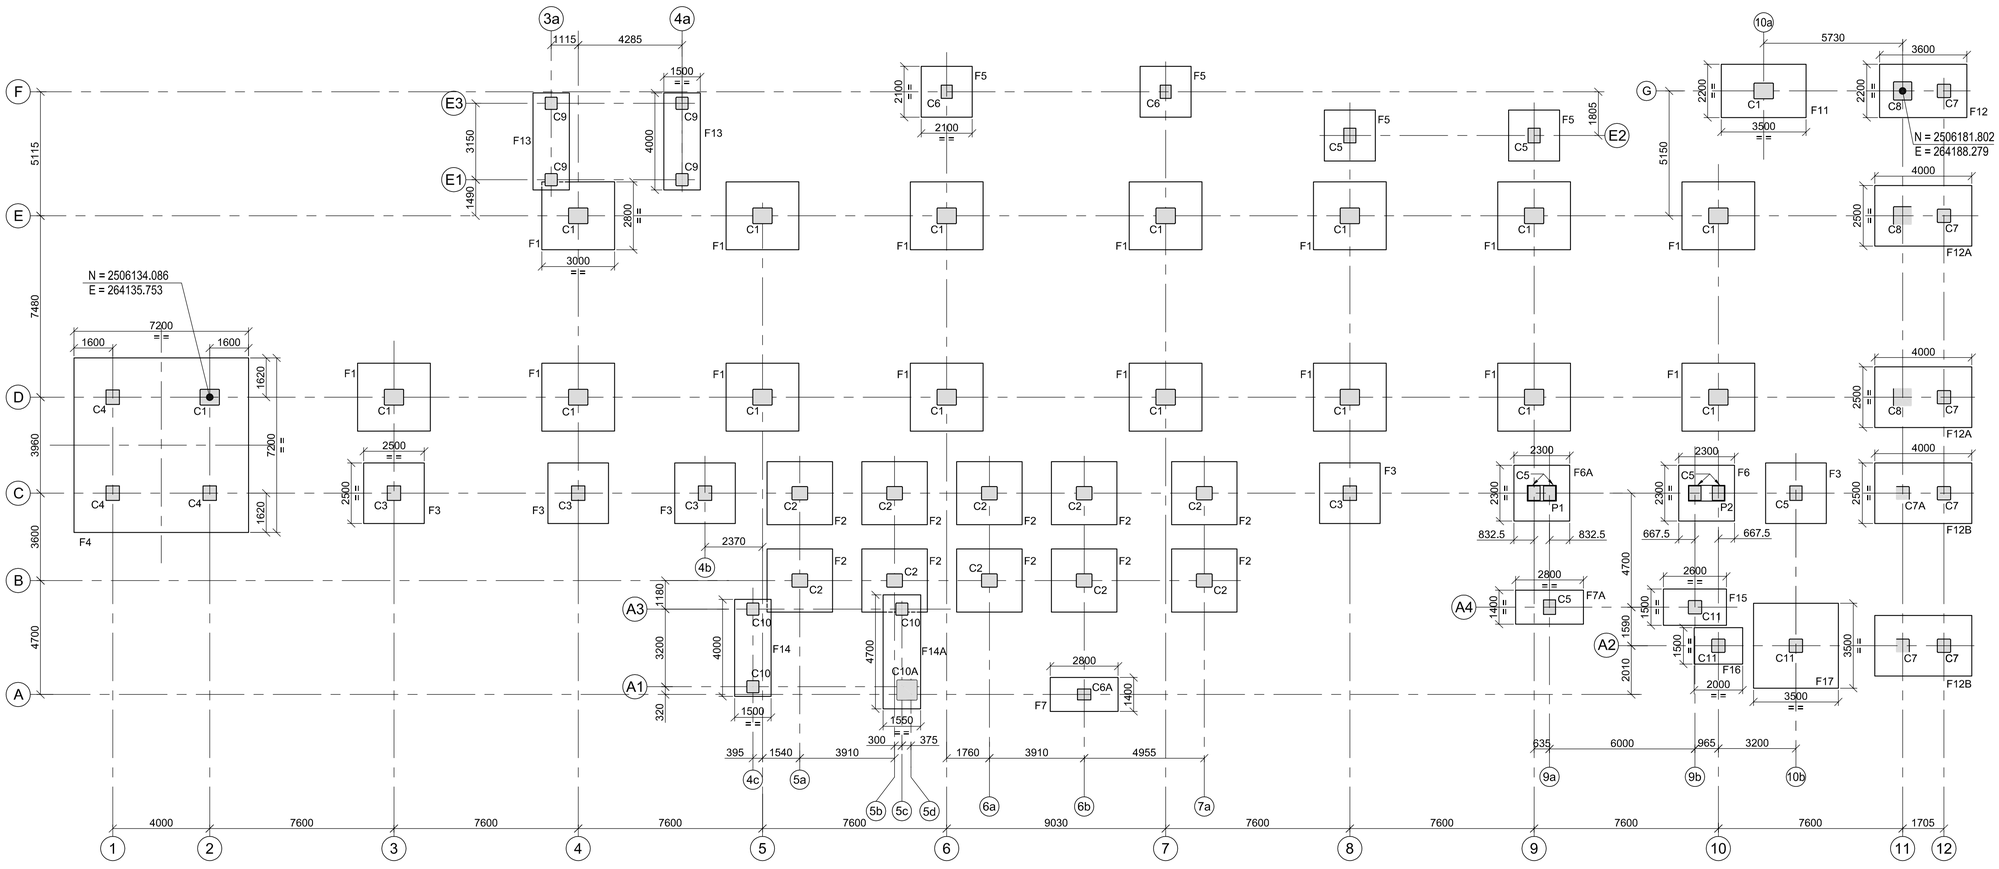

LAYOUT OF FOUNDATION
SCALE 1:125

LEGEND :-

R L - REDUCED LEVEL
T O G - TOP OF GROUT
CJ - CONSTRUCTION JOINT
F G L - FINISHED GROUND LEVEL

NOTES:-

1. ALL DIMENSIONS ARE IN MILLIMETRES AND LEVELS AND CO-ORDINATES ARE IN METRES UNLESS OTHERWISE STATED.
2. NET SAFE BEARING CAPACITY OF SOIL AT BOTTOM OF FOUNDATION CONSIDER 450KN/ SQ. M
3. IF ANY PART OF FOUNDATION COMES ON BACKFILL ZONE OF ADJACENT FOUNDATION OR ANY LOOSE SOIL ARE ENCOUNTERED BELOW FOUNDATION LEVEL THE SAME SHALL BE REMOVED AND FILLED WITH PCC (C15).
4. THE CONTENT OF THIS DRAWING SHALL CONFORM TO THE PROVISIONS OF CIVIL, STRUCTURAL AND ARCHITECTURAL DESIGN CRITERIA DOC. NO. MD-216-1000-EG-ST-CRT-1001.

DOCUMENT NUMBER	REFERENCE DOCUMENTS	REV	DATE	REVISION DESCRIPTION	DRN	CHK	ENG	APP	EMP
MD-216-3310-EG-CV-GAD-1176	DETAIL OF FOUNDATION	D01	29/06/2023	AS - BUILT	ABS	SJM	AVG	AG	
MD-216-3310-EG-CV-GAD-1175	DETAIL OF FOUNDATION	C03	06/01/2021	ISSUED FOR CONSTRUCTION	ABS	SJM	AVG	AG	
MD-216-3310-EG-CV-GAD-1174	DETAIL OF FOUNDATION	C02	07/04/2020	ISSUED FOR APPROVAL & REVISED AS MKD. (2)	AMT/JYM	BDA/AVG	SML/MMJ	AG	
MD-216-3310-EG-CV-GAD-1178	DETAILS OF MISCELLANEOUS FOUNDATION	C01	10/02/2020	ISSUED FOR CONSTRUCTION & REVISED AS MKD. (1)	ABS	SJM	AVG	AG	
MD-216-3310-EG-ST-GAD-2163	ROUGHER AND SCAVENGER FLOTATION	A01	14/02/2020	ISSUED FOR REFERENCE	ABS	SJM	AVG	AG	

RESERVED FOR VENDOR LOGO AND DRAWING NUMBER

LARSEN & TOUBRO

This drawing is the property of LARSEN & TOUBRO and must not be passed on to any person or body not authorized by us to receive it nor be copied or otherwise made use either in full or in part by such person or body without our prior permission in writing.

Outotec

The content of these documents are the sole property of Outotec Oyj. Any rights not expressly granted herein are reserved. Reproduction, transfer or distribution of part or all of the contents in any form without prior written permission of Outotec is prohibited.

MA'ADEN معادن
Saudi Arabian Mining Company شركة المعادن العربية السعودية

This document and the information contained herein is Ma'aden proprietary know-how. This document or any part thereof should not be reproduced, stored in a retrieval system or transmitted by any means, electronic or otherwise, or divulged without prior written permission of Ma'aden.

LARSEN & TOUBROW DRAWING NUMBER: 019045_450_C_G_24083_001 | REVISION: 4
OUTOTEC DRAWING NUMBER: 900707__GAU01__ZF01__MTL01__33128 | DOCUMENT ID: OU100665308 | REVISION: 4

DRAWN	ABS	11/02/2020
CHECKED	SJM	13/02/2020
ENGINEER	AVG	11/02/2020
APPROVED	AG	14/02/2020
EMPLOYER		
SCALE	1:125	A1

MANSOURAH - MASSARAH GOLD PROJECT
GENERAL ARRANGEMENT DRAWING
ROUGHER AND SCAVENGER FLOTATION
LAYOUT & DETAIL OF FOUNDATION

DRAWING NUMBER: MD-216-3310-EG-CV-GAD-1173 | REV: D01