


DRAWING NUMBER MD-216-3310-EG-CV-GAD-1175 REV D01

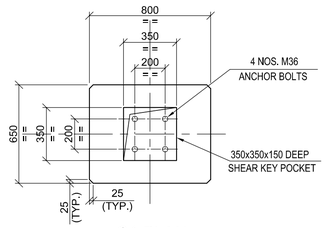


C1 PLAN
SCALE 1:20

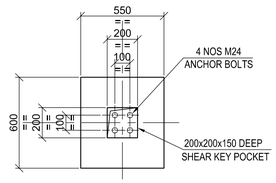


C3 PLAN
SCALE 1:20

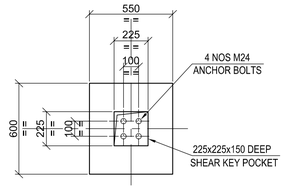


C4 PLAN
SCALE 1:20

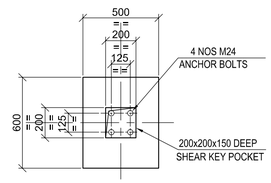


C5 PLAN
SCALE 1:20

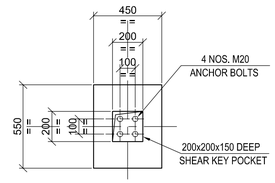


C6,C6A & C6B PLAN
SCALE 1:20

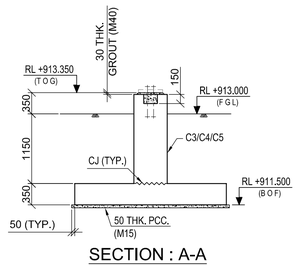


SECTION : A-A
SCALE 1:50

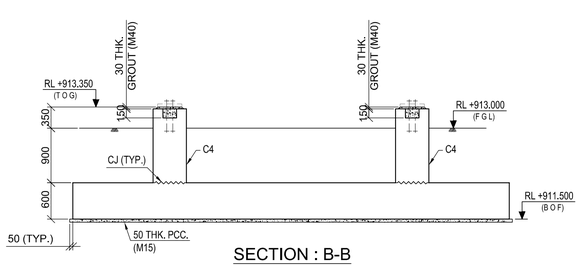


SECTION : B-B
SCALE 1:50

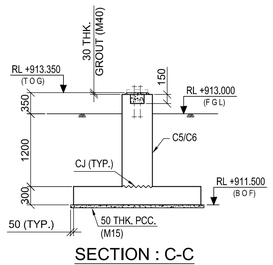


SECTION : C-C
SCALE 1:50

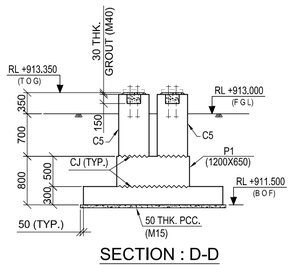


SECTION : D-D
SCALE 1:50

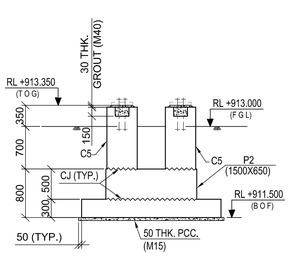


SECTION : E-E
SCALE 1:50

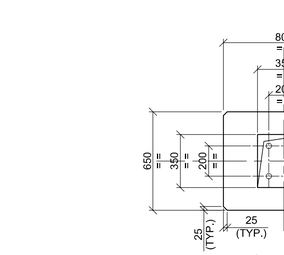


PLAN OF FOUNDATION
MKD. F3
(5 NOS. REQD.)
SCALE 1:50

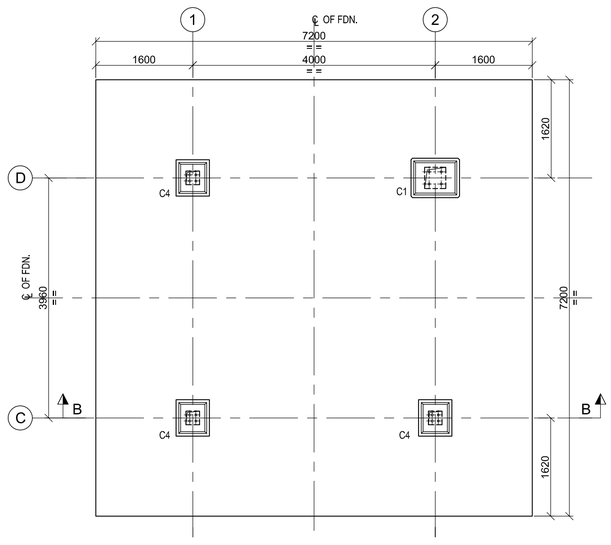


PLAN OF FOUNDATION
MKD. F4
(1 NOS. REQD.)
SCALE 1:50

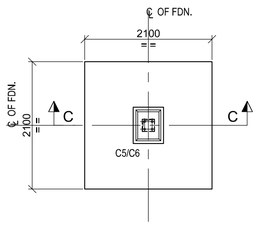

PLAN OF FOUNDATION
MKD. F5
(4 NOS. REQD.)
SCALE 1:50

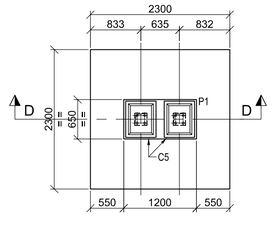

PLAN OF FOUNDATION
MKD. F6A
(1 NOS. REQD.)
SCALE 1:50

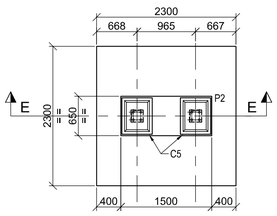

PLAN OF FOUNDATION
MKD. F6
(1 NOS. REQD.)
SCALE 1:50

LEGEND :-

R L - REDUCED LEVEL
T O G - TOP OF GROUT
CJ - CONSTRUCTION JOINT
F G L - FINISHED GROUND LEVEL
P C C - PLAIN CEMENT CONCRETE
FDN. - FOUNDATION
B O F - BOTTOM OF FOUNDATION

NOTES:-

1. FOR DETAIL OF ANCHOR BOLTS, REFER DRAWING NO. MD-216-1000-EG-CV-DED-1003.
2. FOR ALL OTHER NOTES, REFER DRAWING NO. MD-216-3310-EG-CV-GAD-1173. MD-216-3310-EG-CV-GAD-1174. MD-216-3310-EG-CV-GAD-1176. MD-216-1000-EG-CV-DED-1005.

REV	DATE	REVISION DESCRIPTION	DRN	CHK	ENG	APP	EMP
D01	29/06/2023	AS - BUILT	ABS	SJM	AVG	AG	
C02	18/01/2021	ISSUED FOR CONSTRUCTION & REVISED AS MKD. C02	ABS	SJM	AVG	AG	
C01	28/04/2020	ISSUED FOR CONSTRUCTION & REVISED AS PER EMPLOYER'S COMMENTS ON 24/04/2020 & REVISED AS MKD. C01	AMT	BDA	SML	AG	
A01	02/03/2020	ISSUED FOR REFERENCE	AMT	BDA	SML	AG	

MD-216-3310-EG-ST-GAD-2163 | ROUGHER AND SCAVENGER FLOTATION

RESERVED FOR VENDOR LOGO AND DRAWING NUMBER

LARSEN & TOUBRO

This drawing is the property of LARSEN & TOUBRO and must not be passed on to any person or body not authorized by us to receive it nor be copied or otherwise made use either in full or in part by such person or body without our prior permission in writing.

Outotec

The content of these documents are the sole property of Outotec Oyj. Any rights not expressly granted herein are reserved. Reproduction, transfer or distribution of part or all of the contents in any form without prior written permission of Outotec is prohibited.

MA'ADEN معادن
Saudi Arabian Mining Company شركة التعدين العربية السعودية

This document and the information contained herein is Ma'aden proprietary know-how. This document or any part thereof should not be reproduced, stored in a retrieval system or transmitted by any means, electronic or otherwise, or divulged without prior written permission of Ma'aden.

LARSEN & TOUBRO DRAWING NUMBER: 019045_450_C_G_24083_003 | REVISION: 3
OUTOTEC DRAWING NUMBER: 900707 _ GAU01 _ ZF01 _ MTL01 _ 33130 | DOCUMENT ID: OU100665310 | REVISION: 3

DRAWN	AMT	28/02/2020
CHECKED	BDA	29/02/2020
ENGINEER	SML	28/02/2020
APPROVED	AG	02/03/2020
EMPLOYER		
SCALE	1:20, 1:50	A1

MANSOURAH - MASSARAH GOLD PROJECT
GENERAL ARRANGEMENT DRAWING
ROUGHER AND SCAVENGER FLOTATION
LAYOUT & DETAIL OF FOUNDATION

DRAWING NUMBER: MD-216-3310-EG-CV-GAD-1175 | REV: D01