

DRAWING NUMBER: MD-216-3220-EG-CV-GAD-1001 REV A03

LEVEL +913.000
1:50

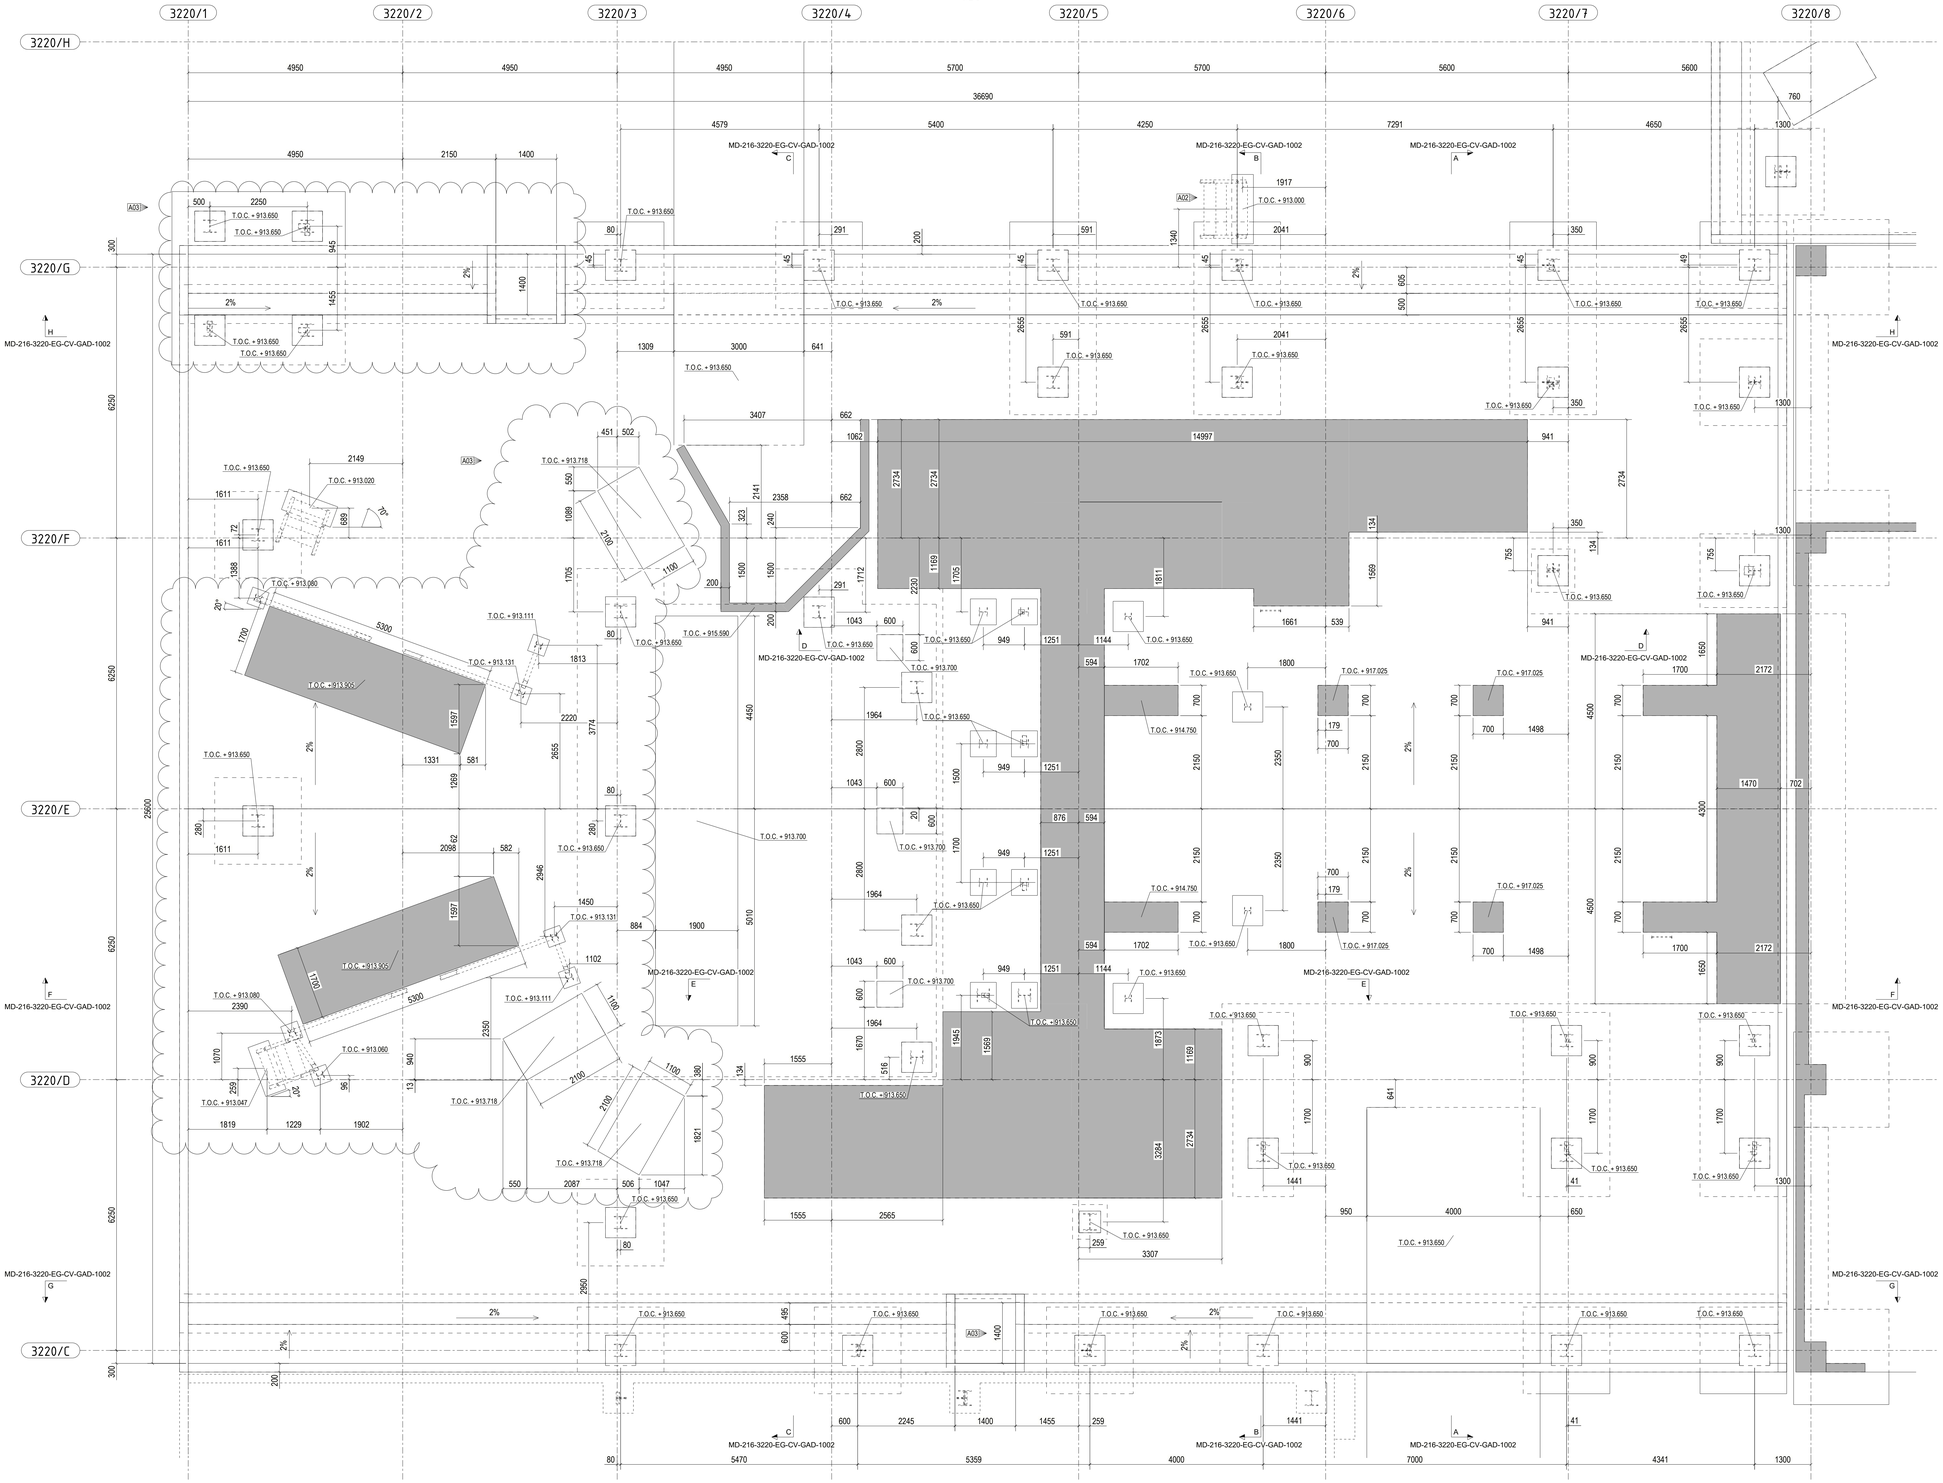

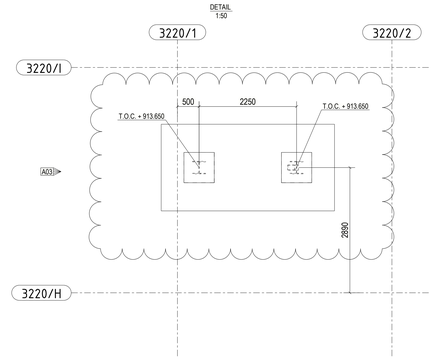

SECTIONS A-A TO H-H ARE SHOWN ON DRAWING MD-216-3220-EG-CV-GAD-1002


THIS DESIGN IS NOT ISSUED FOR CONSTRUCTION

FINISHED TOP GROUND LEVEL (F.G.L) FOR PROCESS AREA 3220 = RL(+)913.000 m

- CONCRETE ELEMENT FLOOR (PRE-CAST SLAB)
- CONCRETE FLOOR
- CONCRETE FLOOR WITH ACID RESISTANT COATING
- CONCRETE WALL

1. ALL DIMENSIONS ARE IN MILLIMETER, ELEVATIONS ARE IN METER UNLESS OTHERWISE STATED
2. CO-ORDINATES ARE SHOWN IN GENERAL ARRENGEMENT DRAWINGS
3. GRATING TYPE (FRP OR NORMAL) IS SPECIFIED IN GENERAL ARRENGEMENT DRAWINGS
4. F.F.L, F.G.L, T.O.C = FINISHED FLOOR LEVEL, FINISHED GROUND LEVEL, TOP OF CONCRETE, T.O.S, B.O.S, B.O.B, = TOP OF STEEL, BOTTOM OF STEEL, BOTTOM OF BASE PLATE
5. BUILDING DIMENSIONS AND HEIGHTS ARE TENTATIVE, SHALL BE FINALIZED DURING DETAIL ENGINEERING SUBJECT TO MINIMUM AS SHOWN.
6. ALL MAINTENANCE FACILITIES, HANDLING PROVISIONS, ACCESS WAYS, PLATFORMS FOR MAINTENANCE SHALL BE PROVIDED DURING DETAIL ENGINEERING WHICH ARE NOT SHOWN ENTIRELY. THIS DRAWING IS TO BE CONSIDERED AS CONCEPTUAL ARRANGEMENT OF THE FACILITIES.

KEYPLAN

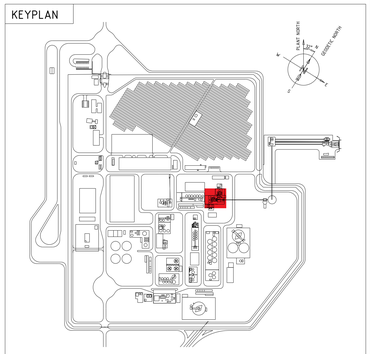

MD-216-3220-EG-CV-GAD-1005	PLAN AT +913.000 - GRID G-J/7-10	MD-216-3220-EG-ST-GAD-1001	PLAN AT +919.020 - GRID C-G/3-8														
MD-216-3220-EG-CV-GAD-1003	PLAN AT EL. +913.000 - GRID C-G/8-11	MD-216-3220-EG-CV-GAD-1004	PLAN AT +913.000 - GRID A-C/1-6														
MD-216-3220-EG-ME-GAD-1035	SECTION F-F	MD-216-3220-EG-CV-GAD-1002	SECTIONS A-A TO H-H & EQUIP. FOUNDATION														
MD-216-3220-EG-ME-GAD-1033	SECTION D-D	MD-216-3220-EG-ME-GAD-1074	SECTION E-E														
MD-216-3220-EG-ME-GAD-1031	SECTION B-B	MD-216-3220-EG-ME-GAD-1072	SECTION C-C														
MD-216-3220-EG-ME-GAD-1069	PLAN VIEW	MD-216-3220-EG-ME-GAD-1070	SECTION A-A							A03	02.07.2020	FOUNDATIONS & CHANNELS UPDATED	EliKo	MiKaLa	LuPiz	SauCha	
MD-216-3220-EG-ME-GAD-1067	PLAN AT EL. +922.180	MD-216-3220-EG-ME-GAD-1068	PLAN AT EL. +924.580							A02	04.03.2020	ISSUED FOR DETAIL DESIGN, FOUNDATIONS UPDATED, STAIRS & PLATFORMS ADDED	NiKlan	MiKaLa	LuPiz	SauCha	
MD-216-1000-EG-ST-CRT-0001	CIVIL, STRUCTURAL AND ARCHITECTURAL DESIGN BASIS	MD-216-3220-EG-ME-GAD-1066	PLAN AT EL. +913.000							A01	04.03.2020	ISSUED FOR DETAIL DESIGN, FOUNDATIONS UPDATED, STAIRS & PLATFORMS ADDED	NiKlan	MiKaLa	LuPiz	SauCha	
DOCUMENT NUMBER	REFERENCE DOCUMENTS	DOCUMENT NUMBER	REFERENCE DOCUMENTS	REV	DATE	REVISION DESCRIPTION	DRN	CHK	ENG	APP	EMP	REV	DATE	REVISION DESCRIPTION	DRN	CHK	ENG	APP	EMP

RESERVED FOR VENDOR LOGO AND DRAWING NUMBER

LARSEN & TOUBRO

This drawing is the property of LARSEN & TOUBRO and must not be passed on to any person or body not authorised by us to receive it nor be copied or otherwise made use either in full or in part by such person or body without our prior permission in writing.

Outotec

The content of these documents are the sole property of Outotec Oyj. Any rights not expressly granted herein are reserved. Reproduction, transfer or distribution of part or all of the contents in any form without prior written permission of Outotec is prohibited.

MA'ADEN معادن
Saudi Arabian Mining Company شركة معادن العربية السعودية

This document and the information contained herein is Ma'aden proprietary know-how. This document or any part thereof should not be reproduced, stored in a retrieval system or transmitted by any means, electronic or otherwise, or divulged without prior written permission of Ma'aden.

LARSEN & TOUBRO DRAWING NUMBER: O19045_450_C_G_24901_001 — REVISION: 2
OUTOTEC DRAWING NUMBER: 900707_GAU01_ZG01_CTA04_32201 — DOCUMENT ID: OU100667740 — REVISION: 2

DRAWN	NiKlan	11.12.2019
CHECKED	MiKaLa	11.12.2019
ENGINEER	LuPiz	11.12.2019
APPROVED	SauCha	11.12.2019
EMPLOYER		
SCALE	1:50	A0

MANSOURAH - MASSARAH GOLD PROJECT
CIVIL WORKS GUIDE DRAWING
GRINDING AND CLASSIFICATION - BALL MILL
PLAN AT EL. +913.000 - GRID C-G/1-8

DRAWING NUMBER: MD-216-3220-EG-CV-GAD-1001 — REV: A03

Tekla Structures