

DRAWING NUMBER: MD-216-3220-EG-CV-GAD-1005
REV: A03


LEVEL +913.000
1:50

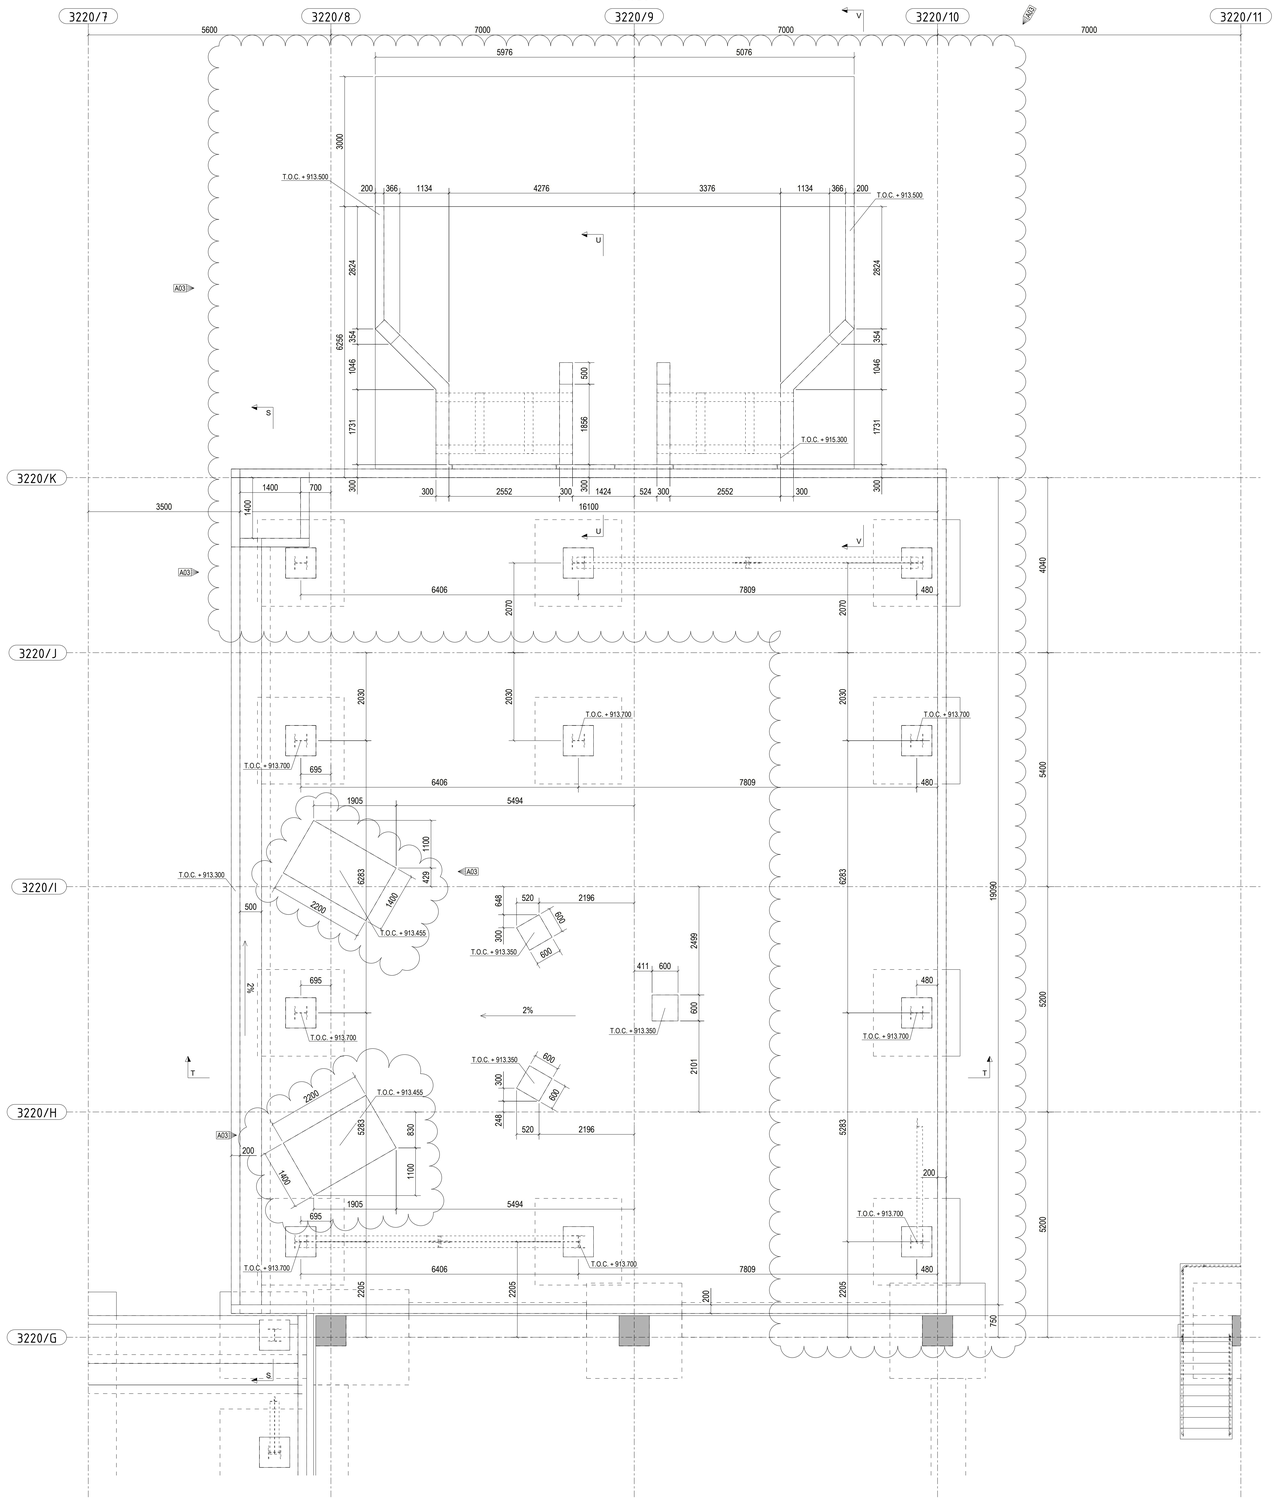


S - S
1:50

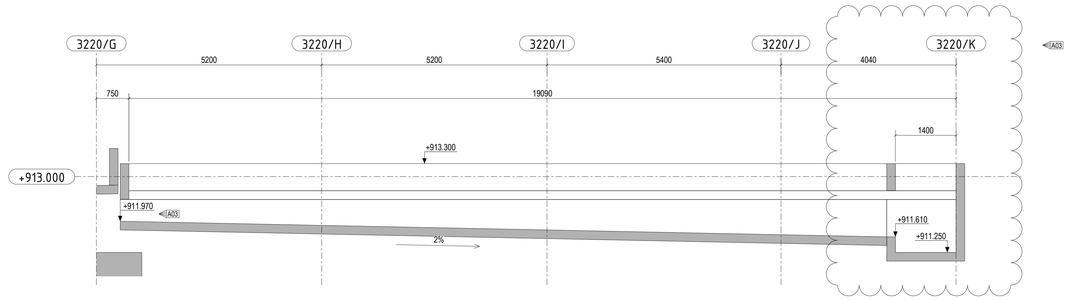

T - T
1:50

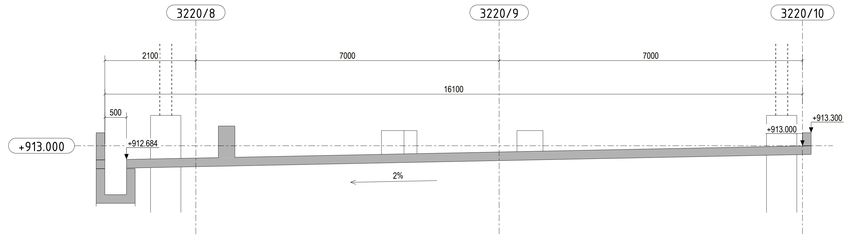

U - U
1:50

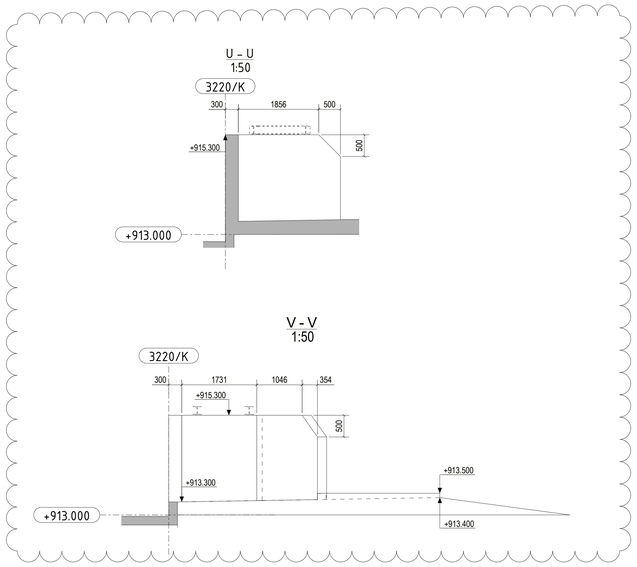

V - V
1:50


THIS DESIGN IS NOT ISSUED FOR CONSTRUCTION

FINISHED TOP GROUND LEVEL (F.G.L) FOR PROCESS AREA 3220 = RL(+)913.000 m

CONCRETE ELEMENT FLOOR (PRE-CAST SLAB)
CONCRETE FLOOR
CONCRETE FLOOR WITH ACID RESISTANT COATING
CONCRETE WALL

1. ALL DIMENSIONS ARE IN MILLIMETER, ELEVATIONS ARE IN METER UNLESS OTHERWISE STATED
2. CO-ORDINATES ARE SHOWN IN GENERAL ARRENGEMENT DRAWINGS
3. GRATING TYPE (FRP OR NORMAL) IS SPECIFIED IN GENERAL ARRENGEMENT DRAWINGS
4. F.F.L, F.G.L, T.O.C = FINISHED FLOOR LEVEL, FINISHED GROUND LEVEL, TOP OF CONCRETE, T.O.S, B.O.S, B.O.B, = TOP OF STEEL, BOTTOM OF STEEL, BOTTOM OF BASE PLATE
5. BUILDING DIMENSIONS AND HEIGHTS ARE TENTATIVE, SHALL BE FINALIZED DURING DETAIL ENGINEERING SUBJECT TO MINIMUM AS SHOWN.
6. ALL MAINTENANCE FACILITIES, HANDLING PROVISIONS, ACCESS WAYS, PLATFORMS FOR MAINTENANCE SHALL BE PROVIDED DURING DETAIL ENGINEERING WHICH ARE NOT SHOWN ENTIRELY. THIS DRAWING IS TO BE CONSIDERED AS CONCEPTUAL ARRANGEMENT OF THE FACILITIES.

KEYPLAN

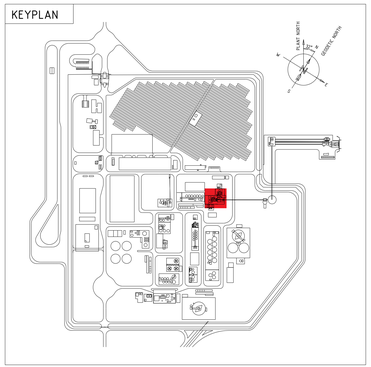

DOCUMENT NUMBER	REFERENCE DOCUMENTS	DOCUMENT NUMBER	REFERENCE DOCUMENTS
MD-216-3220-EG-CV-GAD-1004	PLAN AT EL. +913.000 - GRID A-C/1-6	MD-216-3220-EG-ST-GAD-1006	PLAN AT EL. +920.690 - GRID G-J/8-10
MD-216-3220-EG-CV-GAD-1002	SECTIONS A-A TO H-H & EQUIP. FOUNDATION	MD-216-3220-EG-CV-GAD-1003	PLAN AT EL. +913.000 - GRID C-G/8-11
MD-216-3220-EG-ME-GAD-1075	SECTION F-F	MD-216-3220-EG-CV-GAD-1001	PLAN AT EL. +913.000 - GRID C-G/1-8
MD-216-3220-EG-ME-GAD-1073	SECTION D-D	MD-216-3220-EG-ME-GAD-1074	SECTION E-E
MD-216-3220-EG-ME-GAD-1071	SECTION B-B	MD-216-3220-EG-ME-GAD-1072	SECTION C-C
MD-216-3220-EG-ME-GAD-1069	PLAN VIEW	MD-216-3220-EG-ME-GAD-1070	SECTION A-A
MD-216-3220-EG-ME-GAD-1067	PLAN AT EL. +922.180	MD-216-3220-EG-ME-GAD-1068	PLAN AT EL. +924.580
MD-216-1000-EG-ST-CRT-0001	CIVIL, STRUCTURAL AND ARCHITECTURAL DESIGN BASIS	MD-216-3220-EG-ME-GAD-1066	PLAN AT EL. +913.000

REV	DATE	REVISION DESCRIPTION	DRN	CHK	ENG	APP	EMP
A03	02.07.2020	FOUNDATIONS, SLAB & CHANNELS UPDATED	ElliKiv	MikLai	LuiPiz	SouCha	
A02	04.03.2020	ISSUED FOR DETAIL DESIGN, EQUIPMENT FOUNDATION UPDATED	NikJan	MikLai	LuiPiz	SouCha	
A01	11.12.2019	ISSUED FOR APPROVAL	NikJan	MikLai	LuiPiz	SouCha	

RESERVED FOR VENDOR LOGO AND DRAWING NUMBER

LARSEN & TOUBRO

This drawing is the property of LARSEN & TOUBRO and must not be passed on to any person or body not authorized by us to receive it nor be copied or otherwise made use either in full or in part by such person or body without our prior permission in writing.

Outotec

The content of these documents are the sole property of Outotec Oyj. Any rights not expressly granted herein are reserved. Reproduction, transfer or distribution of part or all of the contents in any form without prior written permission of Outotec is prohibited.

MA'ADEN معادن
Saudi Arabian Mining Company شركة معادن العربية السعودية

This document and the information contained herein is Ma'aden proprietary know-how. This document or any part thereof should not be reproduced, stored in a retrieval system or transmitted by any means, electronic or otherwise, or divulged without prior written permission of Ma'aden.

LARSEN & TOUBRO DRAWING NUMBER: 019045_450_C_G_24905_001 — REVISION: 2
OUTOTEC DRAWING NUMBER: 900707_GAU01_ZG01_CTA04_32205 — DOCUMENT ID: OU100667744 — REVISION: 2

DRAWN	NikJan	11.12.2019
CHECKED	MikLai	11.12.2019
ENGINEER	LuiPiz	11.12.2019
APPROVED	SouCha	11.12.2019
EMPLOYER		
SCALE	1:50	A0

MANSOURAH - MASSARAH GOLD PROJECT
CIVIL WORKS GUIDE DRAWING
GRINDING AND CLASSIFICATION - BALL MILL
PLAN AT EL. +913.000 - GRID G-J/7-10

DRAWING NUMBER: MD-216-3220-EG-CV-GAD-1005 — REV: A03

Tekla Structures