


DRAWING NUMBER: MD-216-1800-EG-CV-GAD-1568
REV: D01

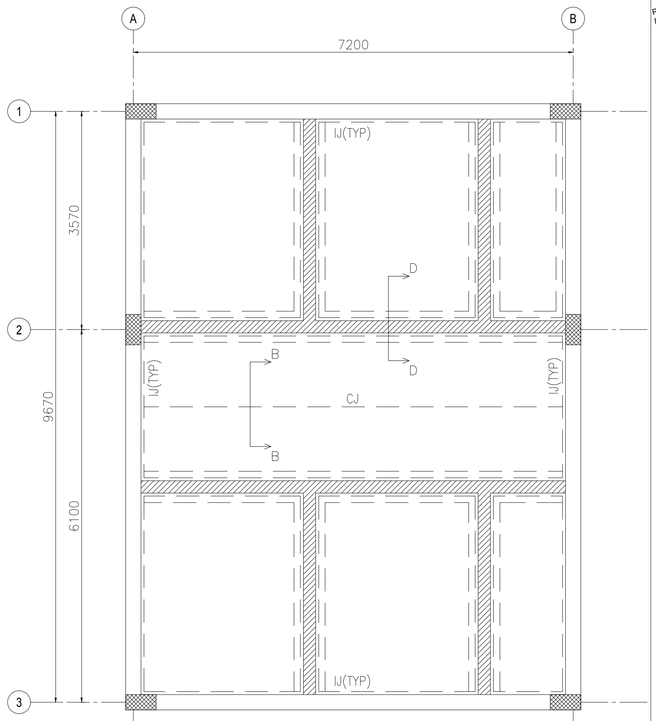

CONCRETE JOINTS LAYOUT
SCALE 1:50

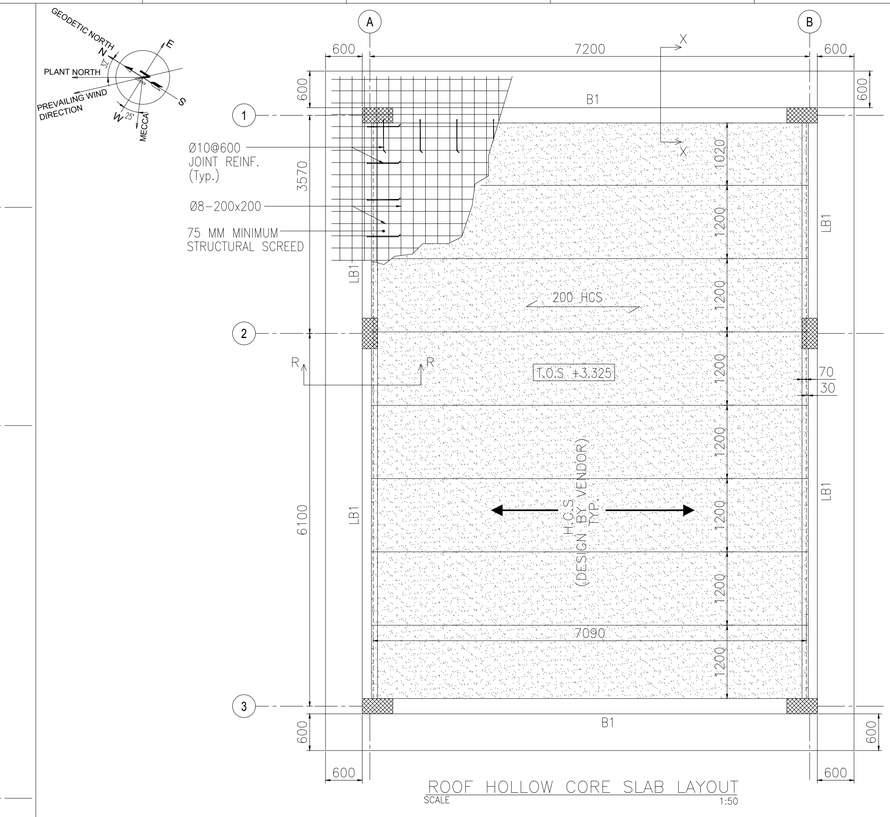



ROOF HOLLOW CORE SLAB LAYOUT
SCALE 1:50

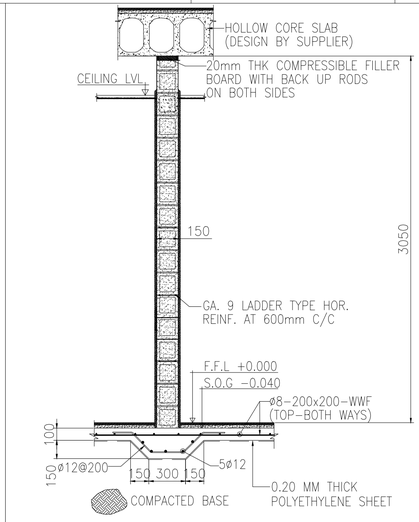

SECTION-D (INTERNAL WALL)
SCALE 1:25

MASTER KEY PLAN

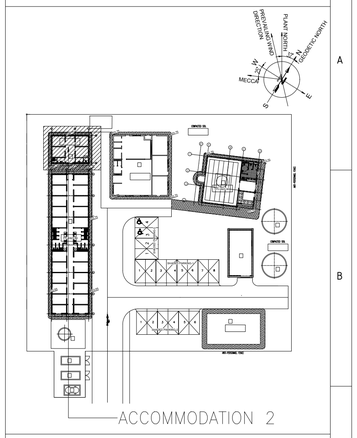


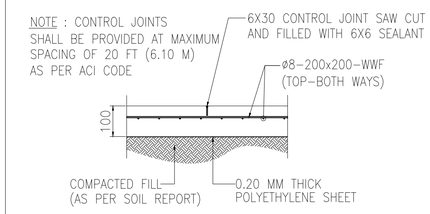


SECTION-B (CJ)
SCALE NTS

SCHEDULE OF ROOF BEAMS


BEAM MARK	DIMENSIONS		STEEL REINFORCEMENT				STIRRUPS
			TOP		BOTTOM		
	WIDTH	DEPTH	STRAIGHT	ADD.	STRAIGHT	ADD.	
LB1	250	500	3ø20	–	3ø20	–	PROVIDE ø10@140 BOTH IN THE ENDSPAN & MIDSPAN
B1	250	450	3ø16	–	3ø16	–	PROVIDE ø10@200 AT THE @DISTANCE OF L/3 FROM THE SUPPORT IN END SPAN & ø10@250 IN THE MID SPAN

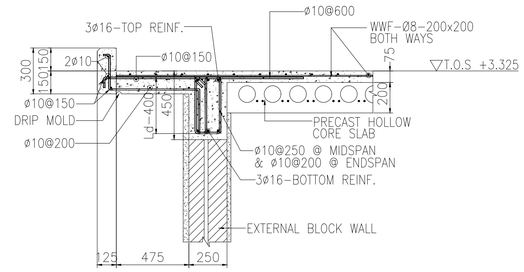


SECTION-X (B1)
SCALE 1:10

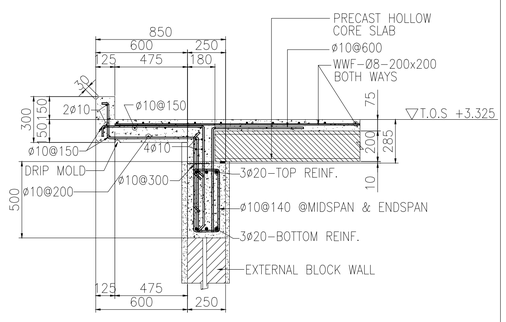

SECTION-LB1 (LB1)
SCALE 1:10

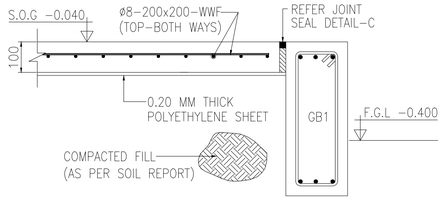

TYP SECTION FOR GRADE SLAB
SCALE 1:10

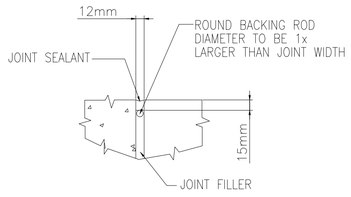

TYP JOINT SEAL DETAIL-C
SCALE 1:10

NOTES

1.) ALL DIMENSIONS ARE GIVEN IN MILLIMETRES AND ELEVATIONS ARE IN METRES UNLESS OTHERWISE NOTED.
2.) MINIMUM REINFORCED CONCRETE GRADE TO BE USED FOR SUPERSTRUCTURE & SUBSTRUCTURES IS M35(5000 PSI).
3.) MINIMUM LEAN CONCRETE GRADE TO BE USED FOR THE SUB-STRUCTURES IS M15(2175 PSI).
4.) ALL REINFORCING STEEL SHALL BE DEFORMED BILLET STEEL BARS CONFORMING TO ASTM-A615, WITH MINIMUM YIELD STRENGTH OF FY420 MPA .
5.) THE NET SOIL BEARING CAPACITY CONSIDERED IN FOUNDATION DESIGN IS 350 KPA.(REFER DOC 216-3000-EG-CV-RPT-1008).
6.) WATER PROOFING INSULATION SHALL BE AS PER PROJECT SPECS AND ITS MATERIAL TO BE APPROVED BY ENGINEER ON SITE.
7.) THE MINIMUM CONCRETE COVER AS PER SBC-304-2018(TABLE 20.6.1.3.1) MEASURED FROM REBAR SHALL BE
   a) CONCRETE CAST AGAINST & PERMANENTLY EXPOSED TO EARTH (INCLUDING FOUNDATIONS OVER SUB-SLAB) FORMED CONCRETE EXPOSED TO EARTH OR WEATHER.....50MM
   b.) CONCRETE NOT EXPOSED TO WEATHER NOR IN CONTACT WITH GROUND
   BEAMS, COLUMNS.....40MM
   SLABS, WALLS, JOISTS.....20MM
   c.) CONCRETE SLAB OVER 50MM SUB-SLAB.....20MM
8.) ALL DRAWINGS MUST BE READ IN CONJUNCTION WITH RELEVANT ARCHITECTURAL AND ENGINEERING DRAWINGS RELATED TO THE SAME SHEET AND ANY ITEM ON IT.
9.) F.F.L +0.00 MENTIONED IS EQUIVALENT TO RL 923.90 AS PER THE CIVIL DRAWING MD-216-1800-EG-CV-GAD-1565-OVERALL LAYOUT PLAN.

F-FOUNDATION
C-COLUMN
FFL-FINISH FLOOR LVL
FGL-FINISH GRADE LVL
TOS-TOP OF SCREED
WWF-WELDED WIRE FABRIC
HCS-HOLLOW CORE SLAB
GB-GRADE BEAM
IJ-ISOLATION JOINT
CJ-CONTROL JOINT
GA-GALVANIZED
S.O.G-SLAB ON GRADE
ARCH-ARCHITECTURAL
HOR.-HORIZONTAL
REINF.-REINFORCEMENT
LVL.-LEVEL
RL-REDUCED LEVEL

LEGEND/ABBREVIATIONS

DOCUMENT NUMBER	REFERENCE DOCUMENTS	REV	DATE	REVISION DESCRIPTION	DRN	CHK	ENG	APP	EMP
MD-216-6000-EG-CV-STD-1002	HOLLOW CORE SLAB STANDARD	D01	29/06/2023	AS -BUILT	--	AVG	--	SJM	
MD-216-6000-EG-CV-STD-1001	REINFORCEMENT STANDARD	C02	06/08/2020	ISSUED FOR CONSTRUCTION & REVISED AS MARKED (C02)	--	AVG	--	SJM	
MD-216-1800-EG-AR-GAD-3152	BUILDING PLANS	C01	23/04/2020	ISSUED FOR CONSTRUCTION	--	AVG	--	SJM	
MD-216-1800-EG-CV-GAD-1565	OVERALL LAYOUT PLAN	A01	23/03/2020	ISSUED FOR APPROVAL	--	AVG	--	SJM	

DESIGNER: مكتب الخليج للاستشارات الهندسية الخبر، المملكة العربية السعودية — GULF CONSULT ARCHITECTS AND ENGINEERS

DATE	13/03/2020	DATE	14/03/2020	DATE	15/03/2020
DRAWN	MAH	CHECKED	MF	APPROVED	FK

DRAWING NUMBER: ACCO-2-ST-002 — REVISION: 0
LARSEN & TOUBRO DRAWING NUMBER: 019045_900_C_G_24245_002 — REVISION: 3
OUTOTEC DRAWING NUMBER: 900707__GAU01__AN02__MTL01__18034 — DOCUMENT ID: OU100668740 — REVISION: 3

LARSEN & TOUBRO
This drawing is the property of LARSEN & TOUBRO and must not be passed on to any person or body not authorized by us to receive it nor be copied or otherwise made use either in full or in part by such person or body without our prior permission in writing.

Outotec
The content of these documents are the sole property of Outotec Oyj. Any rights not expressly granted herein are reserved. Reproduction, transfer or distribution of part or all of the contents in any form without prior written permission of Outotec is prohibited.

MA'ADEN معادن
Saudi Arabian Mining Company شركة معادن العربية السعودية
This document and the information contained herein is Ma'aden proprietary know-how. This document or any part thereof should not be reproduced, stored in a retrieval system or transmitted by any means, electronic or otherwise, or divulged without prior written permission of Ma'aden.

DRAWN	--	--	MANSOURAH - MASSARAH GOLD PROJECT
CHECKED	AVG	22/03/2020	GENERAL ARRANGEMENT
ENGINEER	--	--	SECURITY BASE CAMP: ACCOMMODATION 2
APPROVED	SJM	23/03/2020	LAYOUT & DETAILS OF ROOF & GRADE SLAB
EMPLOYER			
SCALE	1:50	A1	DRAWING NUMBER: MD-216-1800-EG-CV-GAD-1568 — REV: D01