

DRAWING NUMBER: MD-216-1800-EG-CV-GAD-1571
REV: D01

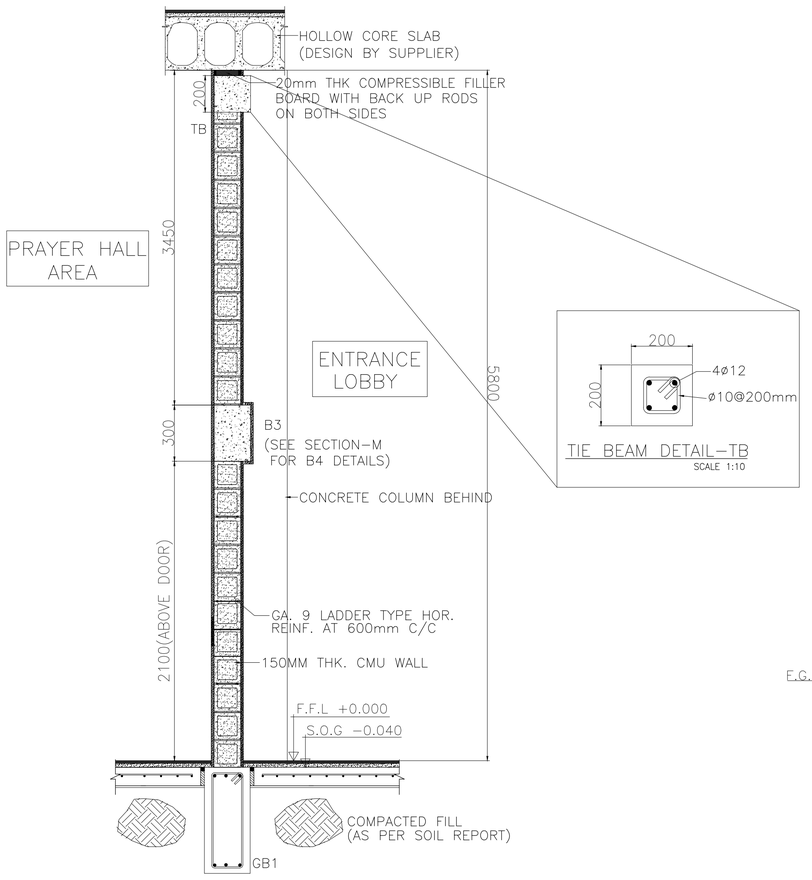


TYP INTERNAL WALL SECTION D
NTS GAD-1570


TIE BEAM DETAIL-TB
SCALE 1:10

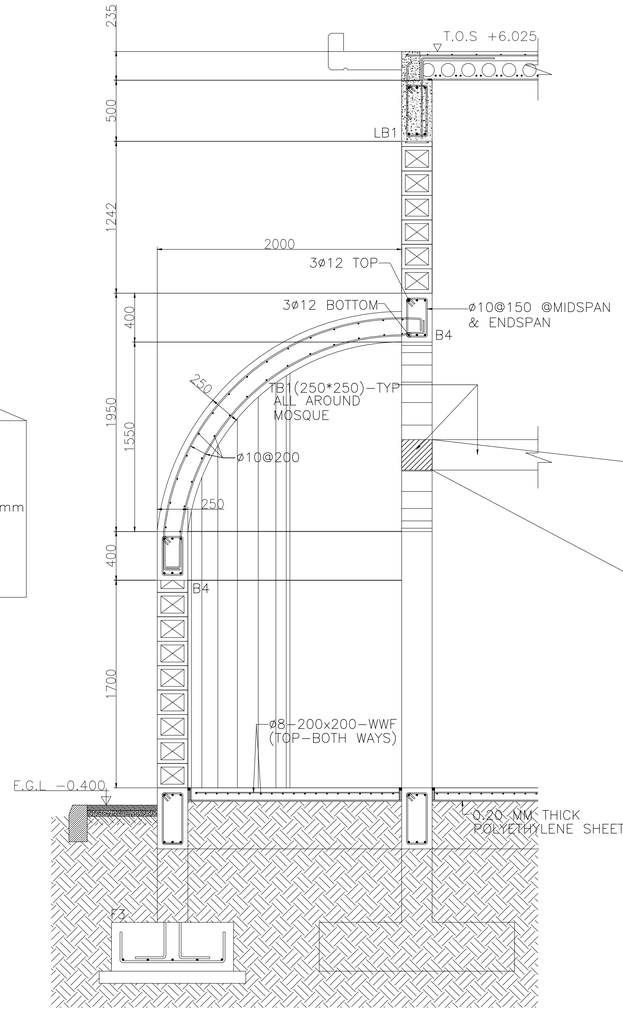

TYP SECTION AT MIHRAB AREA D1
SCALE 1:25 GAD-1570

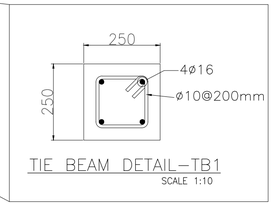

TIE BEAM DETAIL-TB1
SCALE 1:10

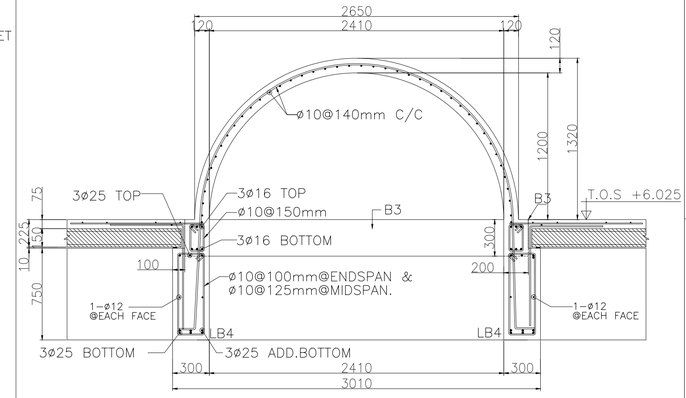

TYPICAL DOME SECTION UNDER LB4 M
SCALE 1:25 GAD-1570

NOTES

1.) ALL DIMENSIONS ARE GIVEN IN MILLIMETRES AND ELEVATIONS ARE IN METRES UNLESS OTHERWISE NOTED.

2.) MINIMUM REINFORCED CONCRETE GRADE TO BE USED FOR SUPERSTRUCTURE & SUBSTRUCTURES IS C35(5000 PSI).

3.) MINIMUM LEAN CONCRETE GRADE TO BE USED FOR THE SUB-STRUCTURES IS C15(2175 PSI).

4.) ALL REINFORCING STEEL SHALL BE DEFORMED BILLET STEEL BARS CONFORMING TO ASTM-A615, WITH MINIMUM YIELD STRENGTH OF FY420 MPA .

5.) THE NET SOIL BEARING CAPACITY CONSIDERED IN FOUNDATION DESIGN IS 350 KPA.(REFER DOC 216-3000-EG-CV-RPT-1008)

6.) WATER PROOFING INSULATION SHALL BE AS PER PROJECT SPECIFICATIONS & ITS MATERIAL TO BE APPROVED BY SITE ENGINEER.

7.) THE MINIMUM CONCRETE COVER AS PER SBC-304-2018(TABLE 20.6.1.3.1) MEASURED FROM REBAR SHALL BE
a) CONCRETE CAST AGAINST & PERMANENTLY EXPOSED TO EARTH (INCLUDING FOUNDATIONS OVER SUB-SLAB) FORMED CONCRETE EXPOSED TO EARTH OR WEATHER.....50MM
b.) CONCRETE NOT EXPOSED TO WEATHER NOR IN CONTACT WITH GROUND
BEAMS, COLUMNS.....40MM
SLABS, WALLS, JOISTS.....20MM
c.) CONCRETE SLAB OVER 50MM SUB-SLAB.....20MM

8.) ALL DRAWINGS MUST BE READ IN CONJUNCTION WITH RELEVANT ARCHITECTURAL AND ENGINEERING DRAWINGS RELATED TO THE SAME SHEET AND ANY ITEM ON IT.

9.) F.F.L +0.00 MENTIONED IS EQUIVALENT TO FINISH FLOOR LVL +922.70M AS PER THE CIVIL DRAWING CE-004A-OVERALL LAYOUT PLAN.

F-FOUNDATION
C-COLUMN
FFL-FINISH FLOOR LVL
FGL-FINISH GRADE LVL
TOS-TOP OF SCREED
WWF-WELDED WIRE FABRIC
HCS-HOLLOW CORE SLAB
GB-GRADE BEAM
IJ-ISOLATION JOINT
CJ-CONTROL JOINT
GA-GALVANIZED
S.O.G-SLAB ON GRADE
ARCH-ARCHITECTURAL
HOR.-HORIZONTAL
REINF.-REINFORCEMENT
LVL.-LEVEL

LEGEND/ABBREVIATIONS

DOCUMENT NUMBER	REFERENCE DOCUMENTS	REV	DATE	REVISION DESCRIPTION	DRN	CHK	ENG	APP	EMP
MD-216-1800-EG-AR-GAD-3166	BUILDING ELEVATIONS & SECTIONS								
MD-216-6000-EG-CV-STD-1002	HOLLOW CORE SLAB STANDARD								
MD-216-6000-EG-CV-STD-1001	REINFORCEMENT STANDARD	D01	05/05/2023	AS- BUILT	--	AVG	--	SJM	
MD-216-1800-EG-AR-GAD-3165	BUILDING PLANS	C01	19/05/2020	ISSUED FOR CONSTRUCTION	--	AVG	--	SJM	
MD-216-1800-EG-CV-GAD-1565	OVERALL LAYOUT PLAN	A01	19/04/2020	ISSUED FOR APPROVAL	--	AVG	--	SJM	

DESIGNER: مكتب الخليج للاستشارات الهندسية الخبر، المملكة العربية السعودية — GULF CONSULT ARCHITECTS AND ENGINEERS

DRAWN	MAH	CHECKED	MF	APPROVED	FK
DATE	15/04/2020	DATE	16/04/2020	DATE	17/04/2020

DRAWING NUMBER: FACILITY-MOSQUE-ST-003 — REVISION: 0

LARSEN & TOUBRO DRAWING NUMBER: 019045_900_C_G_24249_003 — REVISION: 2

OUTOTEC DRAWING NUMBER: 900707__GAU01__AN02__MTL01__18037 — DOCUMENT ID: OU100668743 — REVISION: 2

LARSEN & TOUBRO
This drawing is the property of *LARSEN & TOUBRO* and must not be passed on to any person or body not authorized by us to receive it nor be copied or otherwise made use either in full or in part by such person or body without our prior permission in writing.

Outotec
The content of these documents are the sole property of Outotec Oyj. Any rights not expressly granted herein are reserved. Reproduction, transfer or distribution of part or all of the contents in any form without prior written permission of Outotec is prohibited.

MA'ADEN معادن
Saudi Arabian Mining Company شركة معادن العربية السعودية
This document and the information contained herein is Ma'aden proprietary know-how. This document or any part thereof should not be reproduced, stored in a retrieval system or transmitted by any means, electronic or otherwise, or divulged without prior written permission of Ma'aden.

DRAWN	--	--
CHECKED	AVG	18/04/2020
ENGINEER	--	--
APPROVED	SJM	19/04/2020
EMPLOYER		
SCALE	1:100	A1

MANSOURAH - MASSARAH GOLD PROJECT
GENERAL ARRANGEMENT DRAWING
SECURITY BASE CAMP: MOSQUE
DETAILS OF ROOF DOME & WALL SECTIONS

DRAWING NUMBER: MD-216-1800-EG-CV-GAD-1571 — REV: D01