

DRAWING NUMBER: MD-216-3520-EG-CV-GAD-1001
REV: A02


LEVEL +912.500
1:100

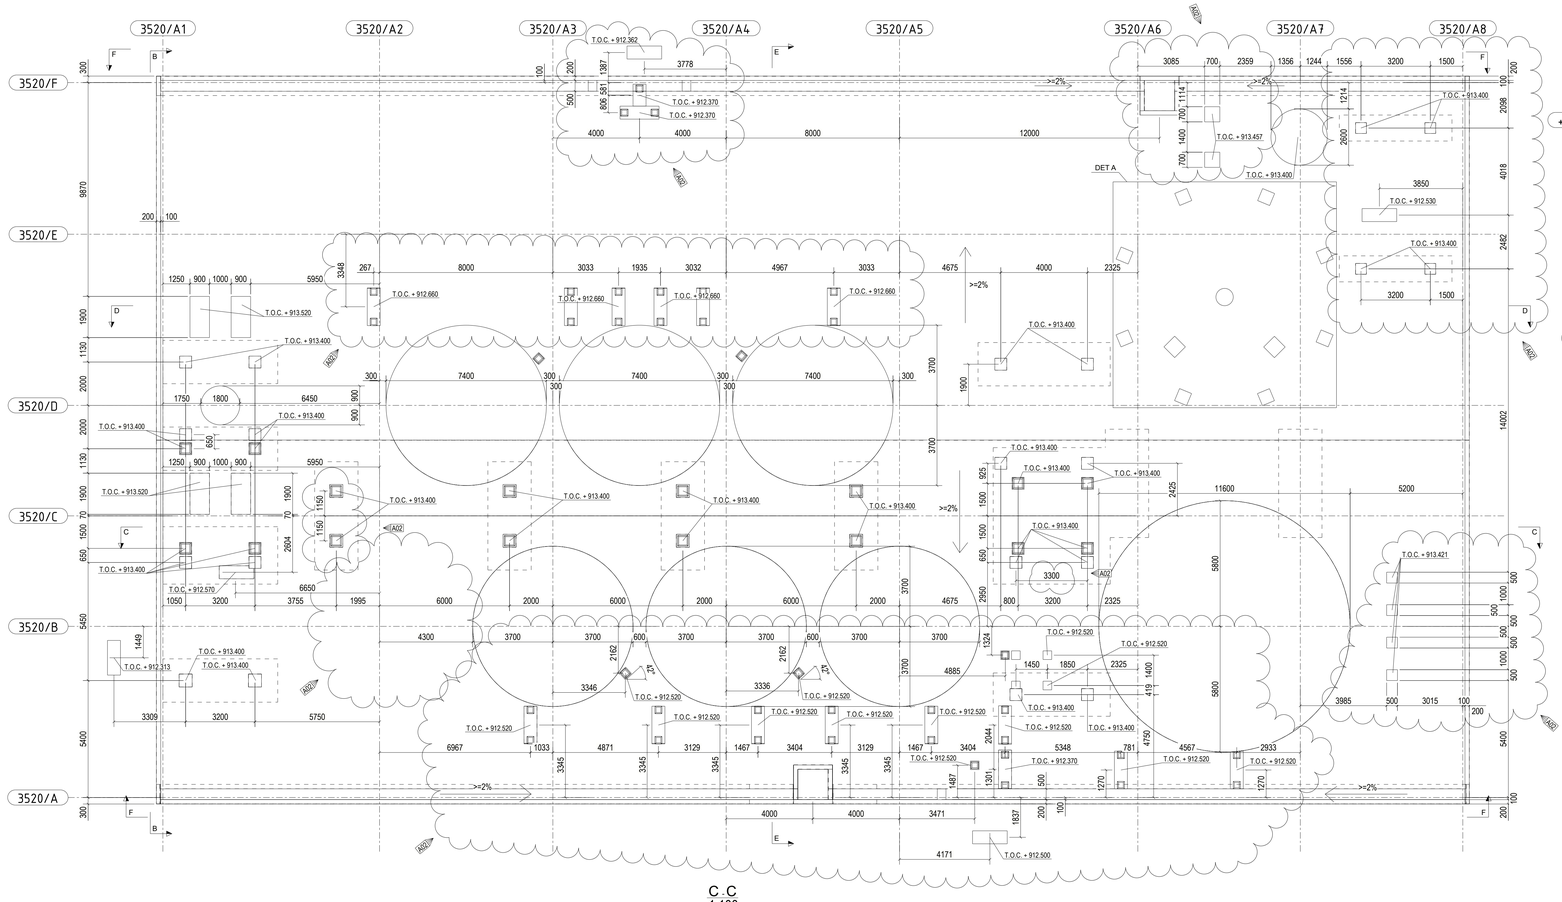

B - B
1:100

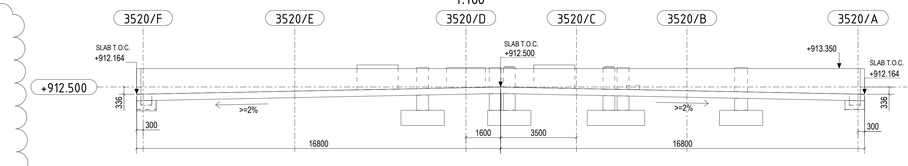

E - E
1:100

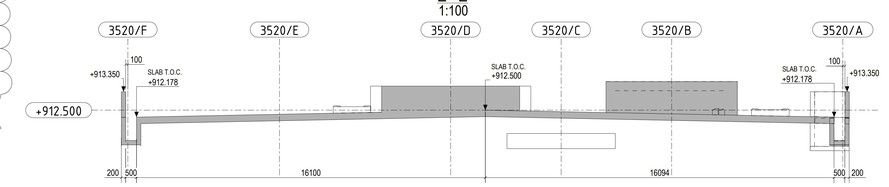


THIS DESIGN IS NOT ISSUED FOR CONSTRUCTION

FINISHED TOP GROUND LEVEL (F.G.L) FOR PROCESS AREA 3520 = RL(+)912.500 m


- CONCRETE ELEMENT FLOOR (PRE-CAST SLAB)
- CONCRETE FLOOR
- CONCRETE FLOOR WITH ACID RESISTANT COATING
- CONCRETE WALL

1. ALL DIMENSIONS ARE IN MILLIMETER, ELEVATIONS ARE IN METER UNLESS OTHERWISE STATED
2. CO-ORDINATES ARE SHOWN IN GENERAL ARRENGEMENT DRAWINGS
3. GRATING TYPE (FRP OR NORMAL) IS SPECIFIED IN GENERAL ARRENGEMENT DRAWINGS
4. F.F.L, F.G.L, T.O.C = FINISHED FLOOR LEVEL, FINISHED GROUND LEVEL, TOP OF CONCRETE, T.O.S, B.O.S, B.O.B, = TOP OF STEEL, BOTTOM OF STEEL, BOTTOM OF BASE PLATE
5. BUILDING DIMENSIONS AND HEIGHTS ARE TENTATIVE, SHALL BE FINALIZED DURING DETAIL ENGINEERING SUBJECT TO MINIMUM AS SHOWN.
6. ALL MAINTENANCE FACILITIES, HANDLING PROVISIONS, ACCESS WAYS, PLATFORMS FOR MAINTENANCE SHALL BE PROVIDED DURING DETAIL ENGINEERING WHICH ARE NOT SHOWN ENTIRELY. THIS DRAWING IS TO BE CONSIDERED AS CONCEPTUAL ARRANGEMENT OF THE FACILITIES.


C - C
1:100

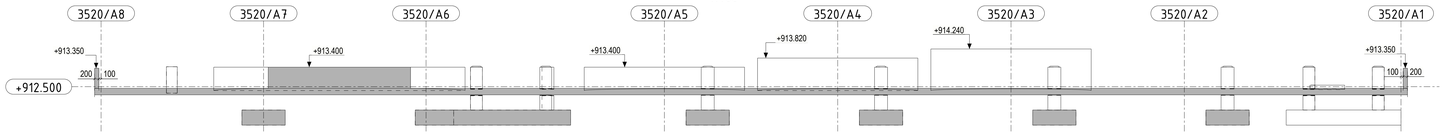


A - A
1:100
T.O.C. +913.400

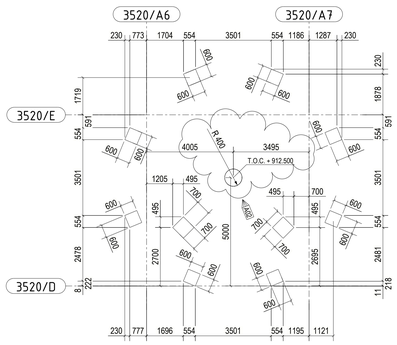


D - D
1:100

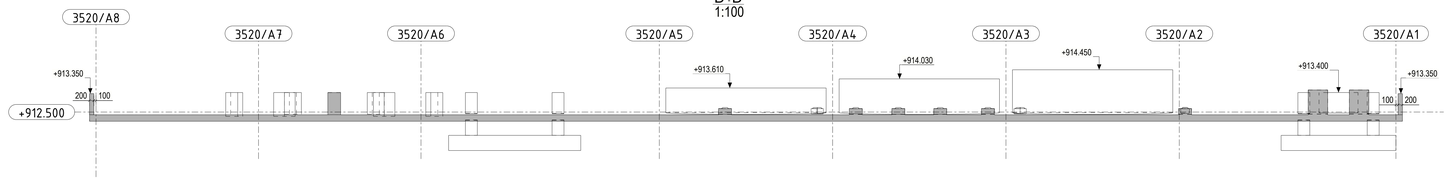

F - F
1:100

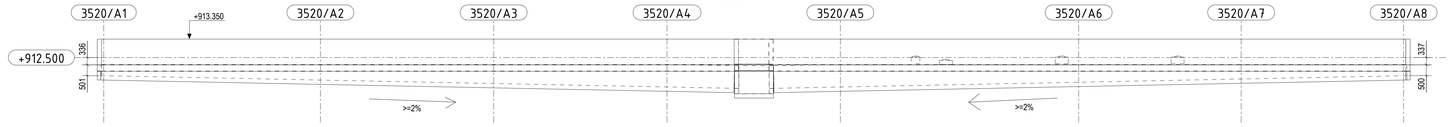

KEYPLAN

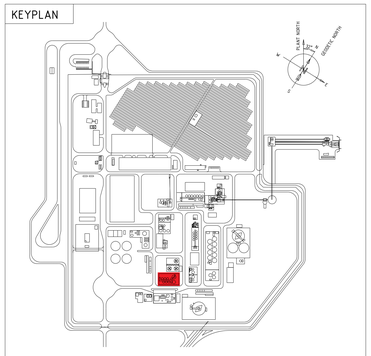

DOCUMENT NUMBER	REFERENCE DOCUMENTS	DOCUMENT NUMBER	REFERENCE DOCUMENTS
MD-216-3520-EG-ST-GAD-1001	3D VIEW	MD-216-3520-EG-ST-GAD-1002	PLAN AND SECTIONS
MD-216-3520-EG-ME-GAD-1043	SECTION D-D	MD-216-1000-EG-ST-CRT-0001	CIVIL,STRUCTURAL AND ARCHITECTURAL DESIGN BASIS
MD-216-3520-EG-ME-GAD-1041	SECTION A-A AND B-B	MD-216-3520-EG-ME-GAD-1042	SECTION C-C
MD-216-3520-EG-ME-GAD-1039	PLAN AT EL. +912.500	MD-216-3520-EG-ME-GAD-1040	PLAN VIEW

REV	DATE	REVISION DESCRIPTION	DRN	CHK	ENG	APP	EMP
A02	30.03.2020	ISSUED FOR DETAIL DESIGN, FOUNDATIONS UPDATED	Kirjak	MAkLai	LuiPiz	SouCha	
A01	11.12.2019	ISSUED FOR APPROVAL	AnnFor	MAkLai	LuiPiz	SouCha	

RESERVED FOR VENDOR LOGO AND DRAWING NUMBER

This drawing is the property of LARSEN & TOUBRO and must not be passed on to any person or body not authorized by us to receive it nor be copied or otherwise made use either in full or in part by such person or body without our prior permission in writing.

The content of these documents are the sole property of Outotec Oy. Any rights not expressly granted herein are reserved. Reproduction, transfer or distribution of part or all of the contents in any form without prior written permission of Outotec is prohibited.

This document and the information contained herein is Ma'aden proprietary know-how. This document or any part thereof should not be reproduced, stored in a retrieval system or transmitted by any means, electronic or otherwise, or divulged without prior written permission of Ma'aden.

LARSEN & TOUBRO DRAWING NUMBER: 019045_450_C_G_24943_001 — REVISION: 1
OUTOTEC DRAWING NUMBER: 900707_GAU01_RN13_CTA04_35201 — DOCUMENT ID: OU100667800 — REVISION: 1

DRAWN	AnnFor	11.12.2019
CHECKED	MAkLai	11.12.2019
ENGINEER	LuiPiz	11.12.2019
APPROVED	SouCha	11.12.2019
EMPLOYER		
SCALE	1:100	A0

MANSOURAH - MASSARAH GOLD PROJECT
CIVIL WORKS GUIDE DRAWING
3520 NEUTRALIZATION AND THICKENING
PLAN AT EL. +912.500

DRAWING NUMBER: MD-216-3520-EG-CV-GAD-1001 — REV: A02

Tekla Structures