

DRAWING NUMBER: MD-216-3980-EG-CV-GAD-V551-1480 REV D01

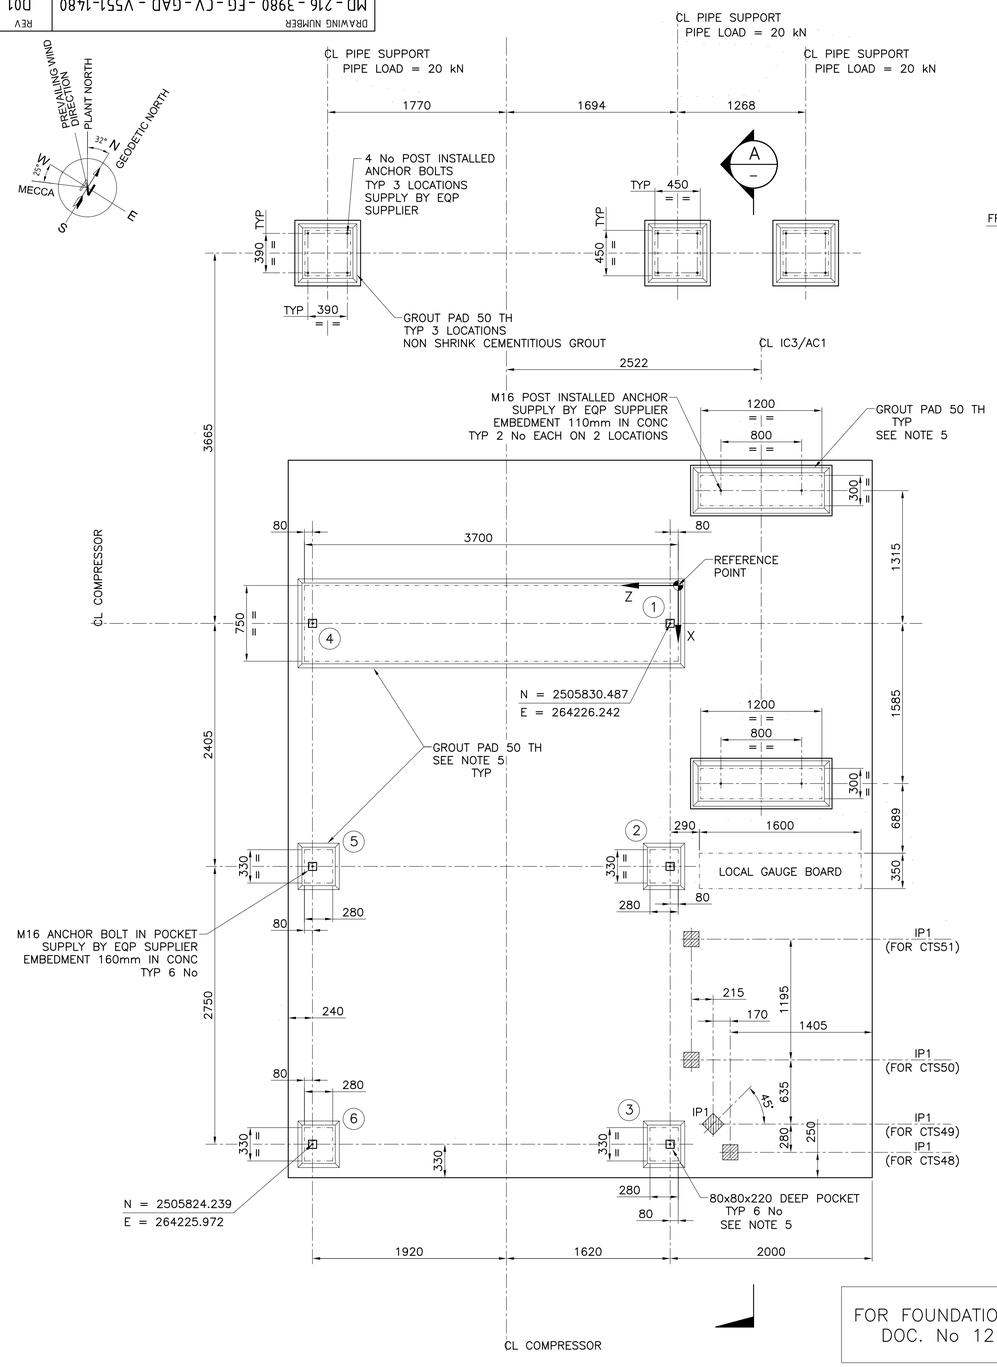

FOR FOUNDATION LOAD DATA REFER TO DOC. No 12126-RE-001-611501


FOUNDATION PLAN MAIN AIR COMPRESSOR

SCALE 1:30

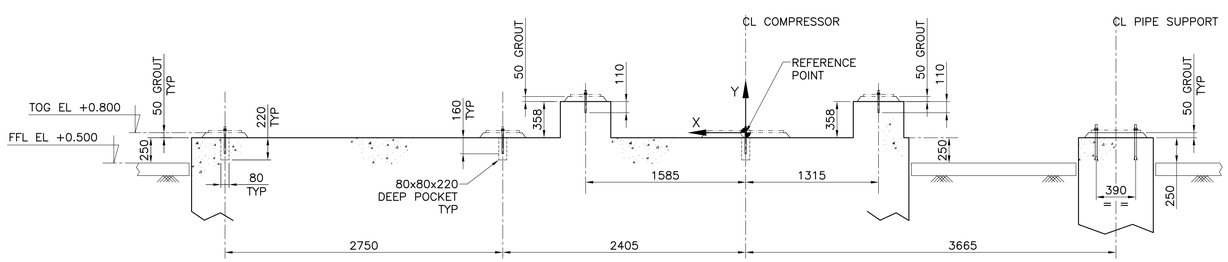

SECTION A – A

SCALE 1:30

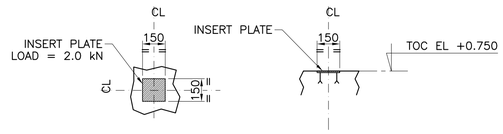

DETAIL OF INSERT PLATE IP1


SCALE 1:20

NOTES

1. ALL DIMENSIONS ARE IN MILLIMETER.
2. ALL LEVELS ARE IN METER.
3. FGL LEVEL ±0.0 CORRESPONDS TO RL 912.350.
4. THE LOADS INDICATED IN LOAD DATA TABLE ARE ACTUAL. FOUNDATION DESIGNER SHOULD CONSIDER NECESSARY MARGIN.
5. NON SHRINK EPOXY GROUT, FREE FROM CHLORIDE AND OIL RESISTANT.
   COMPRESSIVE STRENGTH 70MPa TO 90MPa AFTER 28 DAYS.
   BENDING STRENGTH 10MPa TO 15MPa AFTER 28 DAYS.
6. SIZE OF FOUNDATION AND PEDESTAL SHALL BE DECIDED BY CIVIL DESIGN ENGINEER AS PER GIVEN LOADING AND OTHER REQUIRED DYNAMIC PARAMETERS.
7. ADDITIONAL REBAR REQUIREMENT AROUND ANCHOR BOLTS TO ENSURE NO FAILURE OF CONCRETE SHALL BE DECIDED BY CIVIL DESIGN ENGINEER AS PER GIVEN LOADING.

LEGEND :

CL – CENTER LINE
CONC – CONCRETE
EL – ELEVATION
EQP – EQUIPMENT
FFL – FINISHED FLOOR LEVEL
FGL – FINISHED GROUND LEVEL
Gr – GRADE
MPa – MEGA PASCAL
mm – MILLIMETER
No – NUMBER / NUMBERS
TH – THICKNESS
TOC – TOP OF CONCRETE
TOG – TOP OF GROUT
TYP – TYPICAL

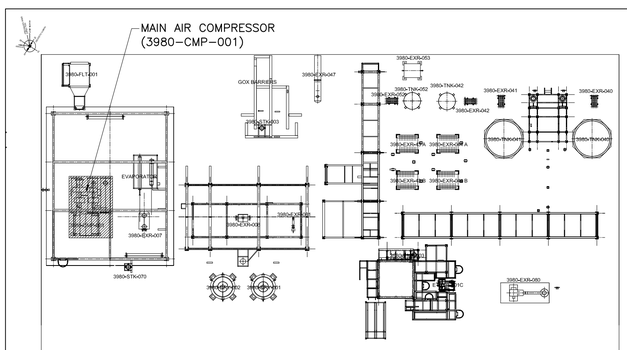

KEY PLAN

DOCUMENT NUMBER	REFERENCE DOCUMENTS	REV	DATE	REVISION DESCRIPTION	DRN	CHK	ENG	APP	EMP
		D01	08/05/2023	AS - BUILT	--	STY/ SYC/ SHH	--	BDA/ PRI/ JPD	
		C01	27/10/2020	ISSUED FOR CONSTRUCTION	--	STY/ SYC/ SHH	--	BDA/ PRI/ JPD	
		A01	03/06/2020	ISSUED FOR INFORMATION	--	STY/ SYC/ SHH	--	BDA/ PRI/ JPD	

AIR LIQUIDE CONFIDENTIAL INFORMATION: THIS PRINT IS THE PROPERTY OF L'AIR LIQUIDE S.A. OR ITS (DIRECT AND INDIRECT) AFFILIATES OR SUBSIDIARIES AND CONTAINS VALUABLE CONFIDENTIAL INFORMATION. COPYRIGHT AND ALL OTHER RIGHTS IN THIS PRINT ARE EXPRESSLY RESERVED. NO PART OF THIS PRINT MAY BE DISCLOSED BY THE INTENDED RECIPIENT TO A THIRD PARTY, REPRODUCED, COPIED, LENT, OR DISPOSED OF, DIRECTLY OR INDIRECTLY, NOR USED FOR ANY PURPOSE OTHER THAN THAT FOR WHICH IT IS EXPRESSLY FURNISHED. THIS PRINT IS LENT SUBJECT TO RETURN ON DEMAND.

This drawing is the property of LARSEN & TOUBRO and must not be passed on to any person or body not authorized by us to receive it nor be copied or otherwise made use either in full or in part by such person or body without our prior permission in writing.

The content of these documents are the sole property of Outotec Oyj. Any rights not expressly granted herein are reserved. Reproduction, transfer or distribution of part or all of the contents in any form without prior written permission of Outotec is prohibited.

This document and the information contained herein is Ma'aden proprietary know-how. This document or any part thereof should not be reproduced, stored in a retrieval system or transmitted by any means, electronic or otherwise, or divulged without prior written permission of Ma'aden.

DRAWING NUMBER				REVISION	STATUS
12126-60-01-CS-141050				1	AFD
DATE	22/10/2020	DATE	23/10/2020	DATE	24/10/2020
DRAWN	SGH	CHECKED	ABM	APPROVED	DS

LARSEN & TOUBRO DRAWING NUMBER		REVISION
019045_080_C_V_24225_007		2
OUTOTEC DRAWING NUMBER	DOCUMENT ID	REVISION
900707__GAU01__AG22__MTL01__39820	OU100680045	2

DRAWN	--	--
CHECKED	STY/ SYC/ SHH	26/10/2020
ENGINEER	--	--
APPROVED	BDA/ PRI/ JPD	27/10/2020
EMPLOYER		
SCALE	1:XX	A1

MANSOURAH - MASSARAH GOLD PROJECT
GENERAL ARRANGEMENT DRAWING
OXYGEN PLANT
FOUNDATION LOAD & ANCHORAGE - COMPRESSOR

DRAWING NUMBER: MD-216-3980-EG-CV-GAD-V551-1480 REV: D01