

DRAWING NUMBER: MD - 216 - 3980 - EG - CV - GAD - V551-1488
REV: D01

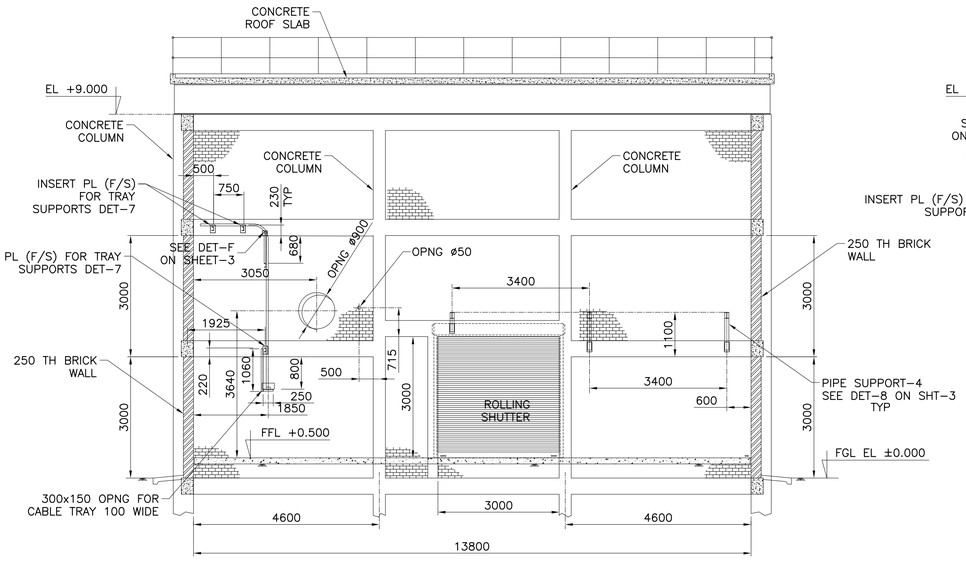

NORTH SIDE GABLE

LOOKING NORTH
SCALE 1:75

NOTE: BUNDLE EXTRACTOR TROLLEY DIMENSION CONSIDERED
WIDTH = 2.500M
HEIGHT = 2.540M

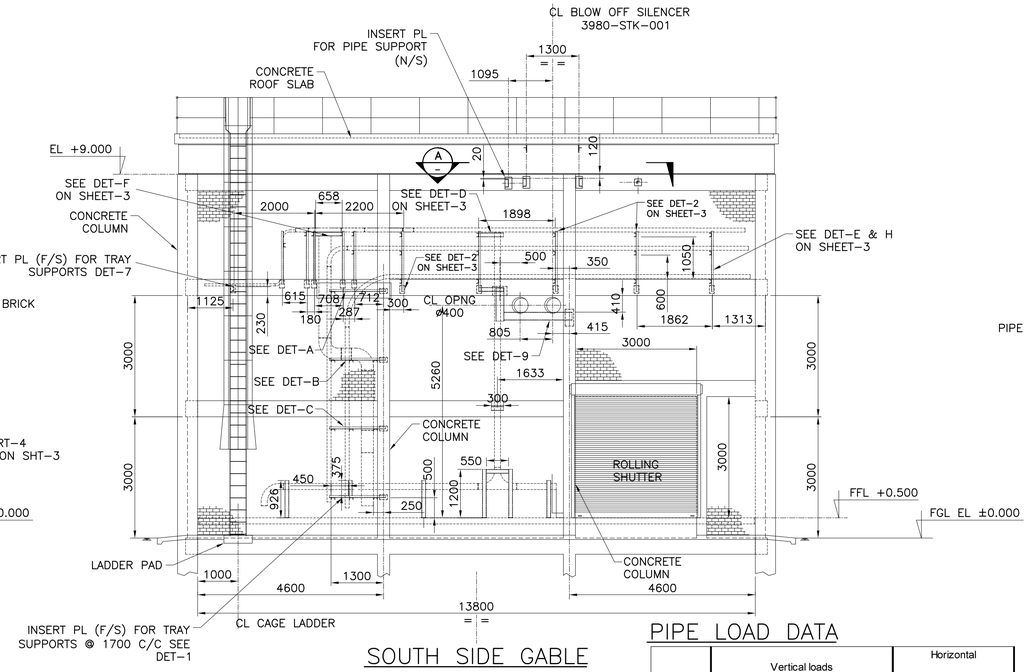


SOUTH SIDE GABLE

LOOKING NORTH
SCALE 1:75

NOTES

1. ALL DIMENSIONS ARE IN MILLIMETER.
2. ALL LEVELS ARE IN METER.
3. FOR ALL OTHER NOTES SEE SHT-1 OF 3.

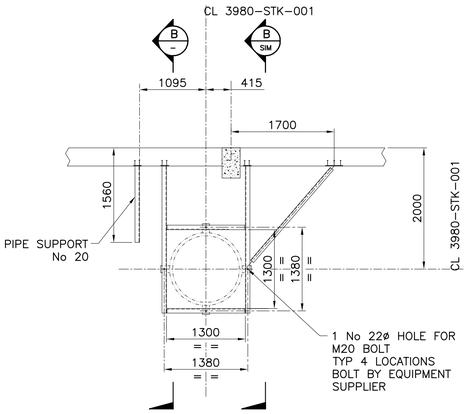

SECTION A – SCALE 1:50

PIPE LOAD DATA

Load No	Vertical loads			Horizontal Operational load	
	Empty [kN]	Operating [kN]	Hydro Test [kN]	FX [kN] (N-S)	FZ [kN] (E-W)
10	-5.0	-25.0	-6.5	5.0	9.0
20	-	-	-	5.0	24.0
30	-	-	-	1.0	1.0
N-S = North South Direction, E-W = East West Direction					

EQUIPMENT LOAD DATA

3980-STK-001

EMPTY LOAD – 16.0 KN
OPERATING LOAD – 16.0 KN

WIND LOAD :
HOZ LOAD – 4 KN
MOMENT – 6 KN-m

SEISMIC LOAD :
HOZ LOAD – 5 KN
MOMENT – 7.5 KN-m

TYPICAL CROSS SECTION

SCALE 1:75

CABLE TRAY LOAD DATA

TRAY WIDTH 600mm – 0.6 KN/m
TRAY WIDTH 450mm – 0.45 KN/m
TRAY WIDTH 300mm – 0.3 KN/m

DOCUMENT NUMBER	REFERENCE DOCUMENTS	REV	DATE	REVISION DESCRIPTION	DRN	CHK	ENG	APP	EMP
		D01	08/05/2023	AS - BUILT	--	STY/SYC/SHH	--	BDA/PRI/JPD	
		C02	23/11/2020	ISSUED FOR CONSTRUCTION	--	STY/SYC/SHH	--	BDA/PRI/JPD	
		C01	10/08/2020	ISSUED FOR CONSTRUCTION	--	STY/SYC/SHH	--	BDA/PRI/JPD	
		A01	16/06/2020	ISSUED FOR INFORMATION	--	STY/SYC/SHH	--	BDA/PRI/JPD	

Air Liquide ENGINEERING & CONSTRUCTION

AIR LIQUIDE CONFIDENTIAL INFORMATION. THIS PRINT IS THE PROPERTY OF L'AIR LIQUIDE, S.A. OR ITS (DIRECT AND INDIRECT) AFFILIATES OR SUBSIDIARIES AND CONTAINS VALUABLE CONFIDENTIAL INFORMATION. COPYRIGHT AND ALL OTHER RIGHTS IN THIS PRINT ARE EXPRESSLY RESERVED. NO PART OF THIS PRINT MAY BE DISCLOSED BY THE INTENDED RECIPIENT TO A THIRD PARTY, REPRODUCED, COPIED, LENT, OR DISPOSED OF, DIRECTLY OR INDIRECTLY, NOR USED FOR ANY PURPOSE OTHER THAN THAT FOR WHICH IT IS EXPRESSLY FURNISHED. THIS PRINT IS LENT SUBJECT TO RETURN ON DEMAND.

DRAWING NUMBER	REVISION	STATUS
12126-60-01-CS-261191	1	AFD

DATE	17/11/2020	DATE	18/11/2020	DATE	19/11/2020
DRAWN	SGH	CHECKED	ABM	APPROVED	DS

LARSEN & TOUBRO DRAWING NUMBER: 019045-080-C-V-24225-026 — REVISION: 3
OUTOTEC DRAWING NUMBER: 900707 __GAU01 __AG22__MTL01 __39846 — DOCUMENT ID: OU100688446 — REVISION: 3

LARSEN & TOUBRO

This drawing is the property of LARSEN & TOUBRO and must not be passed on to any person or body not authorized by us to receive it nor be copied or otherwise made use either in full or in part by such person or body without our prior permission in writing.

Outotec

The content of these documents are the sole property of Outotec Oyj. Any rights not expressly granted herein are reserved. Reproduction, transfer or distribution of part or all of the contents in any form without prior written permission of Outotec is prohibited.

MA'ADEN معادن
Saudi Arabian Mining Company شركة التعدين العربية السعودية

This document and the information contained herein is Ma'aden proprietary know-how. This document or any part thereof should not be reproduced, stored in a retrieval system or transmitted by any means, electronic or otherwise, or divulged without prior written permission of Ma'aden.

DRAWN	--	--	
CHECKED	STY/ SYC/ SHH	20/11/2020	
ENGINEER	--	--	
APPROVED	BDA/ PRI/ JPD	23/11/2020	
EMPLOYER			
SCALE	1:75, 50, 30	A1	

MANSOURAH - MASSARAH GOLD PROJECT
GUIDE DRAWING
OXYGEN PLANT
GUIDE DRAWING - COMPRESSOR ROOM (2 OF 3)

DRAWING NUMBER: MD - 216 - 3980 - EG - CV - GAD - V551-1488 — REV: D01