

DRAWING NUMBER MD-216-3980-EG-CV-GAD-V551-1489 REV D01

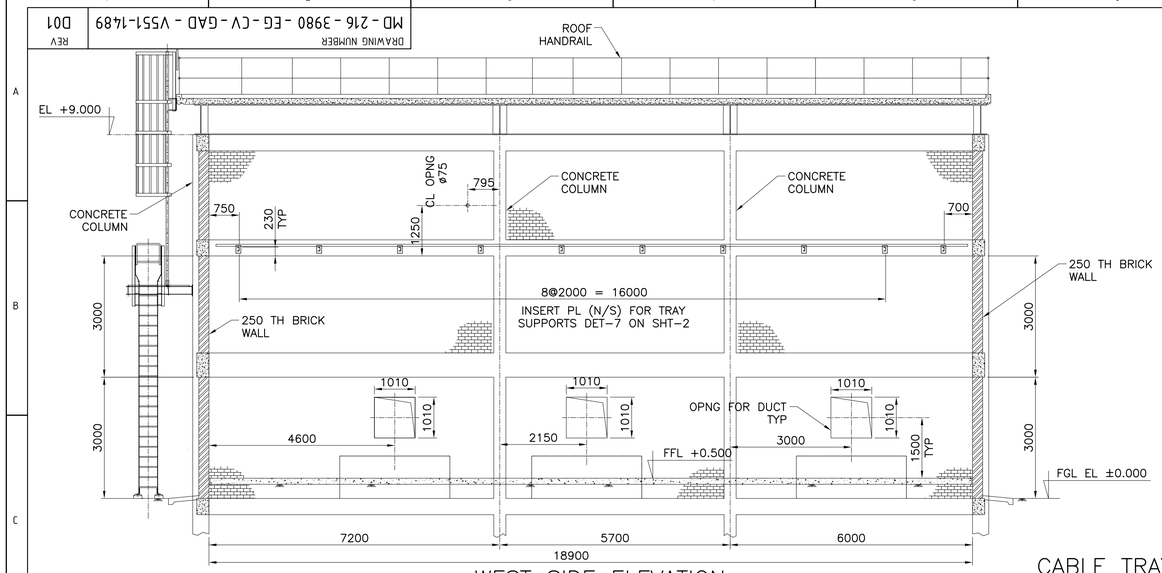

WEST SIDE ELEVATION

LOOKING WEST
SCALE 1:75

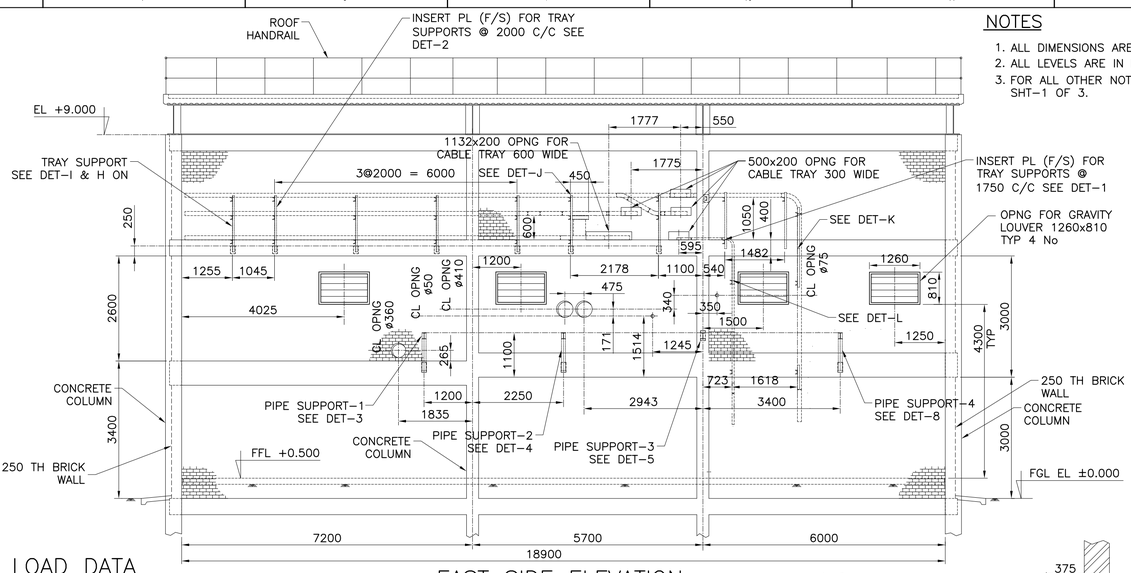

EAST SIDE ELEVATION


LOOKING WEST
SCALE 1:75

CABLE TRAY LOAD DATA


TRAY WIDTH 600mm – 0.6 KN/m
TRAY WIDTH 450mm – 0.45 KN/m
TRAY WIDTH 300mm – 0.3 KN/m

NOTES


1. ALL DIMENSIONS ARE IN MILLIMETER.
2. ALL LEVELS ARE IN METER.
3. FOR ALL OTHER NOTES SEE SHT-1 OF 3.

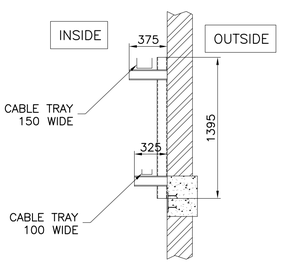


DETAIL 1 / – SCALE 1:30

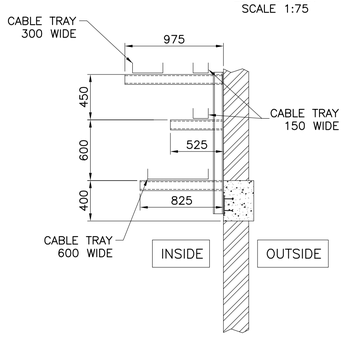


DETAIL 2 / –/SHT-2 SCALE 1:30

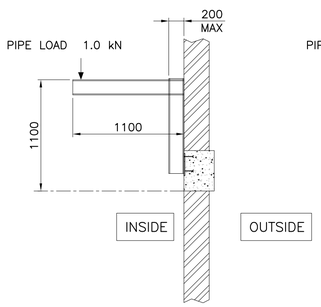


DETAIL 3 / – SCALE 1:30

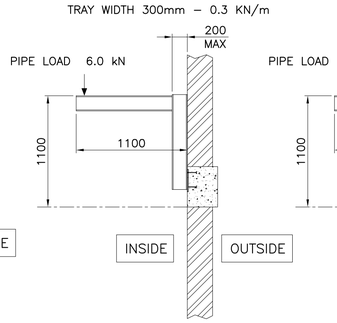


DETAIL 5 / – SCALE 1:30

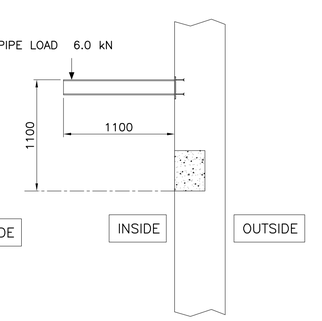


DETAIL 6 / – SCALE 1:30

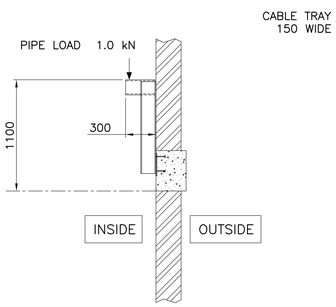


DETAIL 8 / –/SHT-2 SCALE 1:30

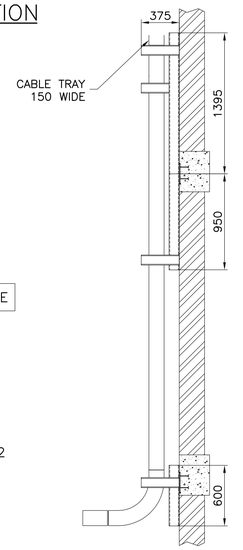


DETAIL K / – SCALE 1:30

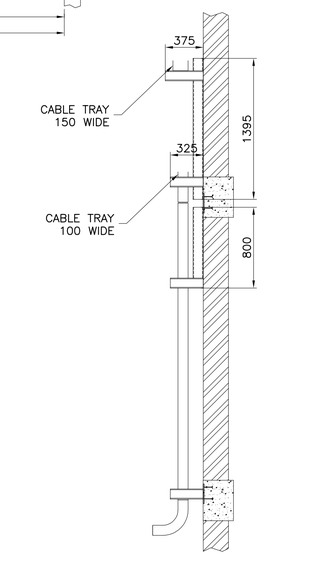


DETAIL L / – SCALE 1:30

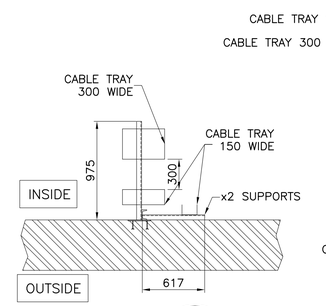


DETAIL D / –/SHT-2 SCALE 1:30

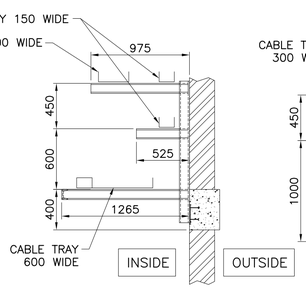


DETAIL E / –/SHT-2 SCALE 1:30

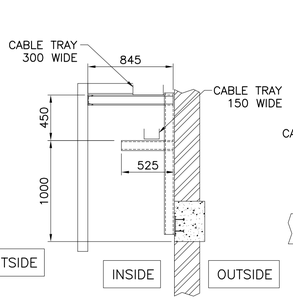


DETAIL F / –/SHT-2 SCALE 1:30

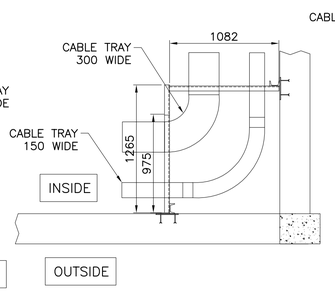


DETAIL H / –/SHT-2 SCALE 1:30

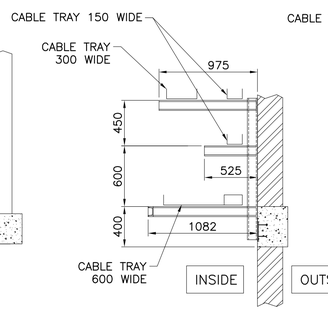

DETAIL I / – SCALE 1:30

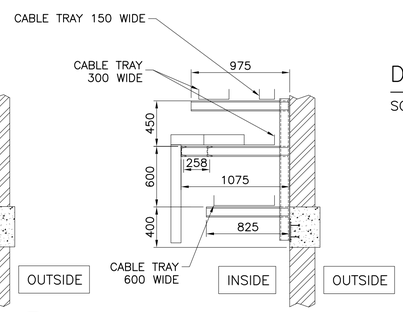

DETAIL J / – SCALE 1:30

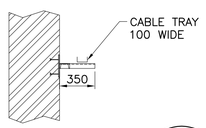

DETAIL G / –/SHT-2 SCALE 1:30

DOCUMENT NUMBER	REFERENCE DOCUMENTS	REV	DATE	REVISION DESCRIPTION	DRN	CHK	ENG	APP	EMP
		D01	08/05/2023	AS - BUILT	--	STY/SYC/SHH	--	BDA/PRI/JPD	
		C02	06/01/2021	ISSUED FOR CONSTRUCTION	--	STY/SYC/SHH	--	BDA/PRI/JPD	
		C01	10/08/2020	ISSUED FOR CONSTRUCTION	--	STY/SYC/SHH	--	BDA/PRI/JPD	
		A01	16/06/2020	ISSUED FOR INFORMATION	--	STY/SYC/SHH	--	BDA/PRI/JPD	

Air Liquide ENGINEERING & CONSTRUCTION

AIR LIQUIDE CONFIDENTIAL INFORMATION: THIS PRINT IS THE PROPERTY OF L'AIR LIQUIDE S.A. OR ITS (DIRECT AND INDIRECT) AFFILIATES OR SUBSIDIARIES AND CONTAINS VALUABLE CONFIDENTIAL INFORMATION. COPYRIGHT AND ALL OTHER RIGHTS IN THIS PRINT ARE EXPRESSLY RESERVED. NO PART OF THIS PRINT MAY BE DISCLOSED BY THE INTENDED RECIPIENT TO A THIRD PARTY, REPRODUCED, COPIED, LENT, OR DISPOSED OF, DIRECTLY OR INDIRECTLY, NOR USED FOR ANY PURPOSE OTHER THAN THAT FOR WHICH IT IS EXPRESSLY FURNISHED. THIS PRINT IS LENT SUBJECT TO RETURN ON DEMAND.

DRAWING NUMBER				REVISION	STATUS
12126-60-01-CS-261192				2	AFD
DATE	26/11/2020	DATE	27/11/2020	DATE	30/11/2020
DRAWN	SGH	CHECKED	ABM	APPROVED	DS

LARSEN & TOUBRO DRAWING NUMBER: 019045-080-C-V-24225-027 — REVISION: 3

OUTOTEC DRAWING NUMBER: 900707 __GAU01 __AG22__MTL01 __39847 — DOCUMENT ID: OU100688447 — REVISION: 3

LARSEN & TOUBRO

This drawing is the property of LARSEN & TOUBRO and must not be passed on to any person or body not authorized by us to receive it nor be copied or otherwise made use either in full or in part by such person or body without our prior permission in writing.

Outotec

The content of these documents are the sole property of Outotec Oyj. Any rights not expressly granted herein are reserved. Reproduction, transfer or distribution of part or all of the contents in any form without prior written permission of Outotec is prohibited.

MA'ADEN معادن Saudi Arabian Mining Company شركة المعادن العربية السعودية

This document and the information contained herein is Ma'aden proprietary know-how. This document or any part thereof should not be reproduced, stored in a retrieval system or transmitted by any means, electronic or otherwise, or divulged without prior written permission of Ma'aden.

DRAWN	--	--
CHECKED	STY/ SYC/ SHH	05/01/2021
ENGINEER	--	--
APPROVED	BDA/ PRI/ JPD	06/01/2021
EMPLOYER		
SCALE	1:75, 30	A1

MANSOURAH - MASSARAH GOLD PROJECT
GENERAL ARRANGEMENT DRAWING
OXYGEN PLANT
GUIDE DRAWING - COMPRESSOR ROOM (3 OF 3)

DRAWING NUMBER: MD-216-3980-EG-CV-GAD-V551-1489 — REV: D01