




DETAIL OF PEDESTAL SPS4
SCALE 1:20

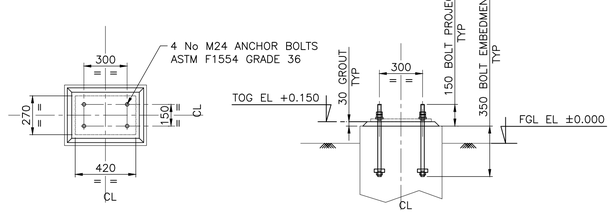


DETAIL OF PEDESTAL SPS13 TO SPS16
SCALE 1:20

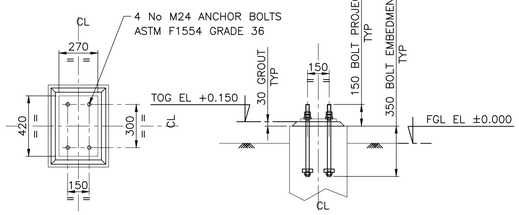


DETAIL OF PEDESTAL SPS17 & SPS18
SCALE 1:20

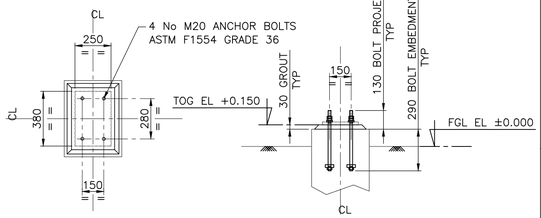


DETAIL OF PEDESTAL SPS19 & SPS20
SCALE 1:20

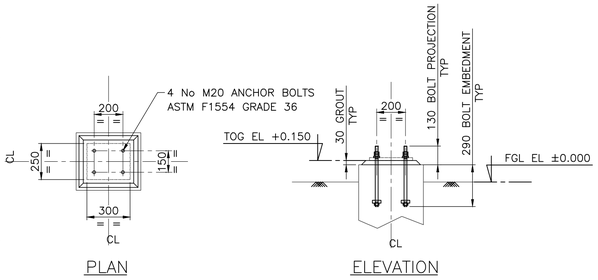


DETAIL OF PEDESTAL CTS5 TO CTS9,
CTS13, CTS23, CTS26
SCALE 1:20

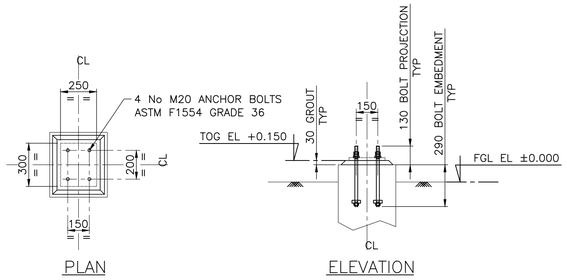

DETAIL OF PEDESTAL CTS10 TO CTS12,
CTS24, CTS27 TO CTS29
SCALE 1:20

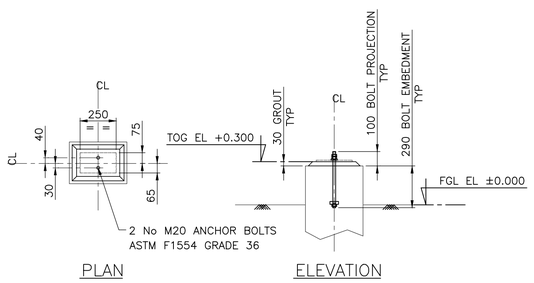

DETAIL OF STAIR PEDESTAL SP5 & SP6
SCALE 1:20

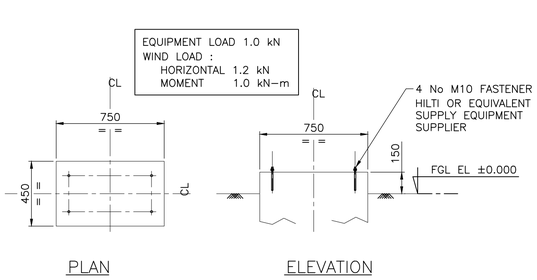

DETAIL OF PEDESTAL ISP1
SCALE 1:20

TABLE–3 : CABLE TRAY SUPPORT [CTS] FOUNDATION LOAD DATA

PEDESTAL MARK	VERTICAL LOAD V (UPWARD POSITIVE) [kN]	HORIZONTAL LOAD		MOMENT AT BASE LEVEL	
		FX (NORTH-SOUTH) [kN]	FZ (EAST-WEST) [kN]	DUE TO FX / V [kN-m]	DUE TO FZ / V [kN-m]
CTS1 TO CTS4	NOT ON PEDESTAL				
CTS5	-1.0	2.0	1.1	4.1	1.8
CTS6	-1.0	2.0	1.1	4.1	1.8
CTS7	-1.6	2.4	1.0	4.8	1.5
CTS8	-2.0	2.6	1.2	5.4	1.9
CTS9	-2.0	2.6	1.2	5.4	1.9
CTS10	-1.3	1.0	2.0	1.5	3.7
CTS11	-1.5	1.8	1.8	2.4	3.0
CTS12	-1.0	1.0	1.0	1.0	1.3
CTS13	-1.0	1.1	1.0	1.2	1.0
CTS14	-0.4	-	0.6	0.1	1.0
CTS15	-0.4	-	0.6	0.1	0.3
CTS16	-0.4	-	0.6	0.1	0.3
CTS17	-0.4	0.6	-	0.4	-
CTS18	-0.4	0.6	-	0.3	0.1
CTS19	-0.4	0.6	-	0.4	-
CTS20	-0.4	-	0.6	-	0.4

PEDESTAL MARK	VERTICAL LOAD V (UPWARD POSITIVE) [kN]	HORIZONTAL LOAD		MOMENT AT BASE LEVEL	
		FX (NORTH-SOUTH) [kN]	FZ (EAST-WEST) [kN]	DUE TO FX / V [kN-m]	DUE TO FZ / V [kN-m]
CTS21	-0.4	0.6	-	0.5	-
CTS22	-0.4	0.6	-	0.4	-
CTS23	-1.0	1.0	1.0	1.6	1.2
CTS24	-1.0	1.0	1.3	1.2	2.2
CTS25	-0.6	0.9	-	1.5	-
CTS-26	-1.5	2.0	1.3	3.7	1.6
CTS-27	-1.0	1.0	1.3	1.0	2.2
CTS-28	-1.0	1.0	1.3	1.0	2.2
CTS-29	-1.0	1.0	1.8	1.3	2.4
CTS-30	-0.6	-	0.9	-	0.4
CTS-31	-0.6	0.9	0.9	0.4	0.4
CTS-32	-0.4	0.6	-	0.4	-
CTS-33	-0.4	0.6	-	0.4	-
CTS-34	-0.4	-	0.6	-	0.4
CTS-35	-0.4	-	0.6	-	0.7
CTS-36	-0.4	-	0.6	-	0.4
CTS-37	NOT ON PEDESTAL				
CTS-38	-0.5	0.8	-	0.6	-

NOTES

1. ALL DIMENSIONS ARE IN MILLIMETER.
2. ALL LEVELS ARE IN METER.
3. FGL LEVEL ±0.0 CORRESPONDS TO RL 912.350.
4. FOR ALL OTHER NOTES SEE SHT–1.
5. FOR PIPE SUPPORT FOUNDATION LOAD DATA SEE SHT–3.

DOCUMENT NUMBER	REFERENCE DOCUMENTS	REV	DATE	REVISION DESCRIPTION	DRN	CHK	ENG	APP	EMP
MD-216-3980-EG-ST-GAD-V551-2397	PIPE & TRAY SUPPORTS (SHEET-5)								
MD-216-3980-EG-ST-GAD-V551-2396	PIPE & TRAY SUPPORTS (SHEET-4)								
MD-216-3980-EG-ST-GAD-V551-2395	PIPE & TRAY SUPPORTS (SHEET-3)								
MD-216-3980-EG-ST-GAD-V551-2394	PIPE & TRAY SUPPORTS (SHEET-2)	D01	08/09/2023	AS - BUILT	--	STY/SYC/SHH	--	BDA/PRI/JPD	
MD-216-3980-EG-ST-GAD-V551-2393	PIPE & TRAY SUPPORTS (SHEET-1)	C01	20/03/2021	ISSUED FOR CONSTRUCTION & REVISED AS MKD. C01	--	STY/SYC/SHH	--	BDA/PRI/JPD	
MD-216-3980-EG-PI-PPD-V551-1001	PLOT PLAN	A01	21/12/2020	ISSUED FOR INFORMATION	--	STY/SYC/SHH	--	BDA/PRI/JPD	

AIR LIQUIDE CONFIDENTIAL INFORMATION: THIS PRINT IS THE PROPERTY OF L'AIR LIQUIDE S.A. OR ITS DIRECT AND INDIRECT AFFILIATES OR SUBSIDIARIES AND CONTAINS VALUABLE CONFIDENTIAL INFORMATION. COPYRIGHT AND ALL OTHER RIGHTS IN THIS PRINT ARE EXPRESSLY RESERVED. NO PART OF THIS PRINT MAY BE DISCLOSED BY THE INTENDED RECIPIENT TO A THIRD PARTY, REPRODUCED, COPIED, LENT, OR DISPOSED OF, DIRECTLY OR INDIRECTLY, NOR USED FOR ANY PURPOSE OTHER THAN THAT FOR WHICH IT IS EXPRESSLY FURNISHED. THIS PRINT IS LENT SUBJECT TO RETURN ON DEMAND.

Air Liquide ENGINEERING & CONSTRUCTION

LARSEN & TOUBRO

This drawing is the property of LARSEN & TOUBRO and must not be passed on to any person or body not authorized by us to receive it nor be copied or otherwise made use either in full or in part by such person or body without our prior permission in writing.

Outotec

The content of these documents are the sole property of Outotec Oyj. Any rights not expressly granted herein are reserved. Reproduction, transfer or distribution of part or all of the contents in any form without prior written permission of Outotec is prohibited.

MA'ADEN معادن
Saudi Arabian Mining Company شركة التعدين العربية السعودية

This document and the information contained herein is Ma'aden proprietary know-how. This document or any part thereof should not be reproduced, stored in a retrieval system or transmitted by any means, electronic or otherwise, or divulged without prior written permission of Ma'aden.

DRAWING NUMBER	12126-60-01-CS-141255	REVISION	1
STATUS	AFD		
DATE	14/12/2020	DATE	15/12/2020
DATE	10/03/2021		
DRAWN	SGH	CHECKED	ABM
APPROVED	DS		

LARSEN & TOUBRO DRAWING NUMBER	019045_080_C_V_24225_033	REVISION 2
OUTOTEC DRAWING NUMBER	900707 _GAU01 _AG22_MTL01 _39894	DOCUMENT ID OU100711120 / REVISION 2

DRAWN	--	--
CHECKED	STY/ SYC/ SHH	11/03/2021
ENGINEER	--	--
APPROVED	BDA/ PRI/ JPD	12/03/2021
EMPLOYER		
SCALE	1:30	A1

MANSOURAH - MASSARAH GOLD PROJECT
GENERAL ARRANGEMENT DRAWING
OXYGEN PLANT
FOUNDATION LOAD-PIPE & TRAY SUPPORT SHT-6

DRAWING NUMBER MD-216-3980-EG-CV-GAD-V551-1503 REV D01