


DRAWING NUMBER MD - 216 - 3660 - EG - CV - GAD - 2002 REV D01

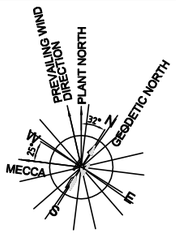


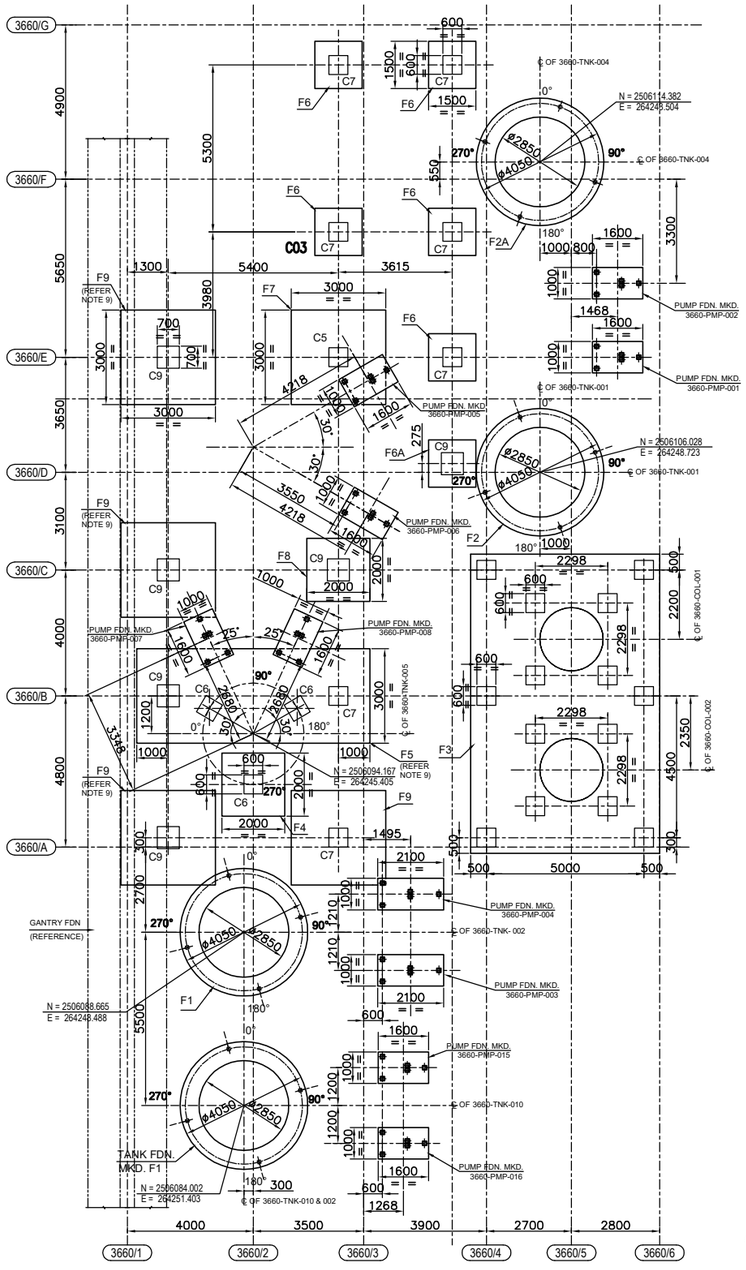


LAYOUT OF FOUNDATION
(SCALE 1:100)

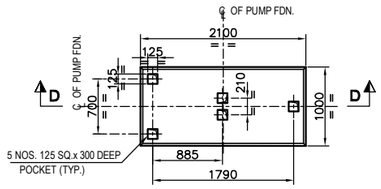


FDN. FOR PUMP MKD. 3660-PMP-003 & 004
SCALE 1:40

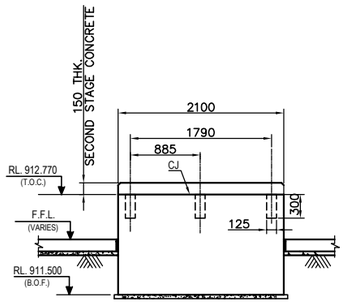


SECTION : D-D
SCALE 1:40

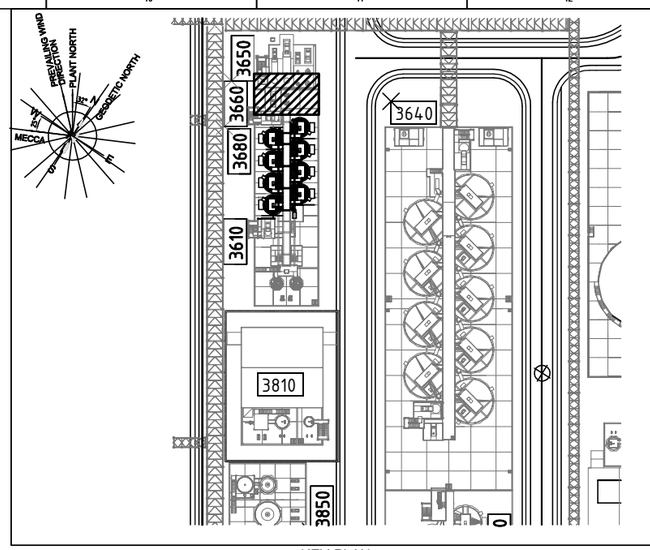


KEY PLAN
(SCALE- 1:750)

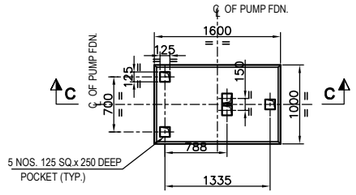


FDN. FOR PUMP MKD. 3660-PMP-005 & 006
SCALE 1:40

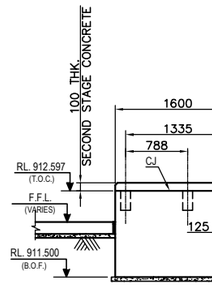


SECTION : C-C
SCALE 1:40

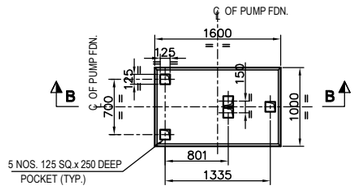


FDN. FOR PUMP MKD. 3660-PMP-001 & 002
SCALE 1:40

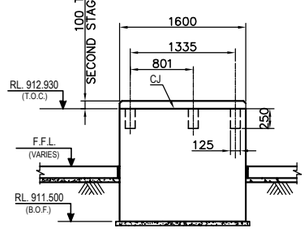


SECTION : B-B
SCALE 1:40

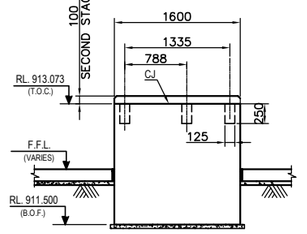


SECTION : E-E
SCALE 1:40

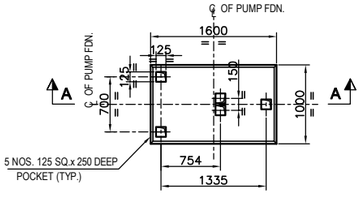

FDN. FOR PUMP MKD. 3660-PMP-015 & 016
SCALE 1:40

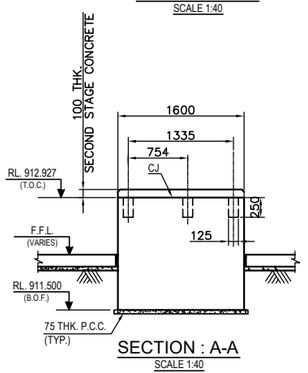

SECTION : A-A
SCALE 1:40

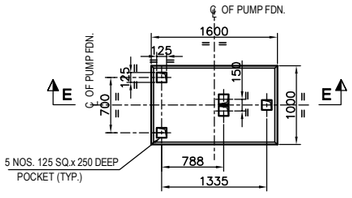

FDN. FOR PUMP MKD. 3360-PMP-007 & 008
SCALE 1:40

LEGEND :-

R.L. - REDUCED LEVEL
T.O.C. - TOP OF CONCRETE.
F.G.L. - FINISHED GROUND LEVEL.
F.F.L. - FINISHED FLOOR LEVEL.
B.O.F. - BOTTOM OF FOUNDATION
TYP. - TYPICAL.
P.C.D. - PITCH CIRCLE DIAMETER.
P.C.C - PLAIN CEMENT CONCRETE
MKD. - MARKED.
THK. - THICK
EQV. - EQUIVALENT
Ø - DIAMETER
CJ - CONSTRUCTION JOINT
SQ - SQUARE
RCC. - REINFORCED CEMENT CONCRETE
DIA - DIAMETER
DRG. - DRAWING
℄ - CENTRE LINE

FDN. - FOUNDATION
REGEN. - REGENERATION

NOTES :-

1. ALL DIMENSIONS ARE IN MILLIMETRES AND LEVELS AND CO-ORDINATES ARE IN METRES. UNLESS OTHERWISE STATED.
2. GRADE OF CONCRETE SHALL BE C35 FOR FOUNDATION.
3. GRADE OF REINFORCEMENT SHALL BE DEFORMED BAR ASTM A615 - GRADE 60 (fy = 420 MPa).
4. NET SAFE BEARING CAPACITY OF SOIL AT BOTTOM OF FOUNDATION IS CONSIDERED 450KN/ SQ. M.
5. IF ANY PART OF FOUNDATION COMES ON BACKFILL ZONE OF ADJACENT FOUNDATION OR ANY LOOSE SOIL ARE ENCOUNTERED BELOW FOUNDATION LEVEL THE SAME SHALL BE REMOVED AND FILLED WITH PCC.
6. THIS DRG. SHALL BE READ IN CONJUNCTION WITH DRG. NO. MD-216-3380-EG-CV-DED-1002.
7. SAND SHALL BE COMPACTED TO A MAXIMUM DEPTH OF 300MM AND SHALL BE COMPACTED TO 80% RELATIVE DENSITY AS DETERMINED BY ASTM D4253 AND ASTM D4254.
8. CHEMICAL RESISTANT COATING SHALL BE APPLIED FOR PROTECTING CONCRETE AGAINST ACID & ALKALI .
9. FOUNDATION F9 TO BE CASTED PRIOR CASTING OF GANTRY FOUNDATION.

DOCUMENT NUMBER	REFERENCE DOCUMENTS			REVISION DESCRIPTION	DRN	CHK	ENG	APP	EMP
		D01	05/05/2023	AS - BUILT	TEC	BJB	TEC	SJM	
		C03	03/02/2021	ISSUED FOR CONSTRUCTION & REVISED AS MARKED (C03)	TEC	BJB	TEC	SJM	
		C02	11/01/2021	ISSUED FOR CONSTRUCTION & REVISED AS MARKED	TEC	BJB	TEC	SJM	
		C01	21/12/2020	ISSUED FOR CONSTRUCTION & REVISED AS MARKED	TEC	BJB	TEC	SJM	
MD-216-3660-EG-ME-GAD-1039	PLAN AT EL+912.200	A01	07/11/2020	ISSUED FOR REFERENCE	RW	TV	SC	RL	

RESERVED FOR VENDOR LOGO AND DRAWING NUMBER

LARSEN & TOUBRO
This drawing is the property of LARSEN & TOUBRO and must not be passed on to any person or body not authorized by us to receive it nor be copied or otherwise made use either in full or in part by such person or body without our prior permission in writing.

Outotec
The content of these documents are the sole property of Outotec Oyj. Any rights not expressly granted herein are reserved. Reproduction, transfer or distribution of part or all of the contents in any form without prior written permission of Outotec is prohibited.

MA'ADEN معادن
Saudi Arabian Mining Company شركة معادن العربية السعودية
This document and the information contained herein is Ma'aden proprietary know-how. This document or any part thereof should not be reproduced, stored in a retrieval system or transmitted by any means, electronic or otherwise, or divulged without prior written permission of Ma'aden.

LARSEN & TOUBRO DRAWING NUMBER	019045_450_C_G_24448_001		REVISION 4
OUTOTEC DRAWING NUMBER	900707 _GAU01 _EE13 _MTL01 _36647	DOCUMENT ID OU100705928	REVISION 4
DRAWN	TEC	04/11/2020	
CHECKED	BJB	06/11/2020	
ENGINEER	TEC	04/11/2020	
APPROVED	SJM	07/11/2020	
EMPLOYER			
SCALE	1:100, 1:40	A1	

MANSOURAH - MASSARAH GOLD PROJECT
GENERAL ARRANGEMENT DRAWING
LOW GRADE ACID WASH/ELUTION/CARBON REGEN
LAYOUT & DETAIL OF FOUNDATION

DRAWING NUMBER MD - 216 - 3660 - EG - CV - GAD - 2002 REV D01