


DRAWING NUMBER: MD-216-3660-EG-CV-GAD-2005 | REV: D01

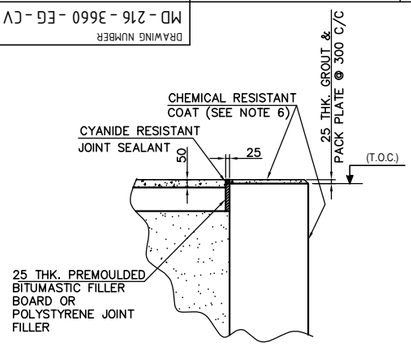


DETAIL - 'X'
SCALE 1:20

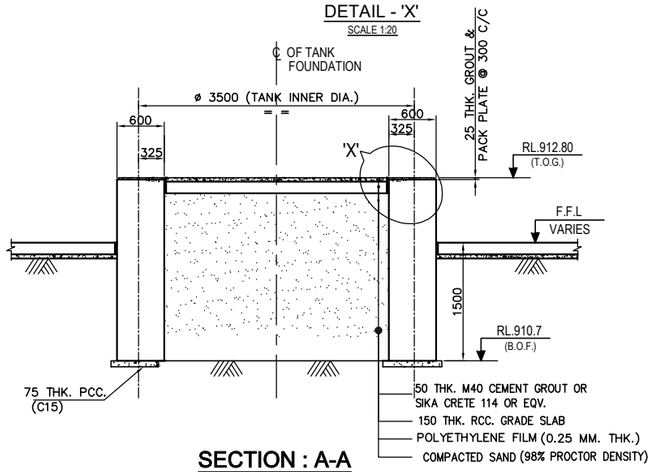


SECTION : A-A
SCALE 1:40

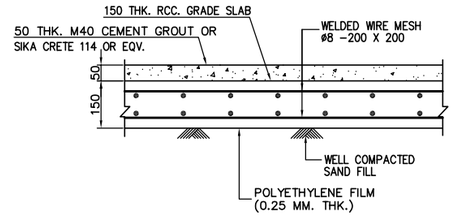


TYP. DET. OF 150 THK. GRADE SLAB
SCALE 1:10

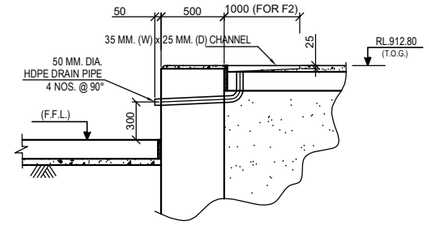


SECTION : B-B
SCALE 1:25

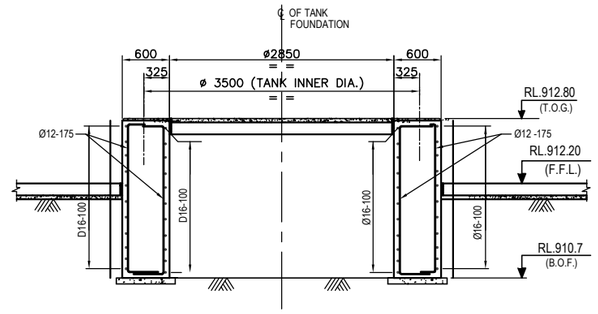


SECTION : C-C
SCALE 1:40

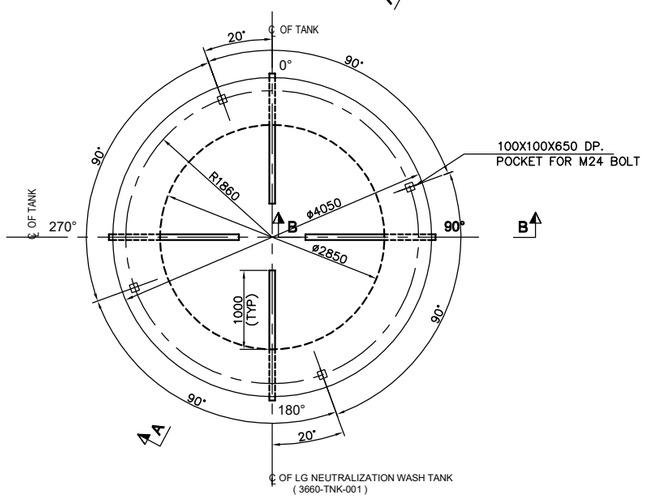

G.A. DETAIL OF TANK FOUNDATION MKD. F2
(FOR 3660-TNK-001)
SCALE 1:40

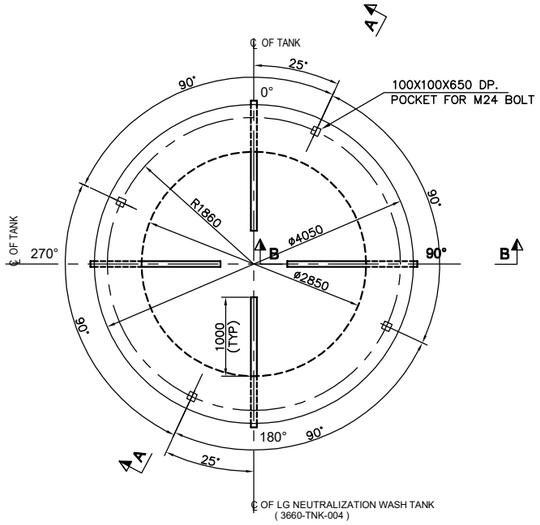

G.A. DETAIL OF TANK FOUNDATION MKD. F2A
(FOR 3660-TNK-004)
SCALE 1:40

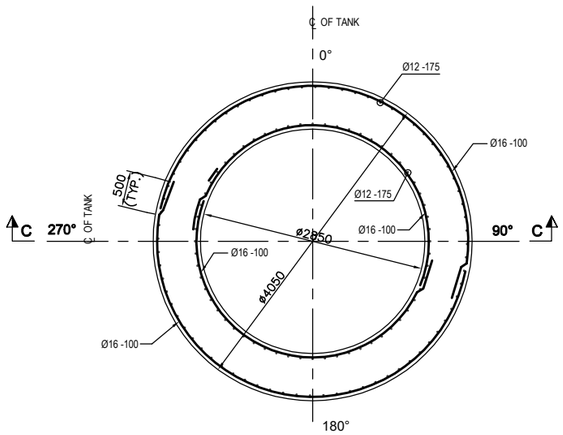

RCC. DETAIL OF TANK FOUNDATION MKD. F2
SCALE 1:40

LEGEND :-
R.L. - REDUCED LEVEL
℄ - CENTRE LINE
T.O.C. - TOP OF CONCRETE
F.G.L. - FINISHED GROUND LEVEL
F.F.L. - FINISHED FLOOR LEVEL
B.O.F. - BOTTOM OF FOUNDATION
TYP. - TYPICAL
R.C.C - REINFORCED CEMENT CONCRETE
P.C.C - PLAIN CEMENT CONCRETE
MKD. - MARKED
I.D. - INTERNAL DIAMETER
THK. - THICK
T.O.G. - TOP OF GROUT
EQV. - EQUIVALENT
DET. - DETAIL
FDN. - FOUNDATION
Ø - DIAMETER OF REINFORCEMENT
C/C - CENTRE TO CENTRE
R - RADIUS
DIA - DIAMETER
G.A - GENERAL ARRANGEMENT
HDPE - HIGH DENSITY POLY ETHYLENE
DP. - DEPTH

NOTES:-
1. ALL DIMENSIONS ARE IN MILLIMETRES AND LEVELS AND CO-ORDINATES ARE IN METRES UNLESS OTHERWISE STATED.
2. GRADE OF CONCRETE SHALL BE C35 (35MPa) FOR FOUNDATION, C30 (30MPa) FOR GRADE SLAB & C15 (15MPa) FOR BLINDING CONCRETE.
3. GRADE OF REINFORCEMENT SHALL BE DEFORMED BAR 420 MPa (GRADE 60) - ASTM A615/A615M.
4. GRADE OF WELDED WIRE MESH SHALL BE GRADE 60 (fy = 420 MPa) ACCORDING TO A1064.
5. NET SAFE BEARING CAPACITY OF SOIL AT BOTTOM OF FOUNDATION IS CONSIDERED AS 350KN/ SQ. M.
6. CLEAR COVER TO REINFORCEMENT SHALL BE AS FOLLOWS
   a) FOUNDATION = 50 mm
   b) WALLS = 50mm
   c) SLAB = 20mm
7. FOR STANDARD REINFORCEMENT DETAIL & GENERAL NOTES FOR CIVIL WORKS REFER DRAWING NO. MD-216-1000-EG-CV-DED-1005 & 1001.
8. ACID/ALKALI RESISTANT COATING TO BE APPLIED ON ALL EXPOSED CONCRETE SURFACE.

DOCUMENT NUMBER	REFERENCE DOCUMENTS	REV	DATE	REVISION DESCRIPTION	DRN	CHK	ENG	APP	EMP
		D01	05/05/2023	AS - BUILT	TEC	BJB	TEC	SJM	
MD-216-3660-EG-CV-GAD-1034	3660-TNK-001 LG ACID WASH TANK	C02	**16/01/2021**	ISSUED FOR CONSTRUCTION & REVISED AS MARKED (C02)	TEC	BJB	**TEC**	SJM	
MD-216-3660-EG-ME-GAD-1037	3660-TNK-004 LG NEUTRALITION WASH TANK	**C01**	21/12/2020	**ISSUED FOR CONSTRUCTION & REVISED AS PER EMPLOYER'S COMMENTS ON 17.12.2020 & REVISED AS MARKED (C01)**	**TEC**	**BJB**	TEC	**SJM**	
MD-216-3660-EG-CV-GAD-2002	LAYOUT & DETAIL OF FOUNDATION	**A01**	07/11/2020	**ISSUED FOR REFERENCE**	**TEC**	**BJB**	TEC	**SJM**	

RESERVED FOR VENDOR LOGO AND DRAWING NUMBER

LARSEN & TOUBRO DRAWING NUMBER: 019045_450_C_G_24448_004 | REVISION: 3
OUTOTEC DRAWING NUMBER: 900707 _GAU01 _EE13 _MTL01 _36650 | DOCUMENT ID: OU100705931 | REVISION: 3

LARSEN & TOUBRO
This drawing is the property of LARSEN & TOUBRO and must not be passed on to any person or body not authorized by us to receive it nor be copied or otherwise made use either in full or in part by such person or body without our prior permission in writing.

Outotec
The content of these documents are the sole property of Outotec Oyj. Any rights not expressly granted herein are reserved. Reproduction, transfer or distribution of part or all of the contents in any form without prior written permission of Outotec is prohibited.

MA'ADEN معادن
Saudi Arabian Mining Company شركة معادن العربية السعودية
This document and the information contained herein is Ma'aden proprietary know-how. This document or any part thereof should not be reproduced, stored in a retrieval system or transmitted by any means, electronic or otherwise, or divulged without prior written permission of Ma'aden.

DRAWN	TEC	04/11/2020
CHECKED	BJB	06/11/2020
ENGINEER	TEC	04/11/2020
APPROVED	SJM	07/11/2020
EMPLOYER		
SCALE	1:75, 1:50, 1;20	A1

MANSOURAH - MASSARAH GOLD PROJECT
GENERAL ARRANGEMENT DRAWING
LOWGRADE ACID WASH/ELUTION/CARBON REGEN LAYOUT & DETAIL OF FOUNDATION

DRAWING NUMBER: MD-216-3660-EG-CV-GAD-2005 | REV: D01