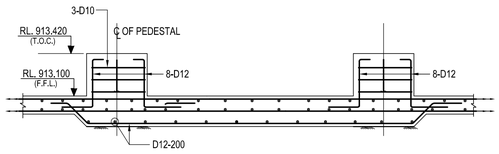
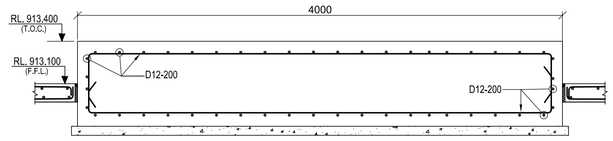


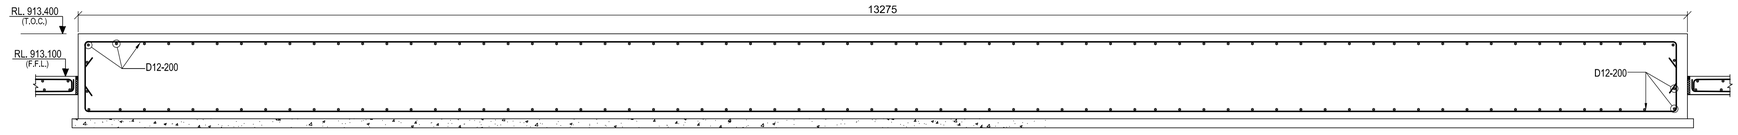

## SECTION D-D
SCALE 1:25




## SECTION C-C
( FOR LOCATION REFER DRAWING NO.
MD-216-3690-EG-CV-GAD-1305)
SCALE 1:25




## SECTION A-A
( FOR LOCATION REFER DRAWING NO.
MD-216-3690-EG-CV-GAD-1305)
SCALE 1:25




## SECTION B-B
( FOR LOCATION REFER DRAWING NO.
MD-216-3690-EG-CV-GAD-1305)
SCALE 1:25

LEGEND.:-

℄ - CENTERLINE
RCC - REINFORCED CEMENT CONCRETE
FDN. - FOUNDATION
T.O.C - TOP OF CONCRETE
F.F.L - FINISHED FLOOR LEVEL

NOTES:-
1. ALL DIMENSIONS ARE IN MILLIMETRES, LEVELS & COORDINATES ARE IN METRES UNLESS OTHERWISE STATED.
2. GRADE OF CONCRETE SHALL BE 35 MPa FOR WALL & 15 MPa FOR BLINDING CONCRETE.
3. NET SAFE BEARING CAPACITY AT THE FOUNDING LEVEL CONSIDERED 400KN /SQ. M
4. GRADE OF REINFORCEMENT SHALL BE DEFORMED BAR 420 MPa (GRADE 60)) - ASTM A615/A615M.
5. CLEAR COVER TO MAIN REINFORCEMENT SHALL BE - 50MM.

| DOCUMENT NUMBER | REFERENCE DOCUMENTS | REV | DATE | REVISION DESCRIPTION | DRN | CHK | ENG | APP | EMP |
|---|---|---|---|---|---|---|---|---|---|
| | | D01 | 05/05/2023 | AS - BUILT | AUD | SJM | SNM | PRI | |
| | | C01 | 24/11/2020 | ISSUED FOR CONSTRUCTION & REVISED AS MARKED C01 | AUD | SJM | SNM | PRI | |
| | | A01 | 10/08/2020 | ISSUED FOR REFERENCE | AUD | SJM | SNM | PRI | |

RESERVED FOR VENDOR LOGO AND DRAWING NUMBER

LARSEN & TOUBRO DRAWING NUMBER: 019045_450_C_D_24133_001 — REVISION: 2
OUTOTEC DRAWING NUMBER: 900707 _GAU01 _EE14 _CTB17 _36906 — DOCUMENT ID: OU100687048 — REVISION: 2

LARSEN & TOUBRO
This drawing is the property of LARSEN & TOUBRO and must not be passed on to any person or body not authorized by us to receive it nor be copied or otherwise made use either in full or in part by such person or body without our prior permission in writing.

Outotec
The content of these documents are the sole property of Outotec Oyj. Any rights not expressly granted herein are reserved. Reproduction, transfer or distribution of part or all of the contents in any form without prior written permission of Outotec is prohibited.

MA'ADEN معادن
Saudi Arabian Mining Company شركة التعدين العربية السعودية
This document and the information contained herein is Ma'aden proprietary know-how. This document or any part thereof should not be reproduced, stored in a retrieval system or transmitted by any means, electronic or otherwise, or divulged without prior written permission of Ma'aden.

| | | |
|---|---|---|
| DRAWN | AUD | 05/08/2020 |
| CHECKED | SJM | 06/08/2020 |
| ENGINEER | SNM | 05/08/2020 |
| APPROVED | PRI | 10/08/2020 |
| EMPLOYER | | |
| SCALE | 1:100 | A1 |

MANSOURAH - MASSARAH GOLD PROJECT
DETAIL DRAWING
GOLD ROOM
RCC DETAILS OF GROUND FLOOR EQUIPMENT FDN.

DRAWING NUMBER: MD - 216 - 3690 - EG - CV - DED -1307 — REV: D01